SO 143 - PŘÍJEZD K DUN v km 1,500
PŘÍČNÉ ŘEZY km 0,060 - 0,300
M 1 : 100

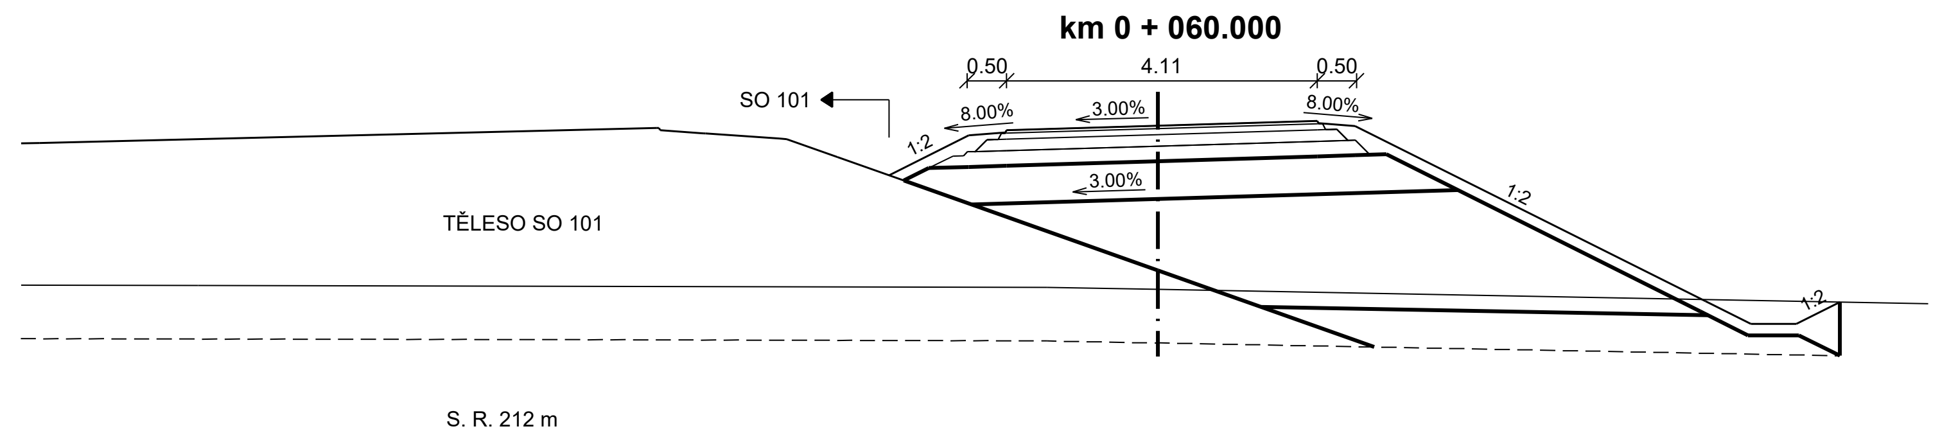
km 0 + 060.000
0.50
4.11
0.50
SO 101
8.00%
3.00%
8.00%
1:2
3.00%
TĚLESO SO 101
1:2
1:2
S. R. 212 m

PROJEKTOVANÝ STAV	215.89	216.42	216.49	216.55	216.61	216.54	213.93	213.93	214.21
ODSAZENÍ OD OSY	-3.56	-2.50	-2.00	0.00	2.11	2.61	7.84	8.44	9.02

STÁVAJÍCÍ TERÉN	214.41	214.38
ODSAZENÍ OD OSY	-1.47	0.00

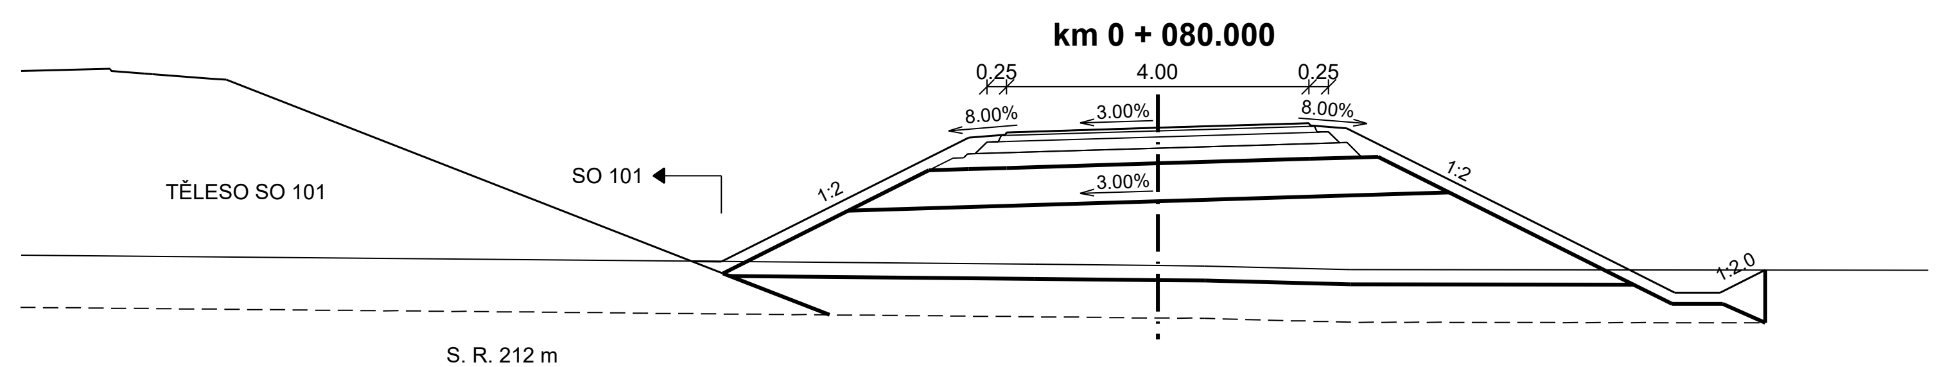
km 0 + 080.000
0.25
4.00
0.25
8.00%
3.00%
8.00%
TĚLESO SO 101
SO 101
1:2
3.00%
1:2
1:2.0
S. R. 212 m

PROJEKTOVANÝ STAV	213.91	213.90	215.54	215.61	215.67	215.73	215.66	213.79	213.49	213.49	213.79
ODSAZENÍ OD OSY	-6.81	-5.77	-2.50	-2.00	0.00	2.00	2.50	6.24	6.84	7.44	8.04

STÁVAJÍCÍ TERÉN	213.87	213.85	213.84	213.79
ODSAZENÍ OD OSY	-1.63	0.00	0.61	2.55

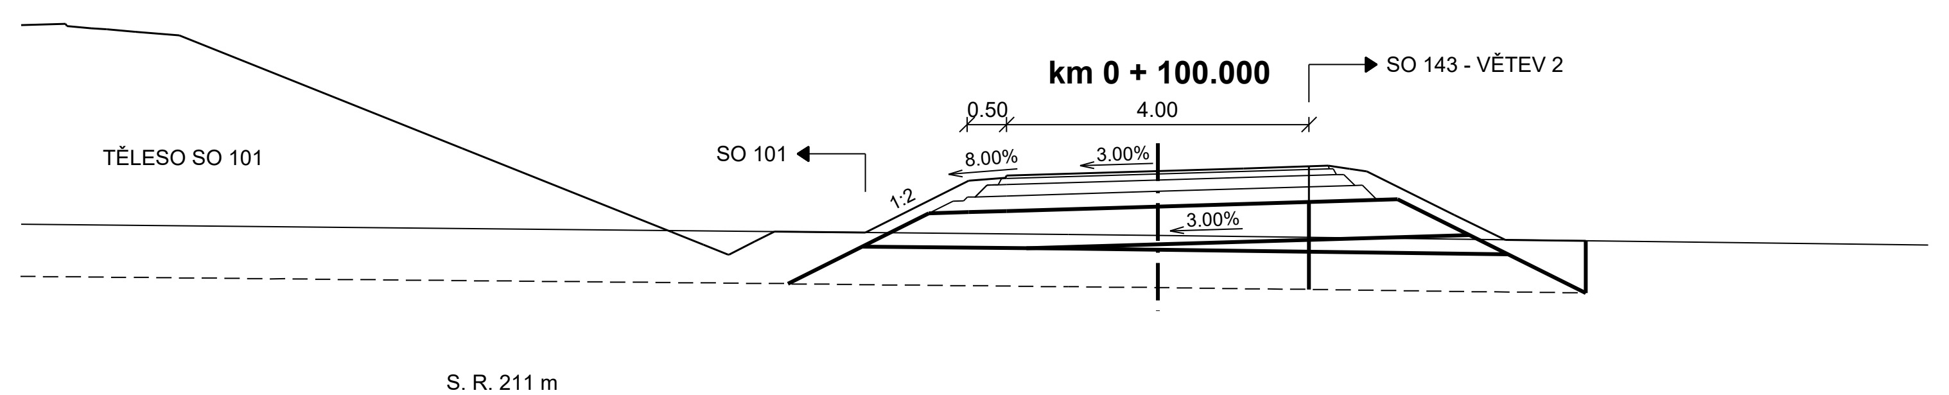
TĚLESO SO 101
km 0 + 100.000
SO 143 - VĚTEV 2
0.50
4.00
SO 101
8.00%
3.00%
1:2
3.00%
S. R. 211 m

PROJEKTOVANÝ STAV	213.66	214.34	214.41	214.47	214.53
ODSAZENÍ OD OSY	-3.87	-2.50	-2.00	0.00	2.00

STÁVAJÍCÍ TERÉN	213.63	213.62
ODSAZENÍ OD OSY	-1.18	0.00

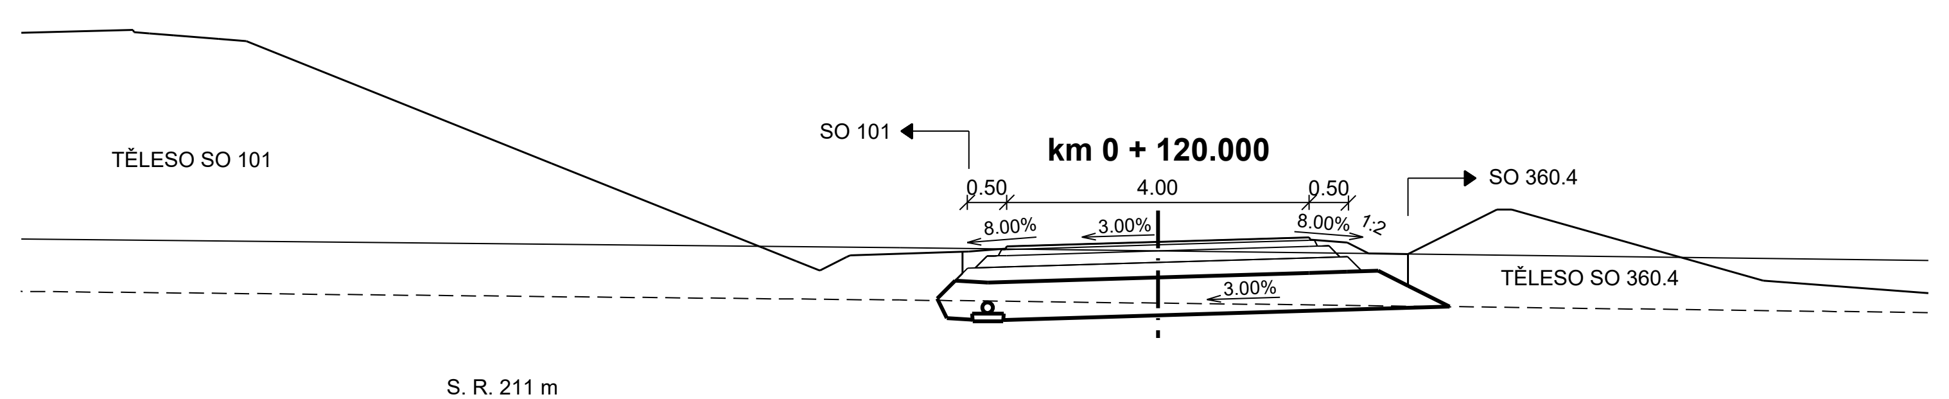
TĚLESO SO 101
SO 101
km 0 + 120.000
0.50
4.00
0.50
SO 360.4
8.00%
3.00%
8.00%
1:2
3.00%
TĚLESO SO 360.4
S. R. 211 m

PROJEKTOVANÝ STAV	213.46	213.53	213.59	213.65	213.58	213.43
ODSAZENÍ OD OSY	-2.50	-2.00	0.00	2.00	2.50	2.79

STÁVAJÍCÍ TERÉN	213.51	213.47
ODSAZENÍ OD OSY	-3.41	0.00

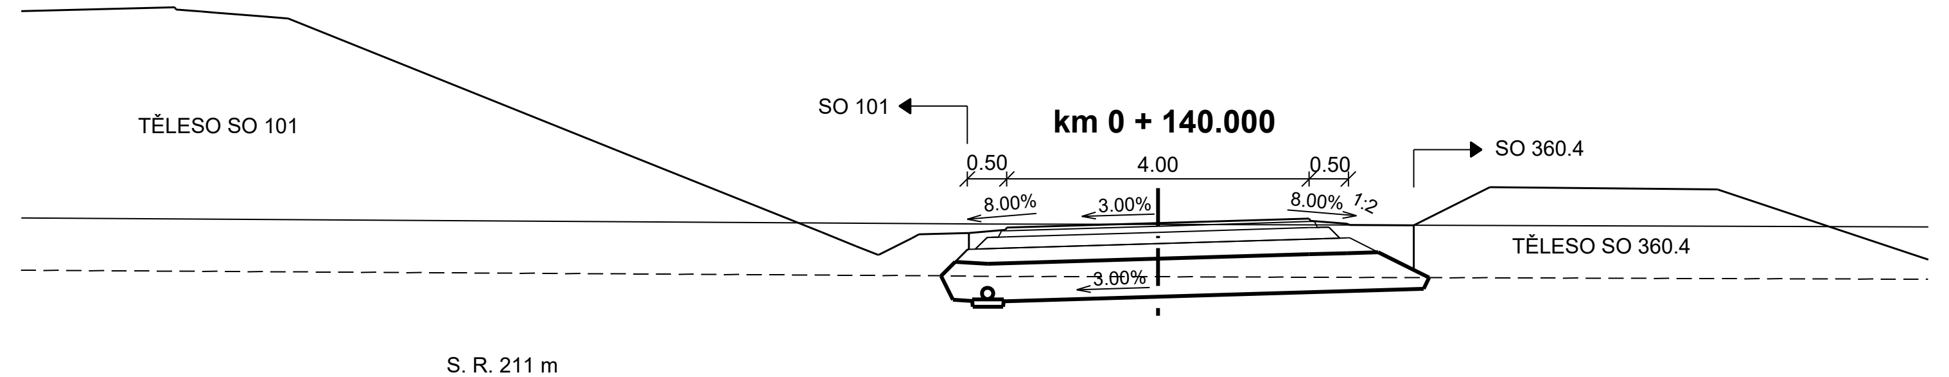
TĚLESO SO 101
SO 101
km 0 + 140.000
0.50
4.00
0.50
SO 360.4
8.00%
3.00%
8.00%
1:2
TĚLESO SO 360.4
3.00%
S. R. 211 m

PROJEKTOVANÝ STAV	213.41	213.48	213.54	213.60	213.53	213.51	213.51
ODSAZENÍ OD OSY	-2.50	-2.00	0.00	2.00	2.50	2.53	3.59

STÁVAJÍCÍ TERÉN	213.53	213.52
ODSAZENÍ OD OSY	-2.23	0.00

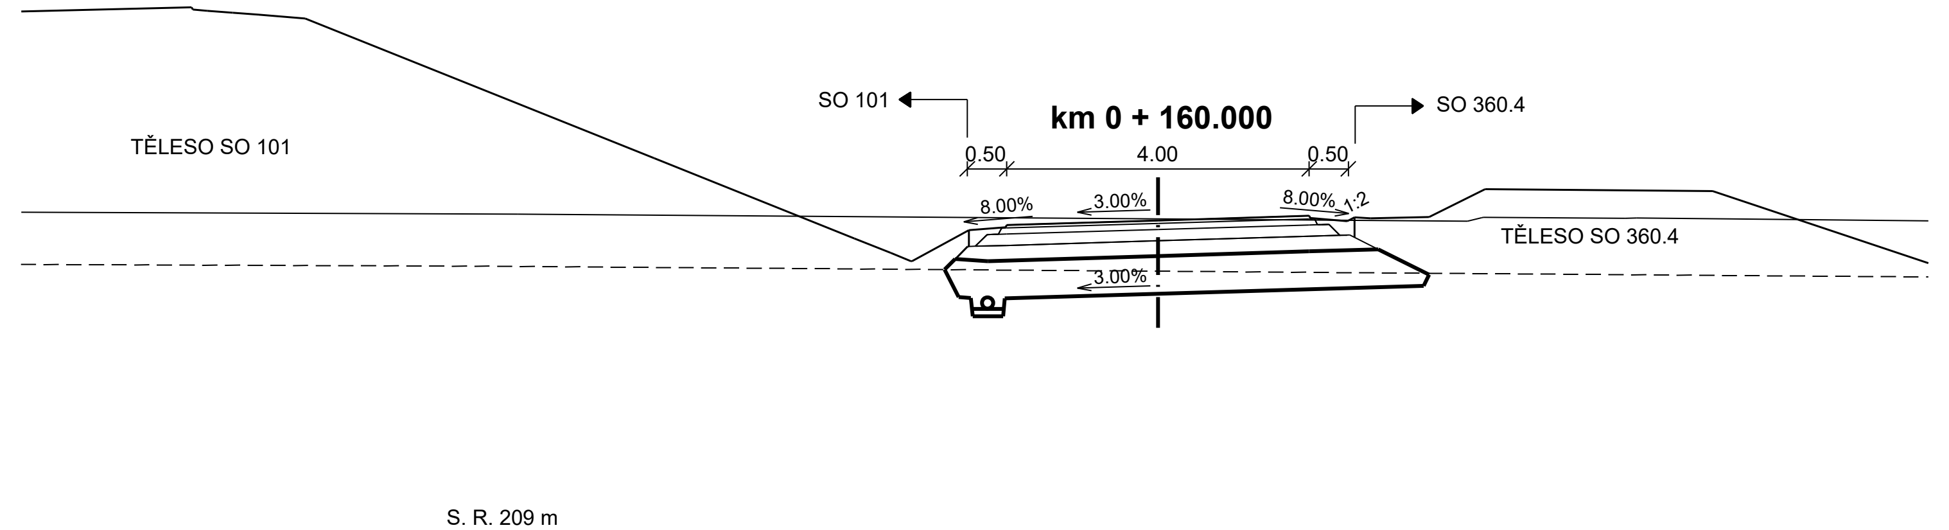
TĚLESO SO 101
SO 101
km 0 + 160.000
SO 360.4
0.50
4.00
0.50
8.00%
3.00%
8.00%
1:2
TĚLESO SO 360.4
3.00%
S. R. 209 m

PROJEKTOVANÝ STAV	213.47	213.54	213.60	213.66	213.59
ODSAZENÍ OD OSY	-2.50	-2.00	0.00	2.00	2.50

STÁVAJÍCÍ TERÉN	213.68	212.42	212.19	212.17	212.17	212.31	212.62	213.59	213.63	213.64	213.63	213.63
ODSAZENÍ OD OSY	-8.47	-3.78	-2.99	-2.03	-1.92	-1.32	0.00	4.09	4.28	4.31	6.18	6.33

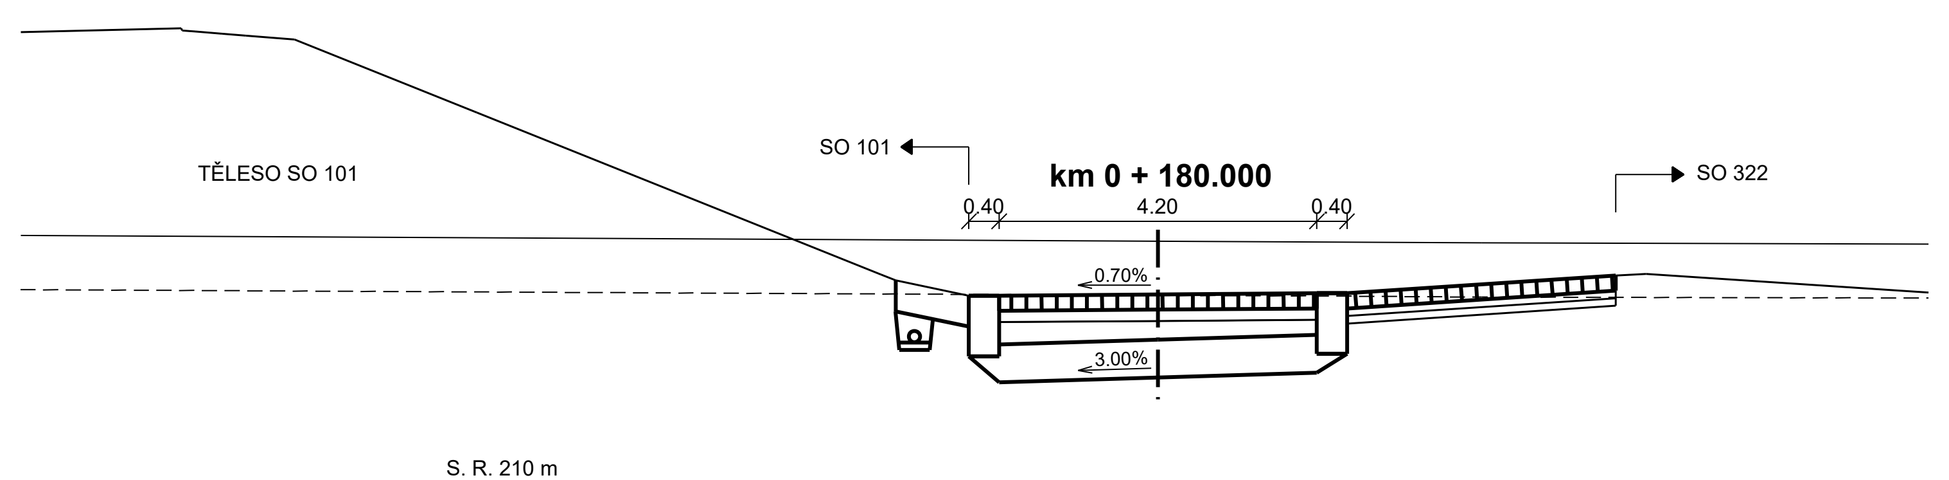
TĚLESO SO 101
SO 101
km 0 + 180.000
SO 322
0.40
4.20
0.40
0.70%
3.00%
S. R. 210 m

PROJEKTOVANÝ STAV	212.94	212.94	212.96	212.97	212.97	213.21
ODSAZENÍ OD OSY	-2.50	-2.10	0.00	2.10	2.50	6.05

STÁVAJÍCÍ TERÉN	213.66	213.64
ODSAZENÍ OD OSY	0.00	4.28

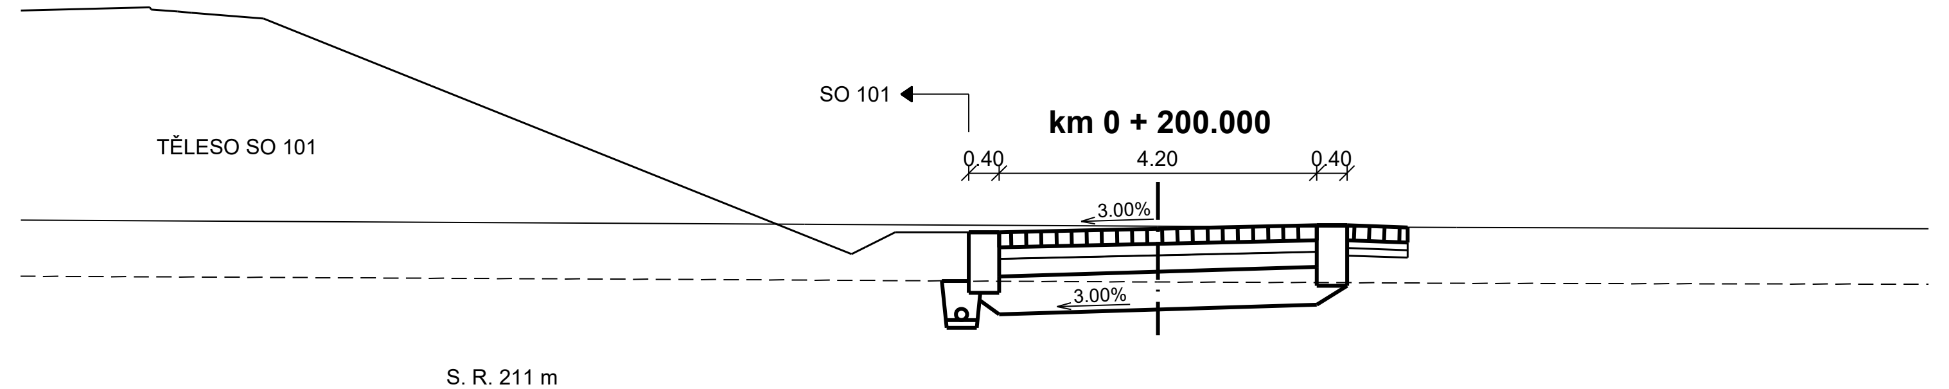
TĚLESO SO 101
SO 101
km 0 + 200.000
0.40
4.20
0.40
3.00%
3.00%
S. R. 211 m

PROJEKTOVANÝ STAV	213.58	213.58	213.63	213.67	213.67	213.64
ODSAZENÍ OD OSY	-2.50	-2.10	0.00	2.10	2.50	3.30

STÁVAJÍCÍ TERÉN	213.68	213.66	213.64
ODSAZENÍ OD OSY	-4.67	0.00	3.95

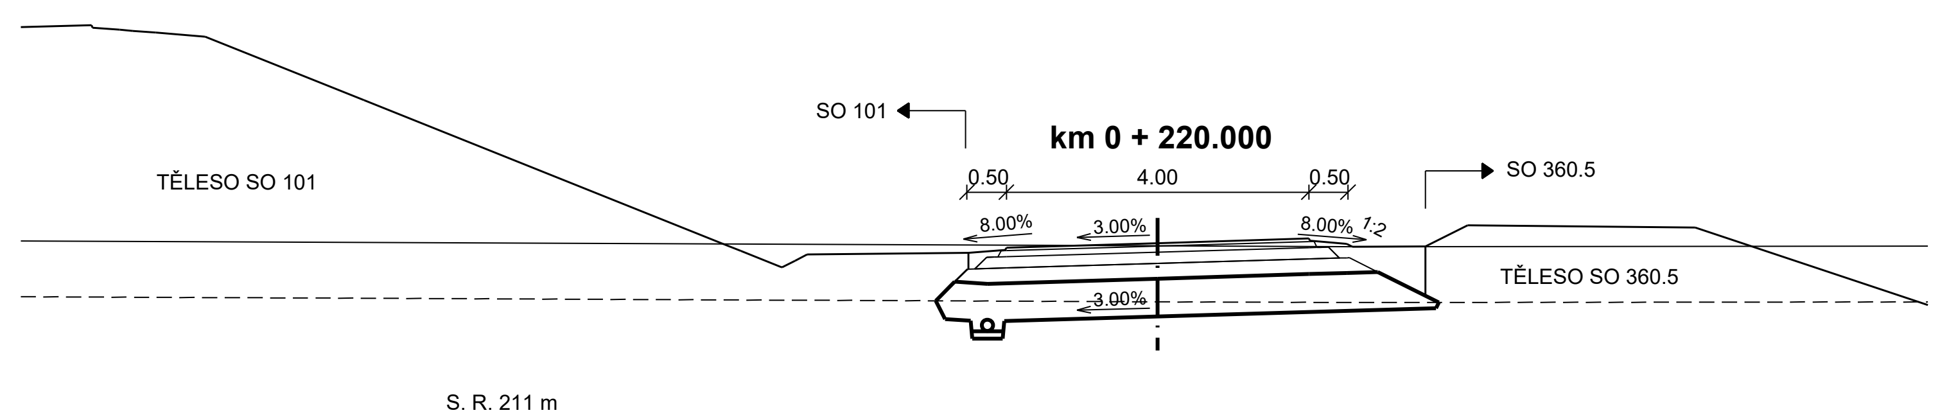
SO 101
km 0 + 220.000
SO 360.5
0.50
4.00
0.50
TĚLESO SO 101
8.00%
3.00%
8.00%
1:2
TĚLESO SO 360.5
3.00%
S. R. 211 m

PROJEKTOVANÝ STAV	213.65	213.72	213.78	213.84	213.77	213.73	213.73
ODSAZENÍ OD OSY	-2.50	-2.00	0.00	2.00	2.50	2.58	3.72

STÁVAJÍCÍ TERÉN	213.74	213.73
ODSAZENÍ OD OSY	0.00	2.63

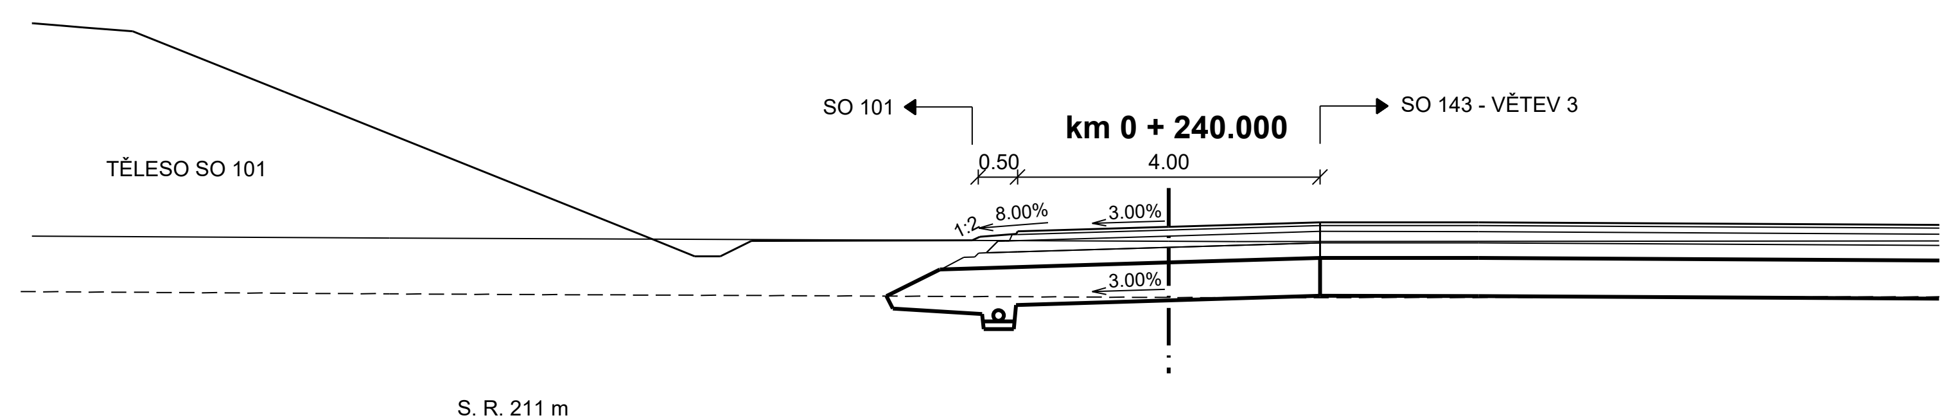
TĚLESO SO 101
SO 101
km 0 + 240.000
SO 143 - VĚTEV 3
0.50
4.00
1:2
8.00%
3.00%
3.00%
S. R. 211 m

PROJEKTOVANÝ STAV	213.88	213.93	214.00	214.06	214.12
ODSAZENÍ OD OSY	-2.60	-2.50	-2.00	0.00	2.00

STÁVAJÍCÍ TERÉN	213.87	213.87
ODSAZENÍ OD OSY	0.00	0.89

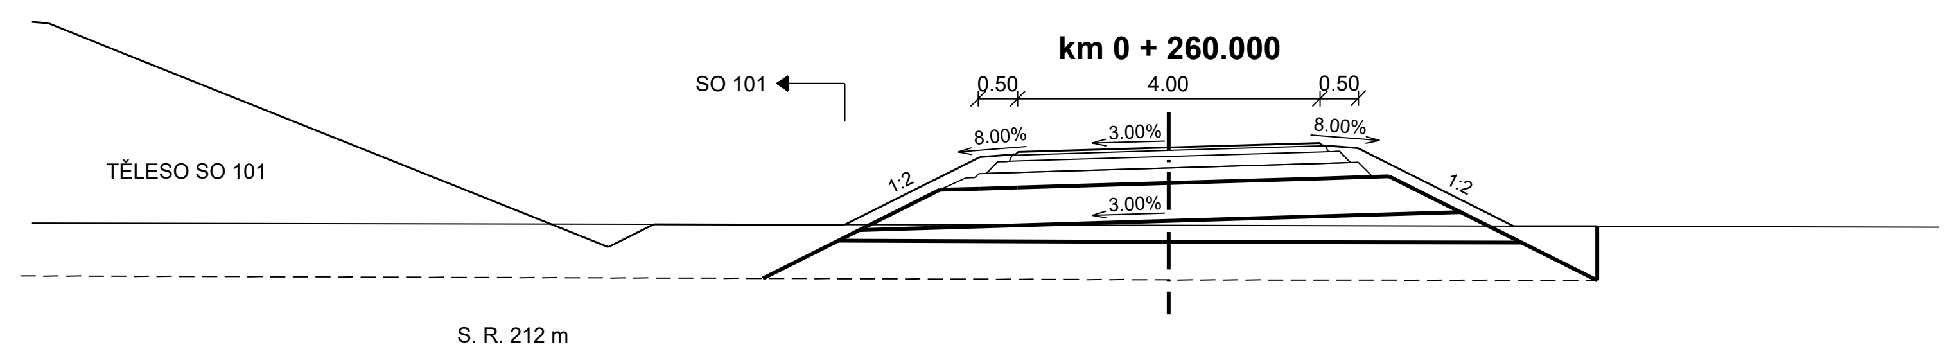
TĚLESO SO 101
SO 101
km 0 + 260.000
0.50
4.00
0.50
8.00%
3.00%
8.00%
1:2
1:2
3.00%
S. R. 212 m

PROJEKTOVANÝ STAV	214.13	215.02	215.09	215.15	215.21	215.14	214.11	214.10
ODSAZENÍ OD OSY	-4.28	-2.50	-2.00	0.00	2.00	2.50	4.56	5.66

STÁVAJÍCÍ TERÉN	214.12
ODSAZENÍ OD OSY	-0.08

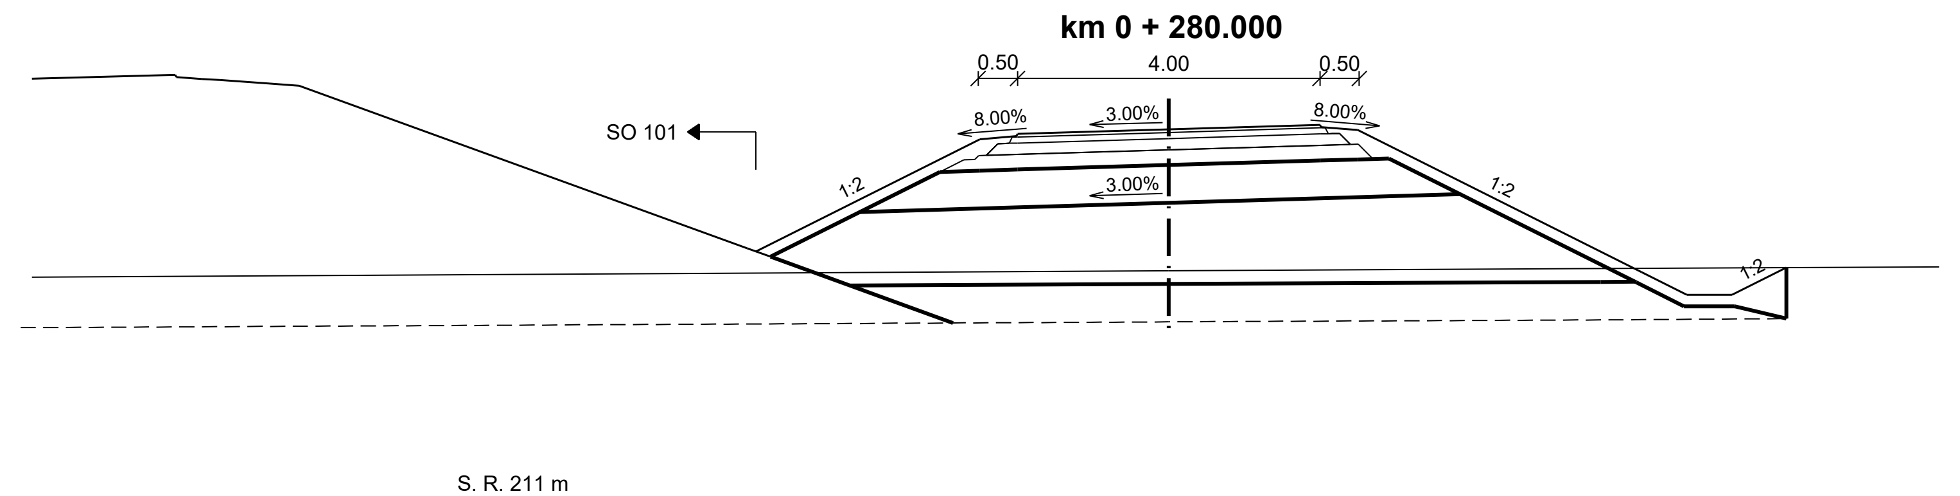
km 0 + 280.000
0.50
4.00
0.50
SO 101
8.00%
3.00%
8.00%
1:2
3.00%
1:2
1:2
S. R. 211 m

PROJEKTOVANÝ STAV	214.74	216.22	216.29	216.35	216.41	216.34	214.16	214.16	214.52
ODSAZENÍ OD OSY	-5.46	-2.50	-2.00	0.00	2.00	2.50	6.85	7.45	8.17

STÁVAJÍCÍ TERÉN	214.48	214.51
ODSAZENÍ OD OSY	0.00	5.72

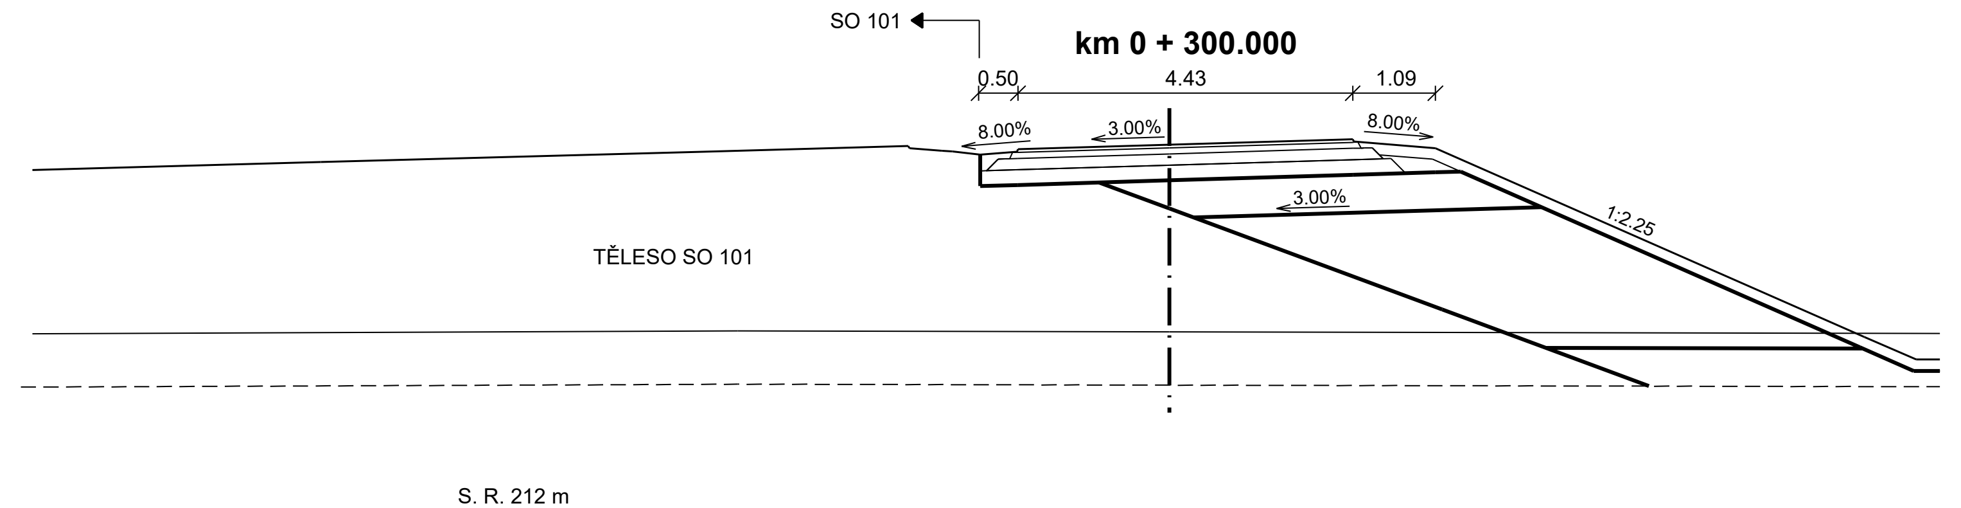
SO 101
km 0 + 300.000
0.50
4.43
1.09
8.00%
3.00%
8.00%
3.00%
1:2.25
TĚLESO SO 101
S. R. 212 m

PROJEKTOVANÝ STAV	217.18	217.25	217.31	217.38	217.26	214.47
ODSAZENÍ OD OSY	-2.50	-2.00	0.00	2.43	3.52	9.88

STÁVAJÍCÍ TERÉN	214.85	214.84
ODSAZENÍ OD OSY	-5.71	0.00

Výškový systém: Bpv

SO 143 Příjezd k DUN v km 1,500

Objednatel:

ŘEDITELSTVÍ SILNIC A DÁLNIC

Ředitelství silnic a dálnic s. p.
Čerčanská 2023/12, Krč, 140 00 Praha 4

Zhotovitel:

Valbek

Valbek, spol. s r.o.
Vaňurova 505/17
460 07 Liberec 3

Vypracoval	Bc. J. HALABURKA		**Zak. číslo**	**21-LI13-001**
Zodp. projektant	ING. T. KLIMENT		**Datum**	**02/2025**
Tech. kontrola	ING. M. HANŽL		**Stupeň**	**PDPS**
Akce			**Počet formátů**	**14 x A4**
I/16 MLADÁ BOLESLAV - MARTINOVICE			**Měřítko**	**1 : 100**
			Č. přílohy	**Paré**
Příloha	PŘÍČNÉ ŘEZY km 0,060 - 0,300		**5**	

Valbek

Zhotovitel:
Valbek, spol. s r.o.
Vaňurova 505/17
460 07 Liberec 3