


SO 144 - PŘÍJEZD K DUN v km 2,600
VZOROVÉ PŘÍČNÉ ŘEZY
M 1 : 50


**KATEGORIE MO1k -/5/30
JEDNOPRUHOVÁ, OBOUSMĚRNÁ**

TŘÍDA DOPRAVNÍHO ZATÍŽENÍ IV
NÁVRHOVÁ ÚROVEŇ PORUŠENÍ D1
TYP PODLOŽÍ PIII (D1-A-2)
D1-N-11, TDZ IV, P III (DLE STARÉHO KATALOGU)


ŘEZ V MÍSTĚ NÁSYPU

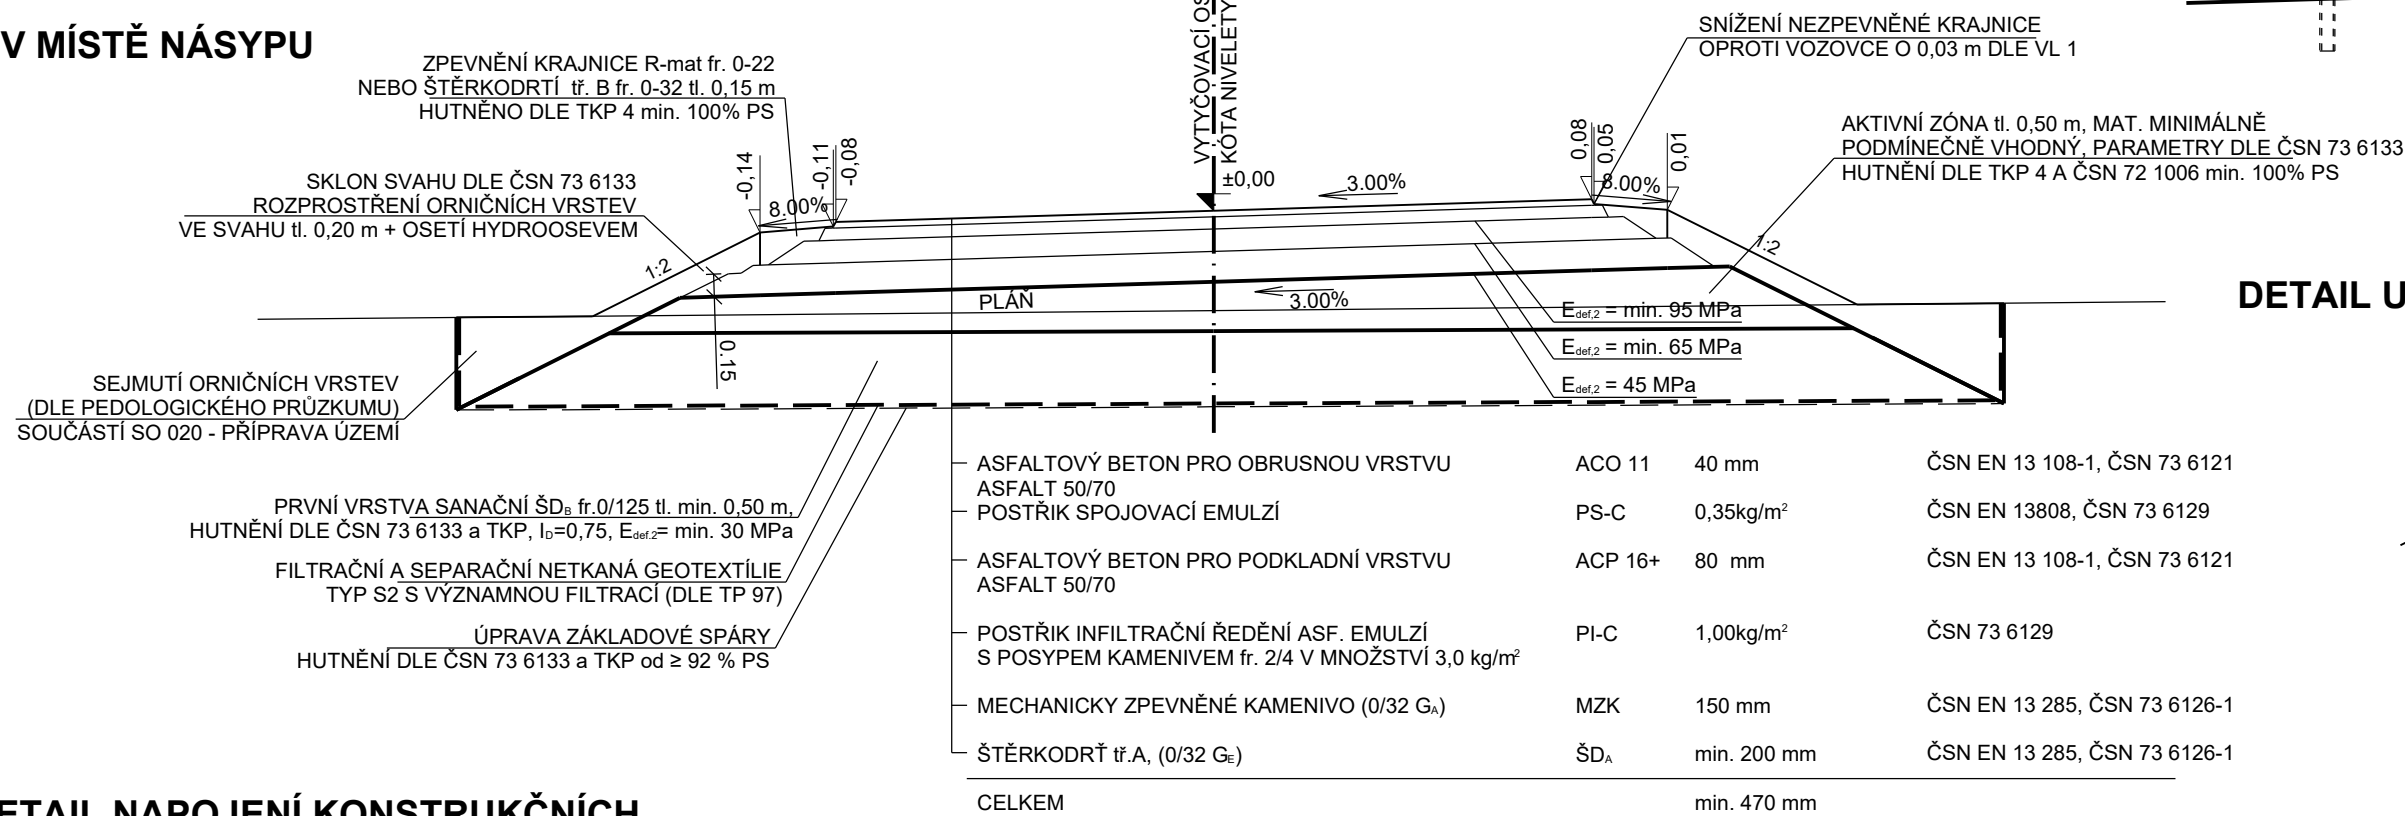


DETAIL NAPOJENÍ KONSTRUKČNÍCH VRSTEV VOZOVKY NA SO 101

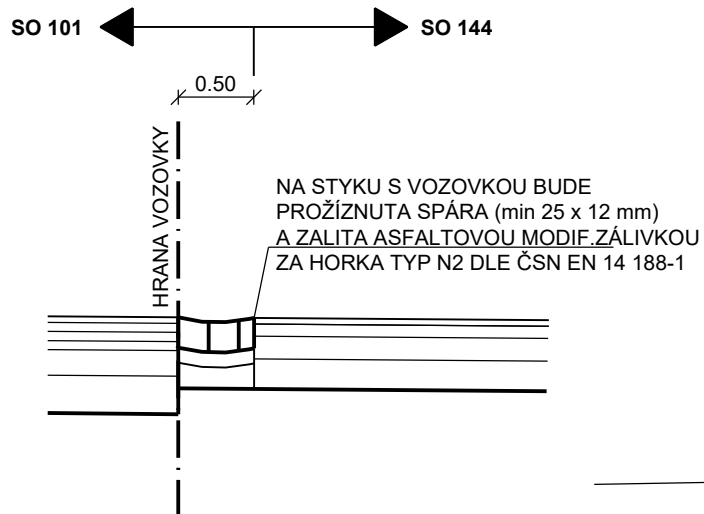

DETAIL V MÍSTĚ KRAJNICE

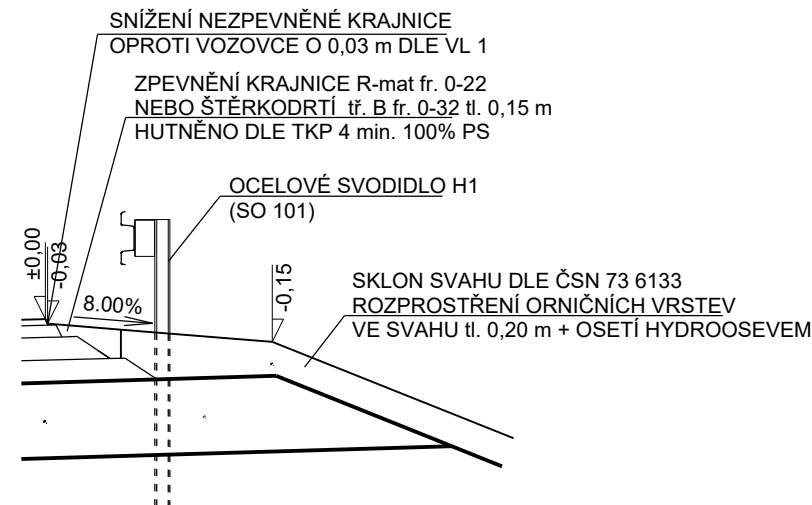

DETAIL UKONČENÍ VRSTEV VOZOVKY

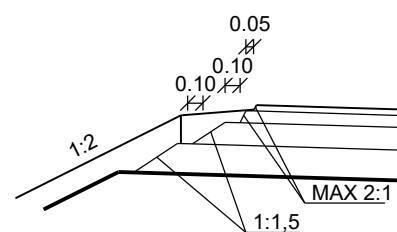

SO 144	Příjezd k DUN v km 2,600
---------------	--------------------------

Objednatel:  ŘEDITELSTVÍ SILNIC A DÁLNIC	Ředitelství silnic a dálnic s. p. Čerčanská 2023/12, Krč, 140 00 Praha 4
---	--

Zhotovitel: 	Valbek, spol. s r.o. Vaňurova 505/17 460 07 Liberec 3
--	---

	Vypracoval Bc. J. HALABURKA	Zak. číslo 21-LI13-001
	Zodp. projektant ING. T. KLIMENT	Datum 02/2025
	Tech. kontrola ING. M. HANŽL	Stupeň PDPS
	Akce I/16 MLADÁ BOLESLAV - MARTINOVICE	Počet formátů 3 x A4
		Měřítko 1 : 50
Zhotovitel: Valbek, spol. s r.o. Vaňurova 505/17 460 07 Liberec 3	Příloha VZOROVÉ PŘÍČNÉ ŘEZY	Č. přílohy Paré 4