
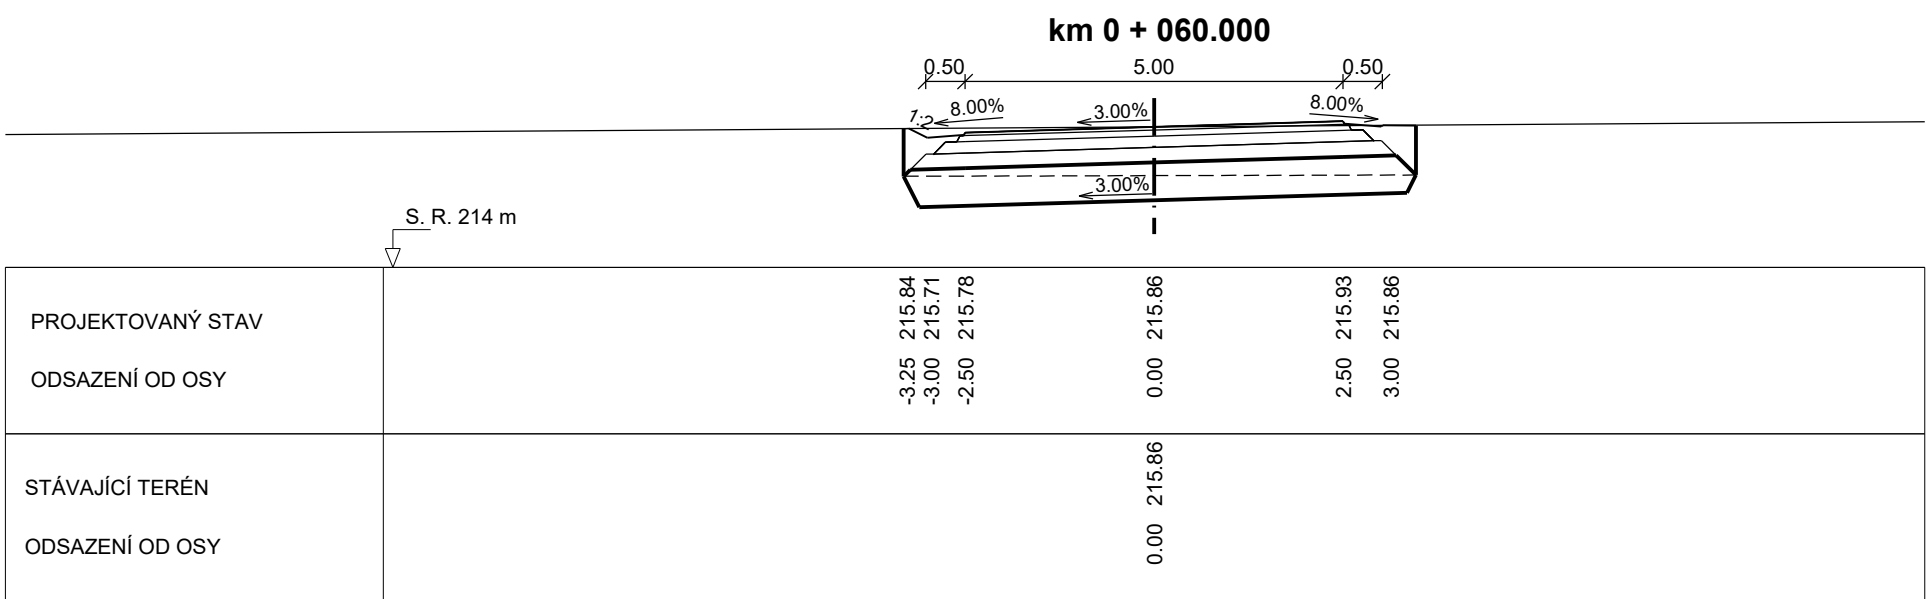
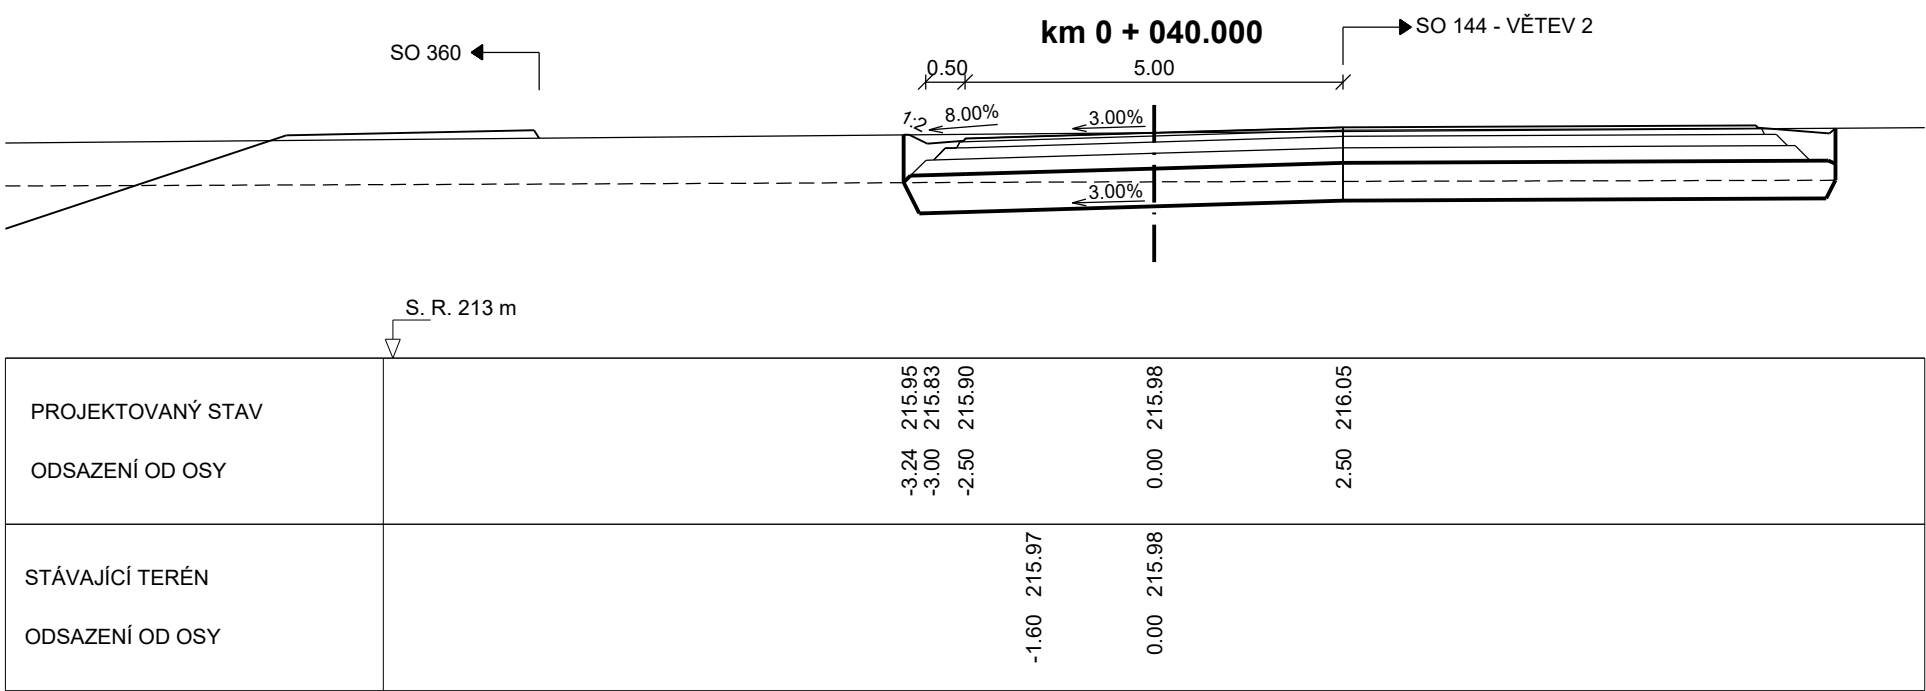


SO 144 - PŘÍJEZD K DUN v km 2,600

PŘÍČNÉ ŘEZY km 0,020 - 0,060

M 1 : 100

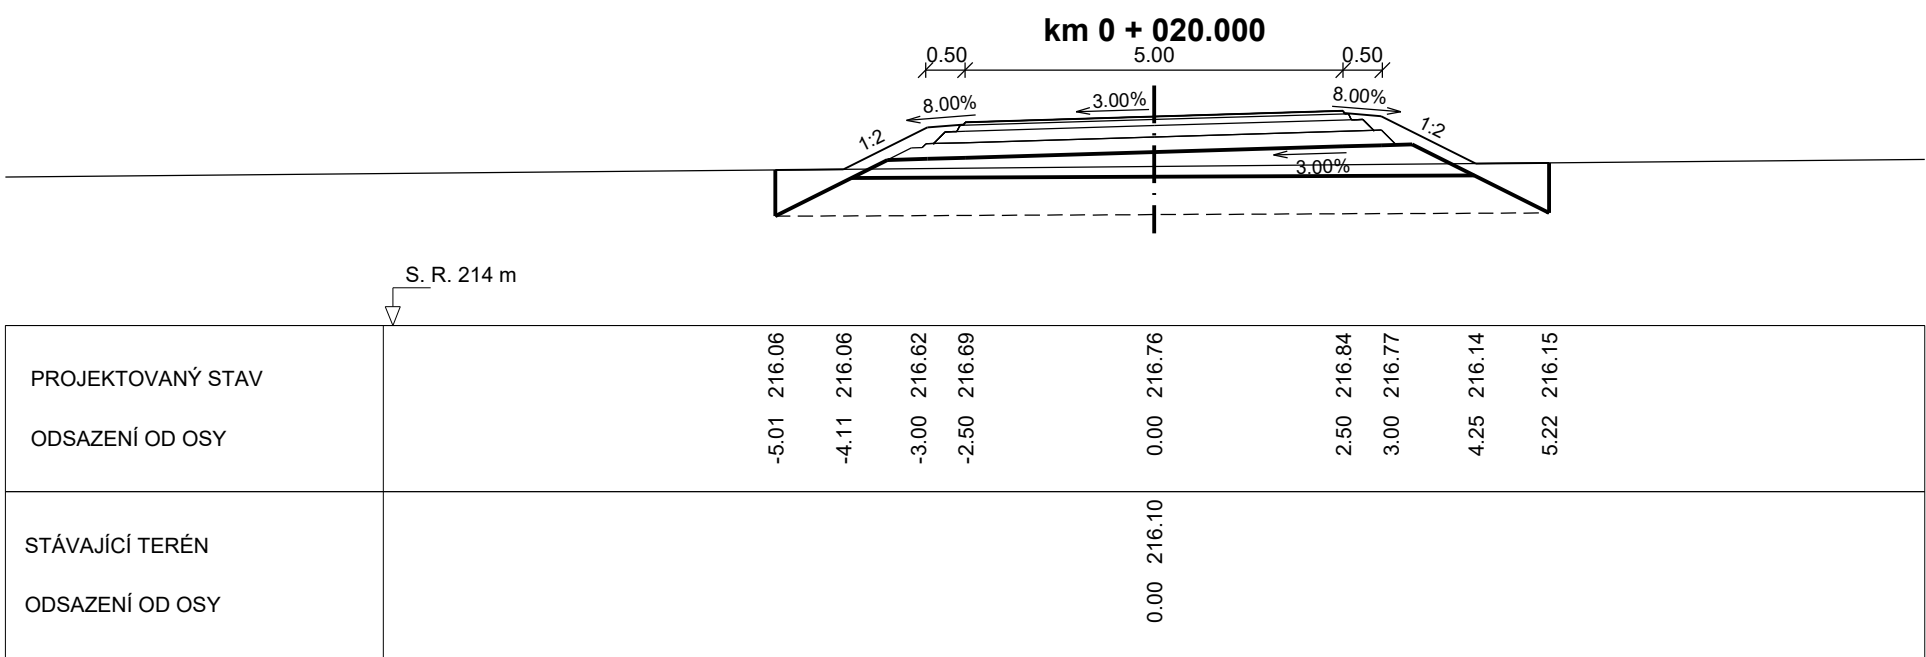

Výškový systém: Bpv

SO 144 Příjezd k DUN v km 2,600

Objednatel:



Ředitelství silnic a dálnic s. p.
Čerčanská 2023/12, Krč, 140 00 Praha 4

Zhotovitel:



Valbek, spol. s r.o.
Vaňurova 505/17
460 07 Liberec 3

	Vypracoval	Bc. J. HALABURKA	Zak. číslo	21-LH13-001
	Zodp. projektant	ING. T. KLIMENT	Datum	02/2025
	Tech. kontrola	ING. M. HANŽL	Stupeň	PDPS
	Akce I/16 MLADÁ BOLESLAV - MARTINOVICE		Počet formátů	6 x A4
			Měřítko	1 : 100
Zhotovitel: Valbek, spol. s r.o. Vaňurova 505/17 460 07 Liberec 3	Příloha PŘÍČNÉ ŘEZY km 0,020 - 0,060		5	Paré