



SO 144 - PŘÍJEZD K DUN V km 2,600
PROPUSTEK v km 0,014
M 1 : 50


PŮDORYS

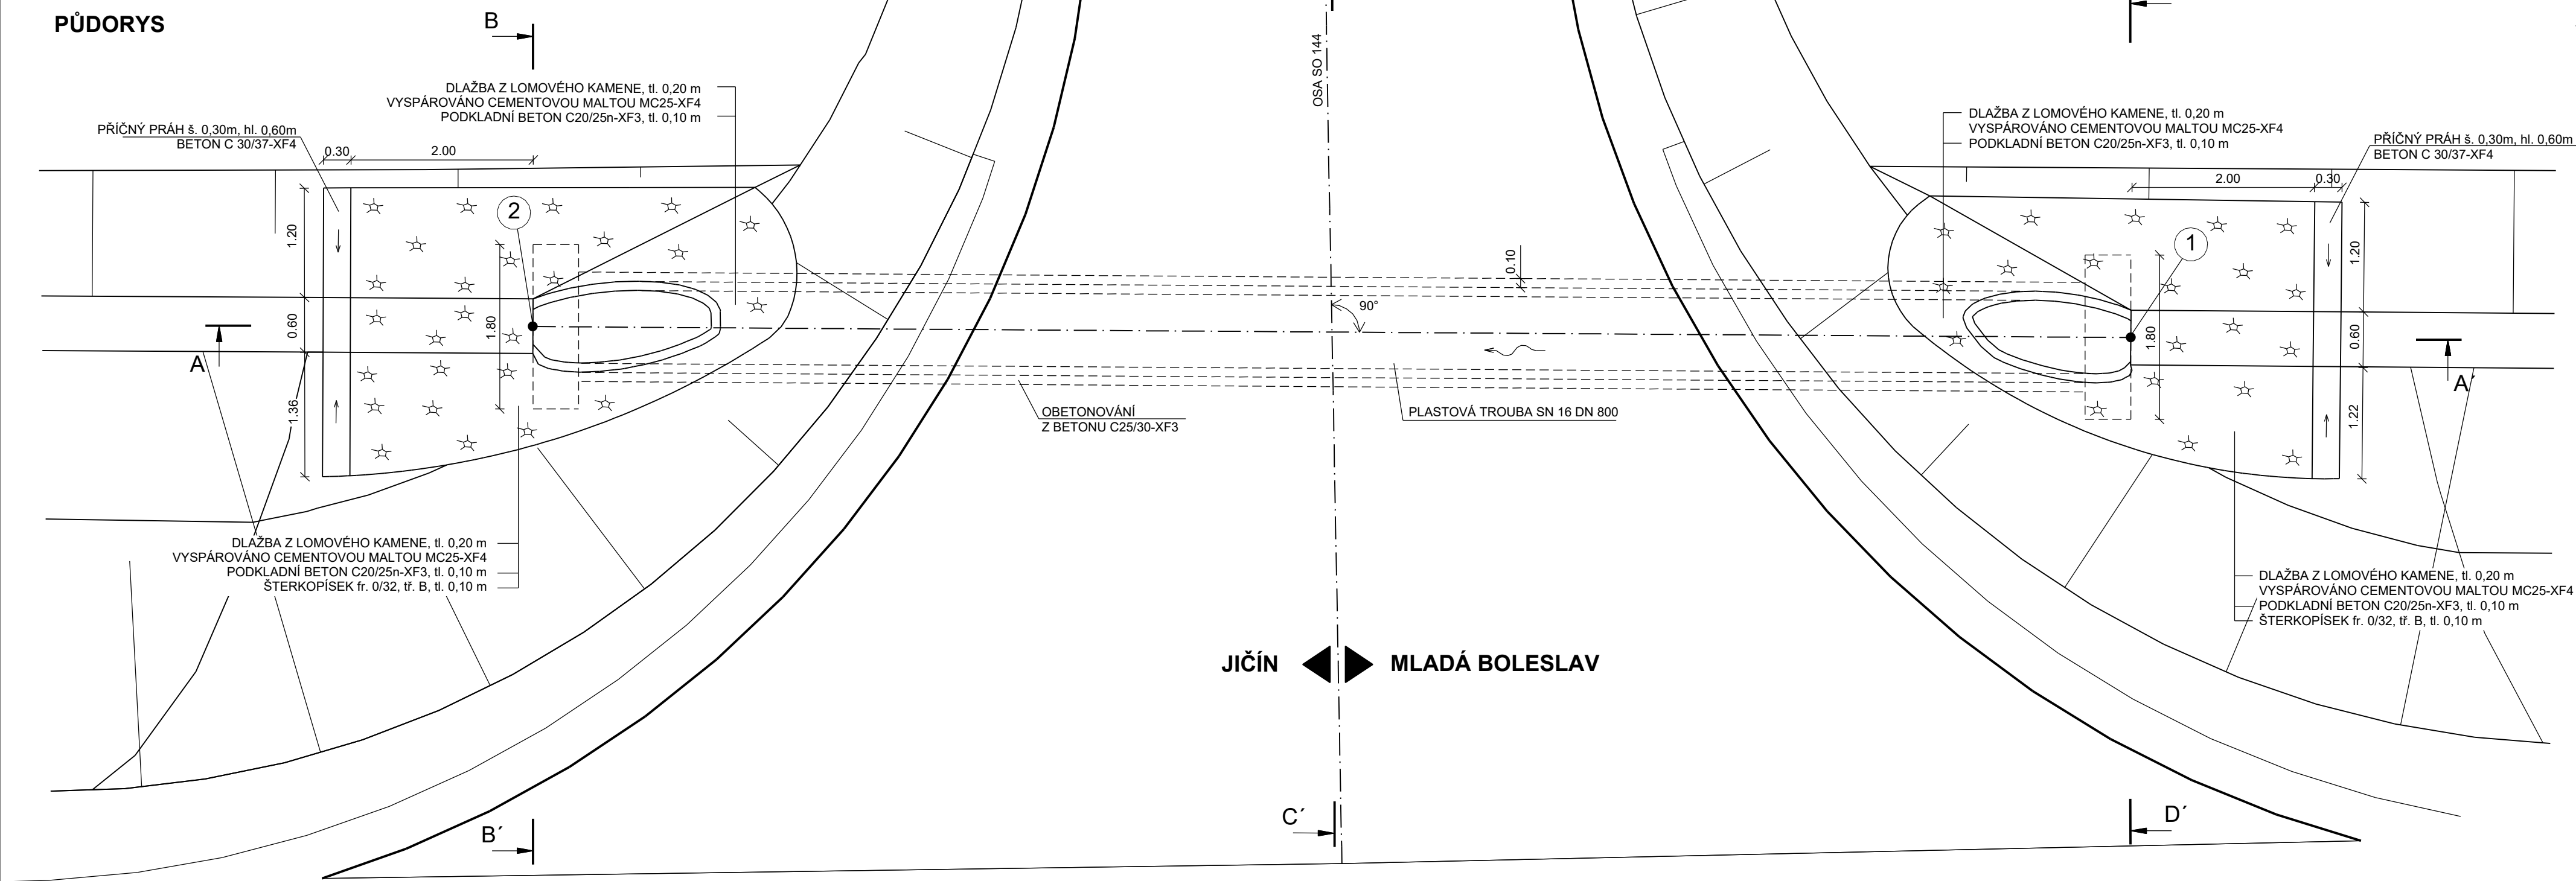

PODÉLNÝ ŘEZ A-A'

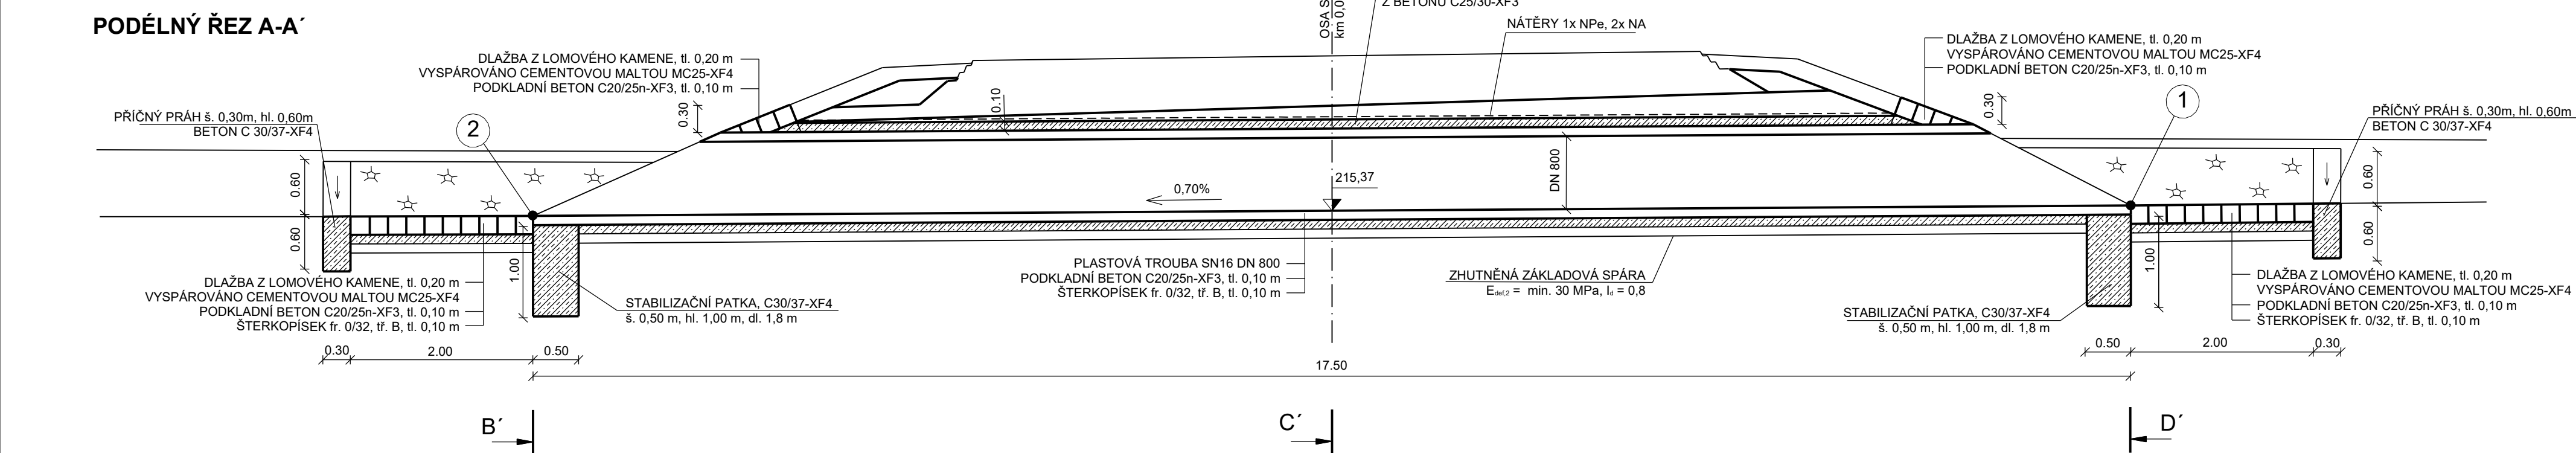


POHLED NA VÝTOK ŘEZ B-B'

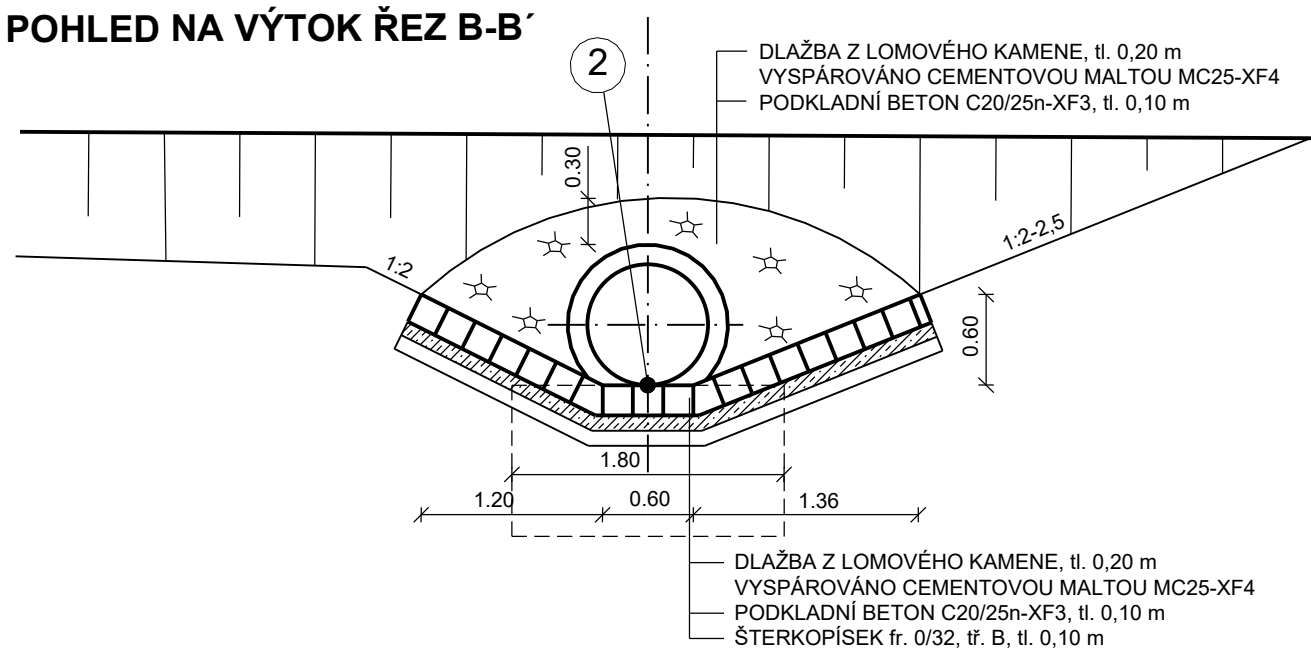


POZNÁMKY:

- SPÁROVÁNÍ DLAŽBY Z LOMOVÉHO KAMENE BUDE VYPLNĚNÉ CEMENTOVOU MALTOU MC25-XF4, tl. min. 0,20 m
- OBETONOVÁNÍ V MÍSTĚ HRDLA MINIMÁLNĚ 0,10 m
- VŠECHNY BETONOVÉ PRVKY, KTERÉ PŘIJÍDOU DO STYKU SE ZEMINOU MUSÍ BYT OPATŘENY NÁTĚRY: 1x NP_e A 2x NA
- VYTÝČENÍ BUDE PROVEDENO DLE TKP 1 A SOUVEJÍJÍCÍCH PŘEDPISŮ
- SKLONY SVAHŮ JSOU URČENY SKLODEM SILNIČNÍHO TĚLESA A PŘÍLEHLÝCH PŘÍKOPŮ
- ŠÍŘE PODKLADNÍHO PRAHU JE 0,50 m NA KAŽDOU STRANU OD VNĚJŠÍHO OBRYSU TROUBY
- BETONOVÉ VYROBKY VYSTAVENÉ PŘÍMÉMU OSTRÍKU ROZMRAZOVACÍCH PROSTŘEDKŮ A MRAZU A UMÍSTĚNÉ VE ZVZDÁLENOSTI MOŽNÉHO OSTRÍKU (OD HRANY VOZOVKY 10 m VČETNĚ SOLNĚ MLHY) MUSÍ SPLŇOVAT POŽADAVKY NA STUPEŇ VLIVU PROSTŘEDÍ XF4.

POHLED NA VTOK ŘEZ D-D'

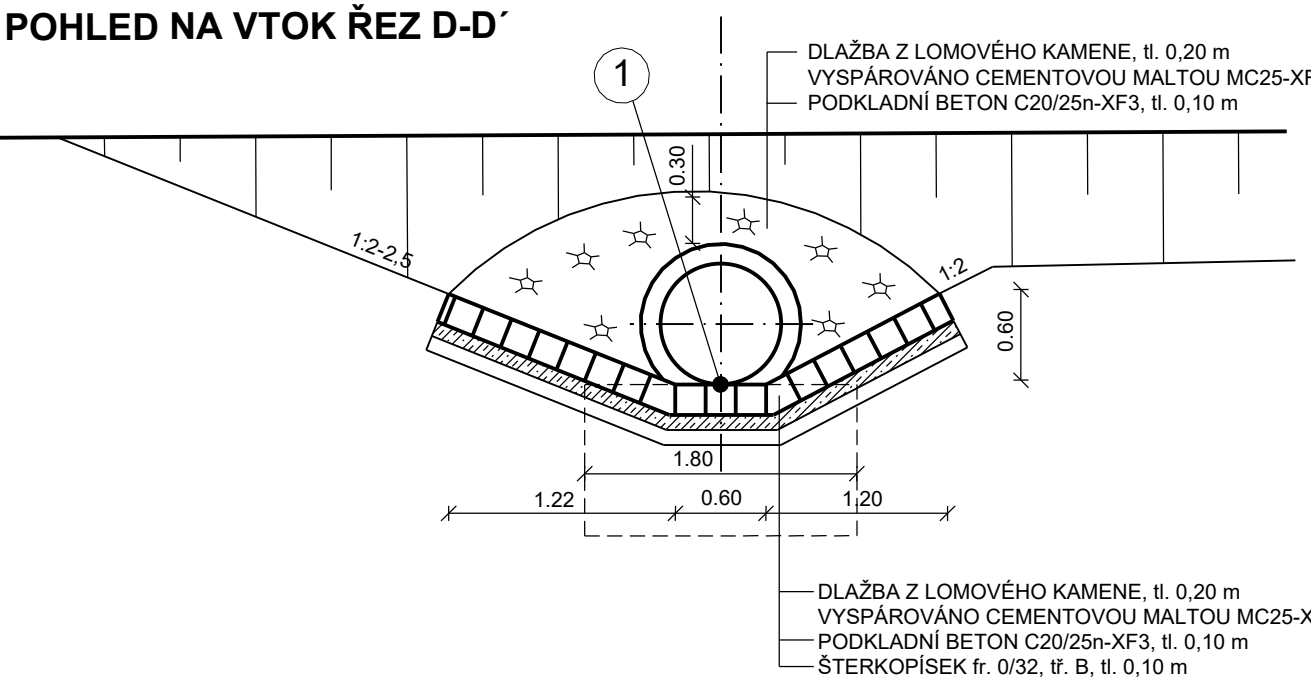

PŘÍČNÝ ŘEZ C-C'

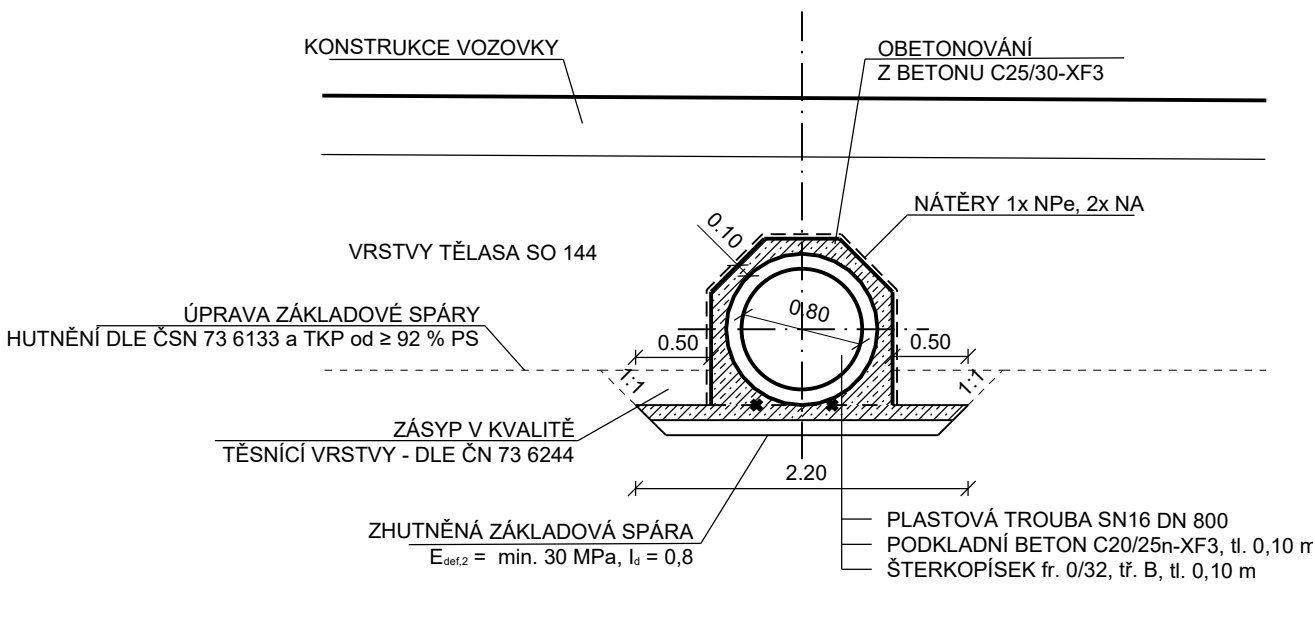

PARAMETRY PROPUSTKŮ					VÝTYČOVANÉ BODY		
STANIČENÍ [km]	TROUBA DN [mm]	DĚLKA DL [m]	SKLON S. [%]	ÚHEL α [°]	VTOK - 01 Y / X [S-JTSK] / Z [Bpv]	VÝTOK - 02 Y / X [S-JTSK] / Z [Bpv]	
0,014	800	17,50	0,70	90	698546.802 / 1011531.227 / 215.459	698529.579 / 1011534.352 / 215.345	

Souřadnicový systém: S-JTSK
Výškový systém: Bpv

SO 144 Příjezd k DUN v km 2,600

Objednatel:

**ŘEDITELSTVÍ
SILNIC
A DÁLNIC**

Ředitelství silnic a dálnic s. p.
Čerčanská 2023/12, Krč, 140 00 Praha 4

Zhotovitel:

**Valbek**

Valbek, spol. s r.o.
Vaňurova 505/17
460 07 Liberec 3

	Vypracoval	Bc. J. HALABURKA	Zak. číslo	21-LI13-001
	Zodp. projektant	ING. T. KLIMENT	Datum	02/2025
	Tech. kontrola	ING. M. HANŽL	Stupeň	PDPS
	Akce	I/16 MLADÁ BOLESLAV - MARTINOVICE		Počet formátů
Měřítka	1 : 50			
Č. přílohy	Paré			
Zhotovitel: Valbek, spol. s r.o. Vaňurova 505/17 460 07 Liberec 3	Příloha	PROPUSTEK v km 0,014		6