


SO 145 - PŘÍJEZD K DUN v km 2,760
SITUACE
M 1 : 1000

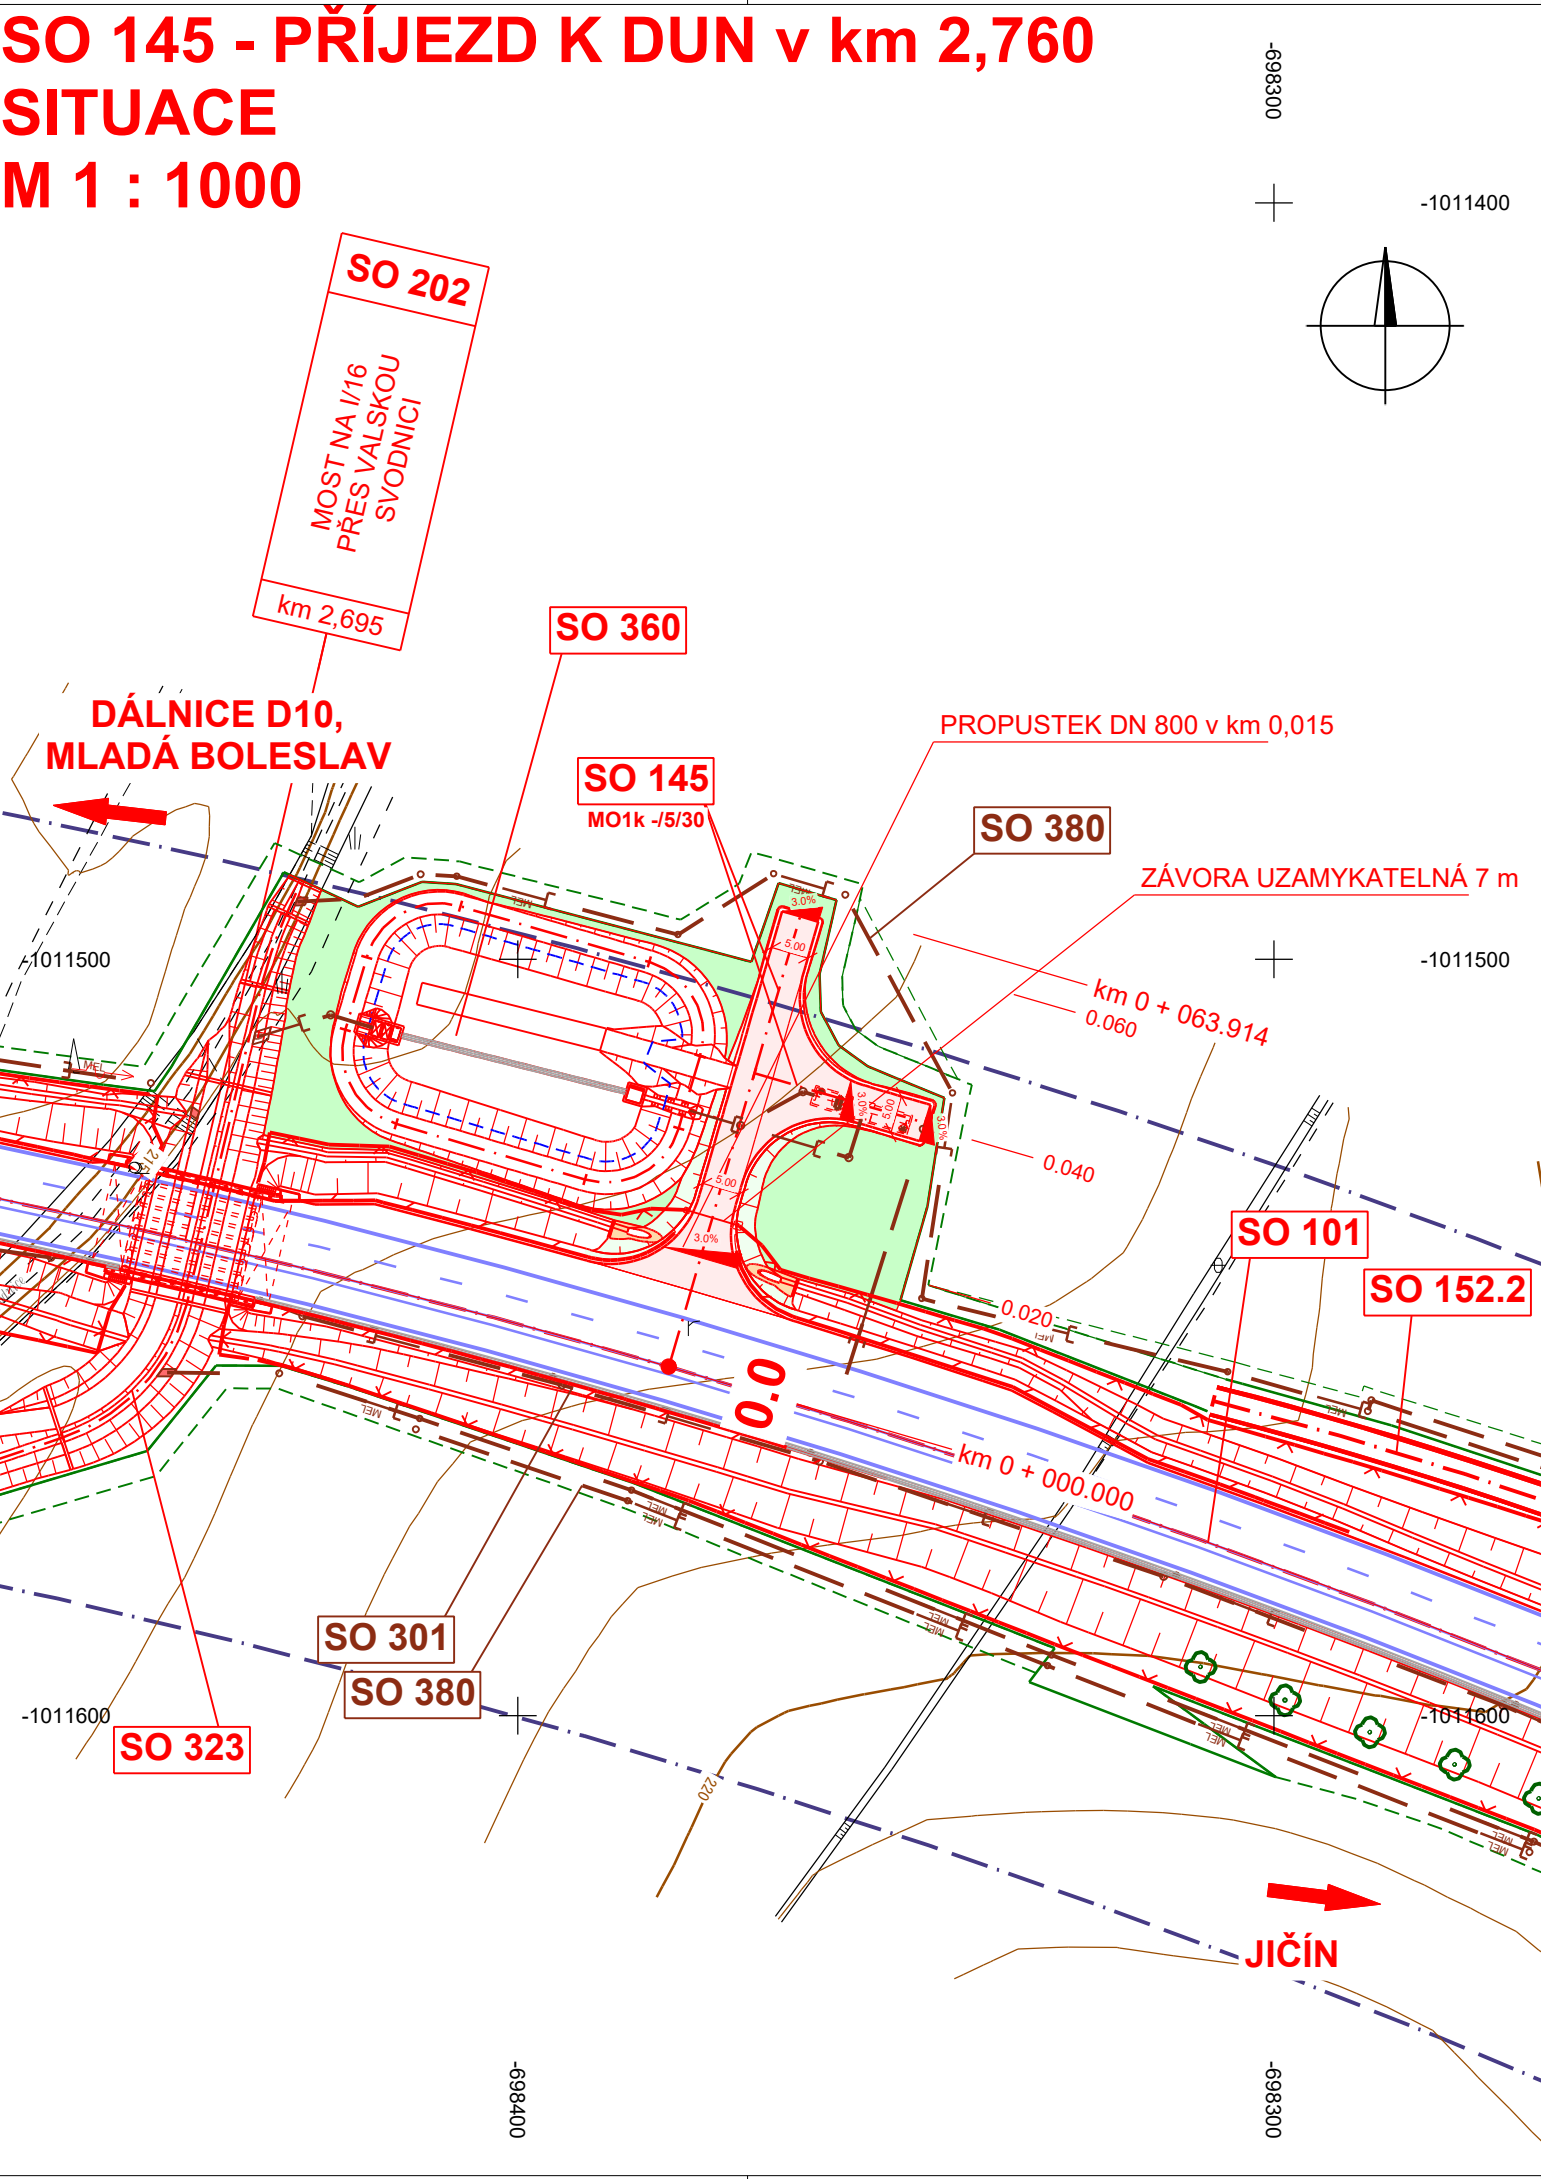

LEGENDA:

- PLOCHY
- VOZOVKA - ASFALTOVÝ KRYT
 - VOZOVKA - FRÉZOVANÁ
 - VOZOVKA - POLNÍ CESTY
 - CHODNÍK
 - DLAŽBA VOZOVKY
 - SVAHY VÝKOPU
 - SVAHY NÁSYPU
 - VEGETAČNÍ ÚPRAVY
- OBVOD STAVBY
- TRVALÝ ZÁBOR
 - DOČASNÝ ZÁBOR
- NOVÉ IS
- DEŠŤOVÁ KANALIZACE
 - MELIORACE
 - VÝTLAK
 - VODOVOD
 - NADZEMNÍ VEDENÍ NN
 - NADZEMNÍ VEDENÍ VN
 - PODZEMNÍ VEDENÍ NN
 - PODZEMNÍ SDĚLOVACÍ VEDENÍ
 - PLYNOVOD - STL
- STÁVAJÍCÍ IS - INFORMATIVNÍ ZÁKRES
- PODZEMNÍ VEDENÍ NN
 - PODZEMNÍ VEDENÍ VN
 - NADZEMNÍ VEDENÍ NN
 - NADZEMNÍ VEDENÍ VN
 - NADZEMNÍ VEDENÍ VVN
 - DEŠŤOVÁ KANALIZACE
 - PLYNOVOD - STL
 - PODZEMNÍ SDĚLOVACÍ VEDENÍ
 - VODOVOD

Souřadnicový systém: S-JTSK
Výškový systém: Bpv

SO 145 Příjezd k DUN v km 2,760

Objednatel:



**ŘEDITELSTVÍ
SILNIC
A DÁLNIC**

Ředitelství silnic a dálnic s. p.
Čerčanská 2023/12, Krč, 140 00 Praha 4

Zhotovitel:



Valbek

Valbek, spol. s r.o.
Vaňurova 505/17
460 07 Liberec 3

 Valbek	Vypracoval	Bc. J. HALABURKA	Zak. číslo	21-LI13-001
	Zodp. projektant	ING. T. KLIMENT	Datum	02/2025
	Tech. kontrola	ING. M. HANŽL	Stupeň	PDPS
	Akce I/16 MLADÁ BOLESLAV - MARTINOVICE		Počet formátů	2 x A4
			Měřítko	1 : 1000
Zhotovitel: Valbek, spol. s r.o. Vaňurova 505/17 460 07 Liberec 3	Příloha	SITUACE		Č. přílohy 2 Paré