SO 145 - PŘÍJEZD K DUN v km 2,760
VZOROVÉ PŘÍČNÉ ŘEZY
M 1 : 50

KATEGORIE MO1k -/5/30
JEDNOPRUHOVÁ, OBOUSMĚRNÁ

TŘÍDA DOPRAVNÍHO ZATÍŽENÍ IV
NÁVRHOVÁ ÚROVEŇ PORUŠENÍ D1
TYP PODLOŽÍ PIII (D1-A-2)
D1-N-11, TDZ IV, P III (DLE STARÉHO KATALOGU)

ŘEZ V MÍSTĚ NÁSYPU

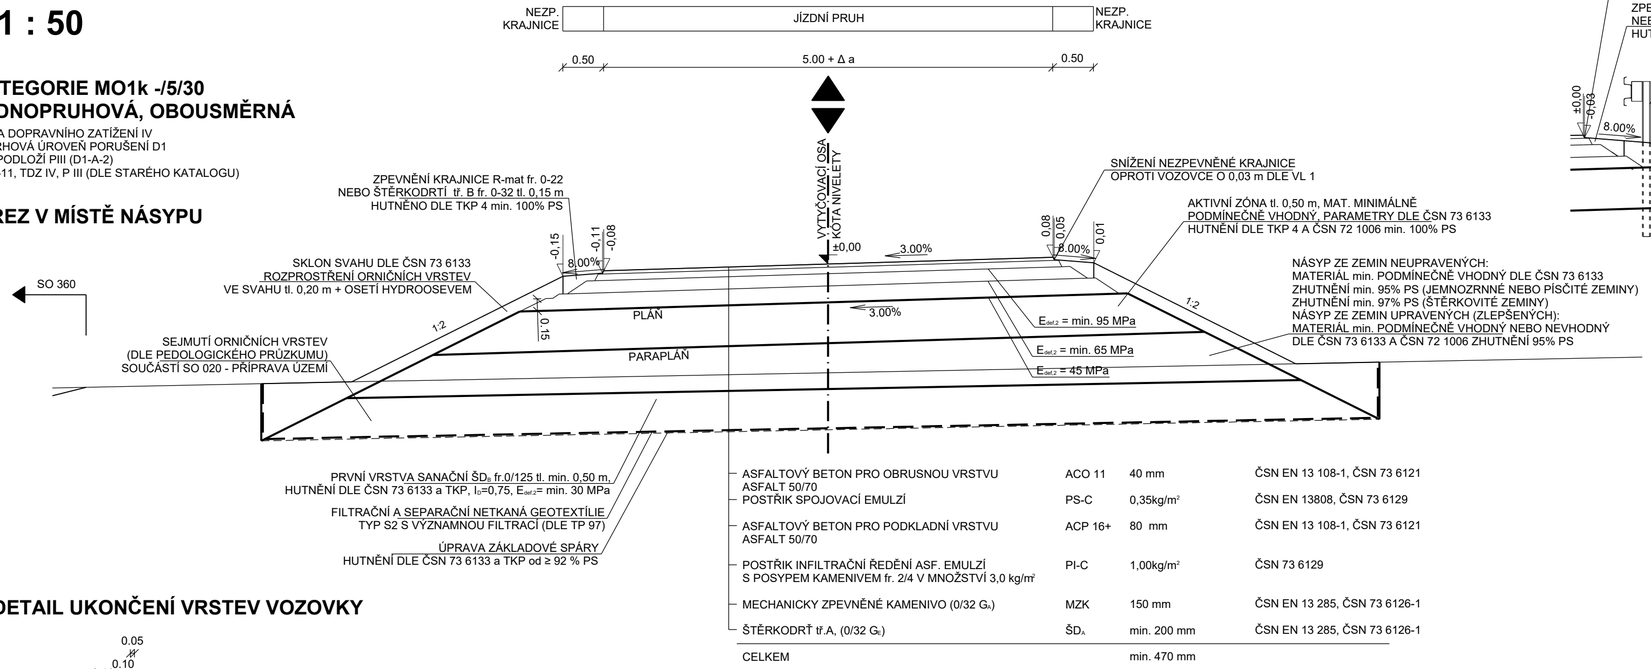

ASFALTOVÝ BETON PRO OBRUSNOU VRSTVU ASFALT 50/70	ACO 11	40 mm	ČSN EN 13 108-1, ČSN 73 6121
POSTŘIK SPOJOVACÍ EMULZÍ	PS-C	0,35kg/m²	ČSN EN 13808, ČSN 73 6129
ASFALTOVÝ BETON PRO PODKLADNÍ VRSTVU ASFALT 50/70	ACP 16+	80 mm	ČSN EN 13 108-1, ČSN 73 6121
POSTŘIK INFILTRAČNÍ ŘEDĚNÍ ASF. EMULZÍ S POSYPEM KAMENIVEM fr. 2/4 V MNOŽSTVÍ 3,0 kg/m²	PI-C	1,00kg/m²	ČSN 73 6129
MECHANICKY ZPEVNĚNÉ KAMENIVO (0/32 G_A)	MZK	150 mm	ČSN EN 13 285, ČSN 73 6126-1
ŠTĚRKODRŤ tř.A, (0/32 G_B)	$ŠD_A$	min. 200 mm	ČSN EN 13 285, ČSN 73 6126-1
CELKEM		min. 470 mm	

DETAIL V MÍSTĚ KRAJNICE

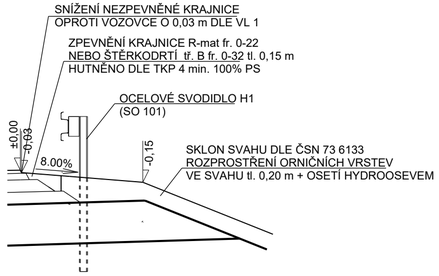

DETAIL UKONČENÍ VRSTEV VOZOVKY

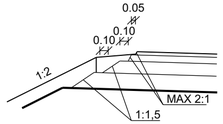

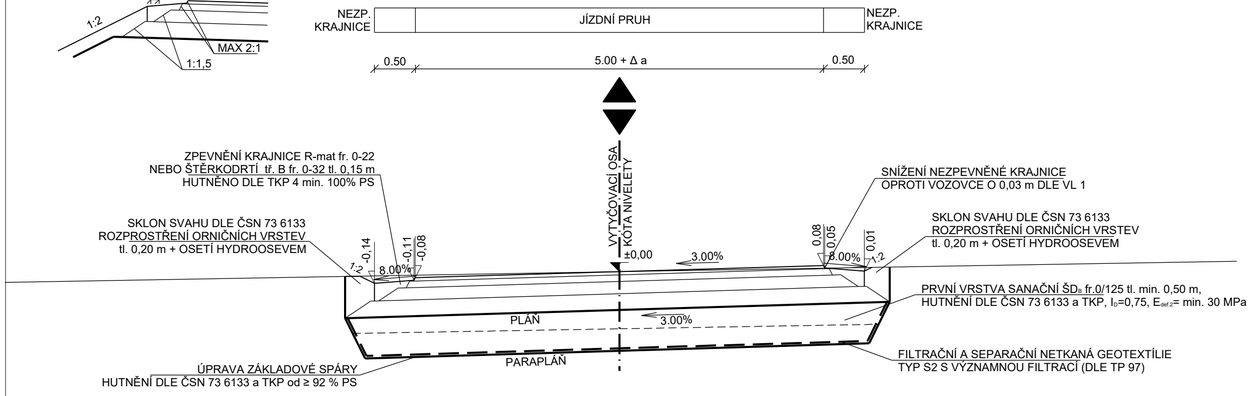

DETAIL NAPOJENÍ KONSTRUKČNÍCH VRSTEV VOZOVKY NA SO 101

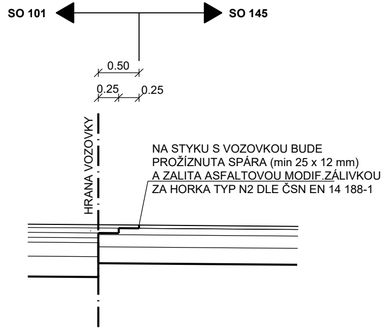

SO 145 Příjezd k DUN v km 2,760

Objednatel:
ŘEDITELSTVÍ SILNIC A DÁLNIC
Ředitelství silnic a dálnic s. p.
Čerčanská 2023/12, Krč, 140 00 Praha 4

Zhotovitel:
Valbek
Valbek, spol. s r.o.
Vaňurova 505/17
460 07 Liberec 3

Valbek	Vypracoval	Bc. J. HALABURKA		Zak. číslo	21-LI13-001
	Zodp. projektant	ING. T. KLIMENT		Datum	02/2025
	Tech. kontrola	ING. M. HANŽL		Stupeň	PDPS
	Akce: **I/16 MLADÁ BOLESLAV - MARTINOVICE**			Počet formátů	3 x A4
				Měřítko	1 : 50
				Č. přílohy	Paré
Zhotovitel: Valbek, spol. s r.o. Vaňurova 505/17 460 07 Liberec 3	Příloha: VZOROVÉ PŘÍČNÉ ŘEZY			4	