



SO 145 - PŘÍJEZD K DUN v km 2,760

PŘÍČNÉ ŘEZY km 0,020 - 0,060


M 1 : 100

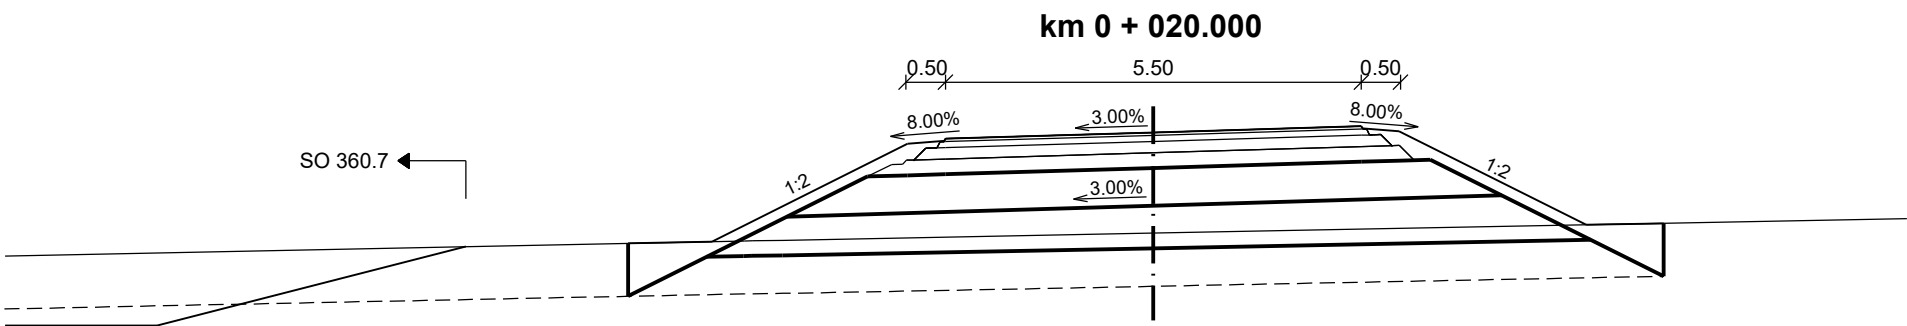

		S. R. 214 m																	
PROJEKTOVANÝ STAV																			
ODSAZENÍ OD OSY																			

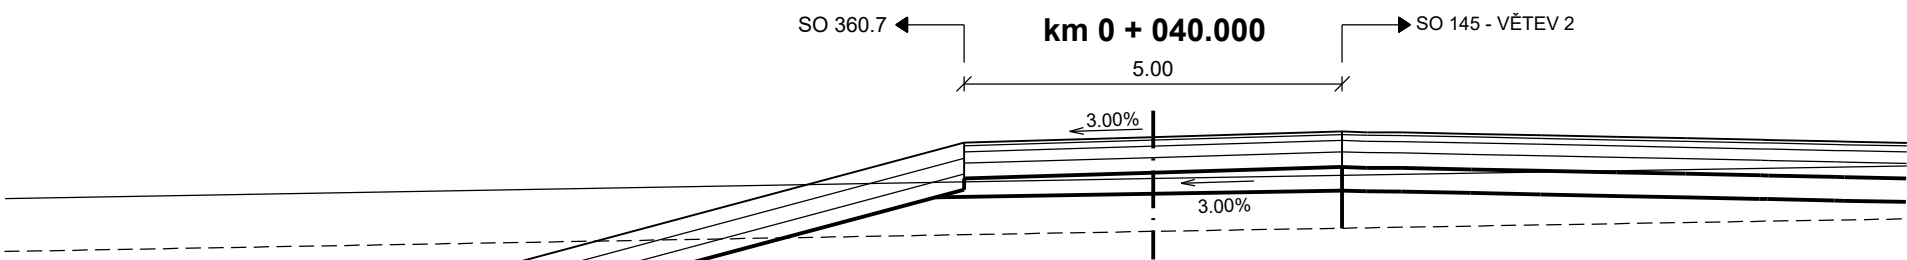

		S. R. 214 m			
PROJEKTOVANÝ STAV					
ODSAZENÍ OD OSY			-2.50	217.42	0.00 217.49 2.50 217.57
STÁVAJÍCÍ TERÉN					
ODSAZENÍ OD OSY			-1.14	216.93	0.00 216.95

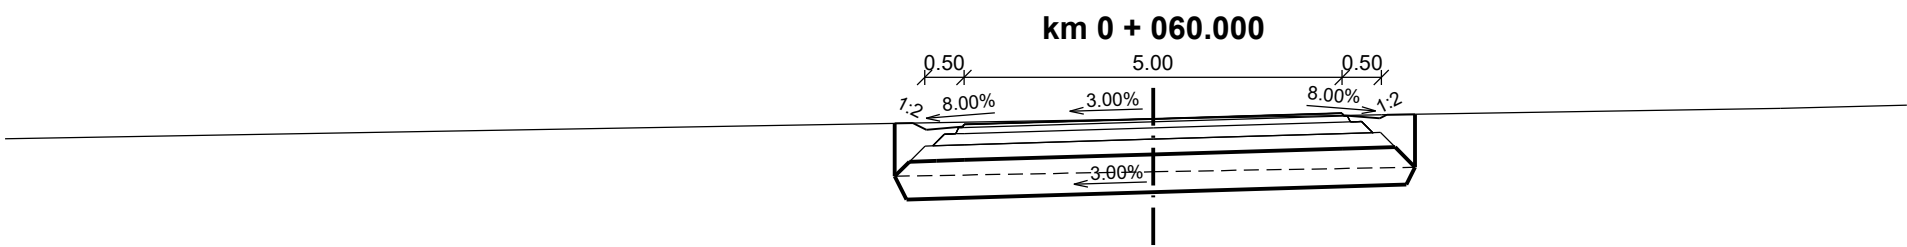

--	--	

Výškový systém: Bpv

SO 145 Příjezd k DUN v km 2,760

Objednatel:



**ŘEDITELSTVÍ
SILNIC
A DÁLNIC**

Ředitelství silnic a dálnic s. p.
Čerčanská 2023/12, Krč, 140 00 Praha 4

Zhotovitel:



Valbek

Valbek, spol. s r.o.
Vaňurova 505/17
460 07 Liberec 3

	Vypracoval	Bc. J. HALABURKA		Zak. číslo	21-LH13-001
	Zodp. projektant	ING. T. KLIMENT		Datum	02/2025
	Tech. kontrola	ING. M. HANŽL		Stupeň	PDPS
	Akce I/16 MLADÁ BOLESLAV - MARTINOVICE			Počet formátů	6 x A4
				Měřítko	1 : 100
Zhotovitel: Valbek, spol. s r.o. Vaňurova 505/17 460 07 Liberec 3	Příloha PŘÍČNÉ ŘEZY km 0,020 - 0,060			5	Paré