



SO 145 - PŘÍJEZD K DUN V km 2,760
PROPUSTEK v km 0,015
M 1 : 50


PŮDORYS

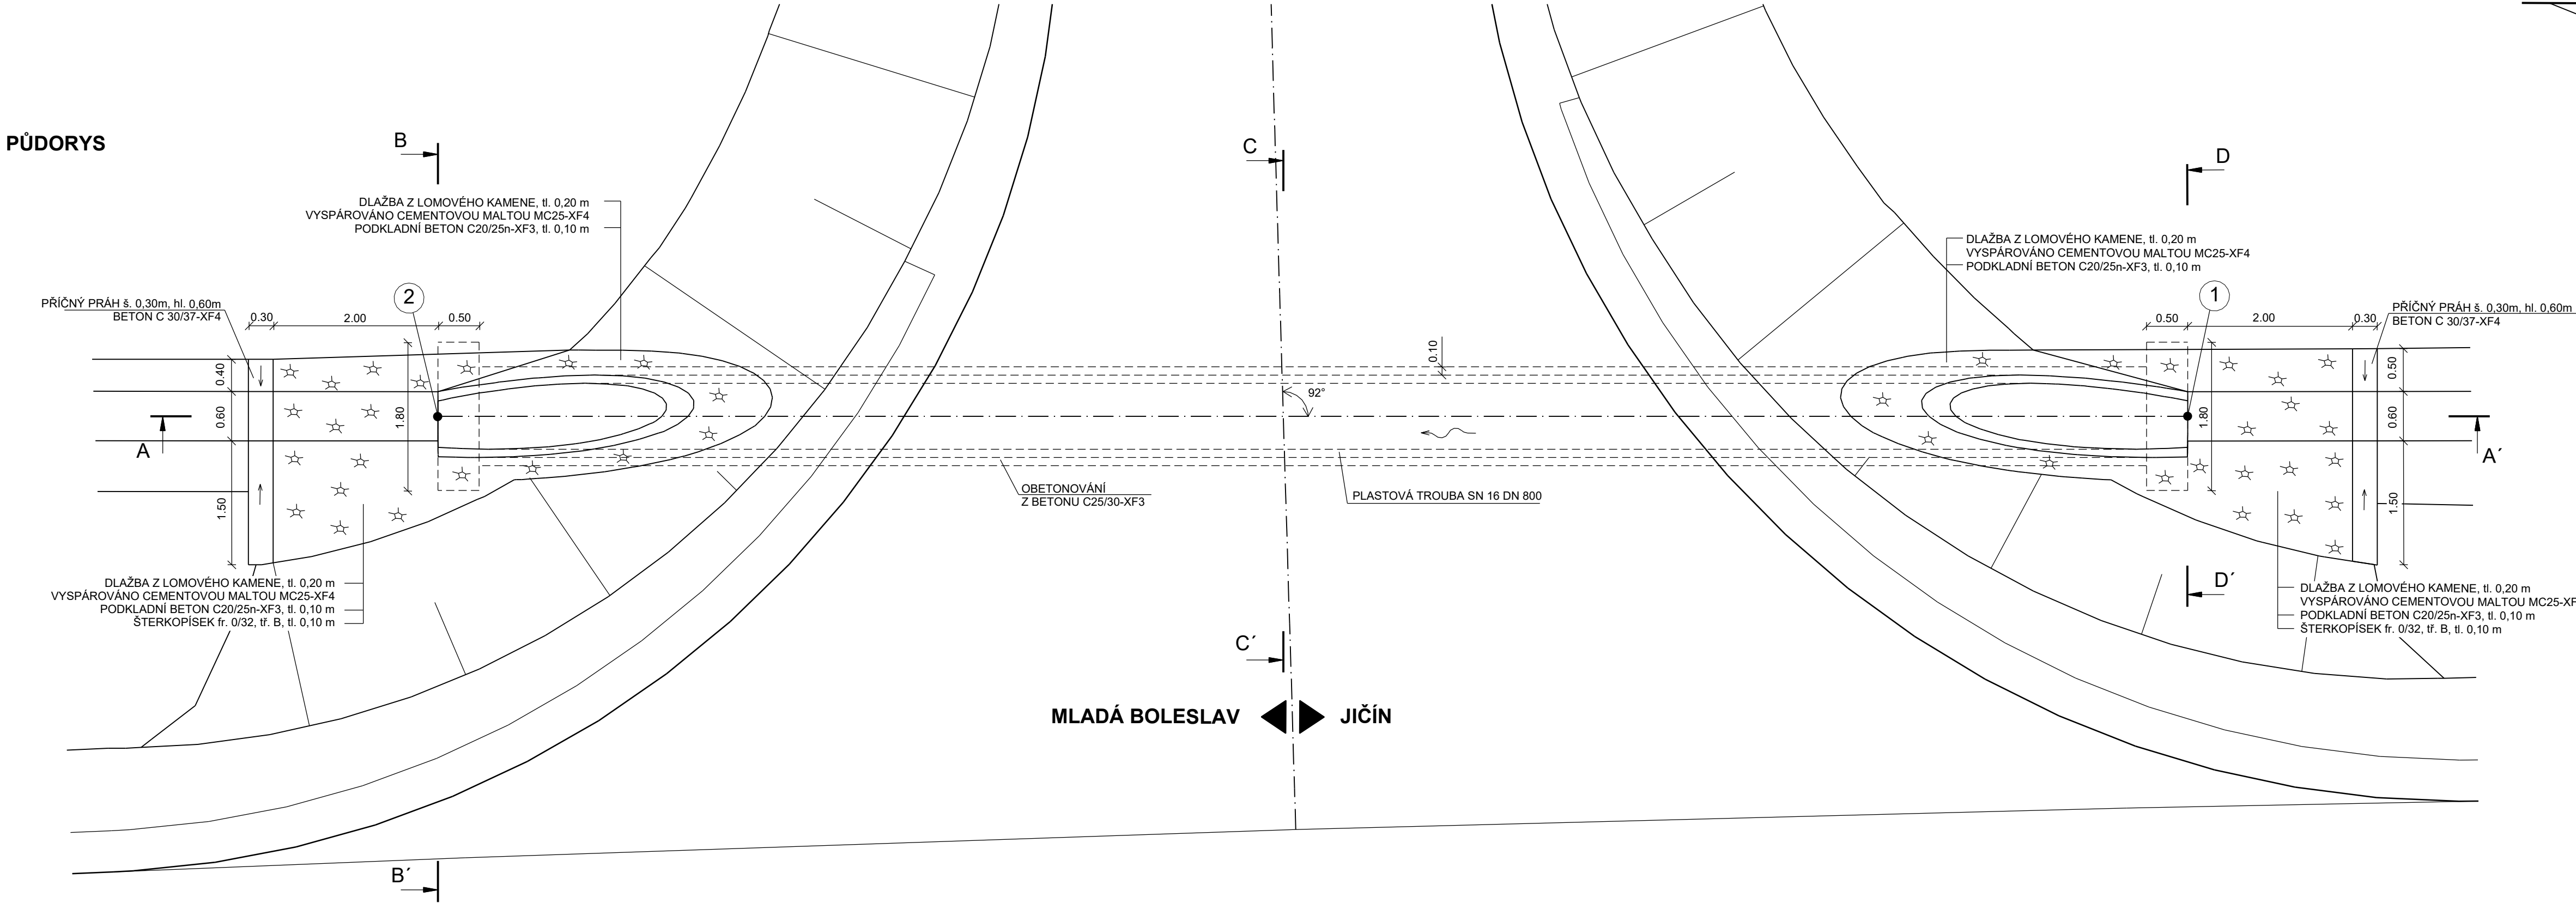


PODÉLNÝ ŘEZ A-A'

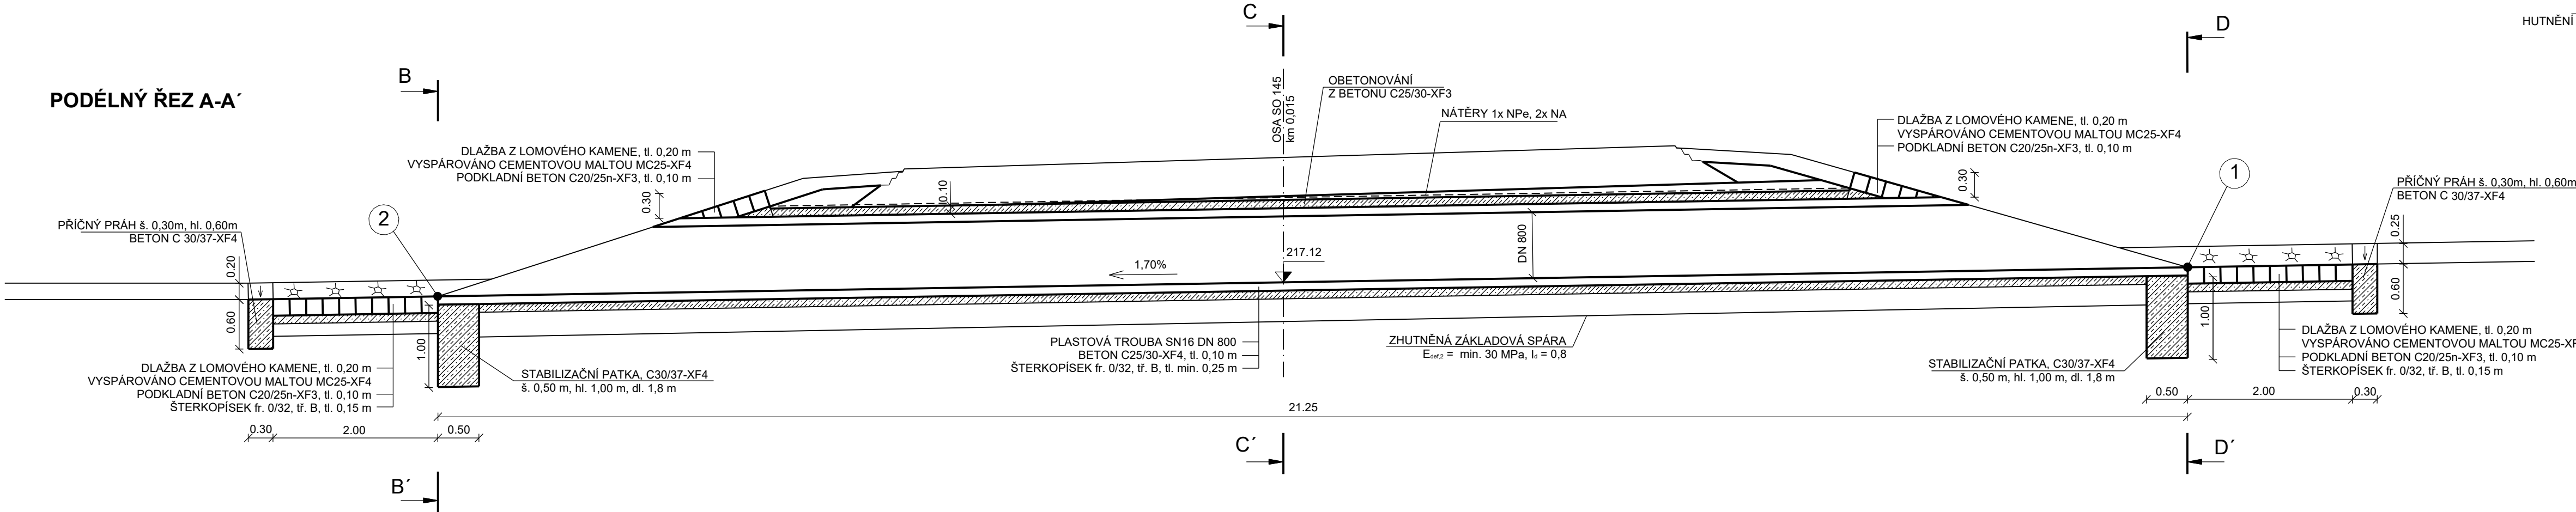


POHLED NA VTOK ŘEZ D-D'

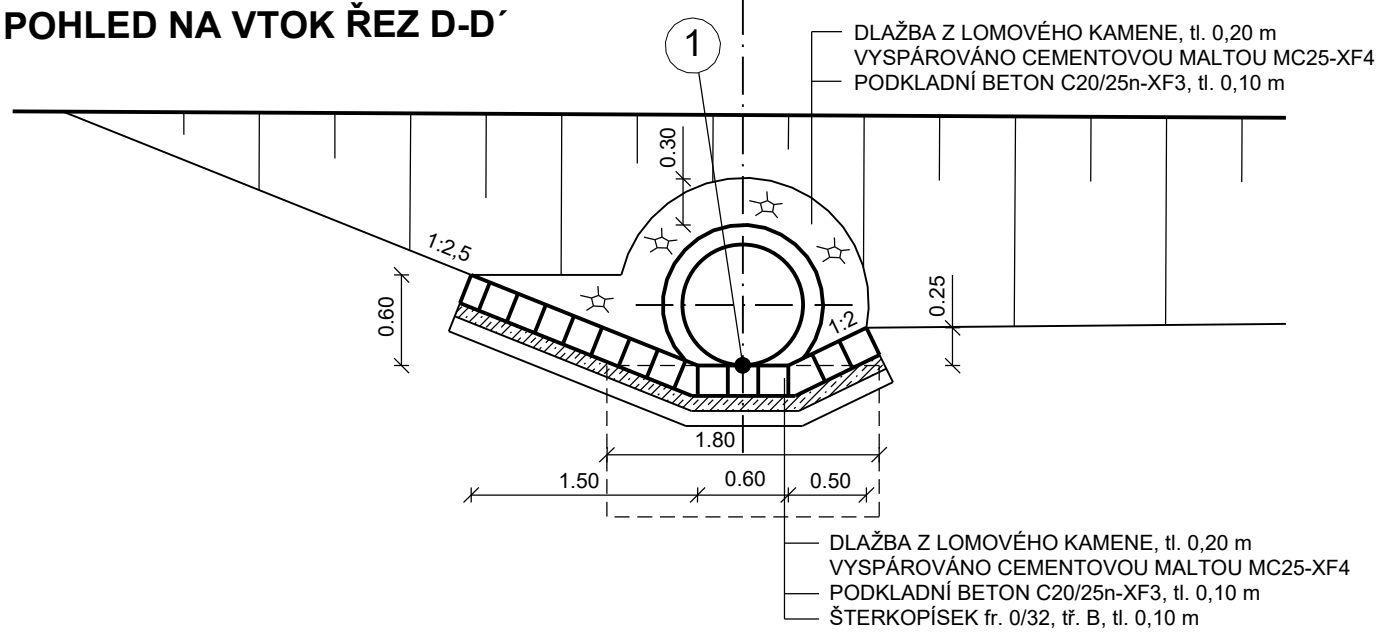

POHLED NA VÝTOK ŘEZ B-B'

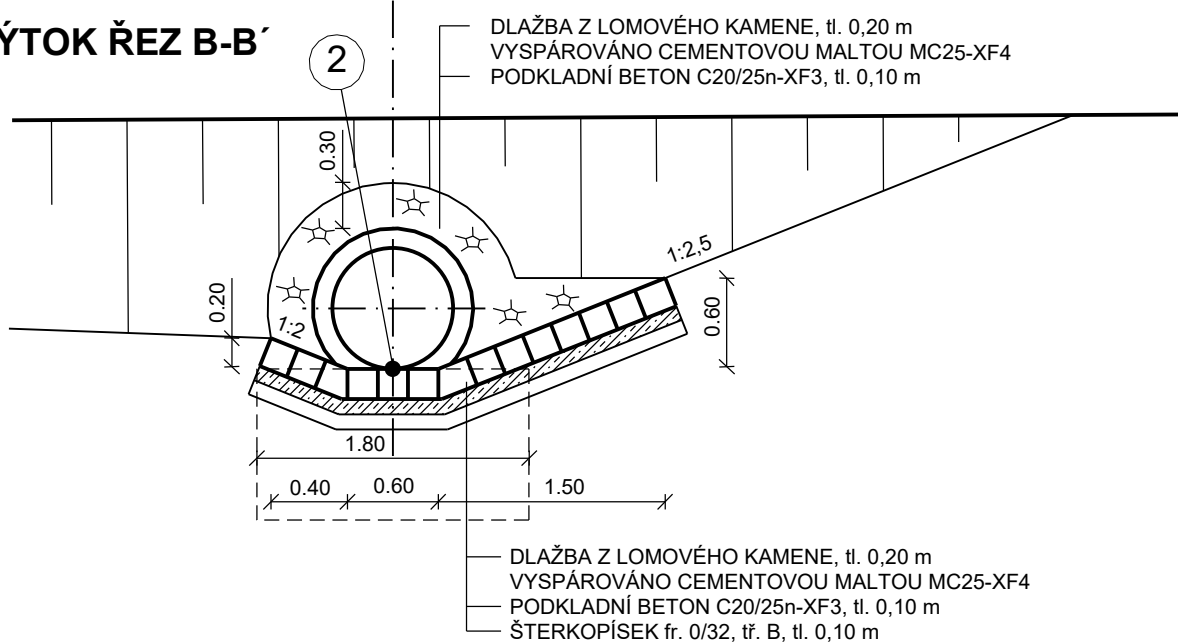

PŘÍČNÝ ŘEZ C-C'

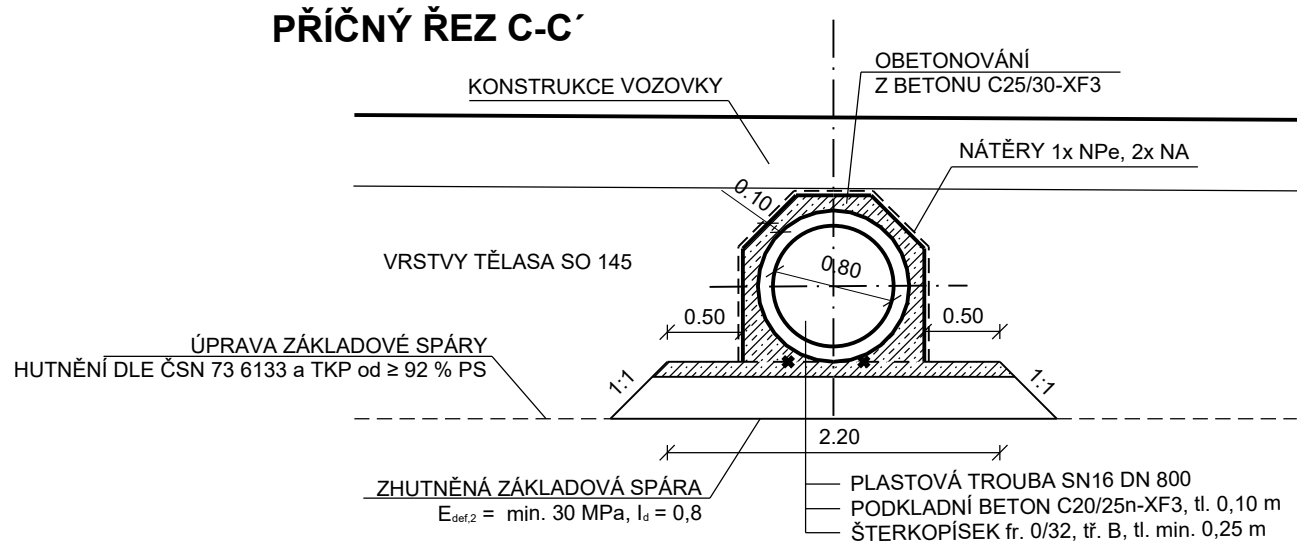

POZNÁMKY:

- SPÁROVÁNÍ DLAŽBY Z LOMOVÉHO KAMENE BUDE VYPLNĚNÉ CEMENTOVOU MALTOU MC25-XF4, tl. min. 0,20 m
- OBETONOVÁNÍ V MÍSTĚ HRDLA MINIMÁLNĚ 0,10 m
- VŠECHNY BETONOVÉ PRVKY, KTERÉ PŘÍJÍDOU DO STYKU SE ZEMINOU MUSÍ BYT OPATŘENY NÁTĚRY: 1x NPe A 2x NA
- VYTÝČENÍ BUDE PROVEDENO DLE TKP 1 A SOUVEŠTĚJÍCÍCH PŘEDPISŮ
- SKLONY SVAHŮ JSOU URČENY SKLONEM SILNIČNÍHO TĚLESA A PŘÍLEHLÝCH PŘÍKOPŮ
- ŠÍŘE PODKLADNÍHO PRAHU JE 0,50 m NA KAŽDOU STRANU OD VNĚJŠÍHO OBRYSU TROUBY
- BETONOVÉ VÝROBKY VYSTAVENÉ PŘÍMĚMU OSTRÍKU ROZMRAZOVACÍCH PROSTŘEDKŮ A MRAZU A UMÍSTĚNÉ VE ZVZDÁLENOSTI MOŽNÉHO OSTRÍKU (OD HRANY VOZOVKY 10 m VČETNĚ SOLNĚ MLHY) MUSÍ SPLŇOVAT POŽADAVKY NA STUPEŇ VLIVU PROSTŘEDÍ XF4.

PARAMETRY PROPUSTKŮ					VYTYČOVANÉ BODY	
STANIČENÍ [km]	TROUBA DN [mm]	DĚLKA DL [m]	SKLON S [‰]	ÚHEL α [°]	VTOK - 01 Y / X [S-JTSK] / Z [Bpv]	VÝTOK - 02 Y / X [S-JTSK] / Z [Bpv]
0,015	800	21,25	1,70	92	698365.208 / 1011542.360 / 217,300	698385.408 / 1011535.805 / 216,943

Souřadnicový systém: S-JTSK
Výškový systém: Bpv

SO 145 Příjezd k DUN v km 2,760

Objednatel:	 ŘEDITELSTVÍ SILNIC A DÁLNIC	Ředitelství silnic a dálnic s. p. Čerčanská 2023/12, Krč, 140 00 Praha 4
-------------	--	--

Zhotovitel:	 Valbek	Valbek, spol. s r.o. Vaňurova 505/17 460 07 Liberec 3
-------------	---	--

	Vypracoval	Bc. J. HALABURKA	Zak. číslo	21-L113-001
	Zodp. projektant	ING. T. KLIMENT	Datum	02/2025
	Tech. kontrola	ING. M. HANŽL	Stupeň	PDPS
	Akce I/16 MLADÁ BOLESLAV - MARTINOVICE		Počet formátů	10 x A4
Měřitko			1 : 50	
Č. přílohy			Paré	
Zhotovitel: Valbek, spol. s r.o. Vaňurova 505/17 460 07 Liberec 3	Příloha	PROPUSTEK v km 0,015		6