


SO 146 - PŘÍJEZD K DUN v km 4,940


PODÉLNÝ PROFIL

M 1 : 1000 / 100

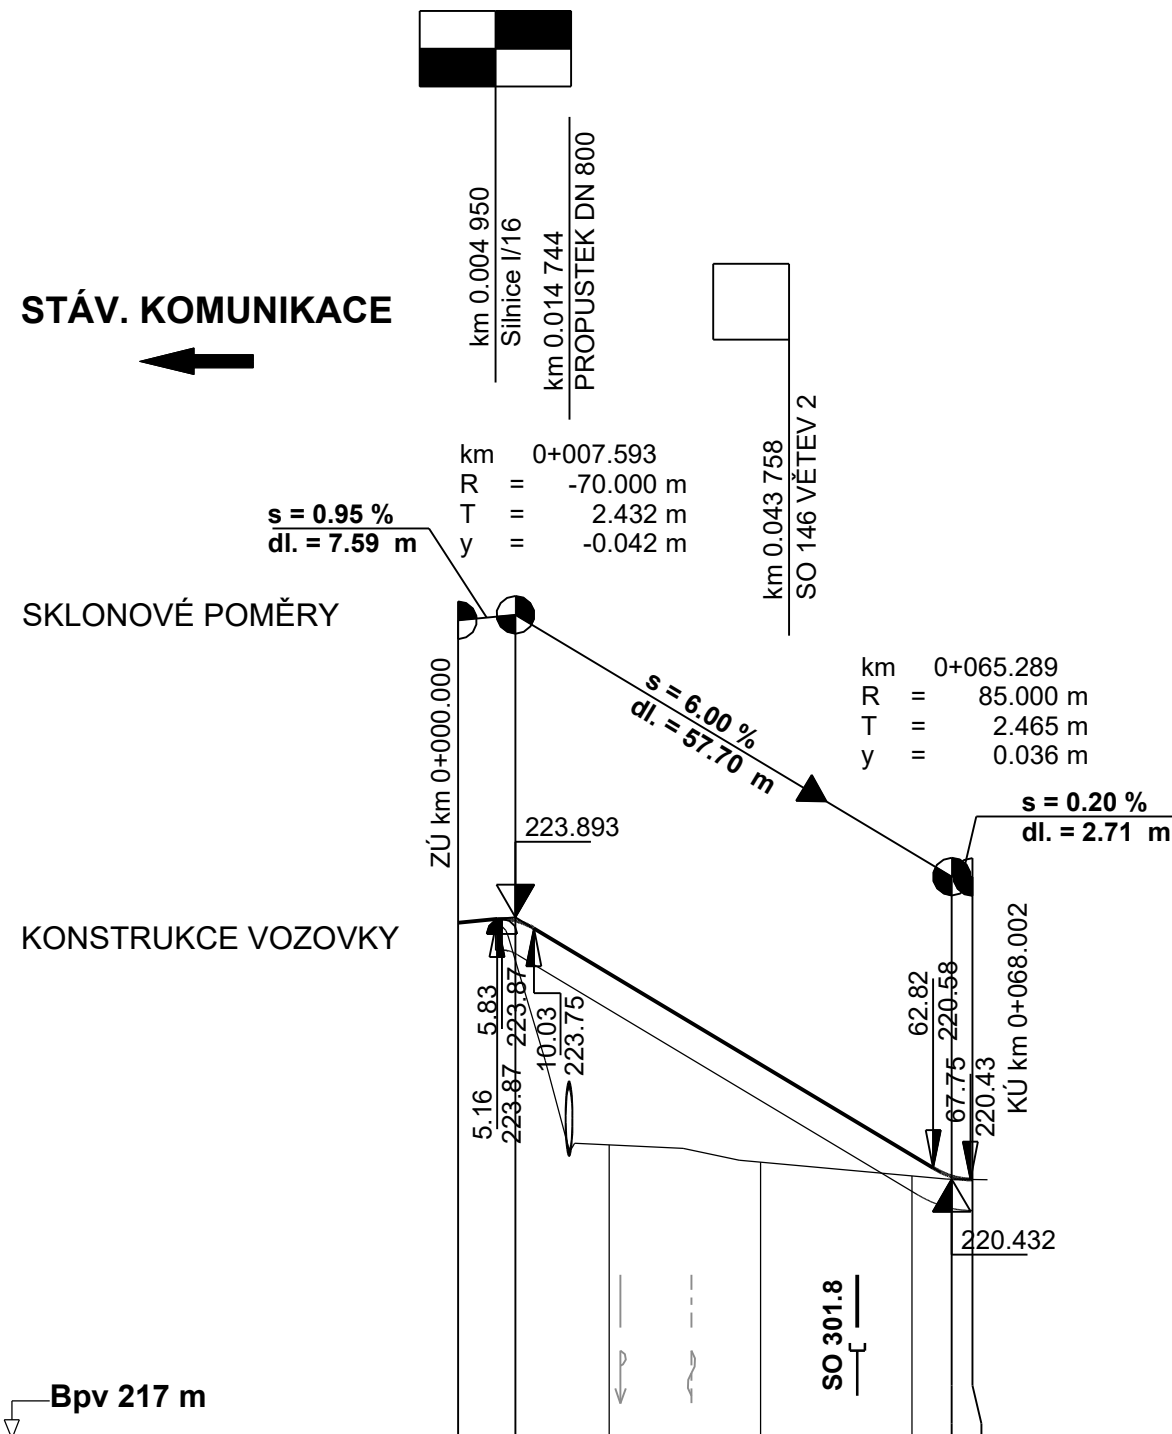

KÓTY NIVELETY	223.82	223.85	223.15	221.95	220.75	220.47	220.43
KÓTY TERÉNU	223.82	223.31	220.88	220.66	220.47	220.43	220.43
STANIČENÍ	0.00	7.59	20.00	40.00	60.00	65.29	68.00

km 0+000

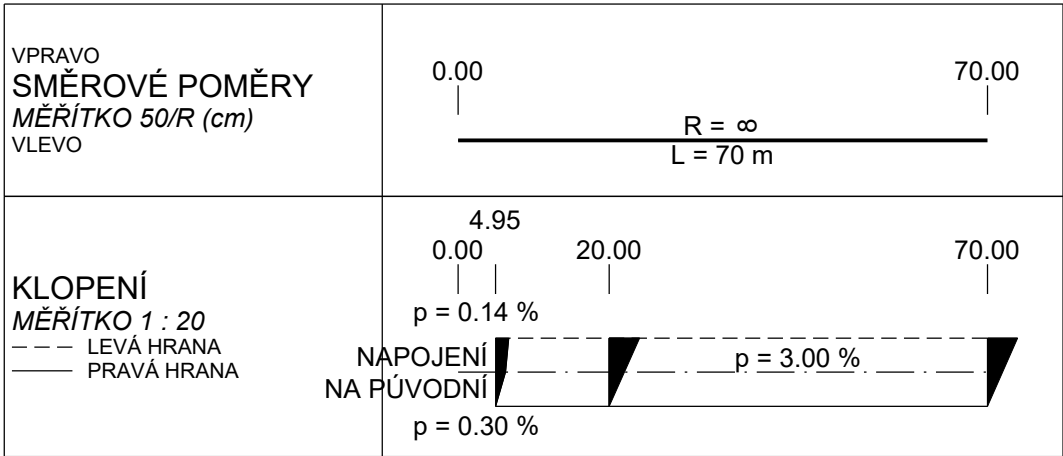

Výškový systém: Bpv

SO 146 Příjezd k DUN v km 4,940

Objednatel:



**ŘEDITELSTVÍ
SILNIC
A DÁLNIC**

Ředitelství silnic a dálnic s. p.
Čerčanská 2023/12, Krč, 140 00 Praha 4

Zhotovitel:



Valbek, spol. s r.o.
Vaňurova 505/17
460 07 Liberec 3

	Vypracoval	Bc. J. HALABURKA		Zak. číslo	21-LI13-001
	Zodp. projektant	ING. T. KLIMENT		Datum	02/2025
	Tech. kontrola	ING. M. HANŽL		Stupeň	PDPS
	Akce I/16 MLADÁ BOLESLAV - MARTINOVICE			Počet formátů	4 x A4
				Měřítko	1 : 1000 / 100
Zhotovitel: Valbek, spol. s r.o. Vaňurova 505/17 460 07 Liberec 3	Příloha PODÉLNÝ PROFIL			Č. přílohy 3	Paré