


SO 146 - PŘÍJEZD K DUN v km 4,940


VZOROVÉ PŘÍČNÉ ŘEZY

M 1 : 50

ŘEZ V MÍSTĚ NÁSYPU

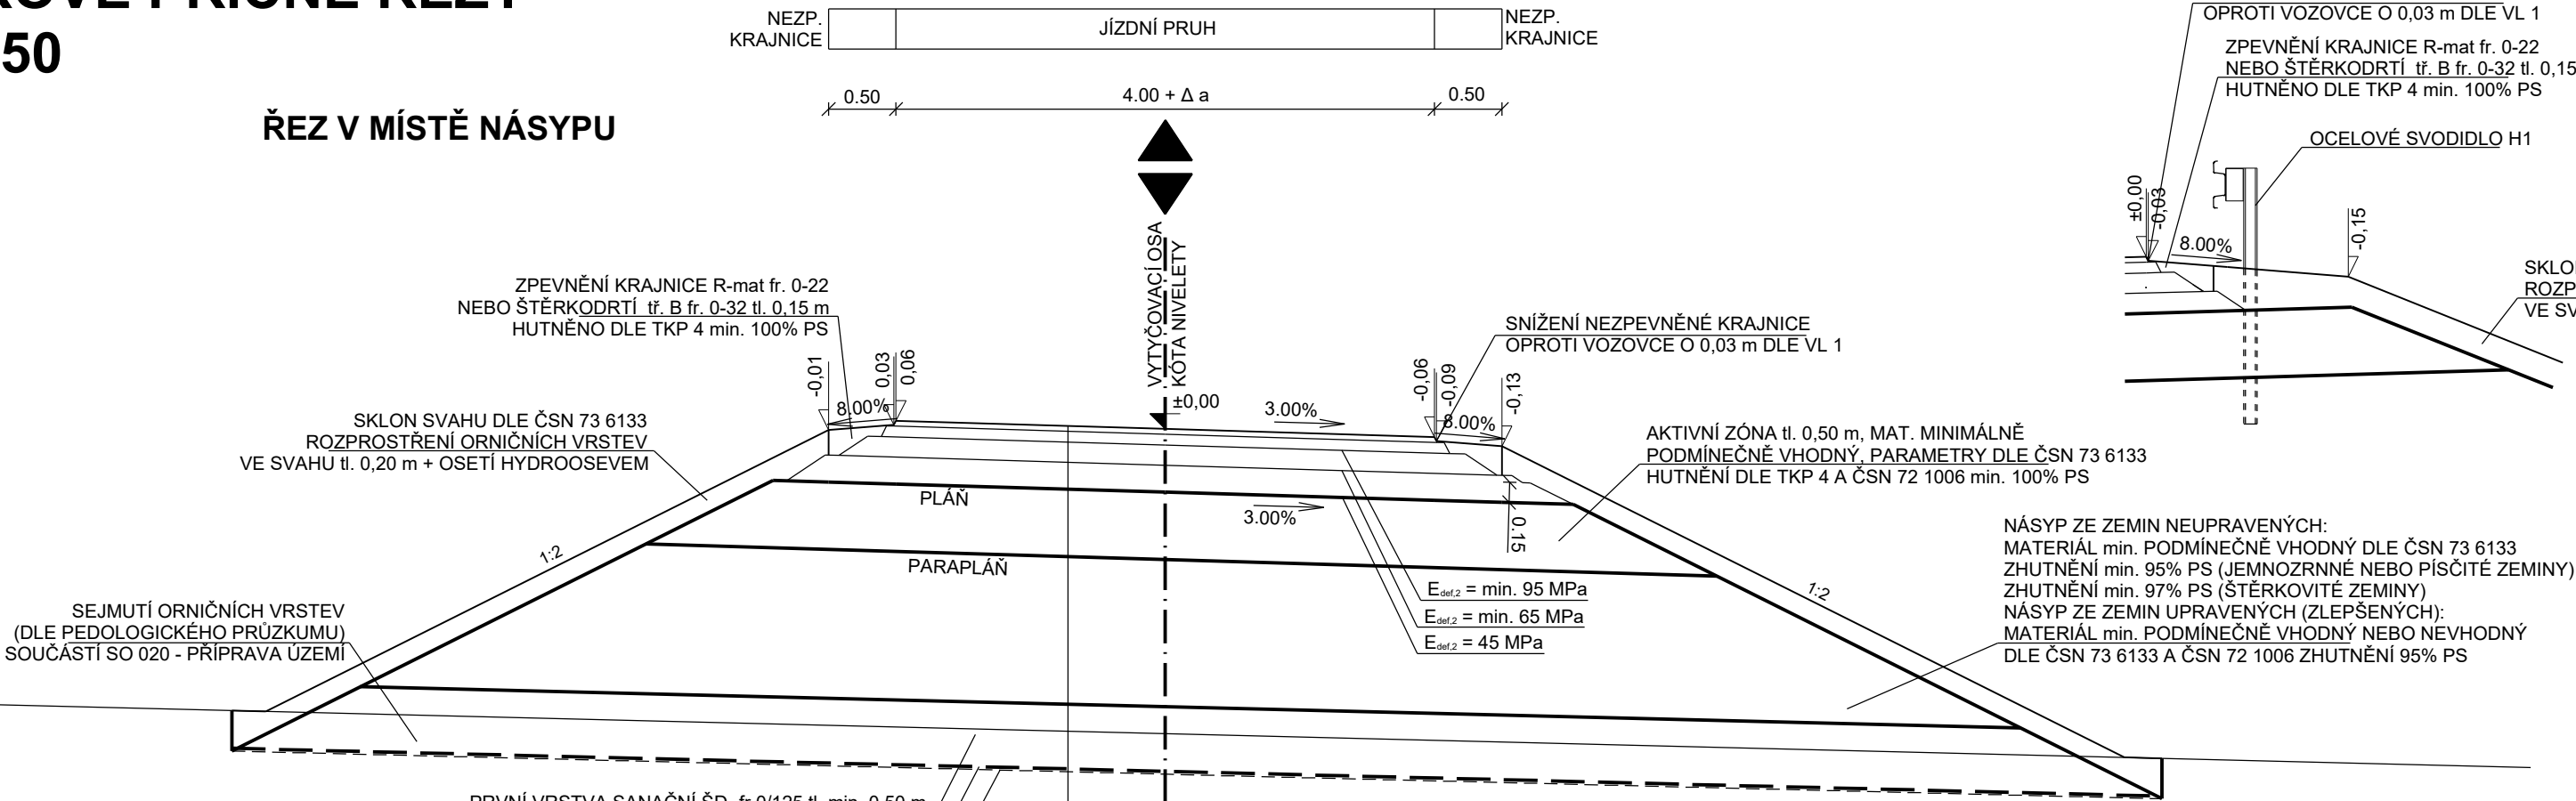

DETAIL V MÍSTĚ KRAJNICE

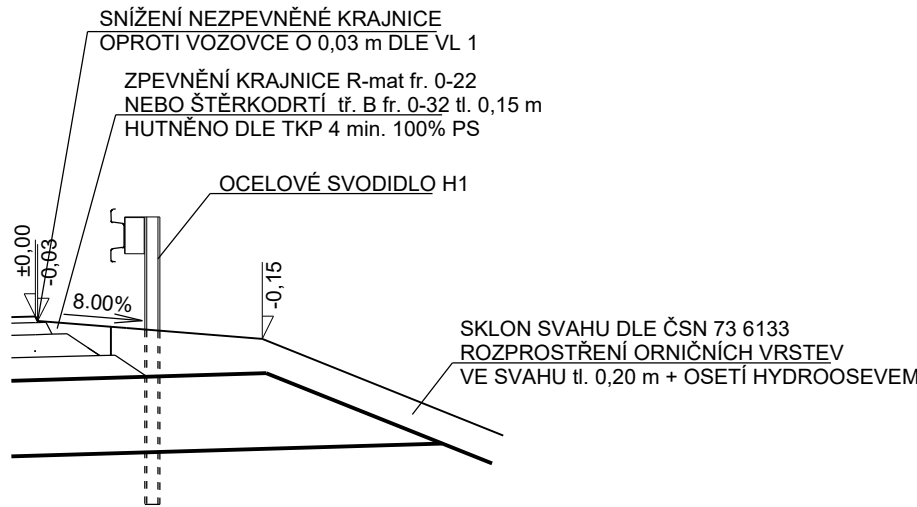

KATEGORIE MO1k -/5/30

JEDNOPRUHOVÁ, OBOUSMĚRNÁ




TŘÍDA DOPRAVNÍHO ZATÍŽENÍ IV

NÁVRHOVÁ ÚROVEŇ PORUŠENÍ D1

TYP PODLOŽÍ PIII (D1-A-2)

D1-N-11, TDZ IV, P III (DLE STARÉHO KATALOGU)


DETAIL UKONČENÍ VRSTEV VOZOVKY

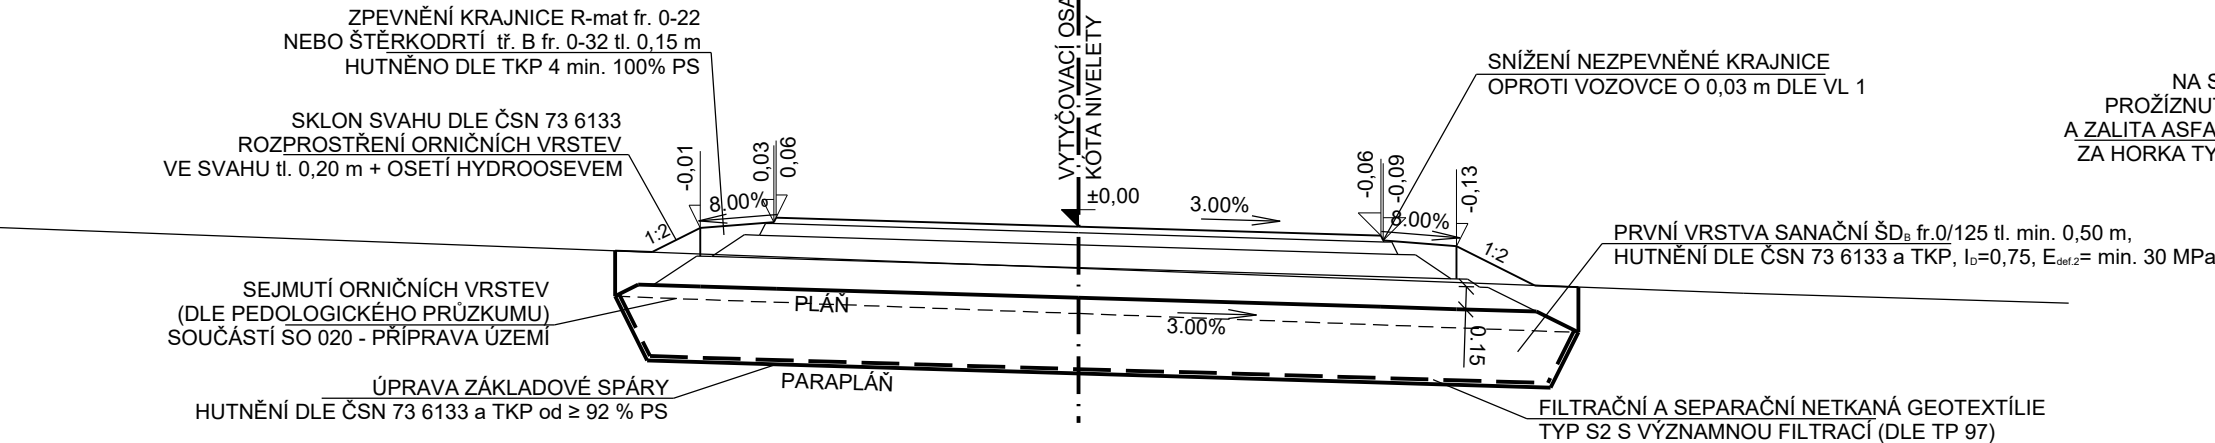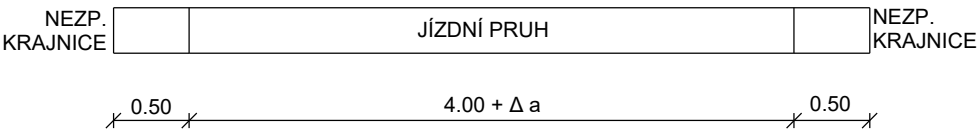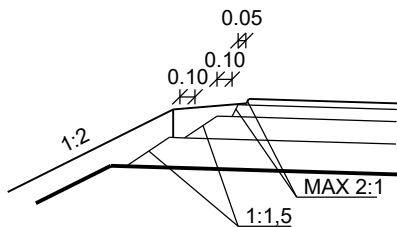

DETAIL NAPOJENÍ KONSTRUKČNÍCH VRSTEV VOZOVKY NA STÁVAJÍCÍ I/16

I/16

SO 146

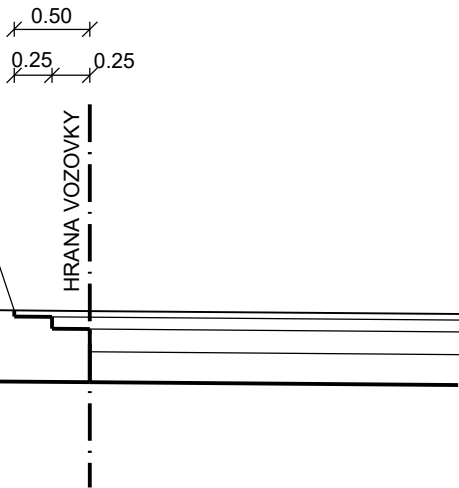

NA STYKU S VOZOVKOU BUDE PROŽÍZNUTA SPÁRA (min 25 x 12 mm) A ZALITA ASFALTOVOU MODIF.ZÁLIVKOU ZA HORKA TYP N2 DLE ČSN EN 14 188-1

SO 146

Příjezd k DUN v km 4,940

Objednatel:



ŘEDITELSTVÍ
SILNIC
A DÁLNIC

Ředitelství silnic a dálnic s. p.

Čerčanská 2023/12, Krč, 140 00 Praha 4

Zhotovitel:



Valbek, spol. s r.o.

Vaňurova 505/17
460 07 Liberec 3



Zhotovitel:

Valbek, spol. s r.o.
Vaňurova 505/17
460 07 Liberec 3

Vypracoval Bc. J. HALABURKA

Zodp. projektant ING. T. KLIMENT

Tech. kontrola ING. M. HANŽL

Akce
I/16 MLADÁ BOLESLAV - MARTINOVICE

Příloha
VZOROVÉ PŘÍČNÉ ŘEZY

Zak. číslo 21-LI13-001

Datum 02/2025

Stupeň PDPS

Počet formátů 3 x A4

Měřítko 1 : 50

Č. přílohy Paré

4