



SO 146 - PŘÍJEZD K DUN v km 4,940

PŘÍČNÉ ŘEZY km 0,020 - 0,060


M 1 : 100

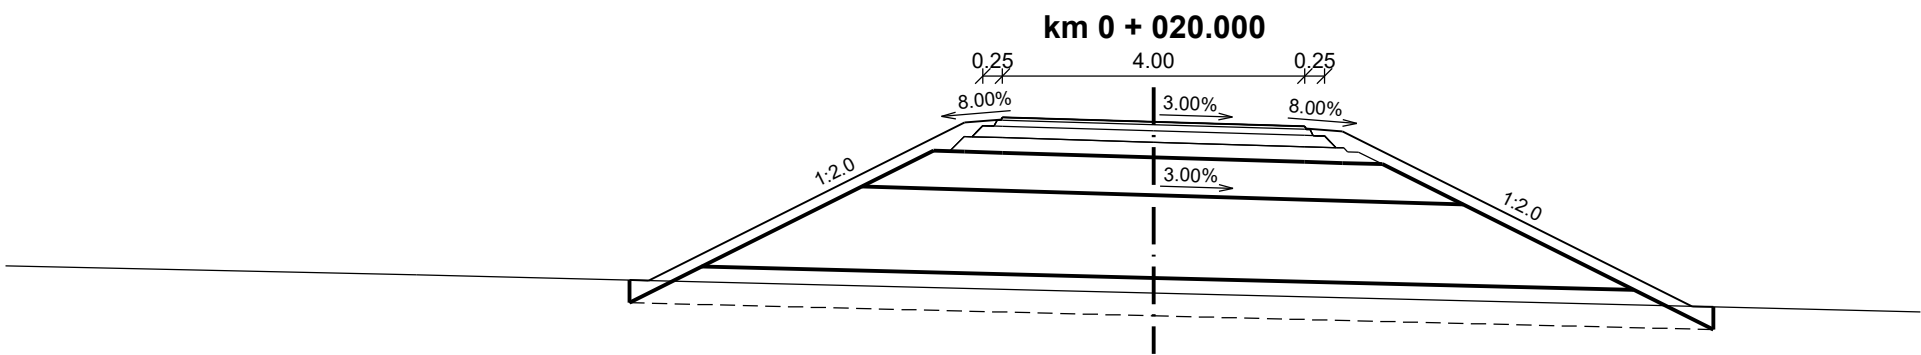

		S. R. 219 m																	
PROJEKTOVANÝ STAV																			
ODSAZENÍ OD OSY																			
STÁVAJÍCÍ TERÉN																			
ODSAZENÍ OD OSY																			

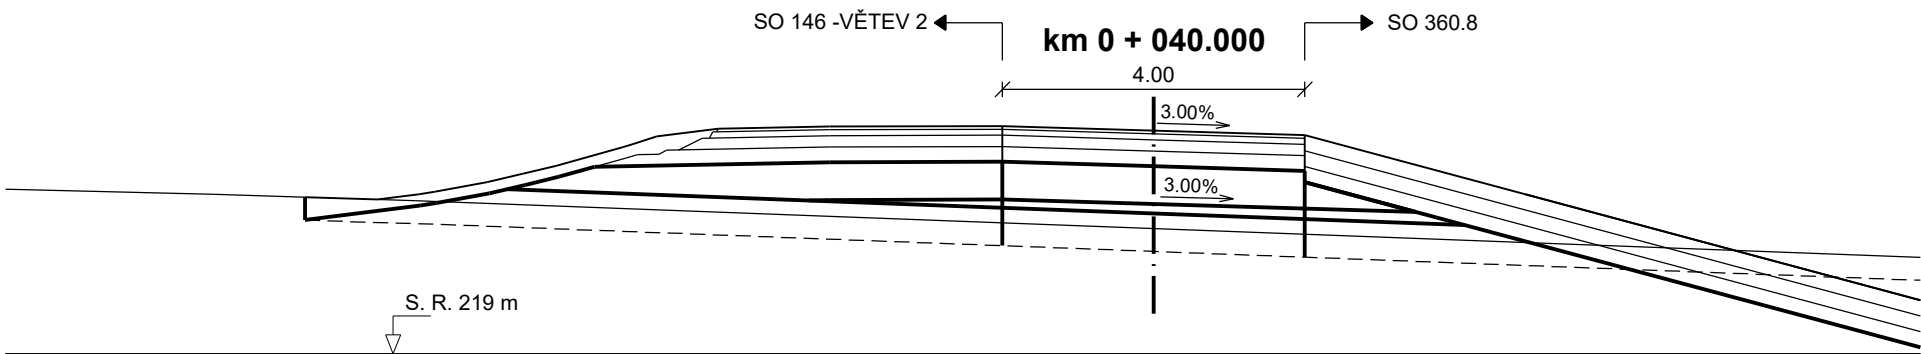

PROJEKTOVANÝ STAV	
-------------------	--	--	

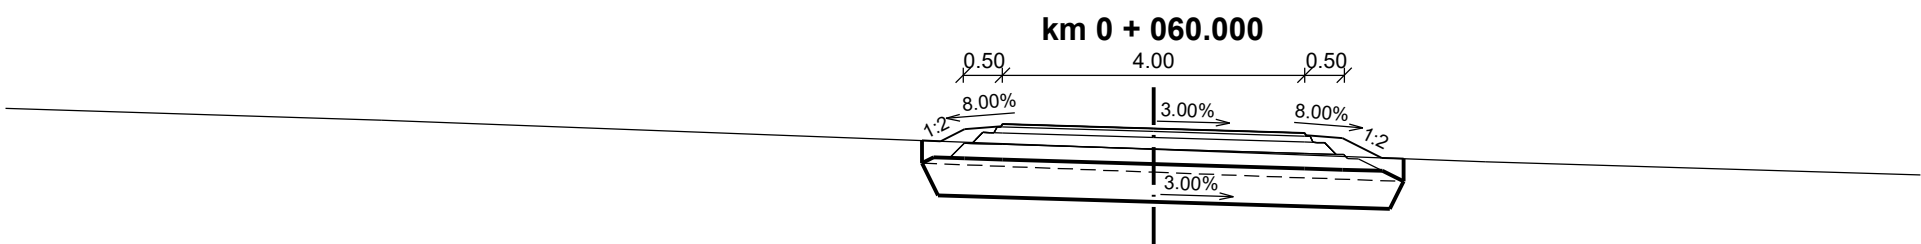

		S. R. 218 m																	
PROJEKTOVANÝ STAV		-3.06	220.59	-2.82	220.58	-2.50	220.74	-2.00	220.81	0.00	220.75	2.00	220.69	2.50	220.62	3.02	220.36	3.31	220.35
ODSAZENÍ OD OSY																			
STÁVAJÍCÍ TERÉN										0.00	220.47								
ODSAZENÍ OD OSY																	4.40	220.31	

Výškový systém: Bpv

SO 146	Příjezd k DUN v km 4,940
--------	--------------------------

Objednatel:				Ředitelství silnic a dálnic s. p.	
				Čerčanská 2023/12, Krč, 140 00 Praha 4	

Zhotovitel:	 Valbek, spol. s r.o. Vaňurova 505/17 460 07 Liberec 3				
-------------	--	--	--	--	--

	Vypracoval	Bc. J. HALABURKA		Zak. číslo	21-LI13-001
	Zodp. projektant	ING. T. KLIMENT		Datum	02/2025
	Tech. kontrola	ING. M. HANŽL		Stupeň	PDPS
	Akce I/16 MLADÁ BOLESLAV - MARTINOVICE			Počet formátů	6 x A4
				Měřítko	1 : 100
Zhotovitel: Valbek, spol. s r.o. Vaňurova 505/17 460 07 Liberec 3	Příloha PŘÍČNÉ ŘEZY km 0,020 - 0,060			5	Paré