



SO 147 - PŘÍJEZD K DUN v km 5,130

VZOROVÉ PŘÍČNÉ ŘEZY

M 1 : 50

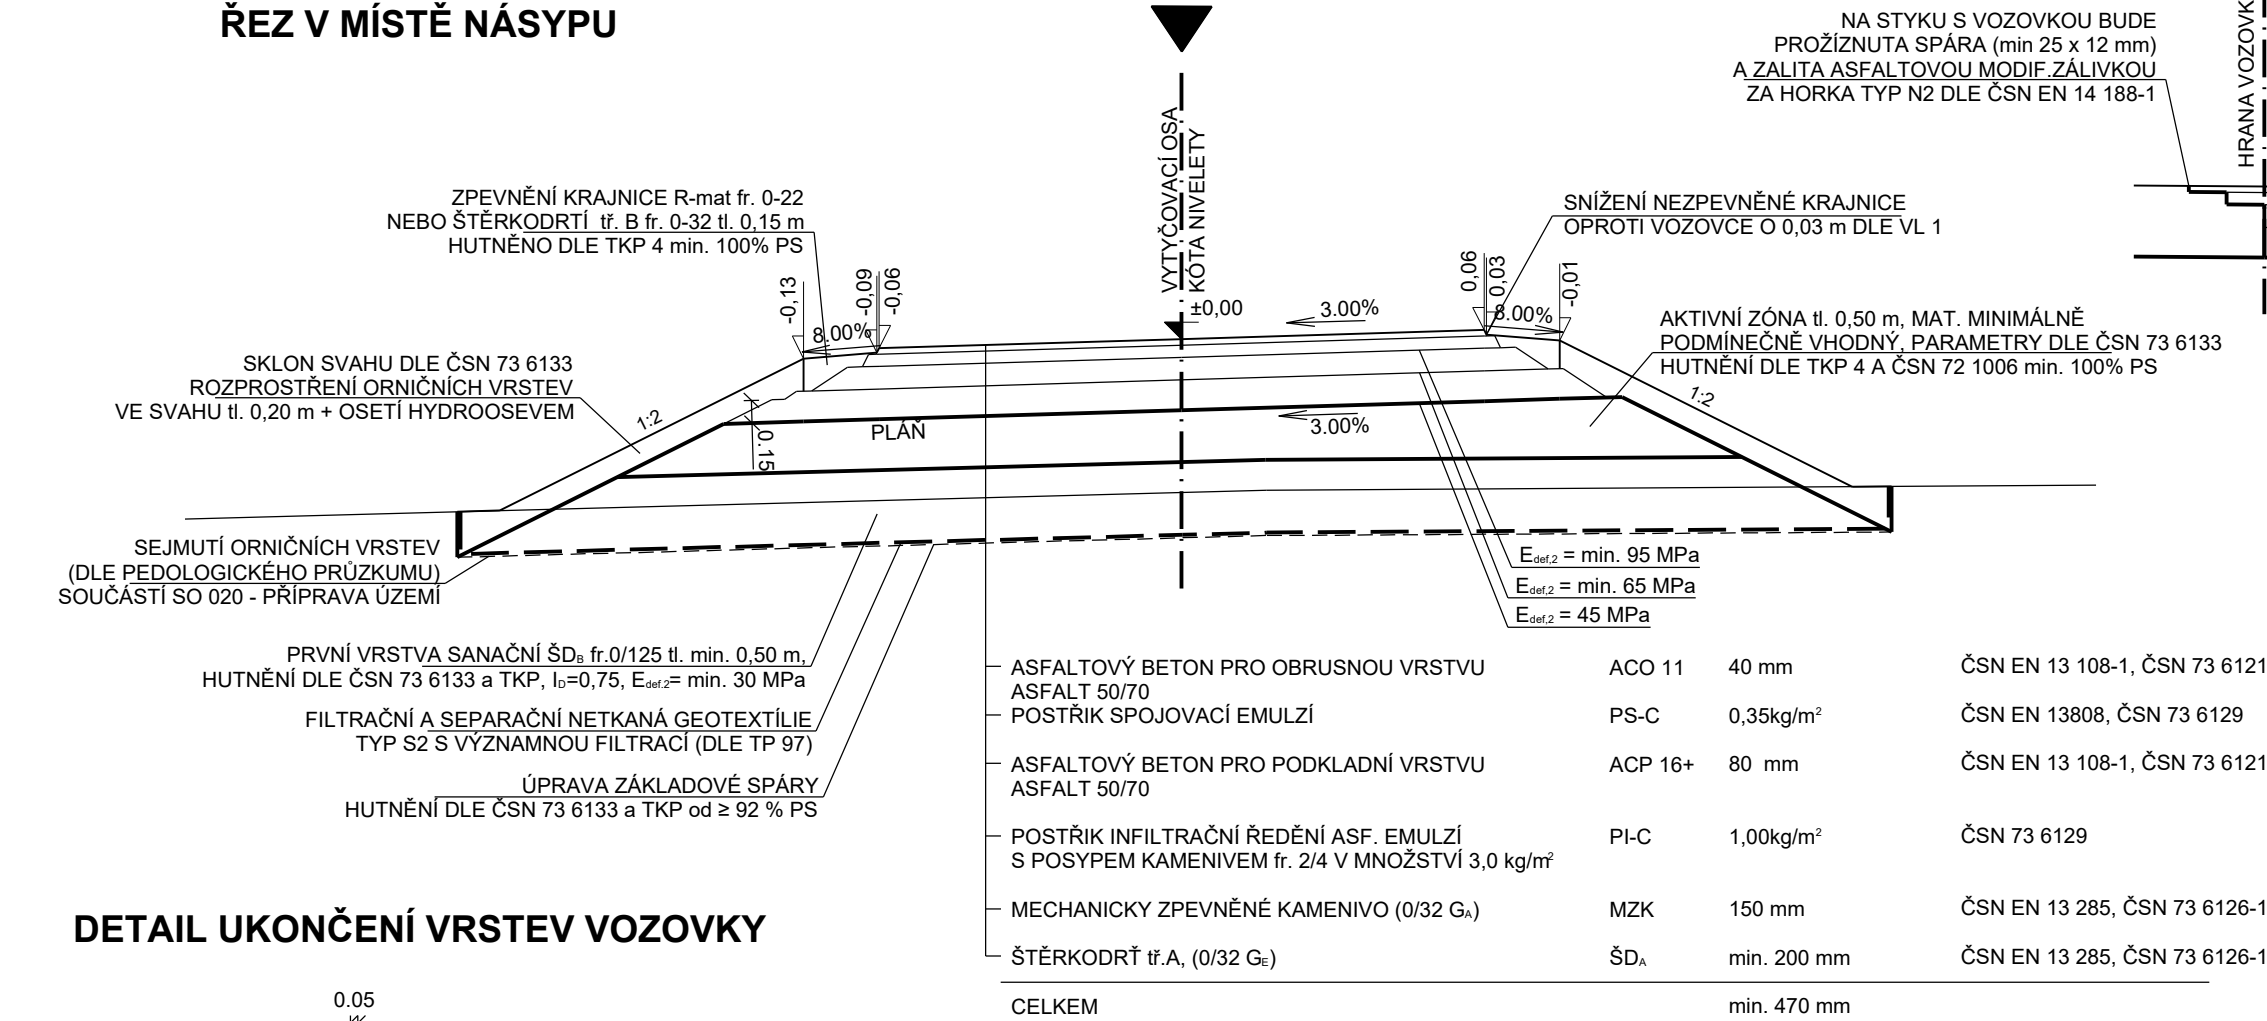

DETAIL UKONČENÍ VRSTEV VOZOVKY

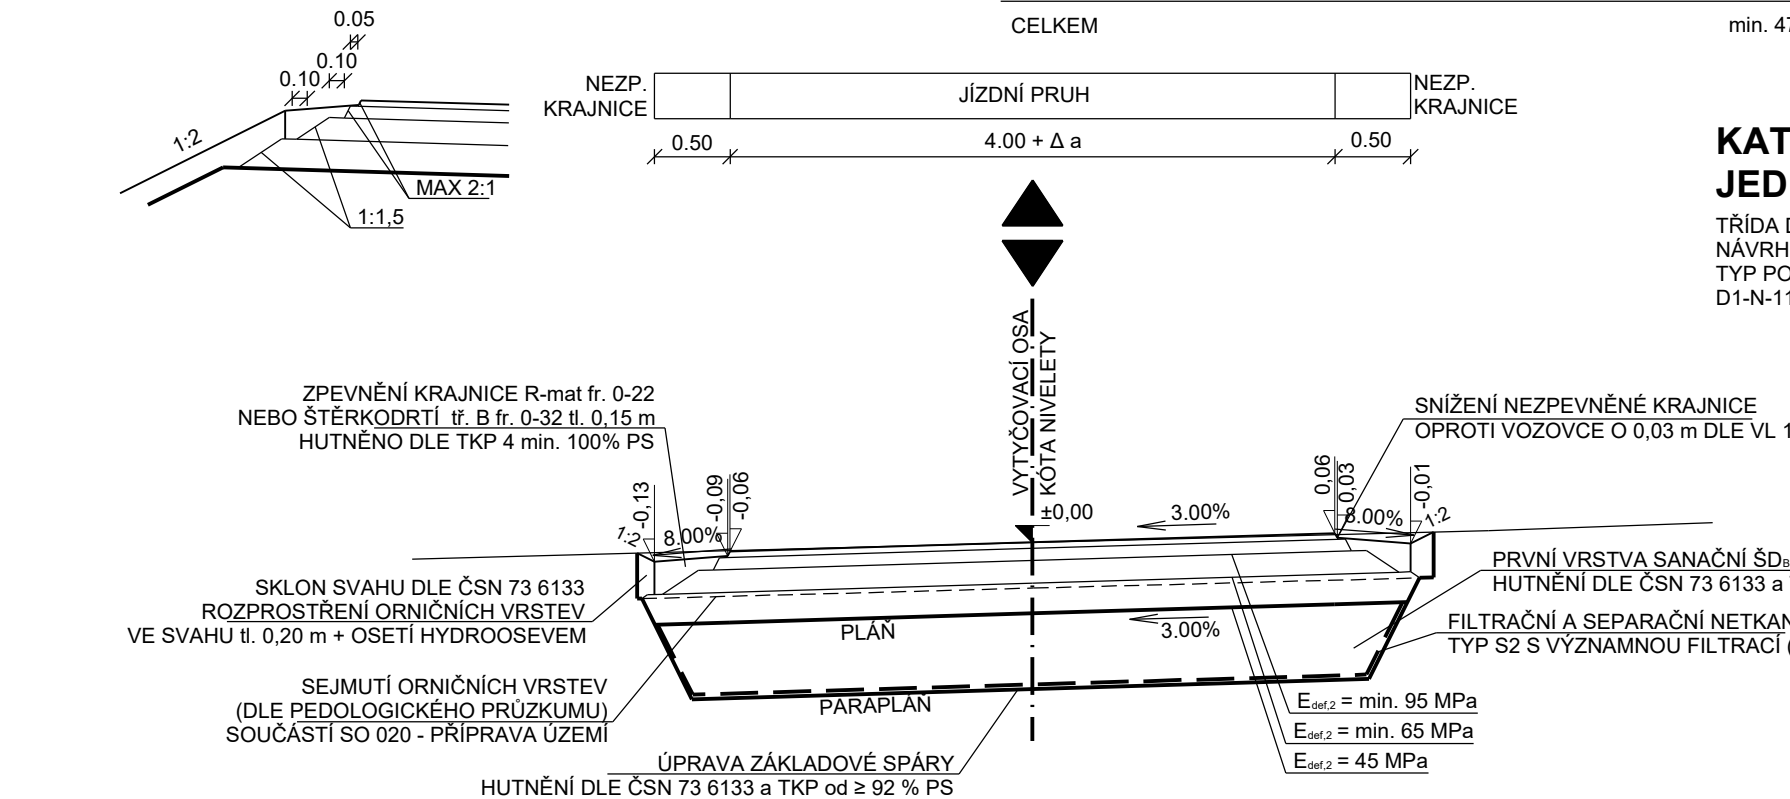

KATEGORIE MO1k -/5/30

JEDNOPRUHOVÁ, OBOUSMĚRNÁ


TŘÍDA DOPRAVNÍHO ZATÍŽENÍ IV

NÁVRHOVÁ ÚROVEŇ PORUŠENÍ D1

TYP PODLOŽÍ PIII (D1-A-2)

D1-N-11, TDZ IV, P III (DLE STARÉHO KATALOGU)

DETAIL NAPOJENÍ KONSTRUKČNÍCH VRSTEV VOZOVKY NA STÁVAJÍCÍ I/16

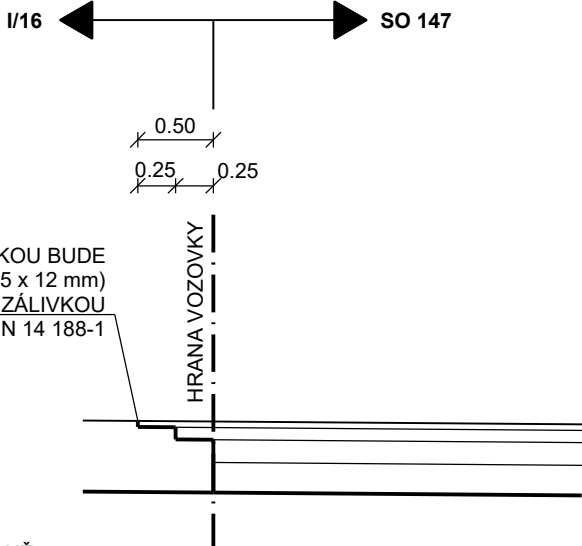

SO 147 Příjezd k DUN v km 5,130

Objednatel:



ŘEDITELSTVÍ
SILNIC
A DÁLNIC

Ředitelství silnic a dálnic s. p.

Čerčanská 2023/12, Krč, 140 00 Praha 4

Zhotovitel:



Valbek, spol. s r.o.

Vaňurova 505/17
460 07 Liberec 3

	Vypracoval	Bc. J. HALABURKA		Zak. číslo	21-LI13-001
	Zodp. projektant	ING. T. KLIMENT		Datum	02/2025
	Tech. kontrola	ING. M. HANŽL		Stupeň	PDPS
	Akce I/16 MLADÁ BOLESLAV - MARTINOVICE			Počet formátů	3 x A4
				Měřítko	1 : 50
Zhotovitel: Valbek, spol. s r.o. Vaňurova 505/17 460 07 Liberec 3	Příloha VZOROVÉ PŘÍČNÉ ŘEZY			Č. přílohy	Paré
				4	