



SO 147 - PŘÍJEZD K DUN v km 5,130

PŘÍČNÉ ŘEZY km 0,020 - 0,060


M 1 : 100

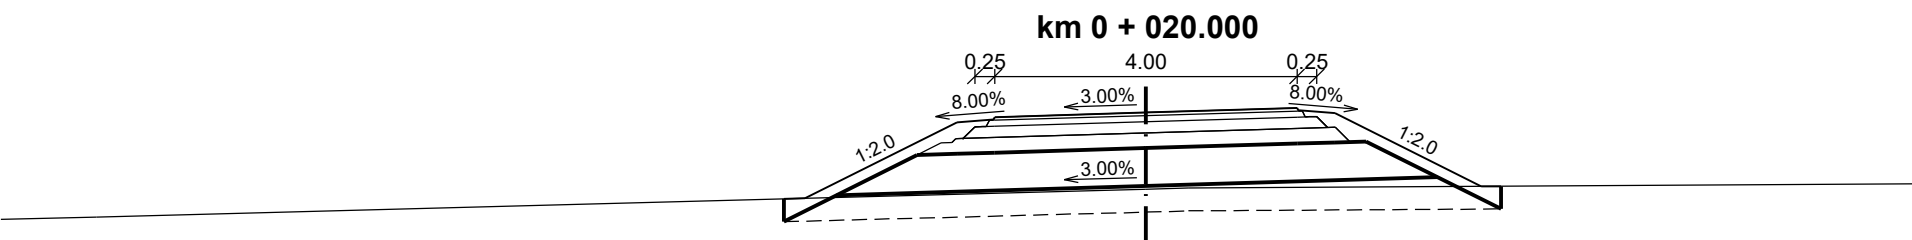

S. R. 220 m							
PROJEKTOVANÝ STAV		4.79	222.47				
ODSAZENÍ OD OSY		-4.51	222.46				
STÁVAJÍCÍ TERÉN							
ODSAZENÍ OD OSY							

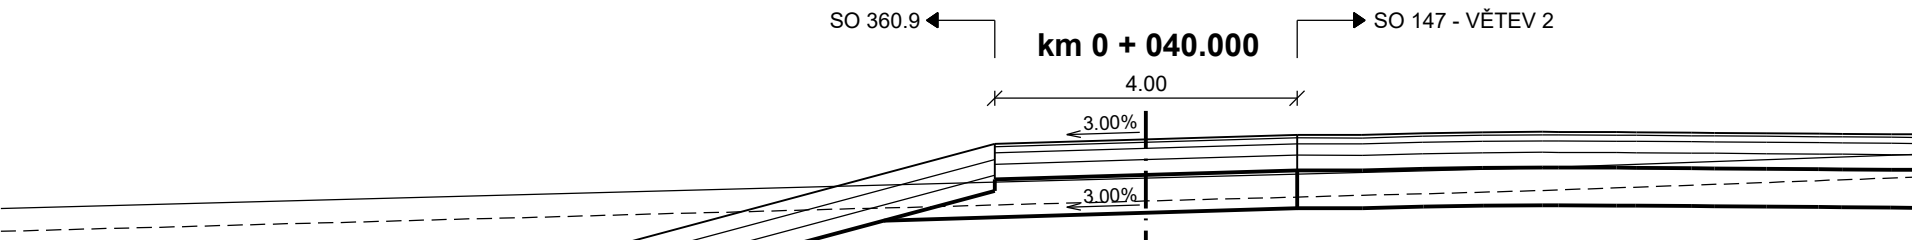

S. R. 219 m							
PROJEKTOVANÝ STAV							
ODSAZENÍ OD OSY							
STÁVAJÍCÍ TERÉN							
ODSAZENÍ OD OSY							

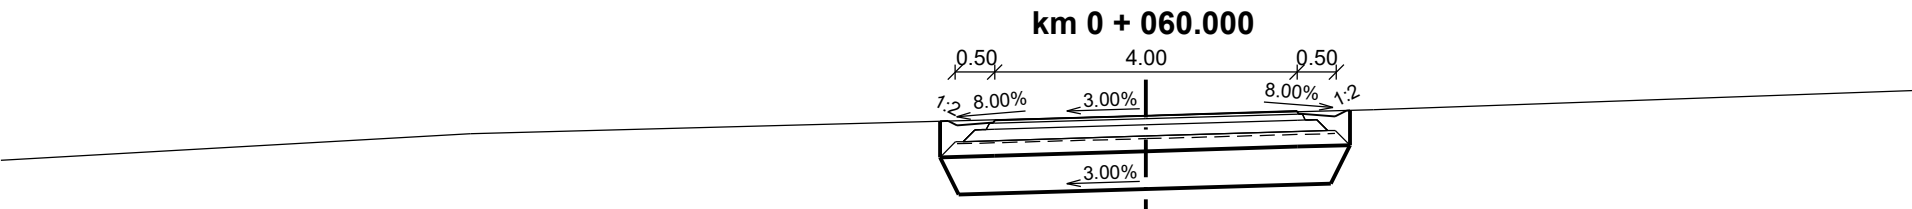

S. R. 219 m							
PROJEKTOVANÝ STAV							
ODSAZENÍ OD OSY							
STÁVAJÍCÍ TERÉN							
ODSAZENÍ OD OSY							

Výškový systém: Bpv

SO 147 Příjezd k DUN v km 5,130

Objednatel:



Ředitelství silnic a dálnic s. p.
Čerčanská 2023/12, Krč, 140 00 Praha 4

Zhotovitel:



Valbek, spol. s r.o.
Vaňurova 505/17
460 07 Liberec 3

	Vypracoval	Bc. J. HALABURKA		Zak. číslo	21-LI13-001
	Zodp. projektant	ING. T. KLIMENT		Datum	02/2025
	Tech. kontrola	ING. M. HANŽL		Stupeň	PDPS
	Akce			Počet formátů	6 x A4
Zhotovitel: Valbek, spol. s r.o. Vaňurova 505/17 460 07 Liberec 3	I/16 MLADÁ BOLESLAV - MARTINOVICE			Měřítko	1 : 100
				Č. přílohy	Paré
				5	
Příloha	PŘÍČNÉ ŘEZY km 0,020 - 0,060				