
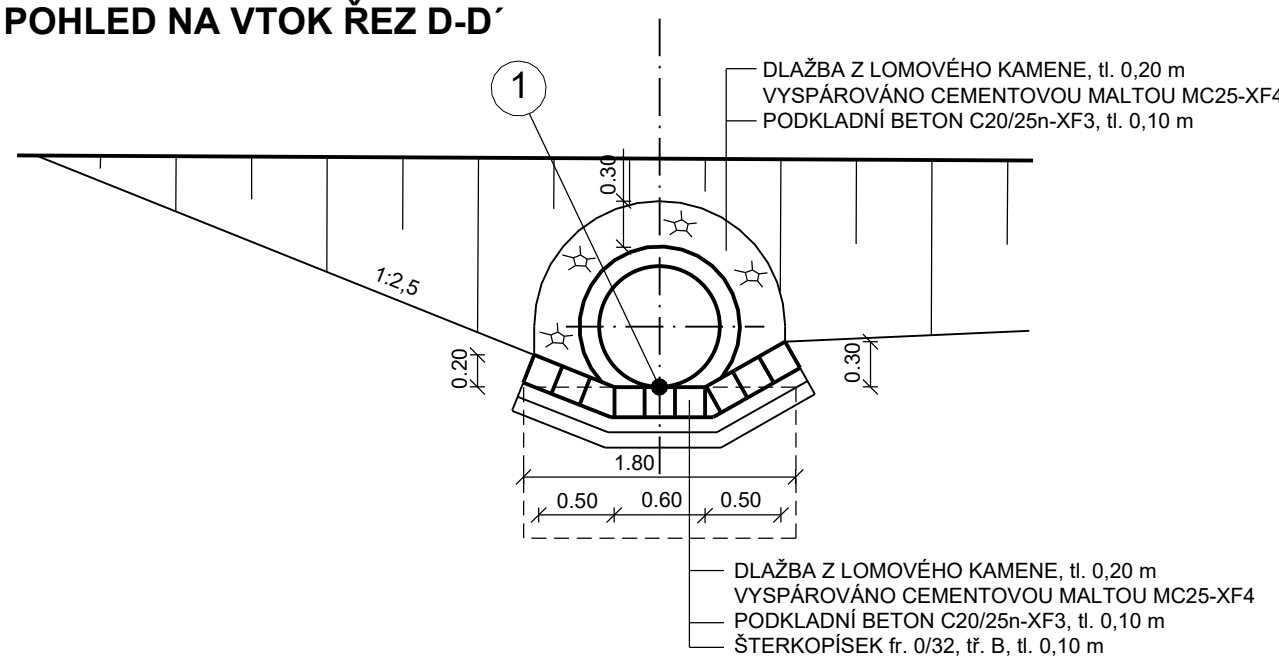




M 1 : 50

PARAMETRY PROPUSTKŮ					VYTÝČOVANÉ BODY	
STANIČENÍ [km]	TROUBA DN [mm]	DLKA [m]	SKLON S. [%]	ÚHEL α [°]	VTKO - 01 Y / X [S-JTSK] / Z [Bpv]	VÝTKO - 02 Y / X [S-JTSK] / Z [Bpv]
0,012	800	18,60	0,90	94	696069.703 / 1011839.547 / 222.458	696087.513 / 1011844.829 / 222.287

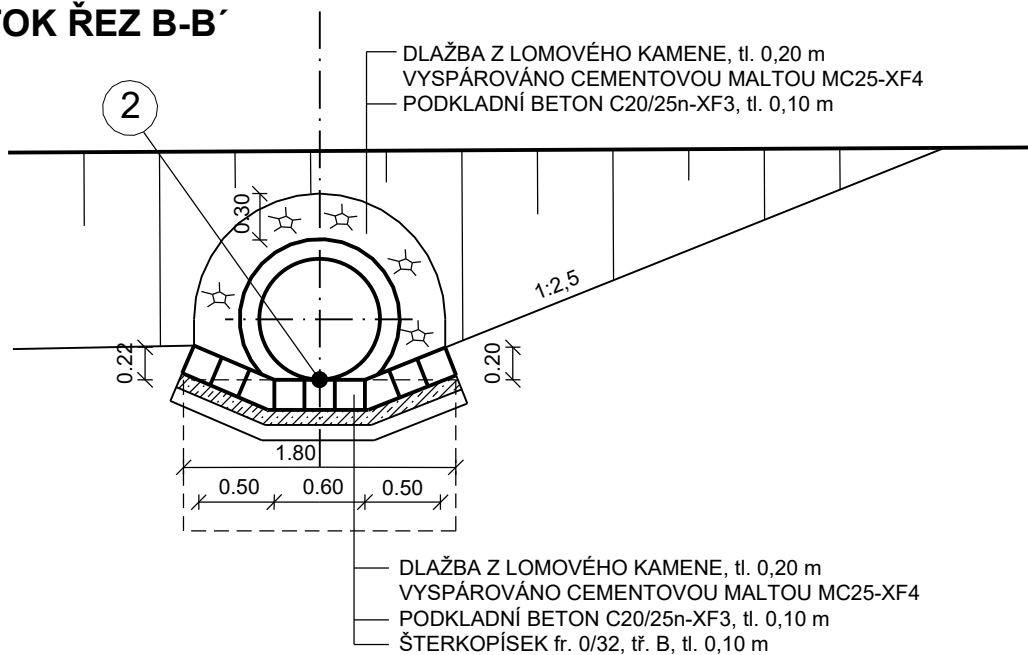

POZNÁMKY:

- SPÁROVÁNÍ DLÁŽBY Z LOMOVÉHO KAMENE BUDE VYPLNĚNÉ CEMENTOVOU MALTOU MC25-VK4, tl. min. 0,20 m
- OBETONOVÁNÍ V MÍSTĚ HRDLA MINIMÁLNĚ 0,10 m
- VŠECHNY BETONOVÉ PRVKY, KTERÉ PRŮJEDOU DO STYKY SE ZEMLINOU MUSÍ BÝT OPATŘENY NÁTĚR: 1x NPc A 2x NA
- VYTÝČENÍ BUDE PROVEDENO DLE TP K A I SOUVISEJÍCÍCH PŘEDPISŮ
- SKLONY SVAHŮ JSOU URČENY SKLONEM SILNIČNÍHO TĚLESA A PŘÍLEHLÝCH PŘÍKOPŮ
- ŠÍŘE PODKLADIŇOVÝCH PRAHU JE 0,50 m NA KAŽDÝ STRANU OD VNĚJŠÍHO OBRYSU TRUBOU
- BETONOVÉ VÝROBKÝ VYSTAVĚNÉ PŘÍMÝMU OSLTUKU ROZMRAZOVACÍCH PROSTŘEDKŮ A MRÁZU A UMÍSTĚNÉ JE ZVÝDAVNĚNÍ MOŽNOSTI OSLTUKU (OD HRANY VOZOVKY 10 m VČETNĚ JEHO NÁVYŠTÍ) SMĚNĚNAT POŽADAVKY NA STUPEŇ VLIVU PROSTŘEDÍ XF4

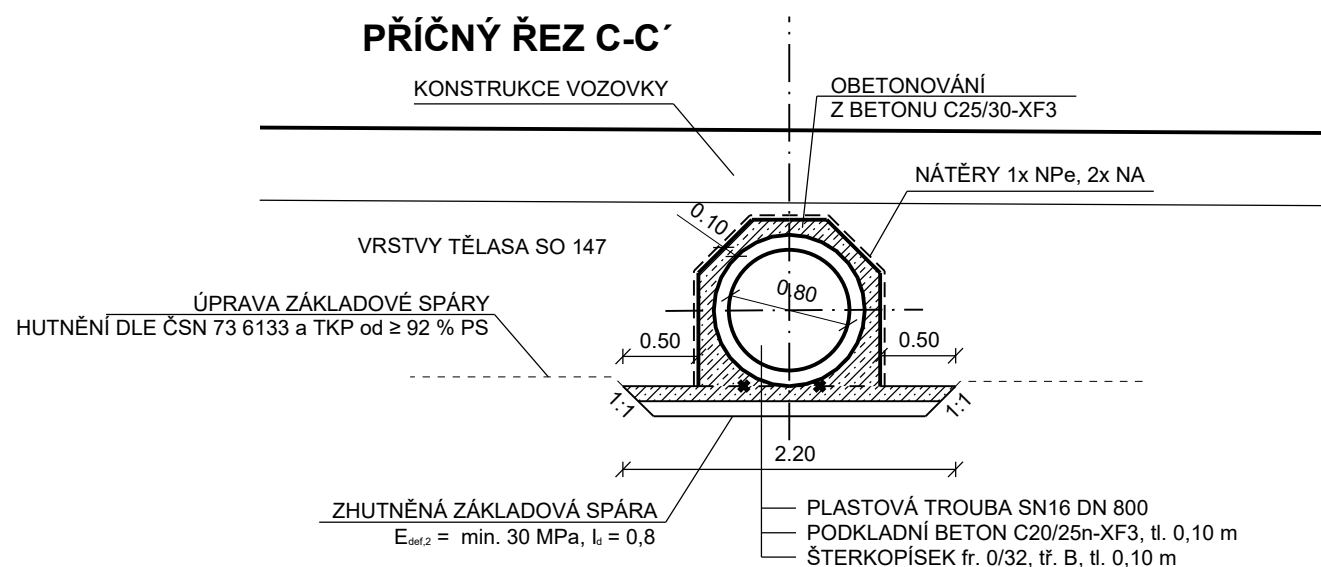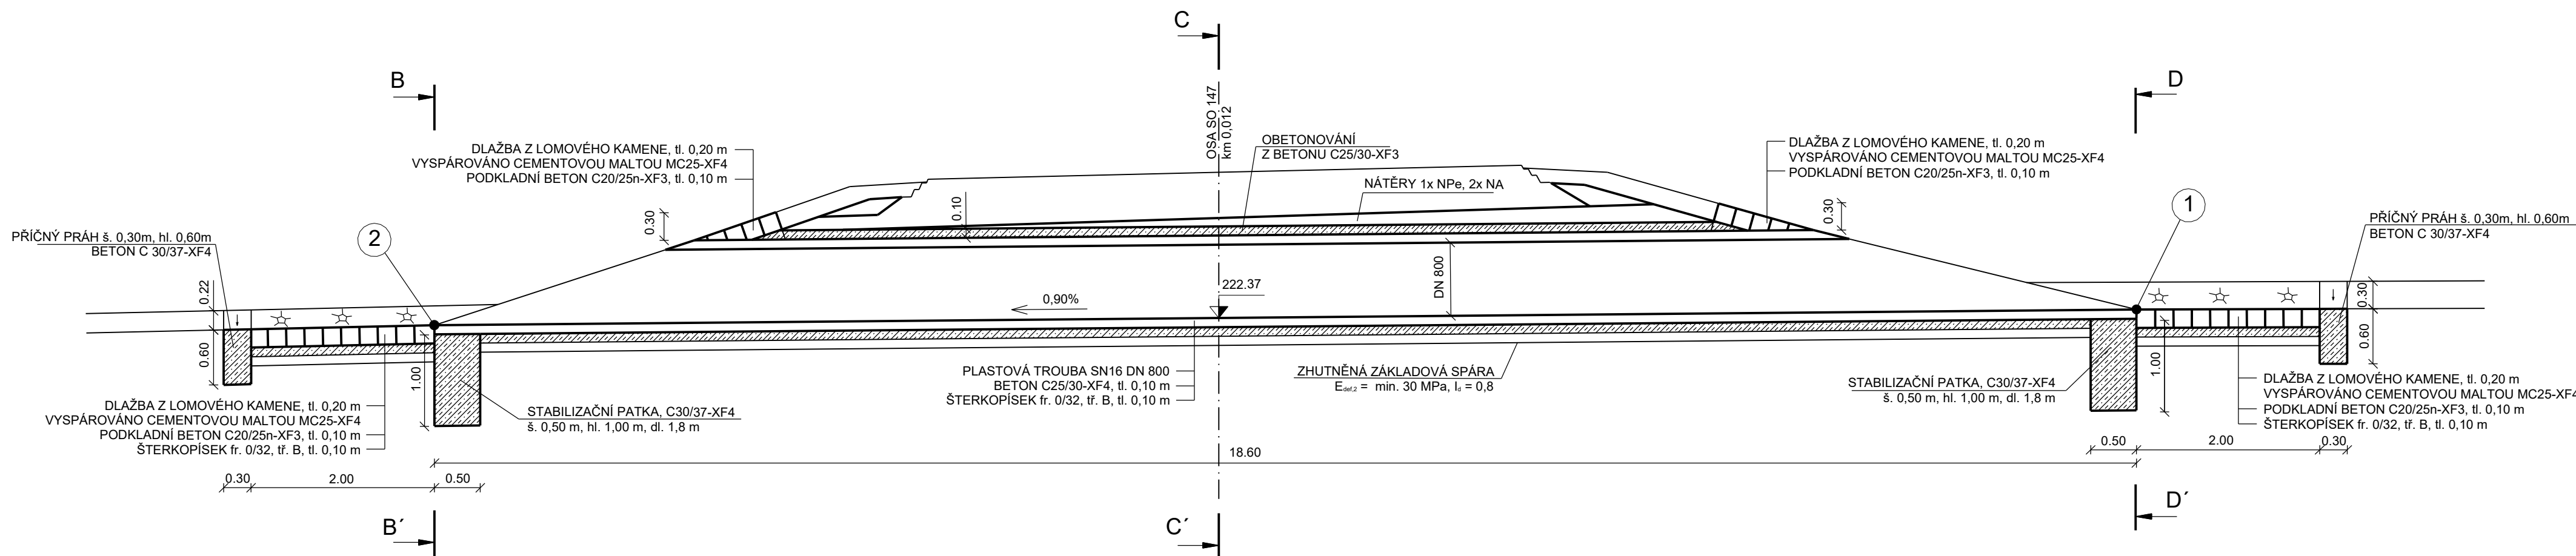

Souřadnicový systém: S-JTSK
Výškový systém: Bpv

SO 147 Příjezd k DUN v km 5,130

Objednatel:

Ředitelství silnic a dálnic s. p.
Čerčanská 2023/12, Krč, 140 00 Praha 4

Zhotovitel:



Valbek, spol. s r.o.
Vaňurova 505/17
460 07 Liberec 3

	Vypracoval Bc. J. HALABURKA	Zak. číslo 21-LH13-001
	Zodp. projektant ING. T. KLIMENT	Datum 02/2025
	Tech. kontrola ING. M. HANŽL	Stupeň PDPS
	Akce I/16 MLADÁ BOLESLAV - MARTINOVICE	Počet formátů 10 x A4
		Měřítka 1 : 50
		Č. přílohy Paré
Zhotovitel: Valbek, spol. s r. o. Vaňurova 505/17 460 07 Liberec 3	Příloha PROPUSTEK v km 0,012	6