



SO 148 - PŘÍJEZD K DUN v km 7,450

PODÉLNÝ PROFIL

M 1 : 1000 / 100

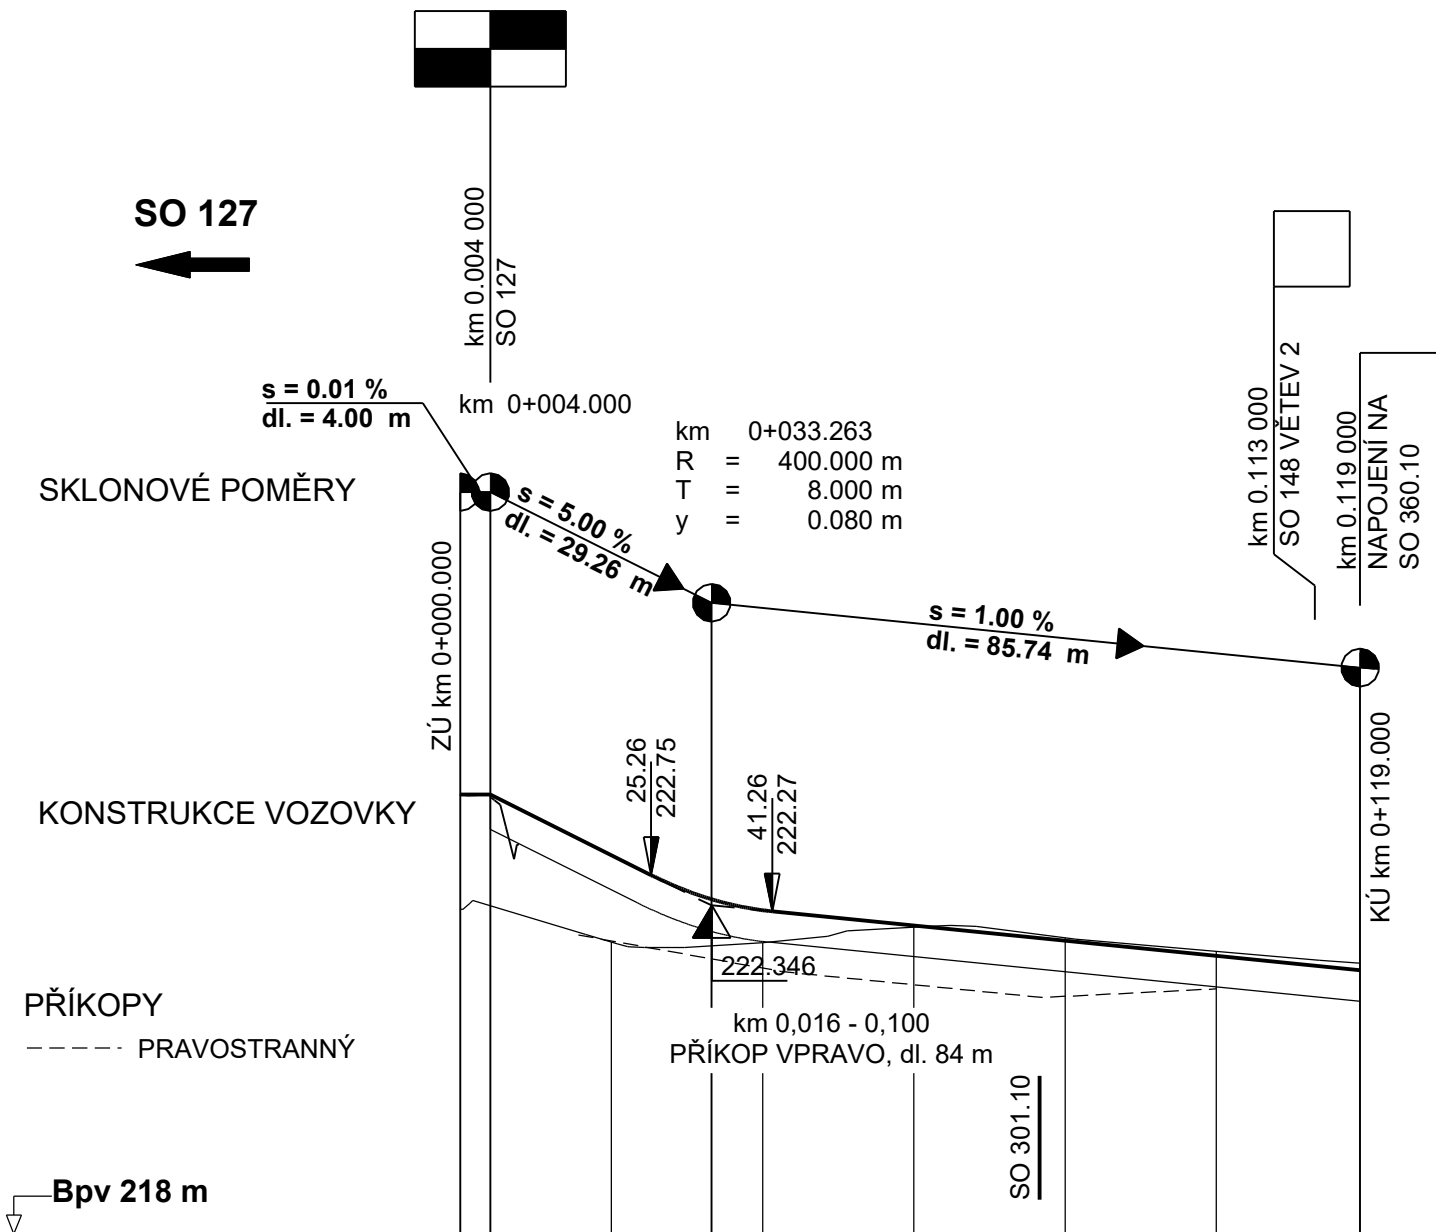

KÓTY NIVELETY	223.81	223.81	223.01	222.43	222.28	222.08	221.88	221.68	221.49
KÓTY TERÉNU	222.29	222.40	221.86	221.80	221.85	222.06	221.91	221.74	221.58
STANIČENÍ	0.00	4.00	20.00	33.26	40.00	60.00	80.00	100.00	119.00

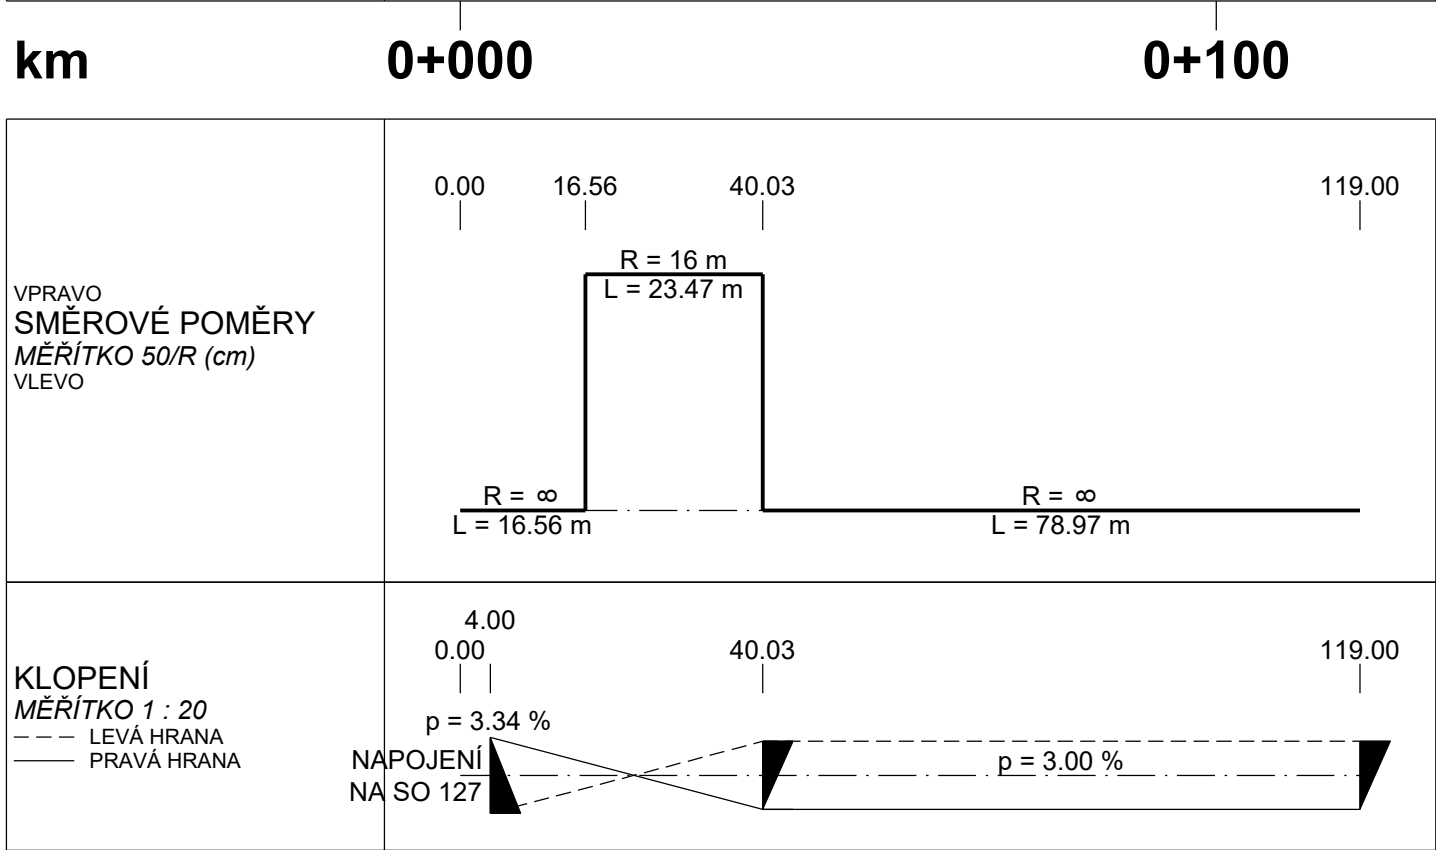

Výškový systém: Bpv

SO 148 Příjezd k DUN v km 7,450

Objednatel:



**ŘEDITELSTVÍ
SILNIC
A DÁLNIC**

Ředitelství silnic a dálnic s. p.
Čerčanská 2023/12, Krč, 140 00 Praha 4

Zhotovitel:



Valbek

Valbek, spol. s r.o.
Vaňurova 505/17
460 07 Liberec 3

	Vypracoval	Bc. J. HALABURKA		Zak. číslo	21-LI13-001
	Zodp. projektant	ING. T. KLIMENT		Datum	02/2025
	Tech. kontrola	ING. M. HANŽL		Stupeň	PDPS
	Akce I/16 MLADÁ BOLESLAV - MARTINOVICE			Počet formátů	4 x A4
				Měřítko	1 : 1000 / 100
Zhotovitel: Valbek, spol. s r.o. Vaňurova 505/17 460 07 Liberec 3	Příloha PODÉLNÝ PROFIL			Č. přílohy	Paré
				3	