
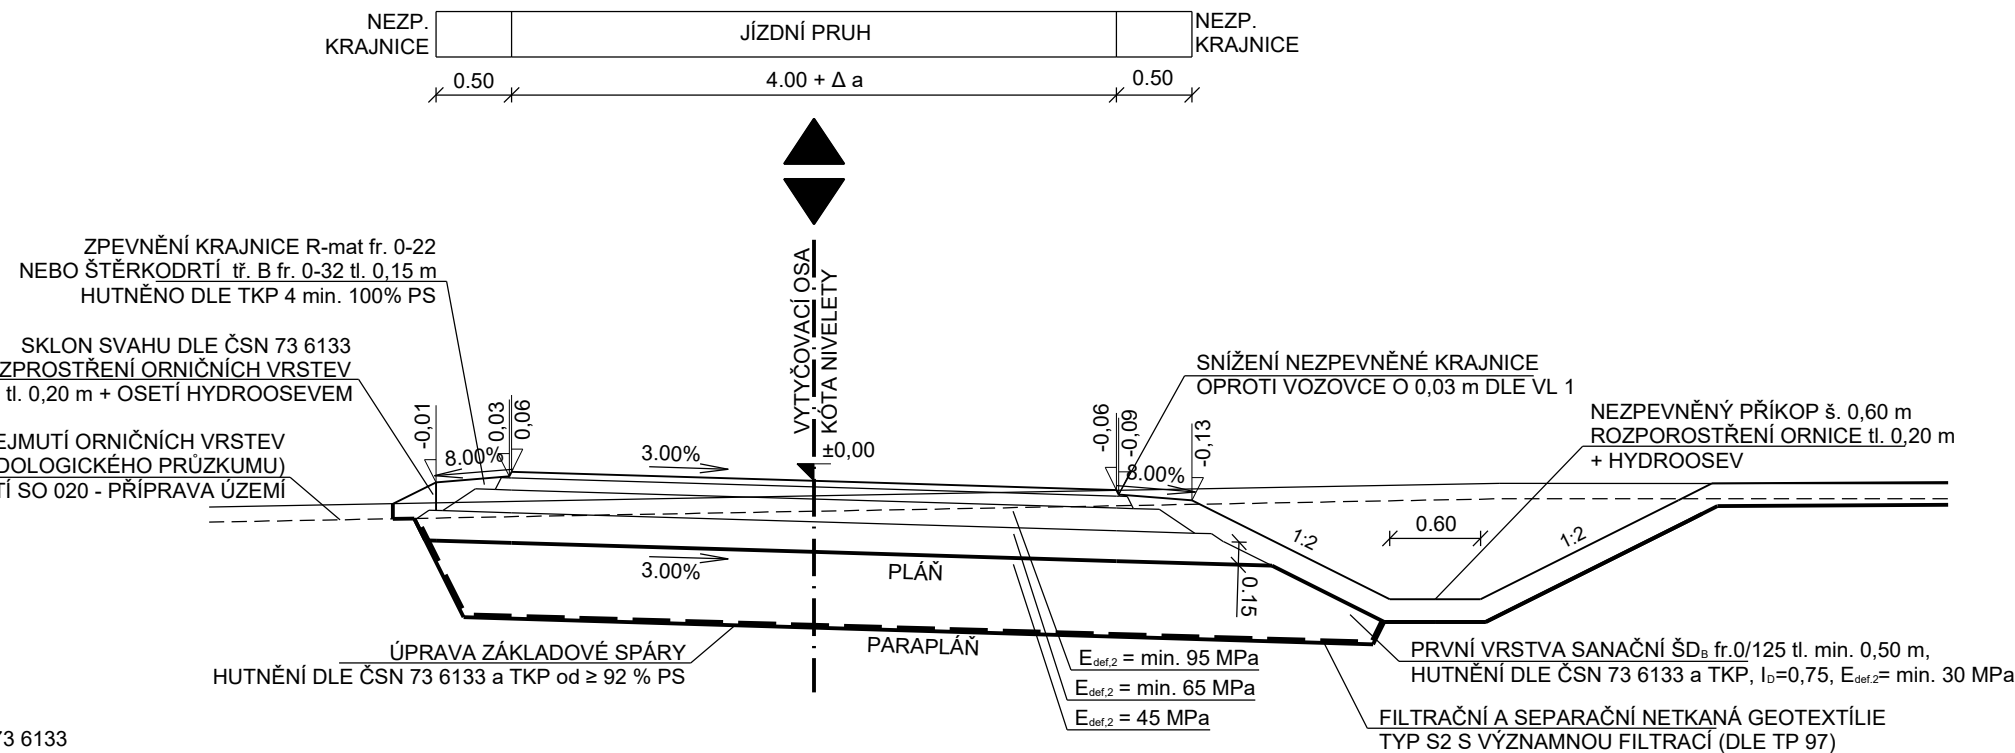
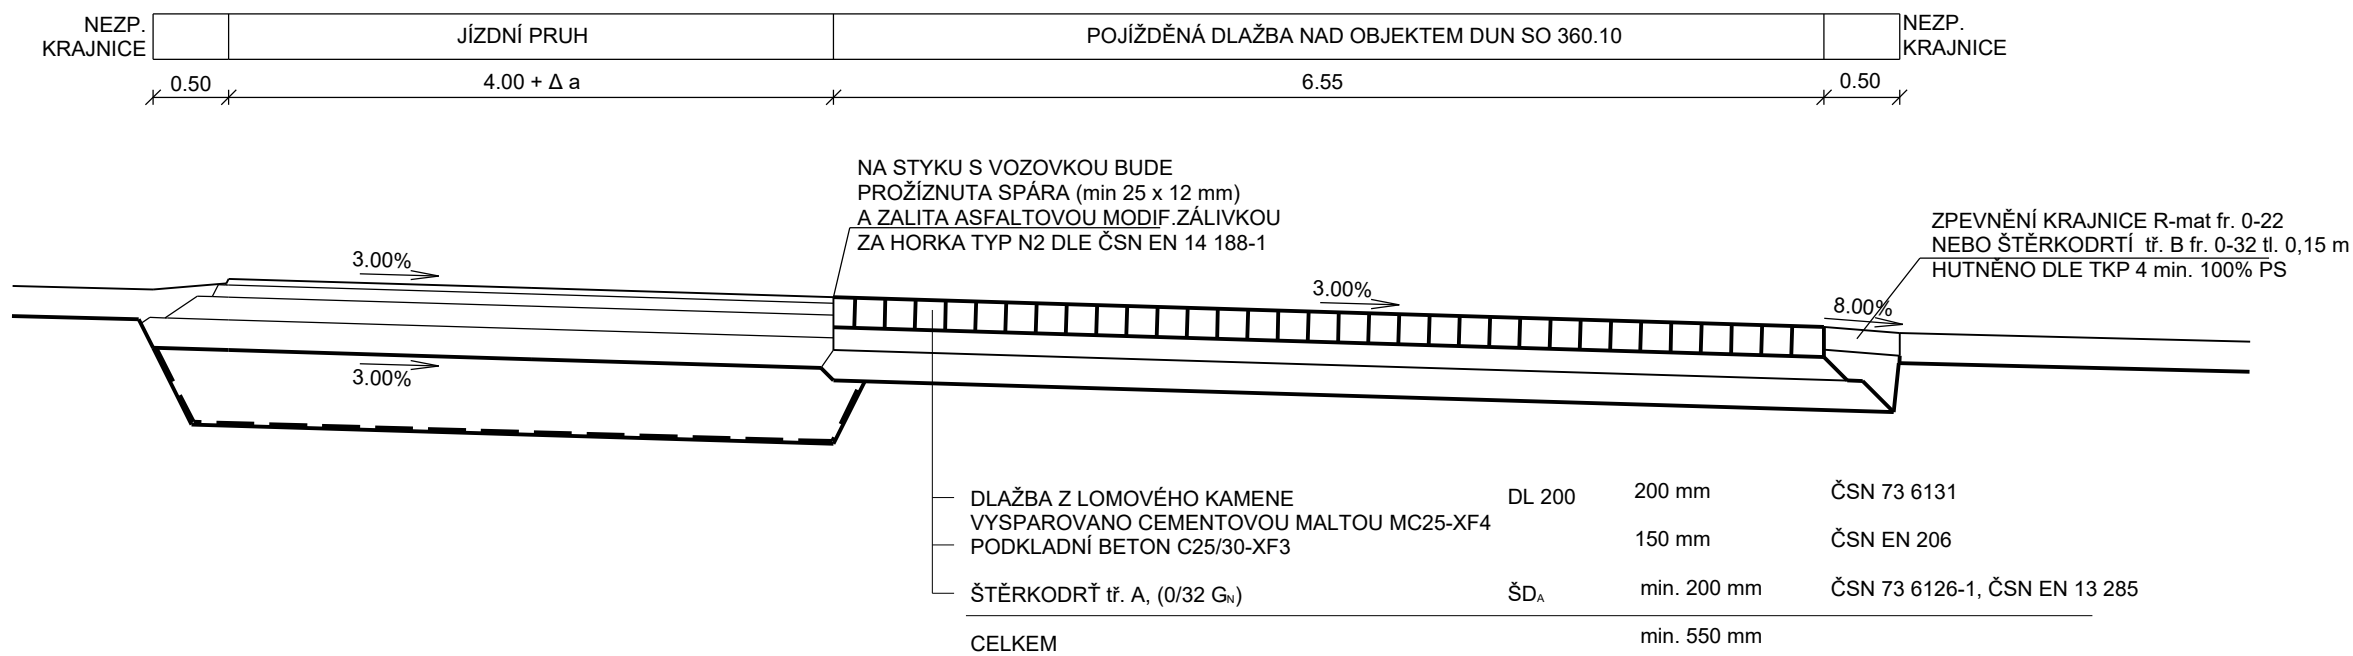



SO 148 - PŘÍJEZD K DUN v km 7,450
VZOROVÉ PŘÍČNÉ ŘEZY
M 1 : 50

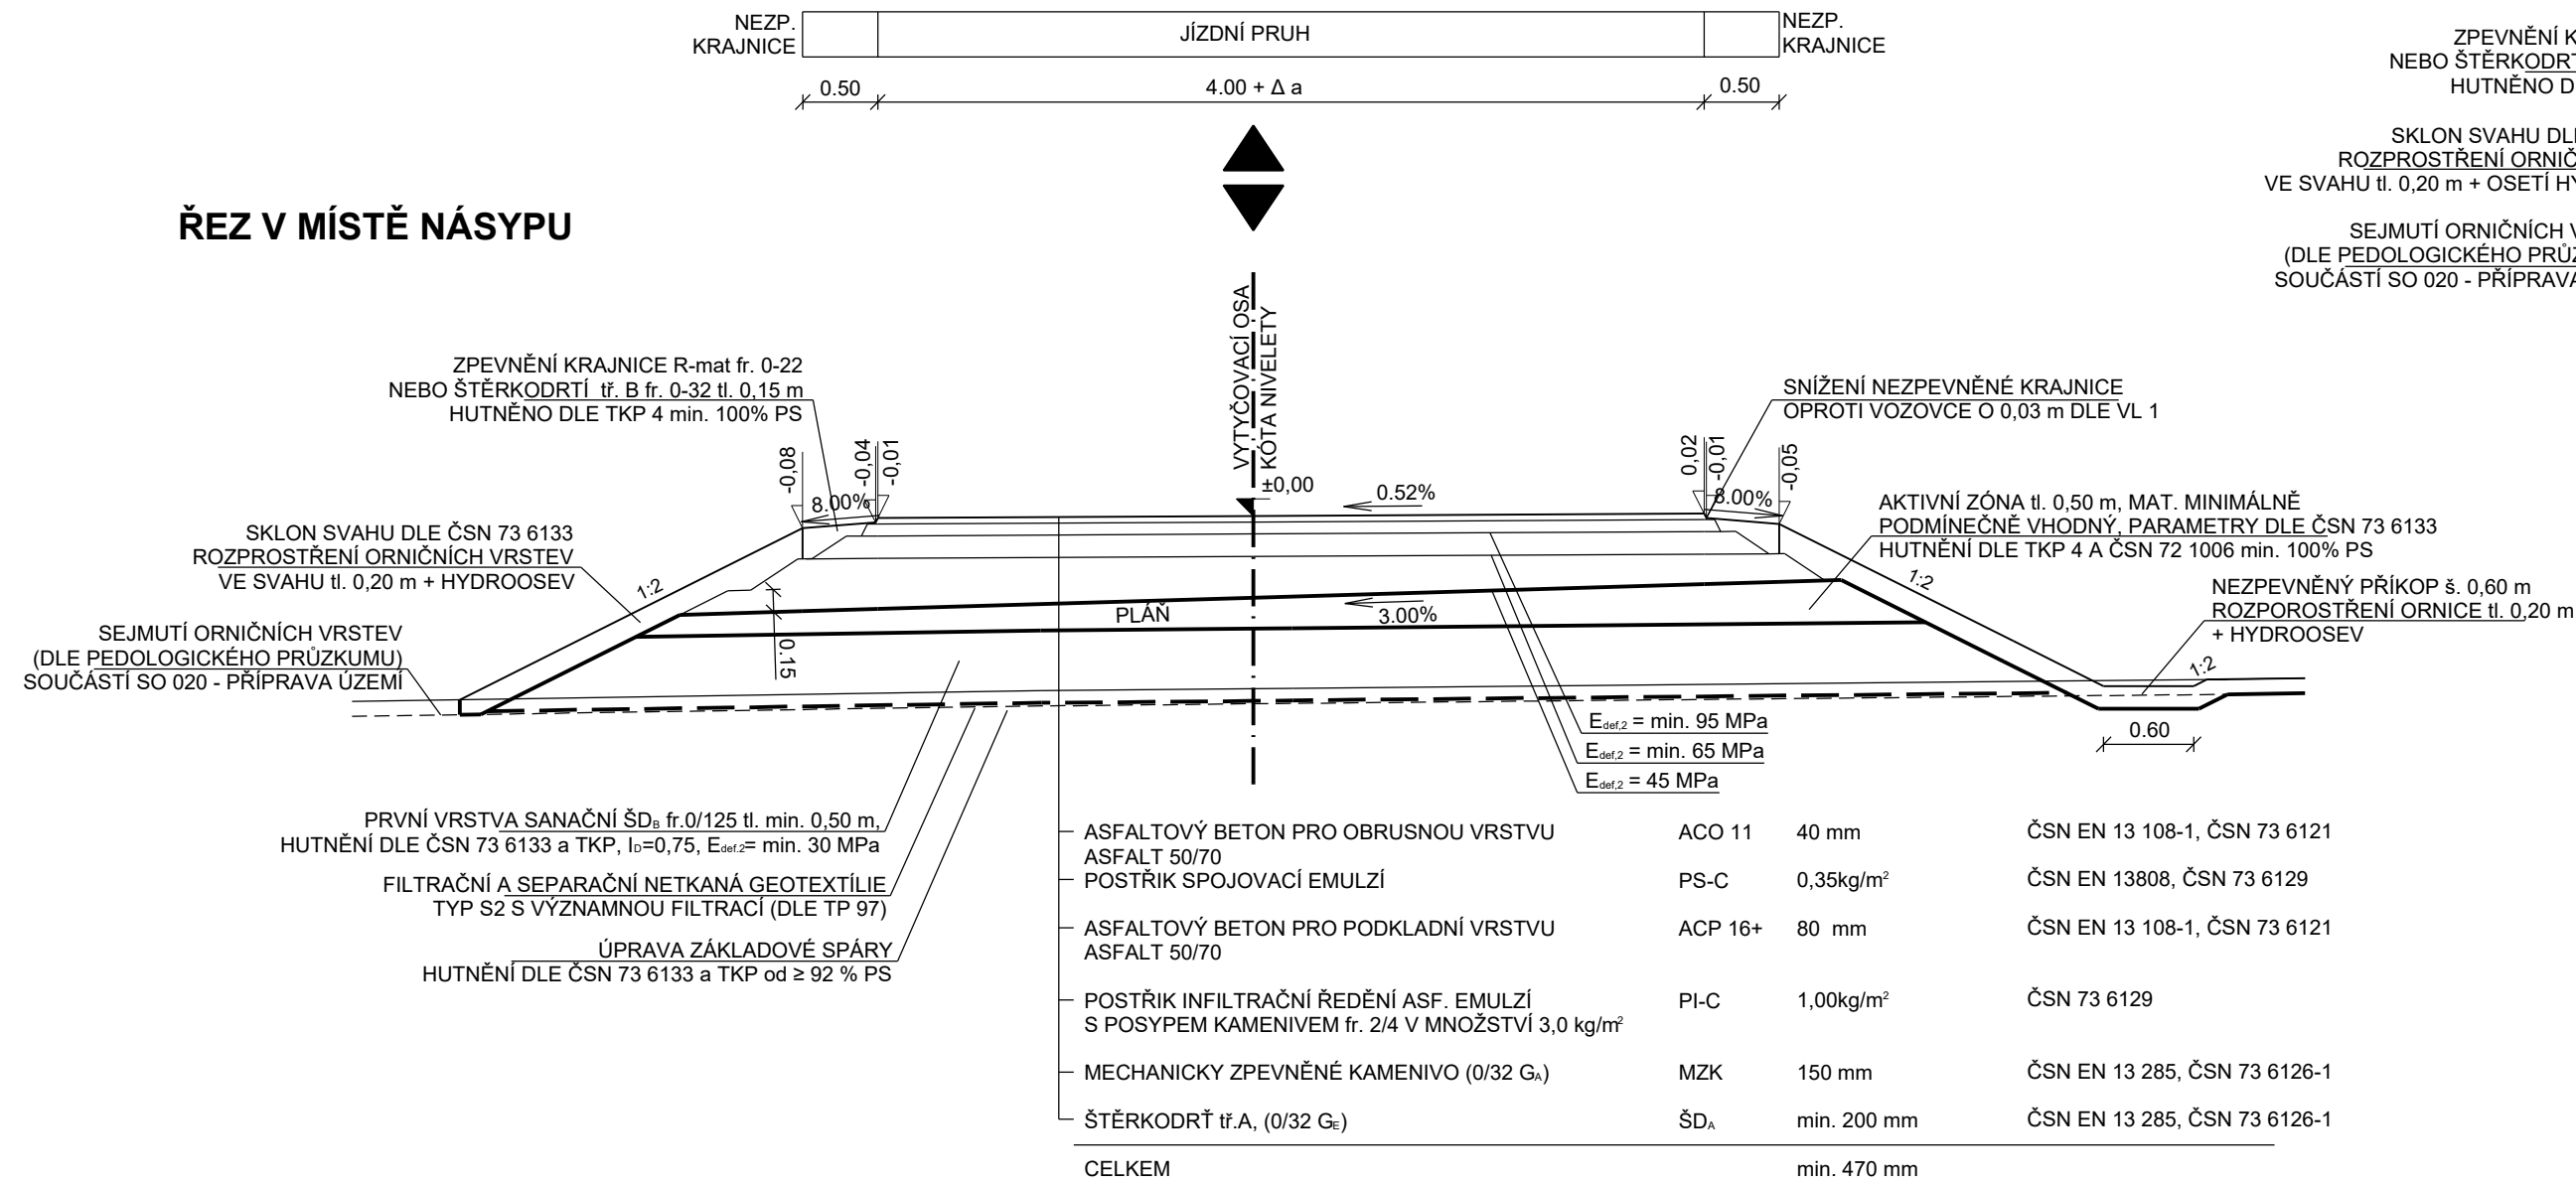


KATEGORIE MO1k -/5/30
JEDNOPRUHOVÁ, OBOUSMĚRNÁ

TŘÍDA DOPRAVNÍHO ZATÍŽENÍ IV
NÁVRHOVÁ ÚROVEŇ PORUŠENÍ D1
TYP PODLOŽÍ PIII (D1-A-2)
D1-N-11, TDZ IV, P III (DLE STARÉHO KATALOGU)

DETAIL UKONČENÍ VRSTEV VOZOVKY

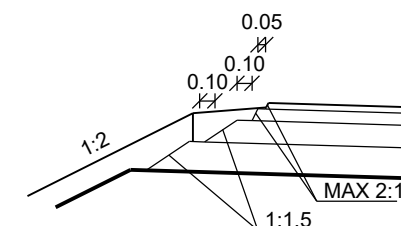

DETAIL NAPOJENÍ KONSTRUKČNÍCH VRSTEV VOZOVKY NA SO 127

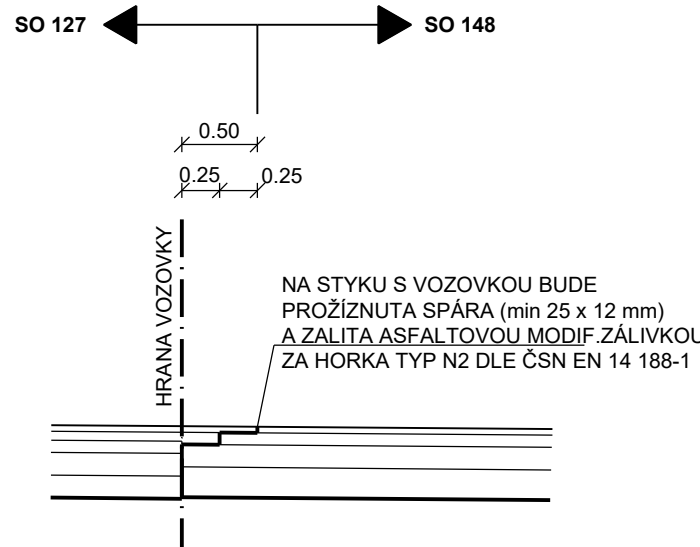

SO 148 Příjezd k DUN v km 7,450

Objednatel:

ŘEDITELSTVÍ SILNIC A DÁLNIC

Ředitelství silnic a dálnic s. p.

Čerčanská 2023/12, Krč, 140 00 Praha 4

Zhotovitel:

**Valbek, spol. s r.o.**

Vaňurova 505/17
460 07 Liberec 3

	Vypracoval	Bc. J. HALABURKA		Zak. číslo	21-LI13-001
	Zodp. projektant	ING. T. KLIMENT		Datum	02/2025
	Tech. kontrola	ING. M. HANŽL		Stupeň	PDPS
	Akce			Počet formátů	4 x A4
	I/16 MLADÁ BOLESLAV - MARTINOVICE			Měřítko	1 : 50
Zhotovitel: Valbek, spol. s r.o. Vaňurova 505/17 460 07 Liberec 3	Příloha VZOROVÉ PŘÍČNÉ ŘEZY	4		Č. přílohy	Paré