



SO 148 - PŘÍJEZD K DUN v km 7,450

PŘÍČNÉ ŘEZY km 0,020 - 0,100


M 1 : 100

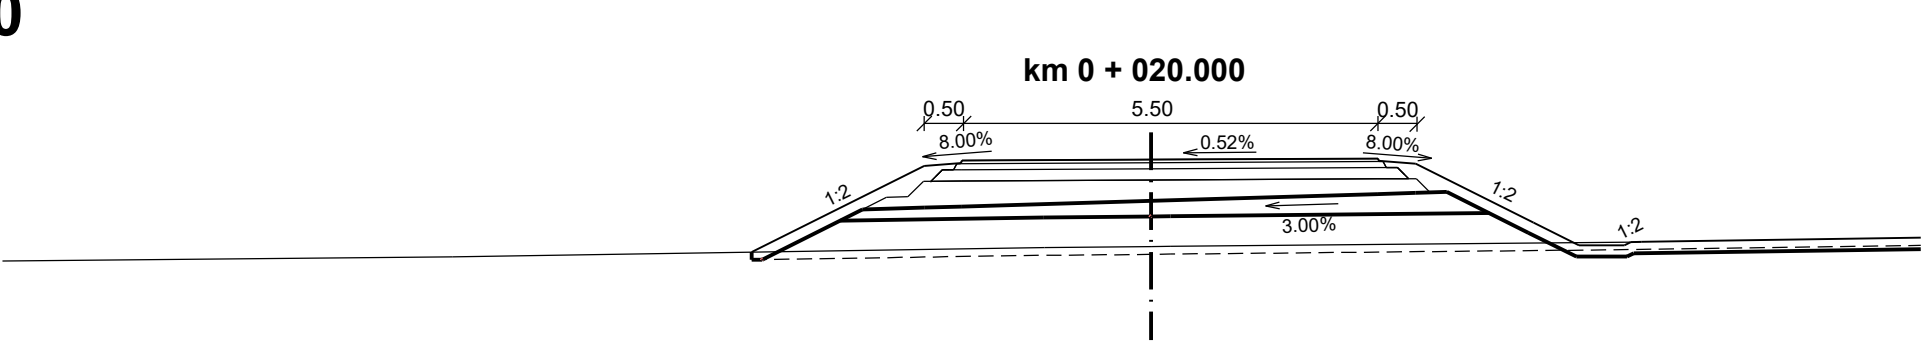


		S. R. 219 m															
PROJEKTOVANÝ STAV																	
ODSAZENÍ OD OSY																	
STÁVAJÍCÍ TERÉN																	
ODSAZENÍ OD OSY																	

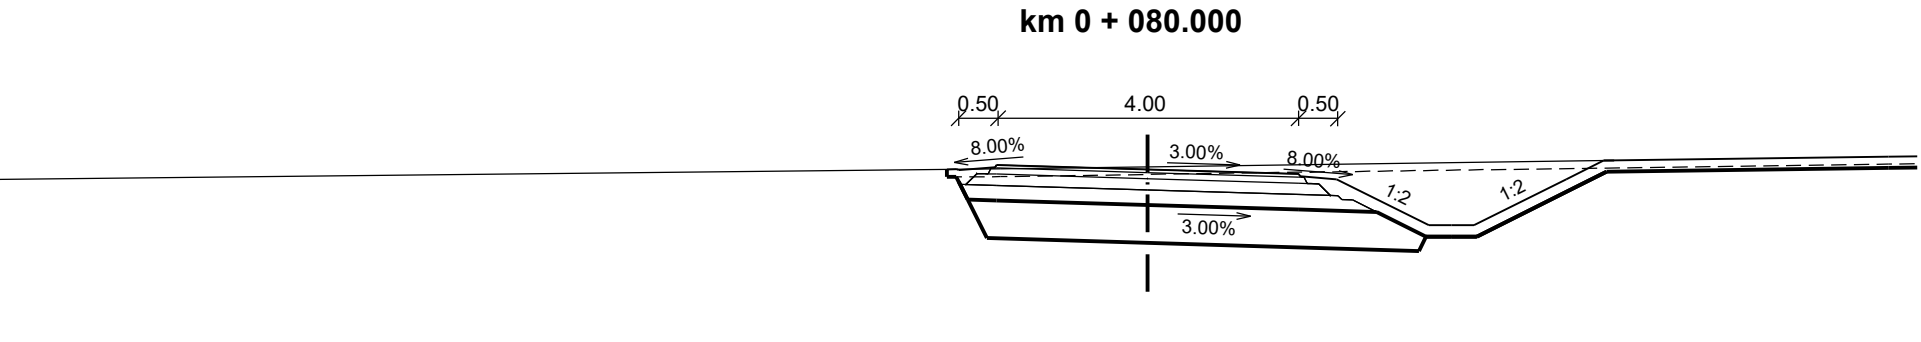


		S. R. 218 m																	
PROJEKTOVANÝ STAV																			
ODSAZENÍ OD OSY																			

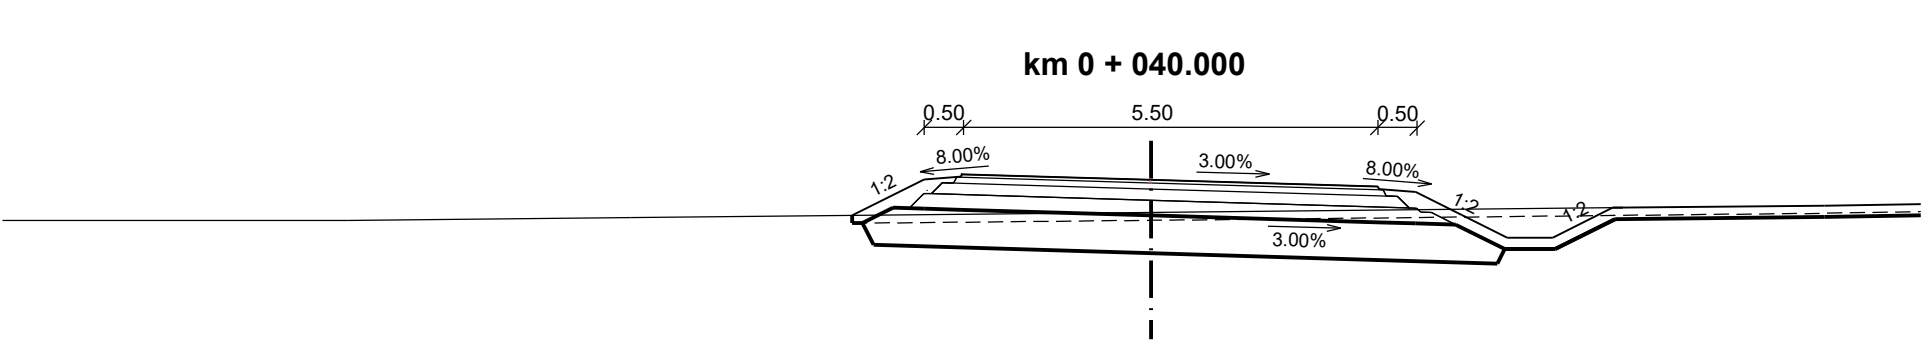

		S. R. 219 m									
PROJEKTOVANÝ STAV											
ODSAZENÍ OD OSY											

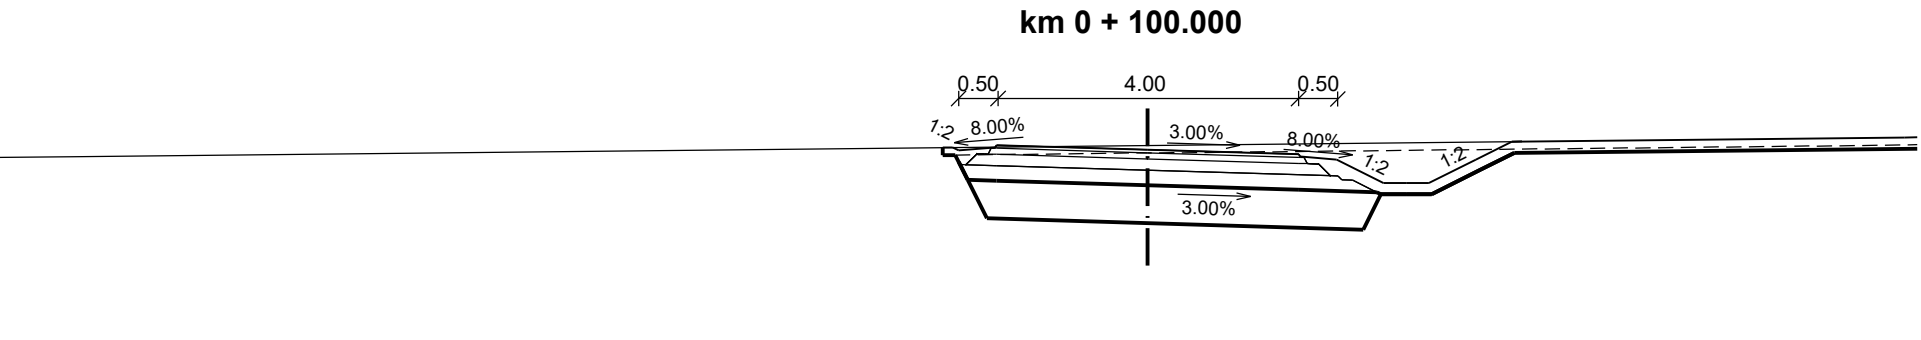

		S. R. 218 m																	
PROJEKTOVANÝ STAV		-2.58	221.71	-2.50	221.67	-2.00	221.74	0.00	221.68	2.00	221.62	2.50	221.55	3.12	221.24	3.72	221.24	4.81	221.79
ODSAZENÍ OD OSY																			
STÁVAJÍCÍ TERÉN								0.00	221.74										
ODSAZENÍ OD OSY																			

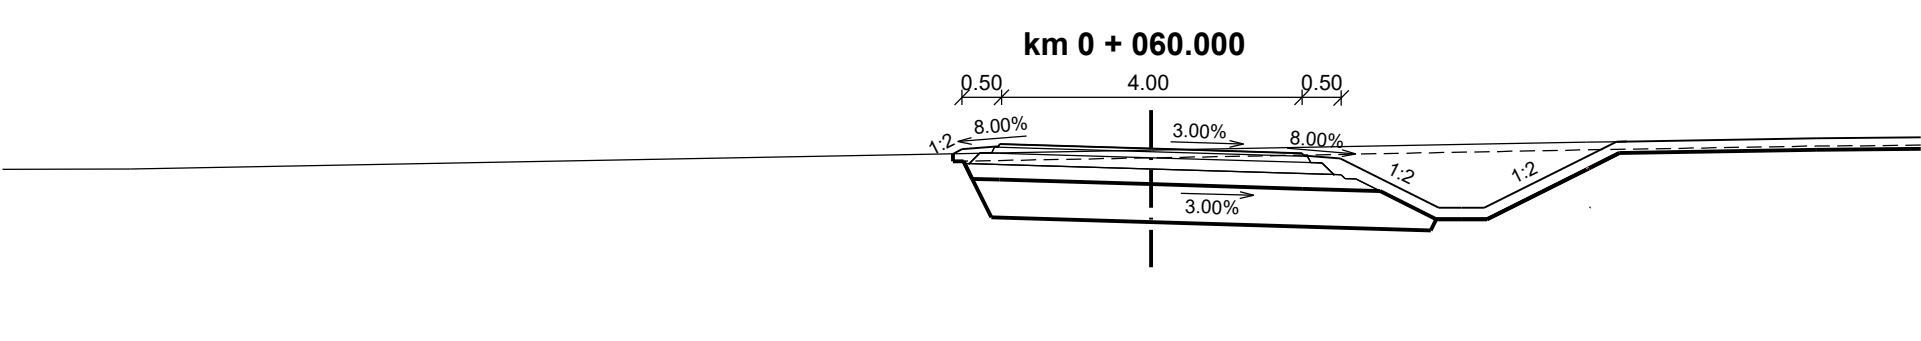

		S. R. 218 m																	
PROJEKTOVANÝ STAV																			
ODSAZENÍ OD OSY		-2.62	222.01	-2.50	222.07	-2.00	222.14	0.00	222.08	2.00	222.02	2.50	221.95	3.81	221.30	4.41	221.30	6.16	222.17
STÁVAJÍCÍ TERÉN								0.00	222.06									5.76	222.16
ODSAZENÍ OD OSY																			8.80 222.21

Výškový systém: Bpv

SO 148 Příjezd k DUN v km 7,450

Objednatel:



**ŘEDITELSTVÍ
SILNIC
A DÁLNIC**

Ředitelství silnic a dálnic s. p.
Čerčanská 2023/12, Krč, 140 00 Praha 4



Valbek

Valbek, spol. s r.o.
Vaňurova 505/17
460 07 Liberec 3

	Vypracoval	Bc. J. HALABURKA		Zak. číslo	21-LI13-001
	Zodp. projektant	ING. T. KLIMENT		Datum	02/2025
	Tech. kontrola	ING. M. HANŽL		Stupeň	PDPS
	Akce I/16 MLADÁ BOLESLAV - MARTINOVICE			Počet formátů	8 x A4
				Měřítko	1 : 100
Zhotovitel: Valbek, spol. s r.o. Vaňurova 505/17 460 07 Liberec 3	Příloha PŘÍČNÉ ŘEZY km 0,020 - 0,100			Č. přílohy	Paré
				5	