
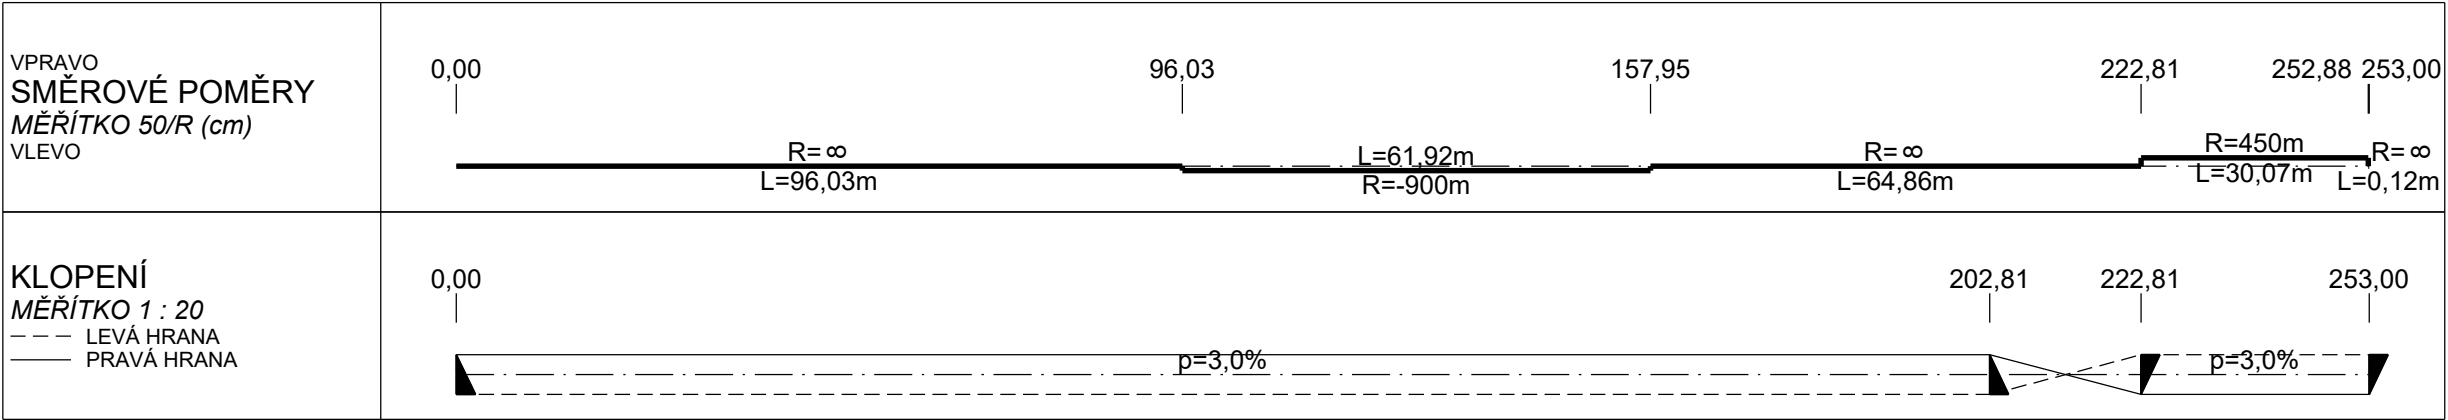


SO 150 - PŘÍSTUP NA POZEMKY k.ú. KOSMONOSY

PODÉLNÝ PROFIL SO 150.2, M 1 : 1 000 / 100

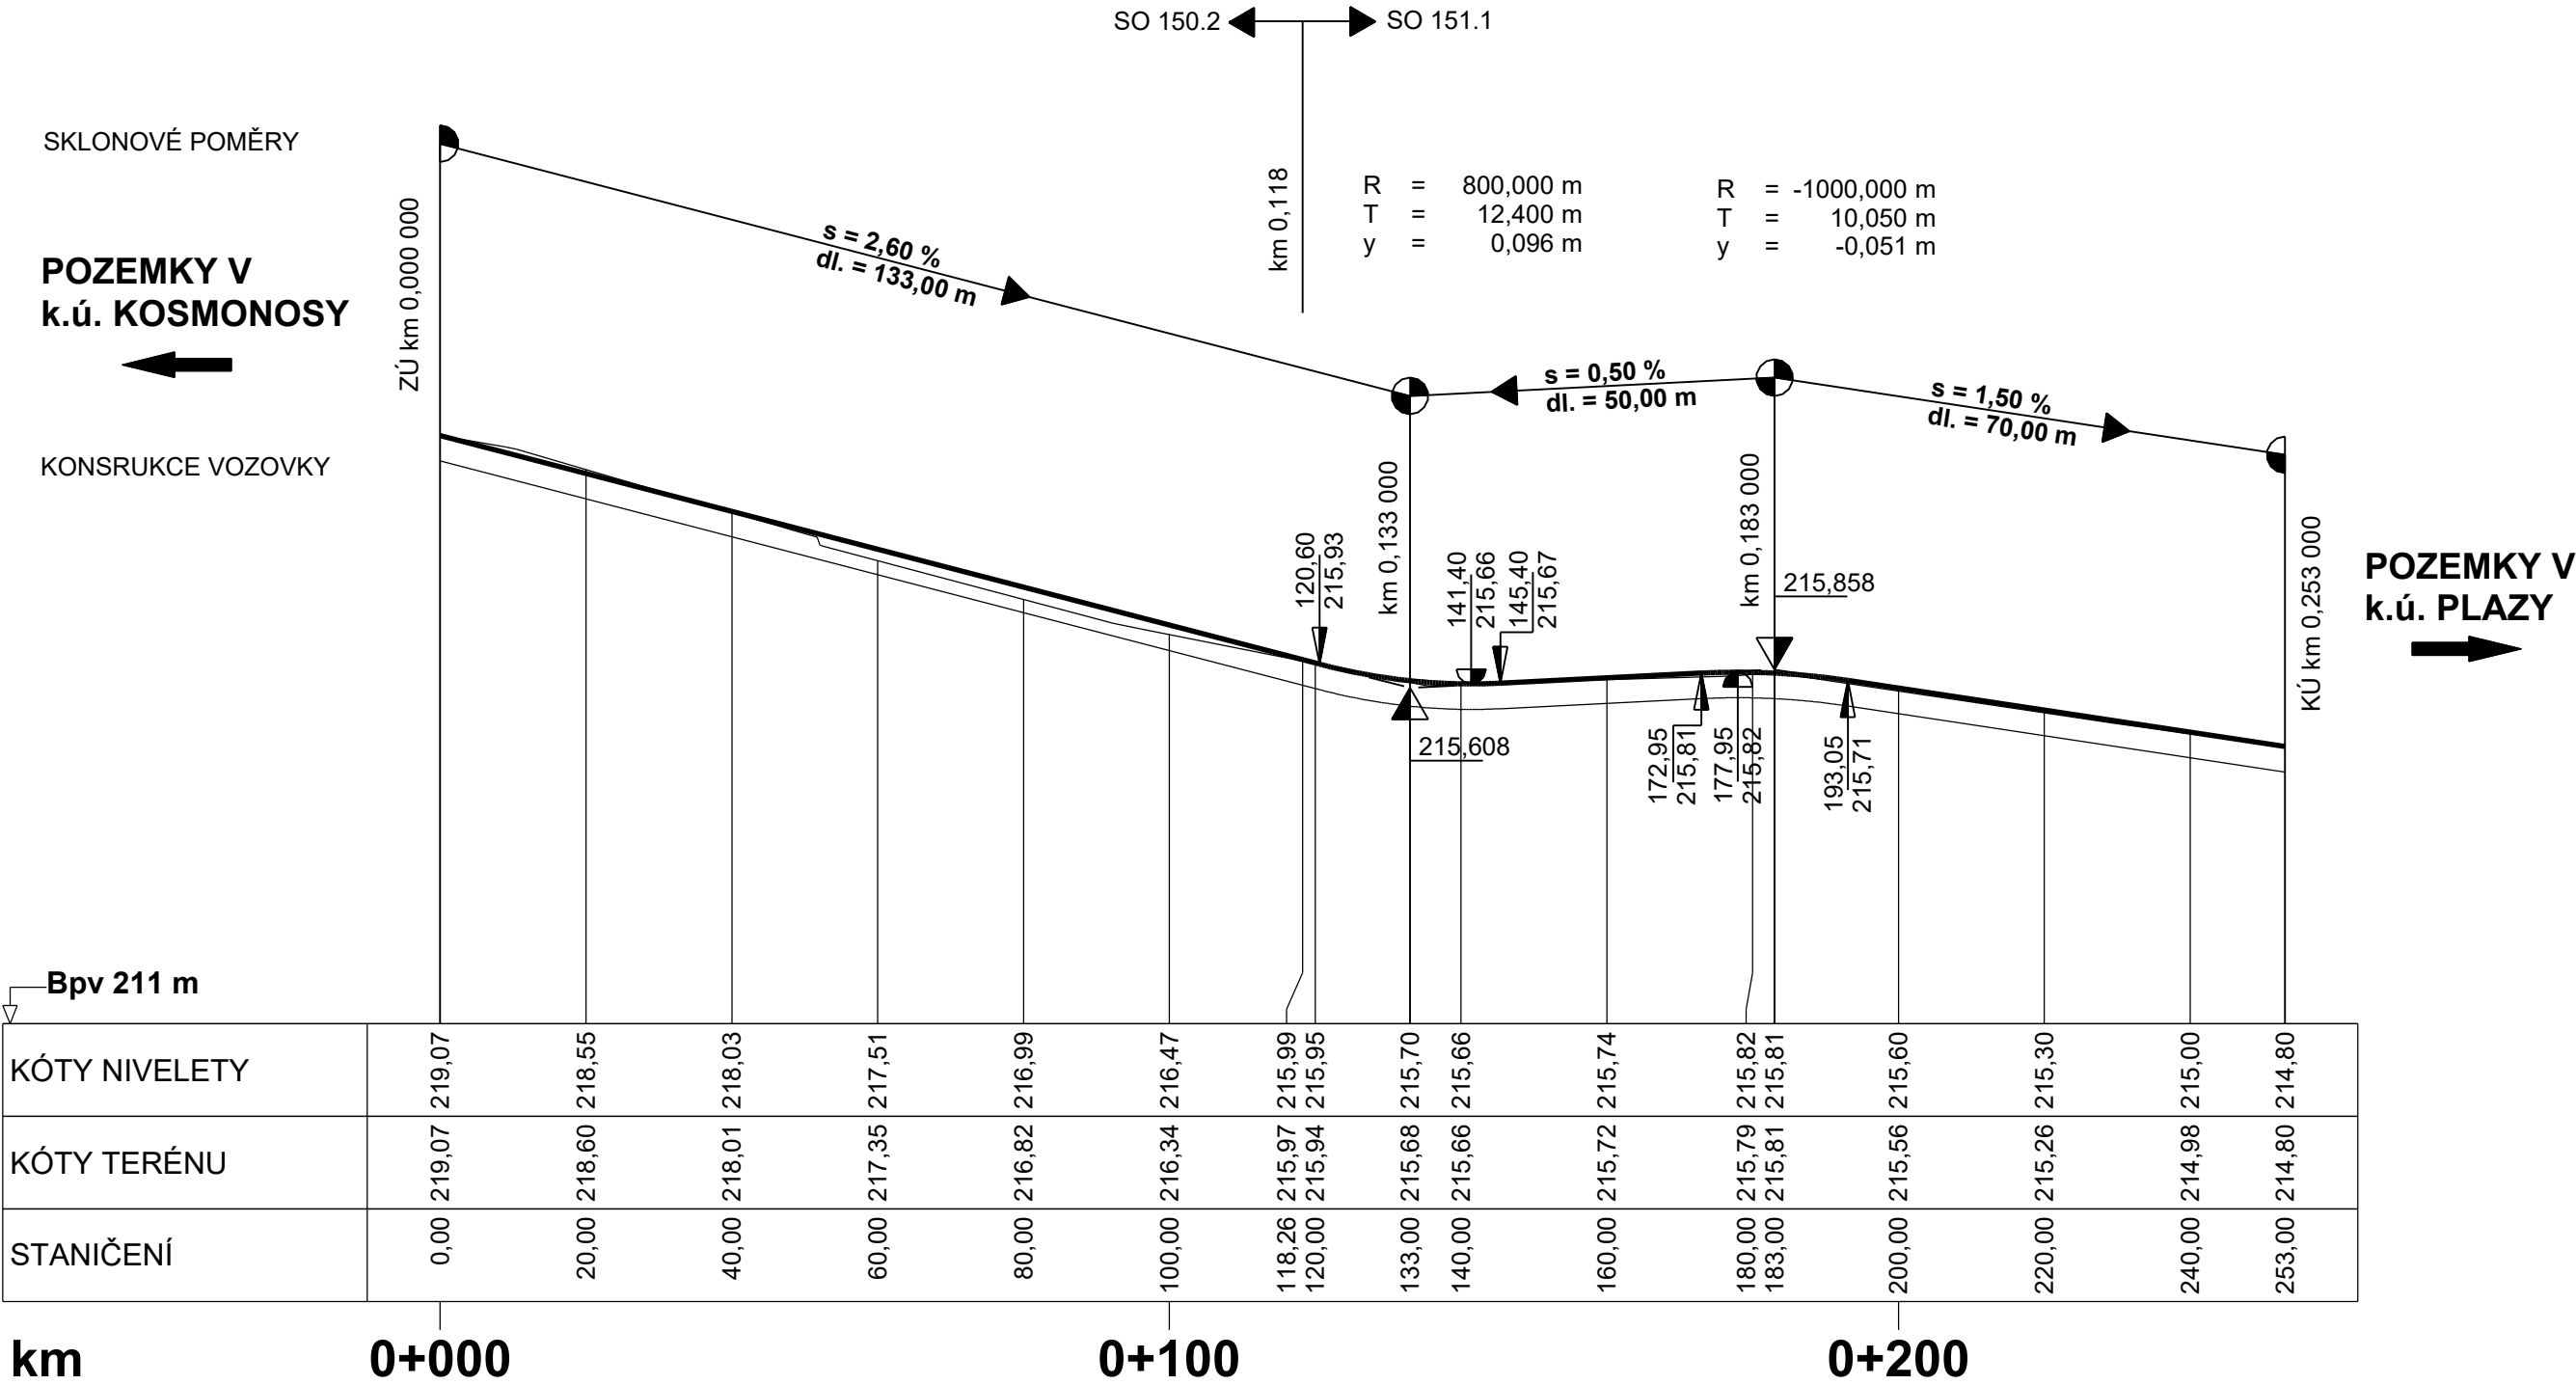

Výškový systém Bpv

SO 150

Přístupy na pozemky k.ú. Kosmonosy

Objednatel:



ŘEDITELSTVÍ
SILNIC
A DÁLNIC

Ředitelství silnic a dálnic s. p.

Čerčanská 2023/12, Krč, 140 00 Praha 4

Zhotovitel:



Valbek, spol. s r.o.

Vaňurova 505/17

460 07 Liberec 3

HIP:

ING. T. KLIMENT



Zhotovitel:

Valbek, spol. s r.o.

Vaňurova 505/17

460 07 Liberec 3

Vypracoval

ING. A. DUMANSKA

Zodp. projektant

ING. T. KLIMENT

Tech. kontrola

ING. M. HANŽL

Akce

I/16 MLADÁ BOLESLAV - MARTINOVICE

Příloha

PODÉLNÝ PROFIL SO 150.2

Zak. číslo

21-LI13-001

Datum

02/2025

Stupeň

PDPS

Počet formátů

3 x A4

Měřítko

1 : 1000/100

Č. přílohy

Paré

3.2