

SO 150 - PŘÍSTUP NA POZEMKY k.ú. KOSMONOSY

VZOROVÉ PŘÍČNÉ ŘEZY, M 1 : 50


KATEGORIE P 4,0/30

JEDNOPRUHOVÁ, OBOUSMĚRNÁ

TŘÍDA DOPRAVNÍHO ZATÍŽENÍ VI

NÁVRHOVÁ ÚROVEŇ PORUŠENÍ D2

TYP PODLOŽÍ PIII (PN 6-5)

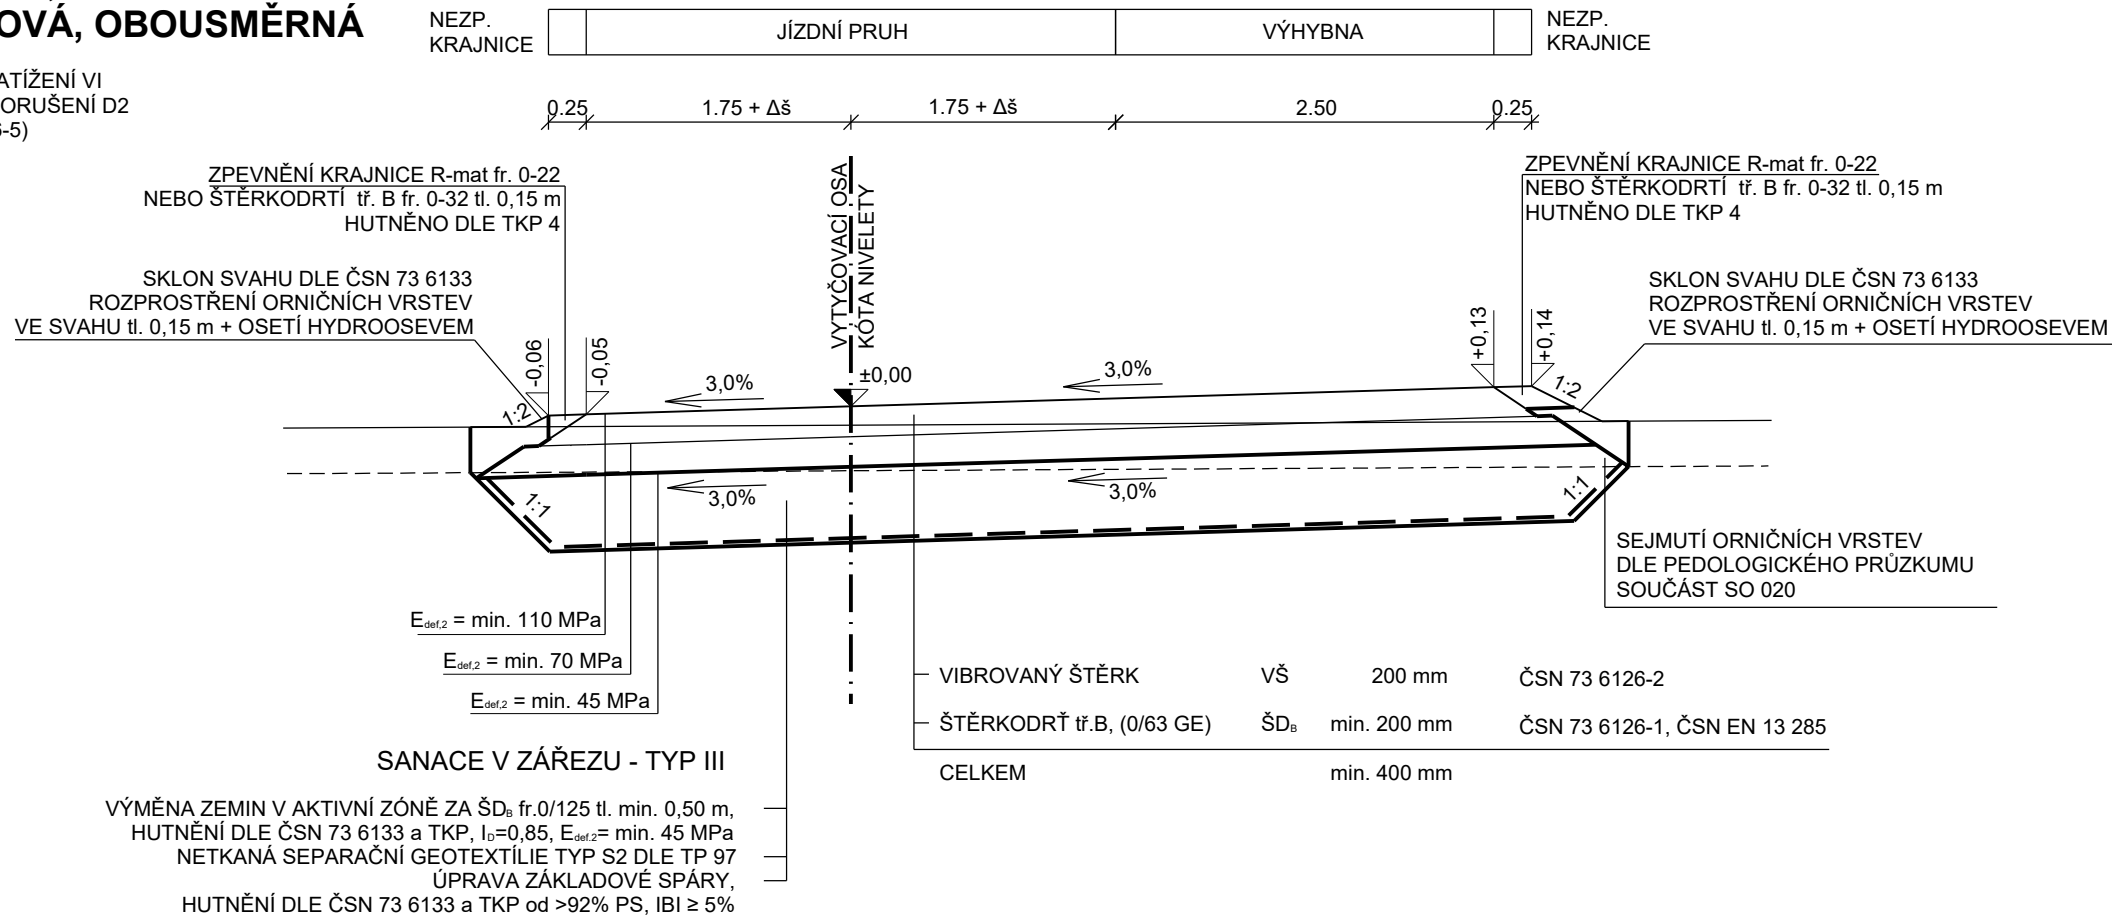

SO 150 Přístupy na pozemky v k.ú. Kosmonosy

Objednatel:



ŘEDITELSTVÍ
SILNIC
A DÁLNIC

Ředitelství silnic a dálnic s. p.
Čerčanská 2023/12, Krč, 140 00 Praha 4

Zhotovitel:



Valbek

Valbek, spol. s r.o.
Vaňurova 505/17
460 07 Liberec 3

	Vypracoval	ING. A.DUMANSKA		Zak. číslo	21-LI13-001
	Zodp. projektant	ING. T. KLIMENT		Datum	02/2025
	Tech. kontrola	ING. M. HANŽL		Stupeň	PDPS
	Akce I/16 MLADÁ BOLESLAV - MARTINOVICE			Počet formátů	3 x A4
				Měřítko	1 : 50
Zhotovitel: Valbek, spol. s r.o. Vaňurova 505/17 460 07 Liberec 3	Příloha VZOROVÉ PŘÍČNÉ ŘEZY			Č. přílohy	Paré