


SO 150 - PŘÍSTUPY NA POZEMKY k.ú. KOSMONOSY
PODÉLNÝ PROFIL SO 150.3, M 1 : 1 000 / 100

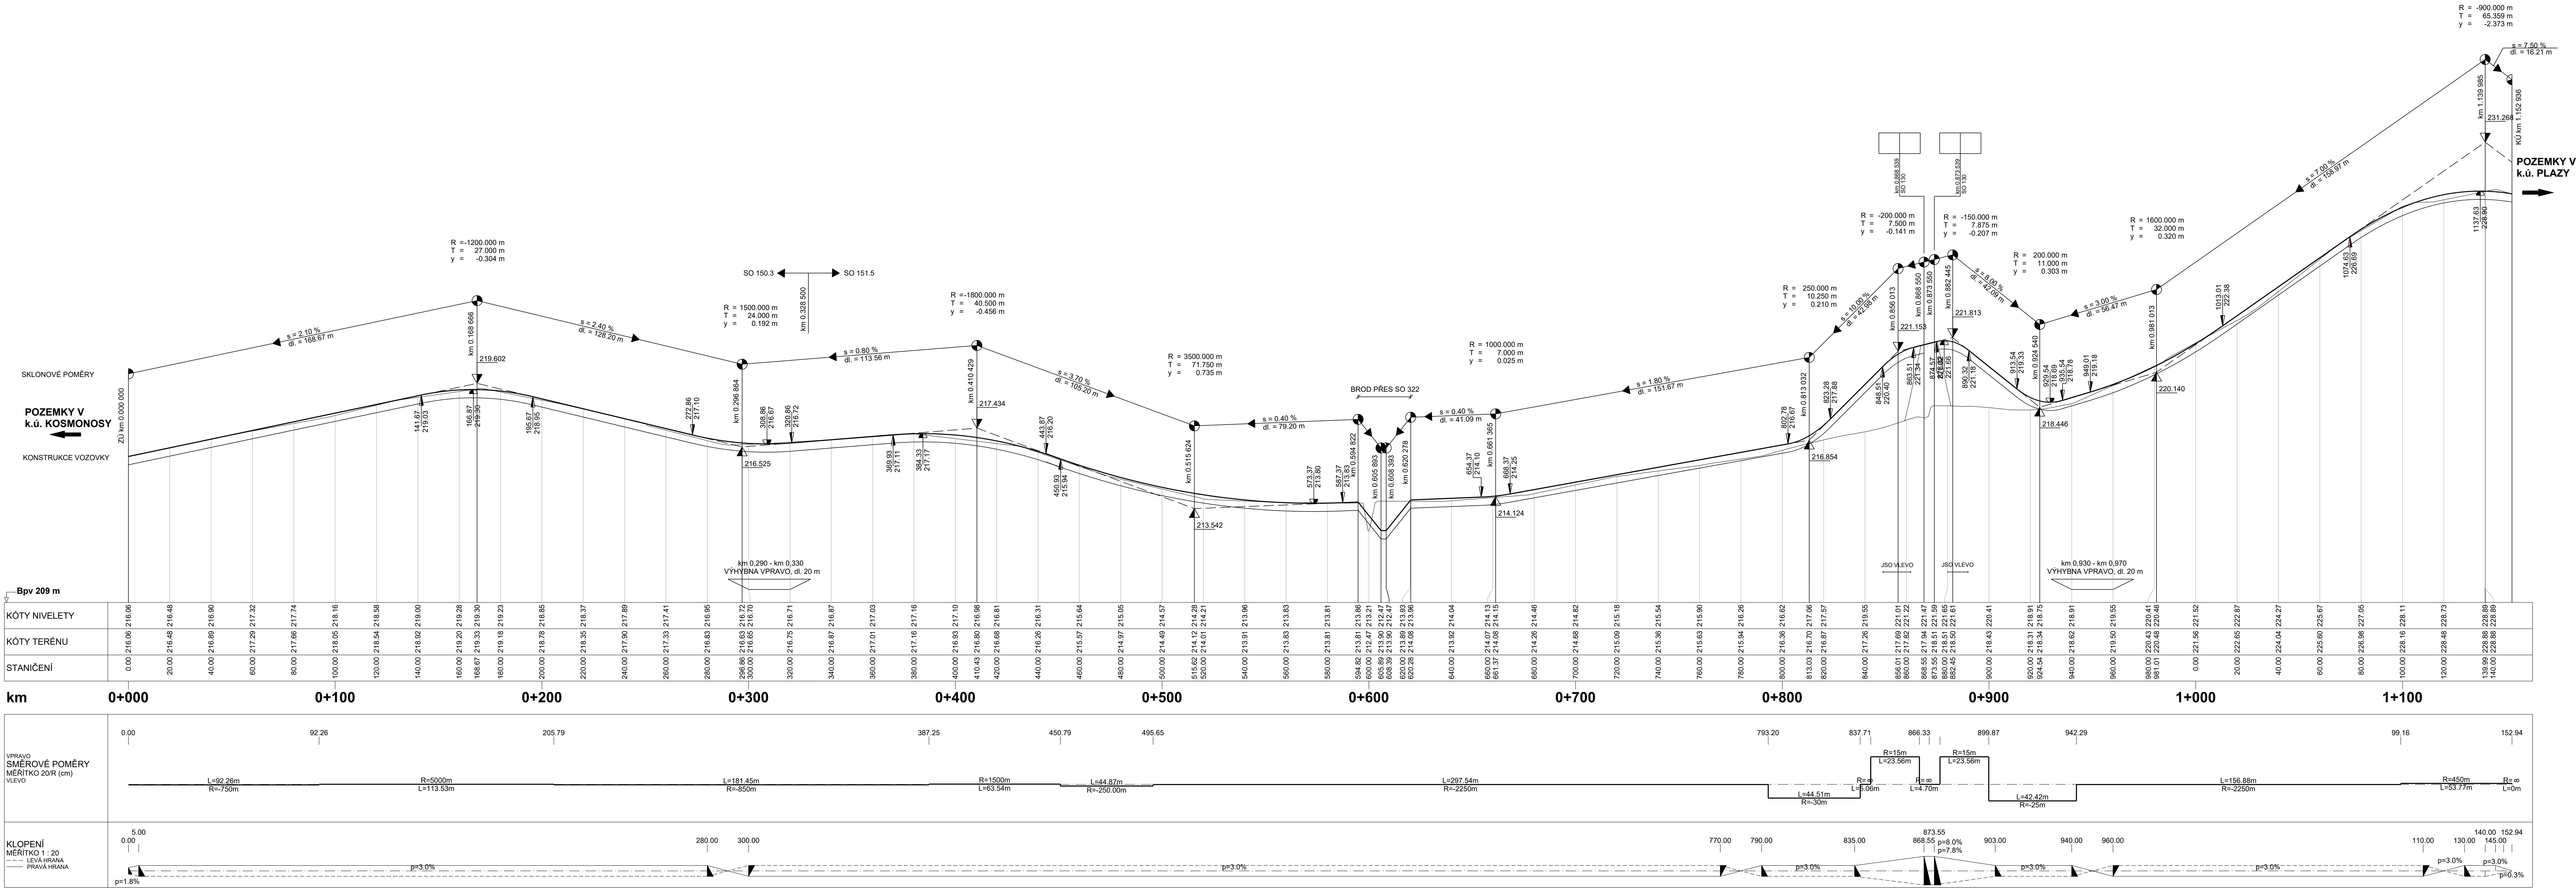

Výškový systém: Bpv

SO 150 Přístupy na pozemky k.ú. Kosmonosy

Objednatel:



Ředitelství silnic a dálnic s. p.
Čerčanská 2023/12, Krč, 140 00 Praha 4

Zhotovitel:



Valbek, spol. s r.o.
Vaňurova 505/17
460 07 Liberec 3

	Vypracoval	P. BARTUSEK		Zak. číslo	21-113-001
	Zodp. projektant	ING. T. KLIMENT		Datum	02/2025
	Techn. kontrola	ING. M. HANŽL		Stupeň	PDFS
	Aceba			Polst. formát	A4
I/16 MLADÁ BOLESLAV - MARTINOVICE				Měřítko	1 : 1 000/150
Zhotovitel: Valbek, spol. s r. o. Valbarká 10 460 07 Liberec 3	Příloha	PODÉLNÝ PROFIL SO 150.3		Č. přílohy	Paré
				3.3	