




SO 150 - PŘÍSTUPY NA POZEMKY k.ú. KOSMONOSY
PŘÍČNÉ ŘEZY SO 150.3, M 1 : 100

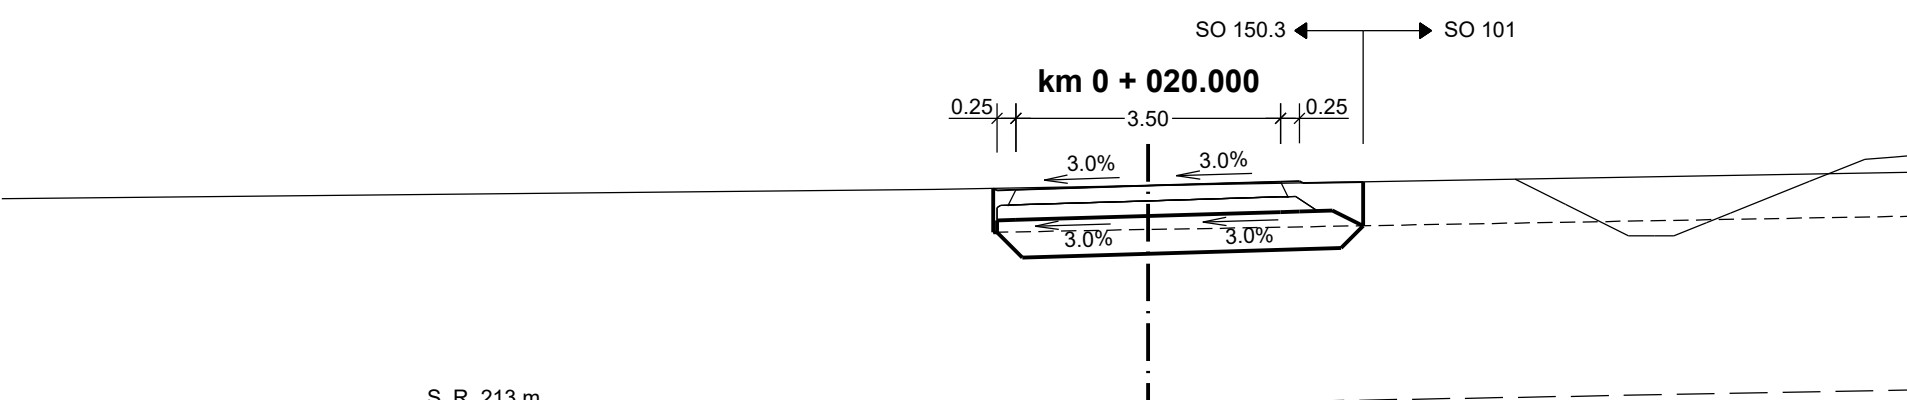


PROJEKTOVANÝ STAV	
ODSAZENÍ OD OSY	
STÁVAJÍCÍ TERÉN	
ODSAZENÍ OD OSY	

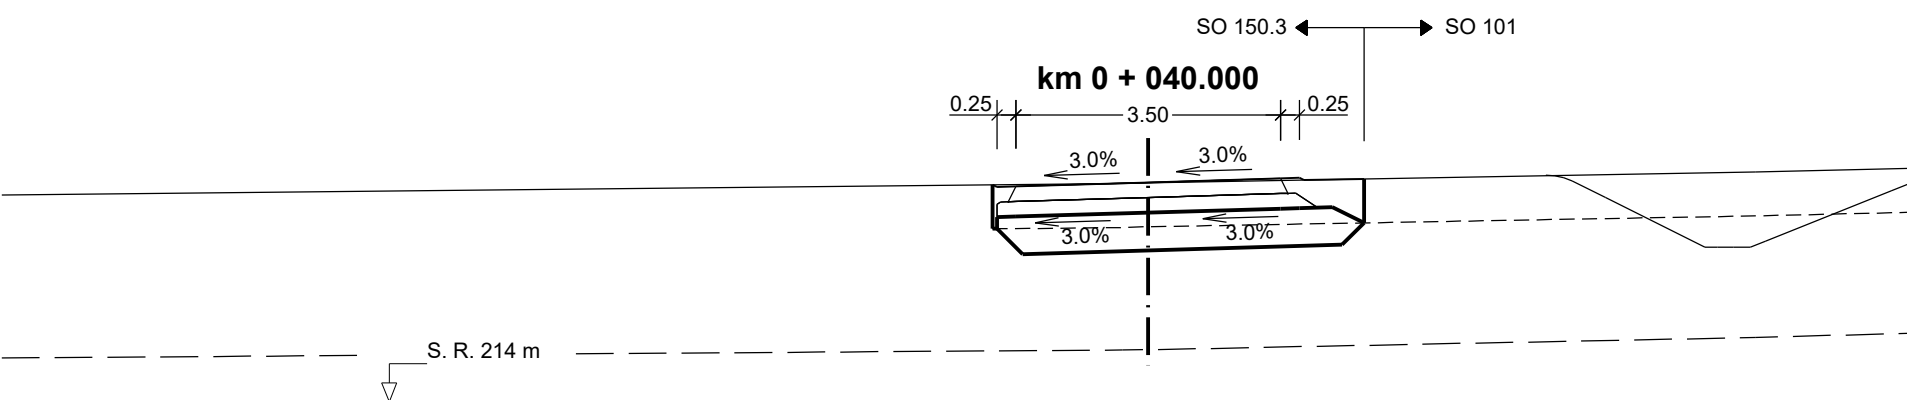


PROJEKTOVANÝ STAV	
ODSAZENÍ OD OSY	
STÁVAJÍCÍ TERÉN	
ODSAZENÍ OD OSY	

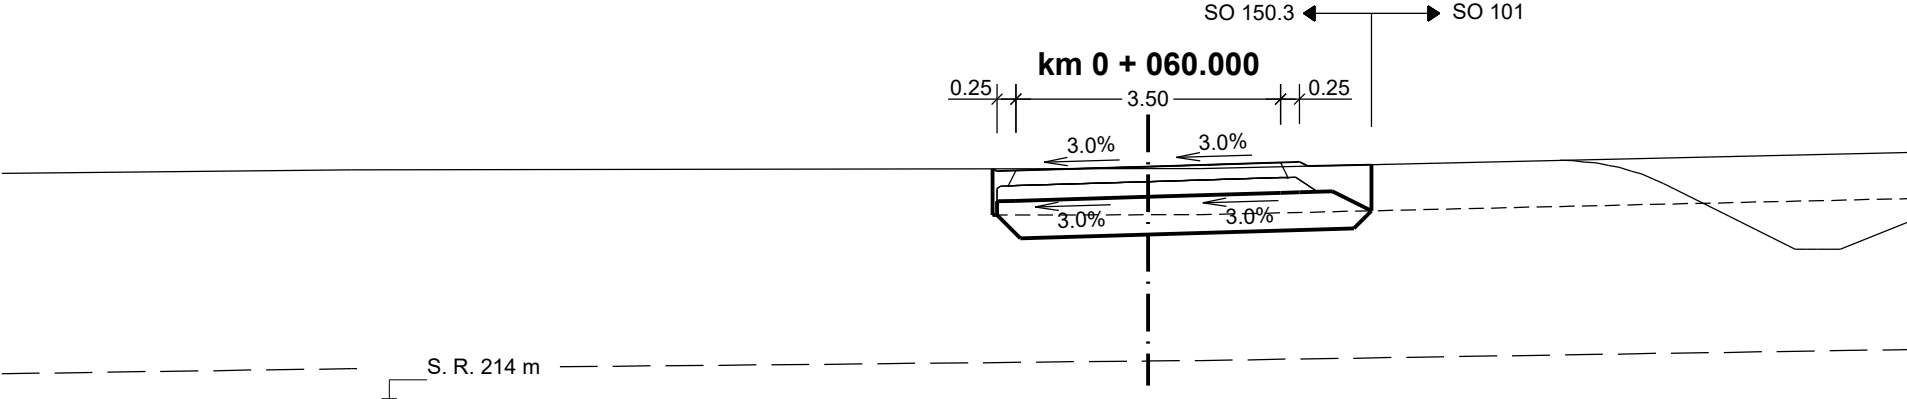


PROJEKTOVANÝ STAV	
ODSAZENÍ OD OSY	
STÁVAJÍCÍ TERÉN	
ODSAZENÍ OD OSY	

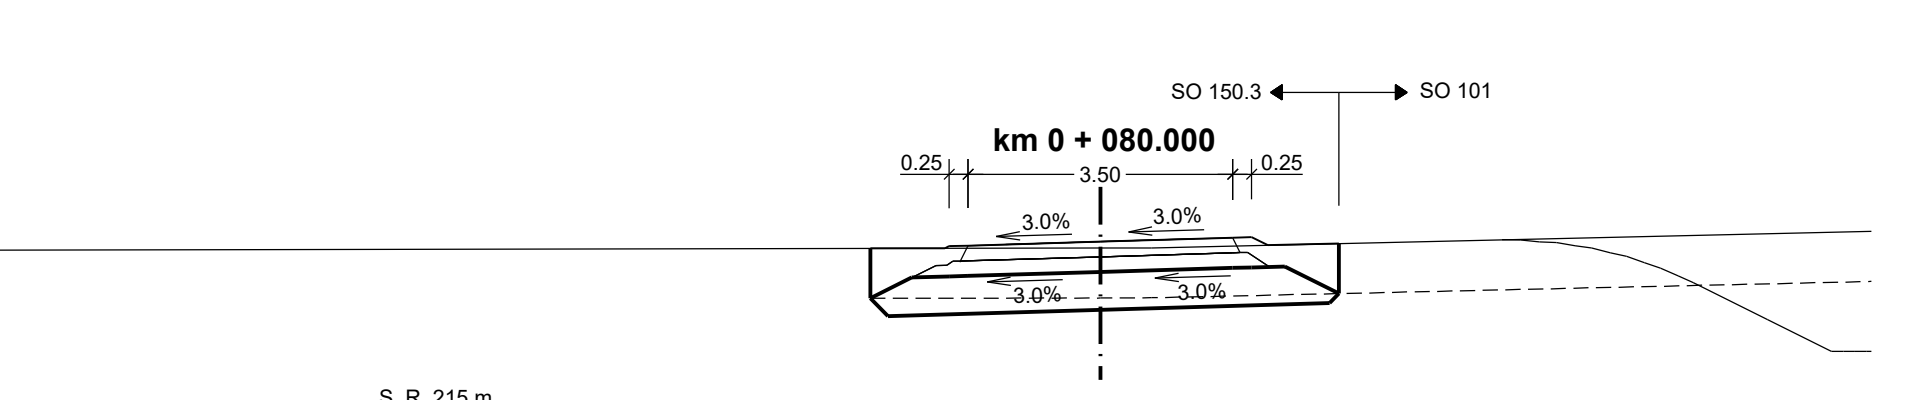


PROJEKTOVANÝ STAV	
ODSAZENÍ OD OSY	
STÁVAJÍCÍ TERÉN	
ODSAZENÍ OD OSY	

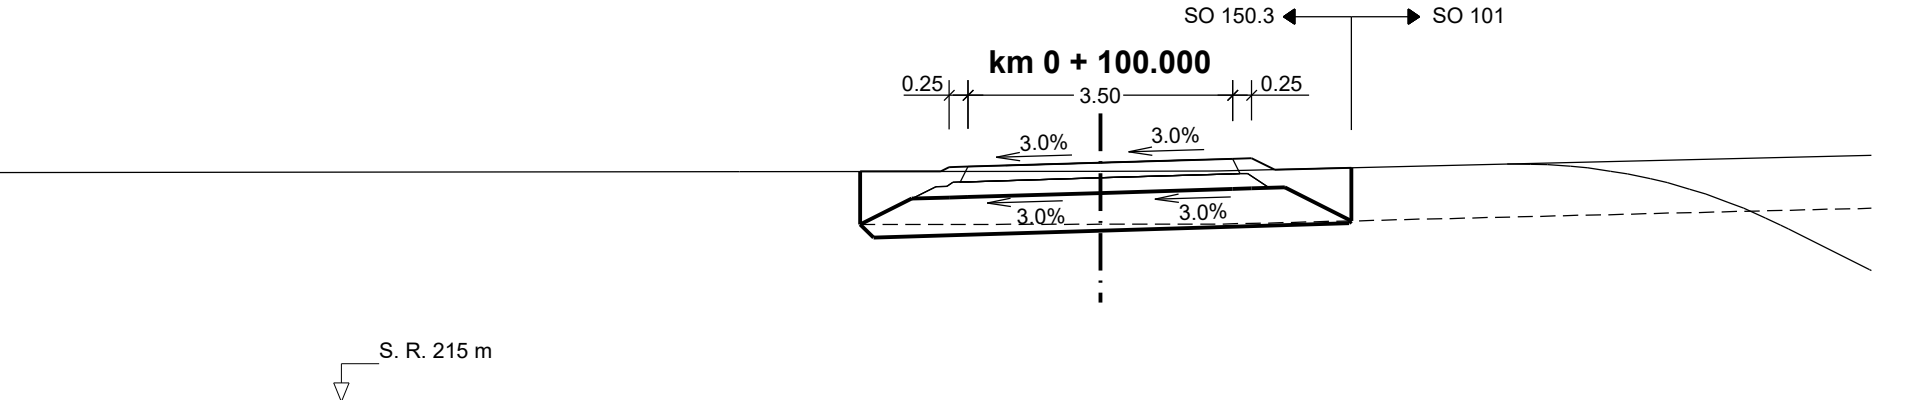


PROJEKTOVANÝ STAV	
ODSAZENÍ OD OSY	
STÁVAJÍCÍ TERÉN	
ODSAZENÍ OD OSY	

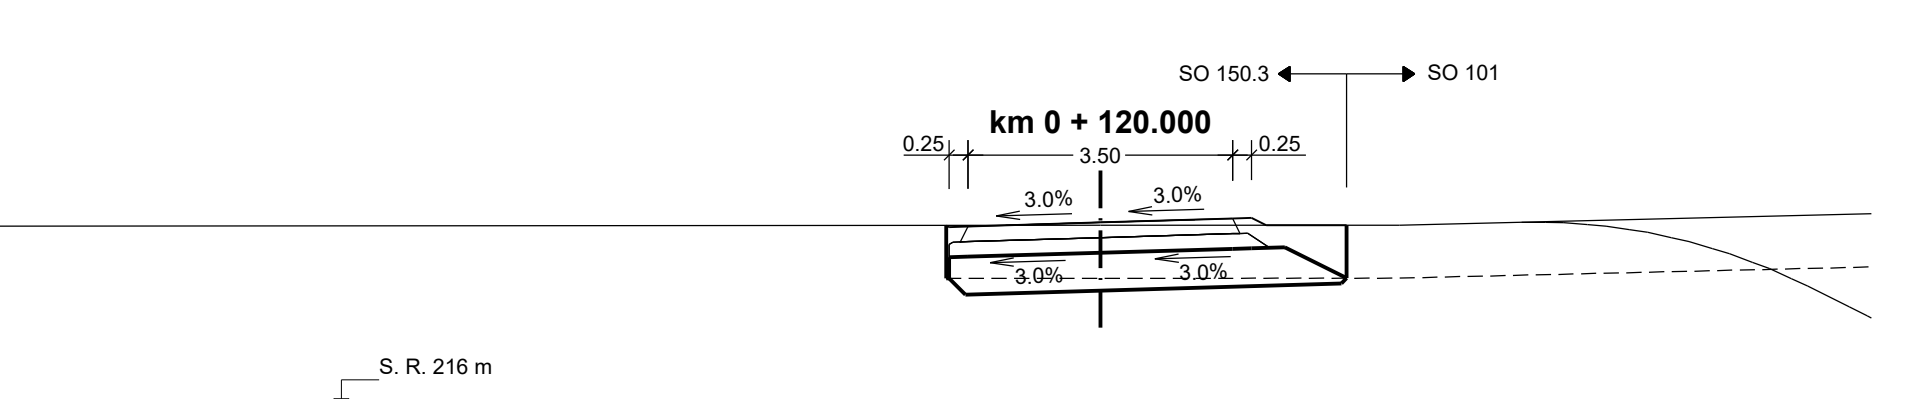


PROJEKTOVANÝ STAV	
ODSAZENÍ OD OSY	
STÁVAJÍCÍ TERÉN	
ODSAZENÍ OD OSY	

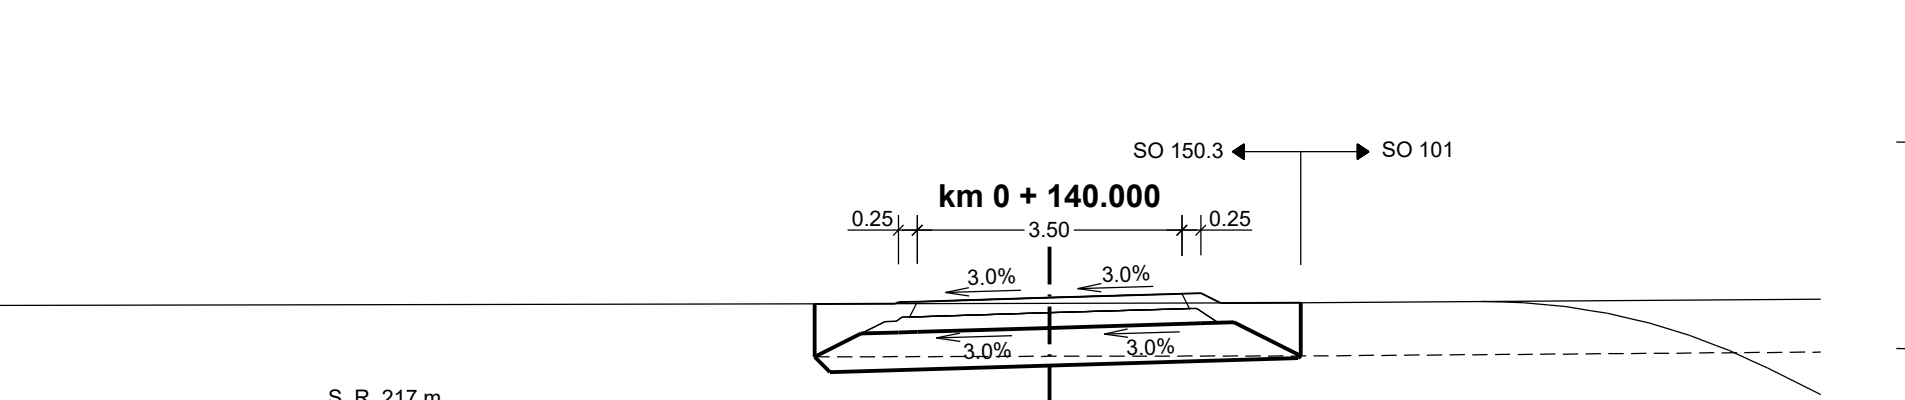


PROJEKTOVANÝ STAV	
ODSAZENÍ OD OSY	
STÁVAJÍCÍ TERÉN	
ODSAZENÍ OD OSY	

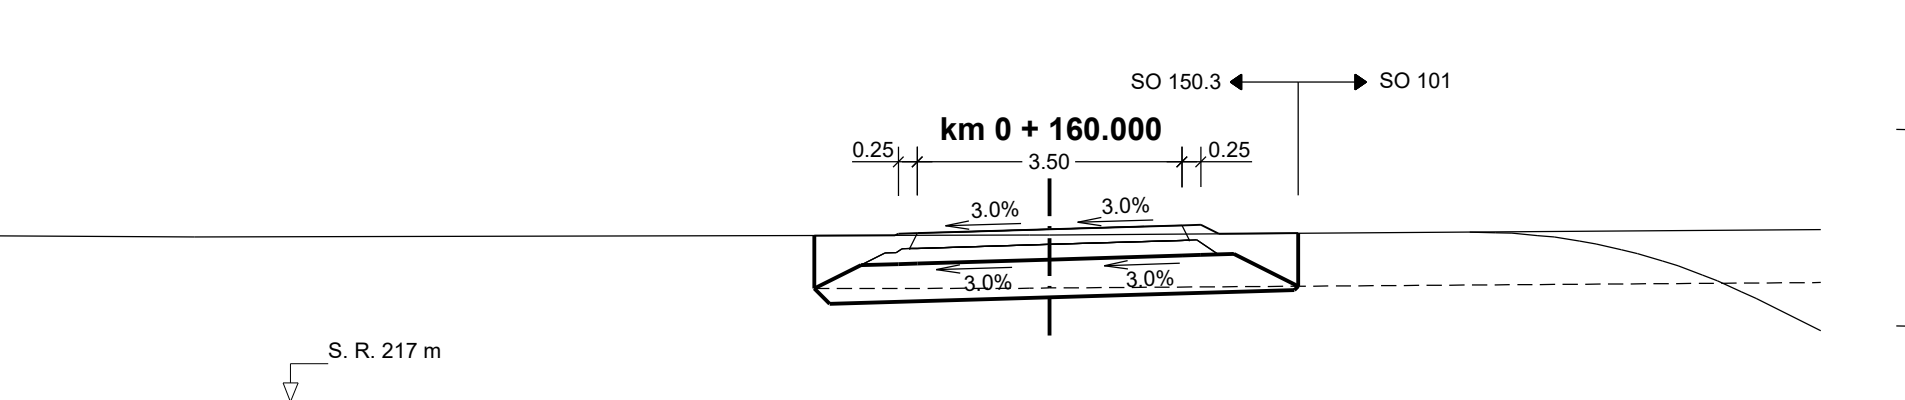


PROJEKTOVANÝ STAV	
ODSAZENÍ OD OSY	
STÁVAJÍCÍ TERÉN	
ODSAZENÍ OD OSY	

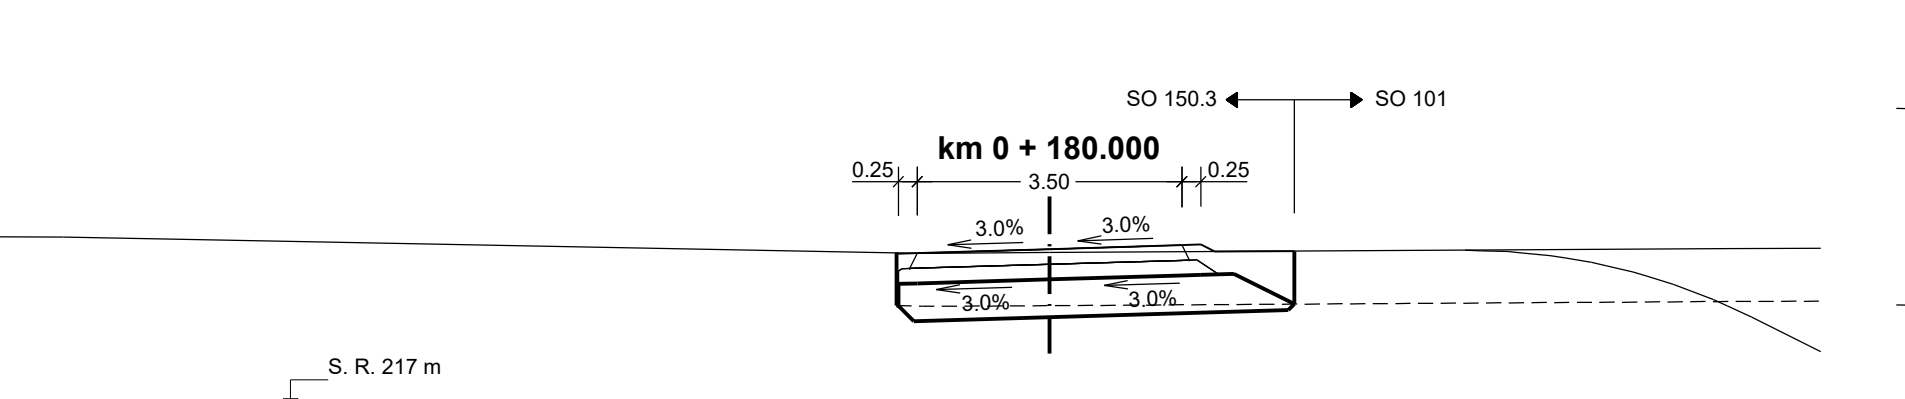


PROJEKTOVANÝ STAV	
ODSAZENÍ OD OSY	
STÁVAJÍCÍ TERÉN	
ODSAZENÍ OD OSY	

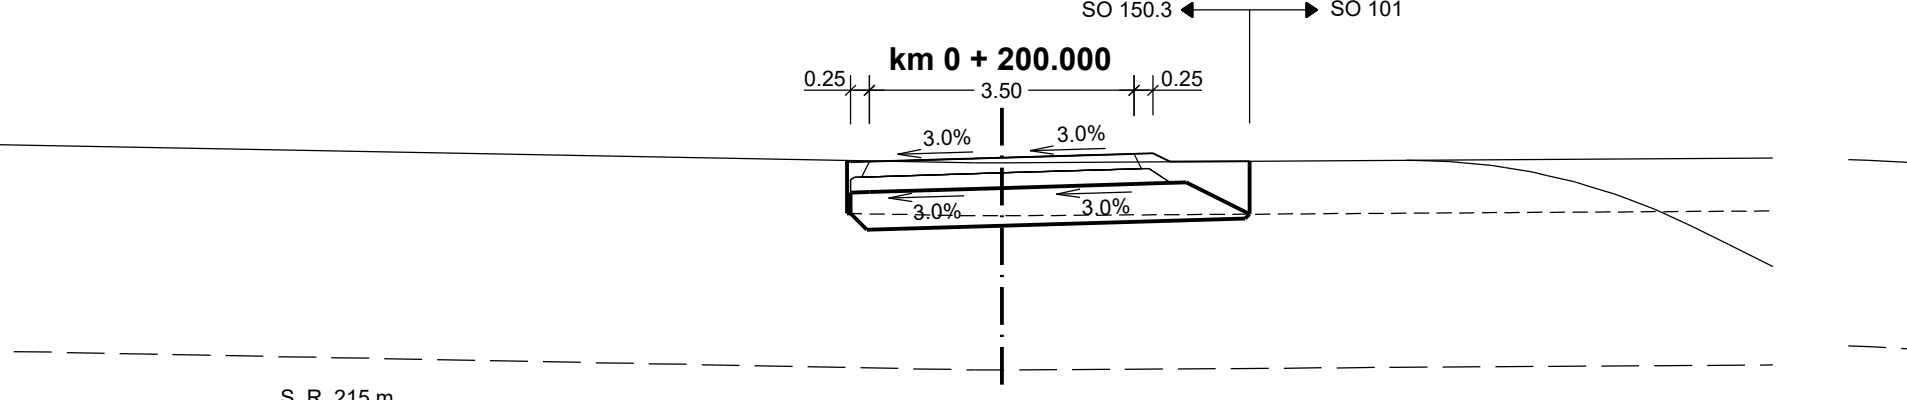


PROJEKTOVANÝ STAV	
ODSAZENÍ OD OSY	
STÁVAJÍCÍ TERÉN	
ODSAZENÍ OD OSY	

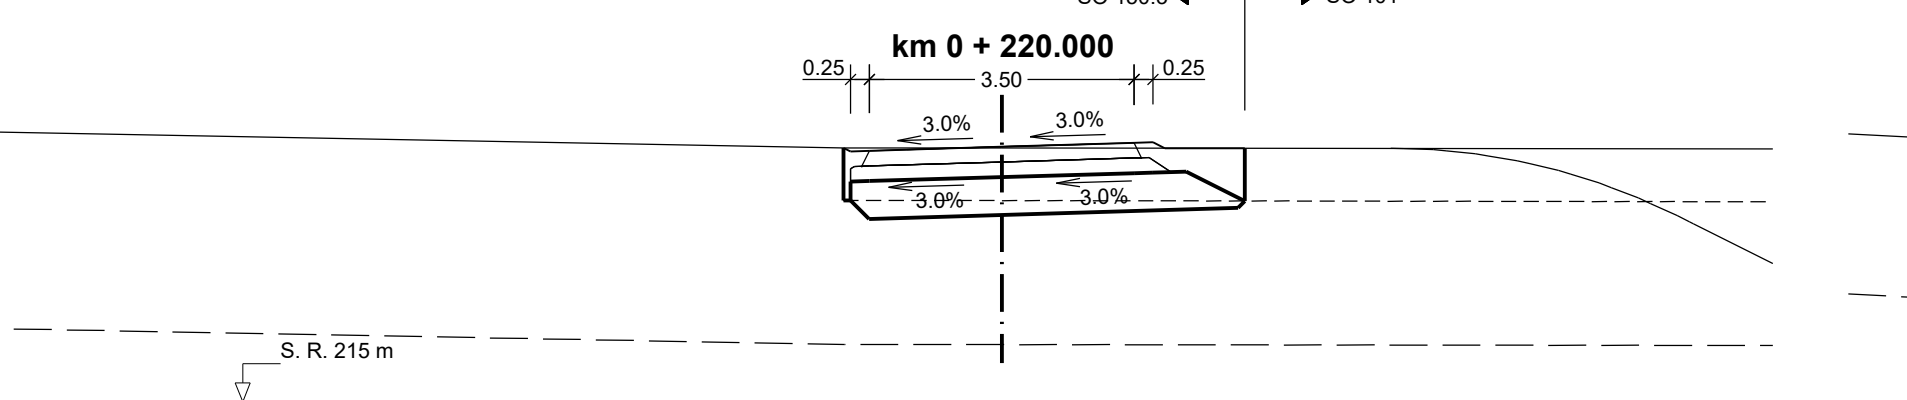


PROJEKTOVANÝ STAV	
ODSAZENÍ OD OSY	
STÁVAJÍCÍ TERÉN	
ODSAZENÍ OD OSY	

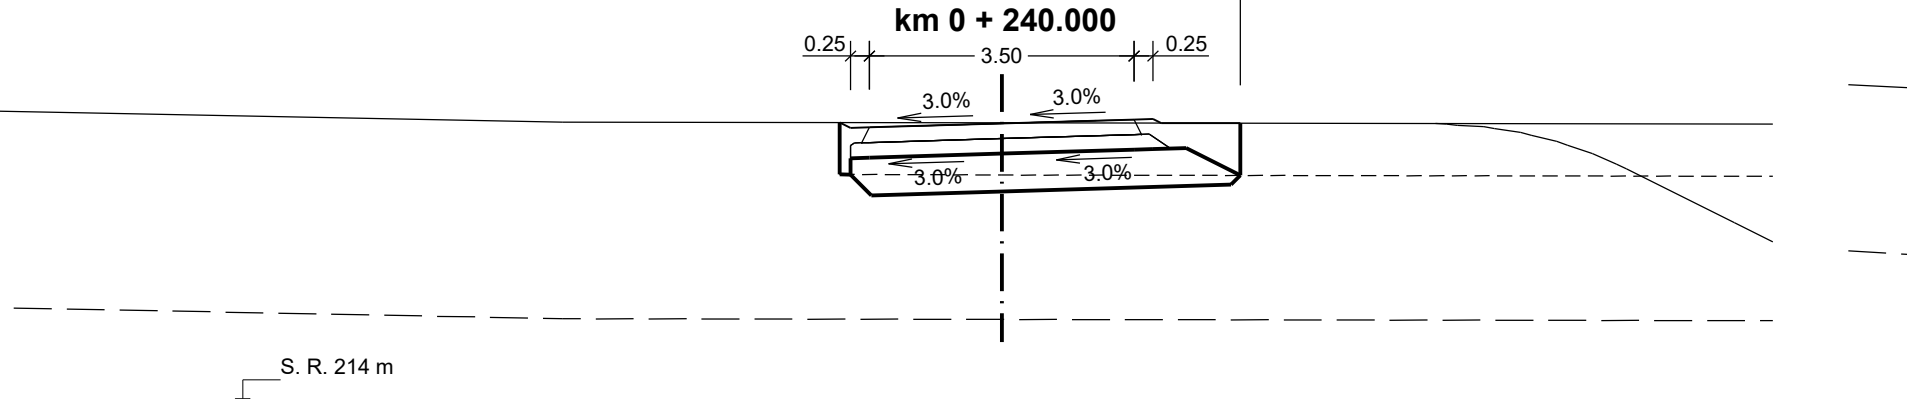


PROJEKTOVANÝ STAV	
ODSAZENÍ OD OSY	
STÁVAJÍCÍ TERÉN	
ODSAZENÍ OD OSY	

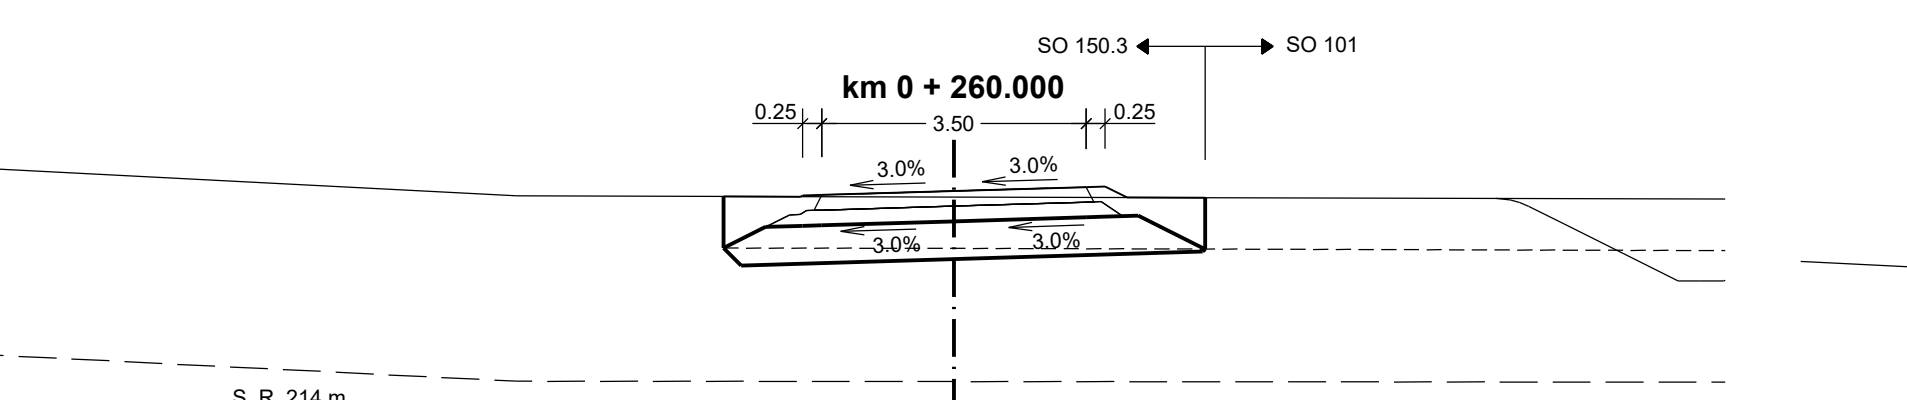


PROJEKTOVANÝ STAV	
ODSAZENÍ OD OSY	
STÁVAJÍCÍ TERÉN	
ODSAZENÍ OD OSY	

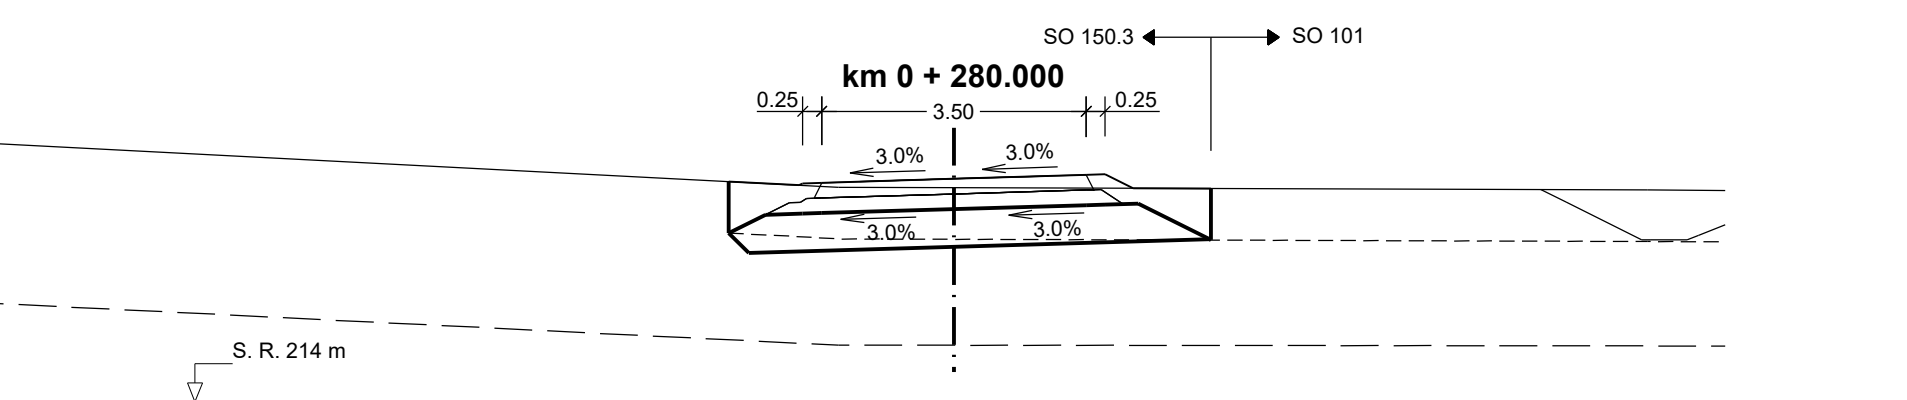

PROJEKTOVANÝ STAV	
ODSAZENÍ OD OSY	
STÁVAJÍCÍ TERÉN	
ODSAZENÍ OD OSY	

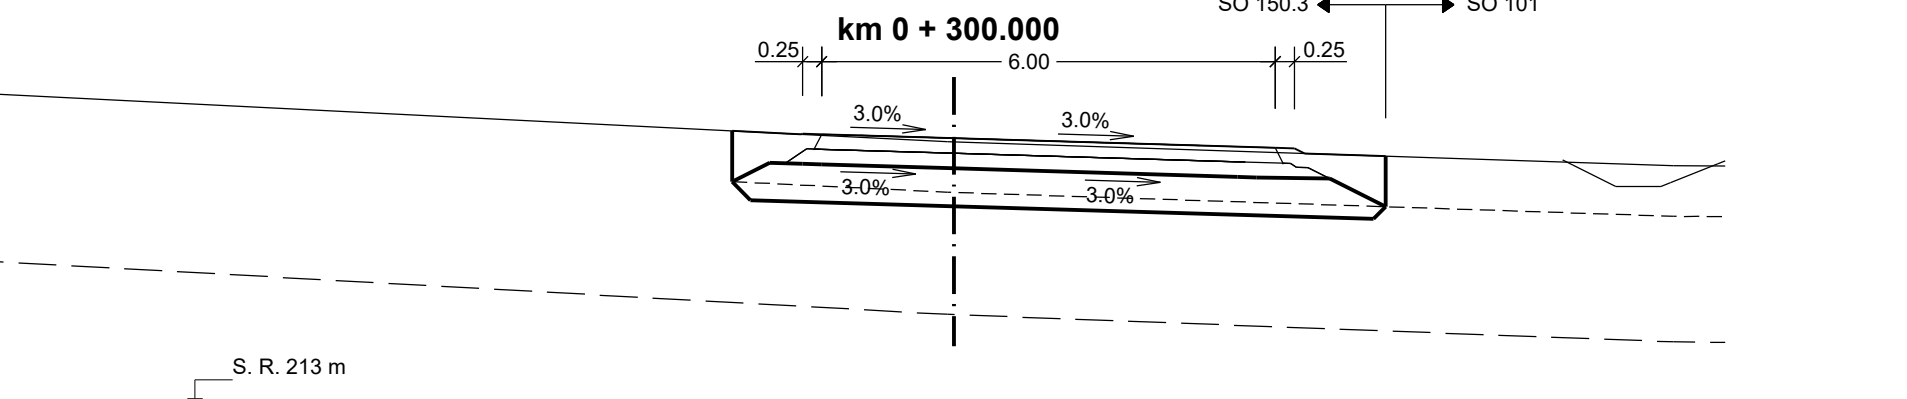

PROJEKTOVANÝ STAV	
ODSAZENÍ OD OSY	
STÁVAJÍCÍ TERÉN	
ODSAZENÍ OD OSY	

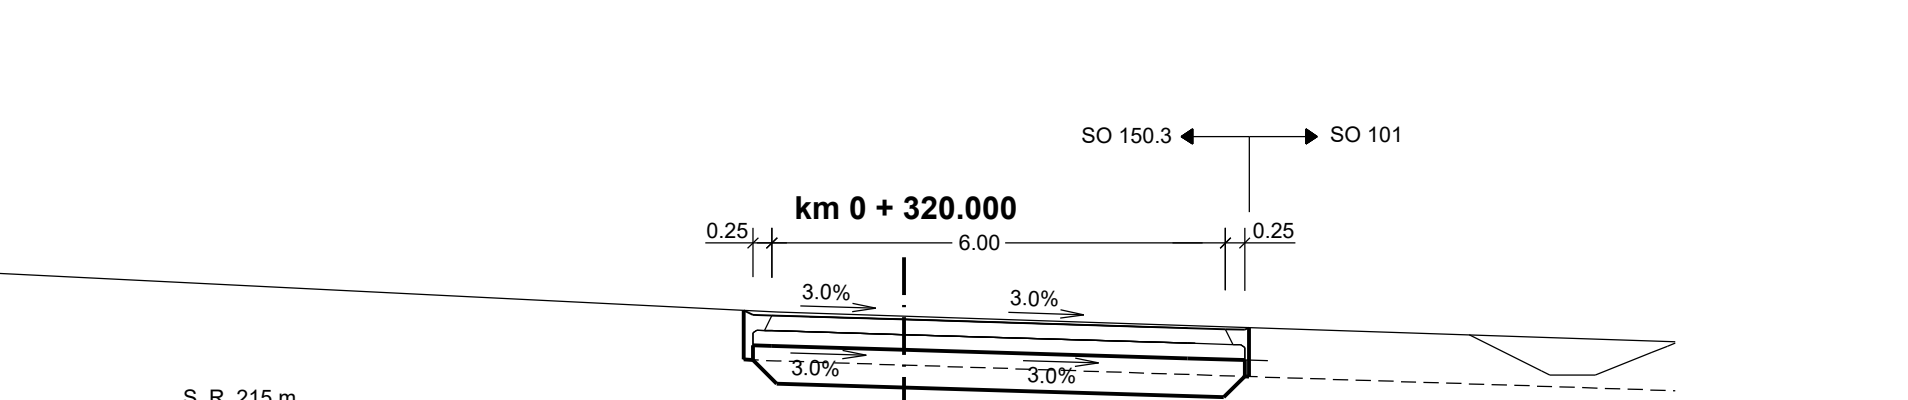

PROJEKTOVANÝ STAV	
ODSAZENÍ OD OSY	
STÁVAJÍCÍ TERÉN	
ODSAZENÍ OD OSY	

Výškový systém: Bpv

SO 150 Přístupy na pozemky k.ú. Kosmonosy

Objednatel: Ředitelství silnic a dálnic
Ředitelství silnic a dálnic s. p.
Čerčanská 2023/12, Krč, 140 00 Praha 4

Zhotovitel: Valbek
Valbek, spol. s r.o.
Vaňurova 505/17
460 07 Liberec 3

Valbek
I/16 MLADÁ BOLESLAV - MARTINOVICE
Zhotovitel: Valbek, spol. s r.o.
Vaňurova 505/17
460 07 Liberec 3
Příloha: PŘÍČNÉ ŘEZY SO 150.3

Zak. číslo: 21-L113-001
Datum: 02/2025
Stupeň: PDP3
Počet formátů: 18 x A4
Měřítko: 1 : 100
Č. přílohy: Paré

5.3