


SO 151 - PŘÍSTUPY NA POZEMKY k.ú. PLAZY
SITUACE - SO 151.1, M 1 : 1 000

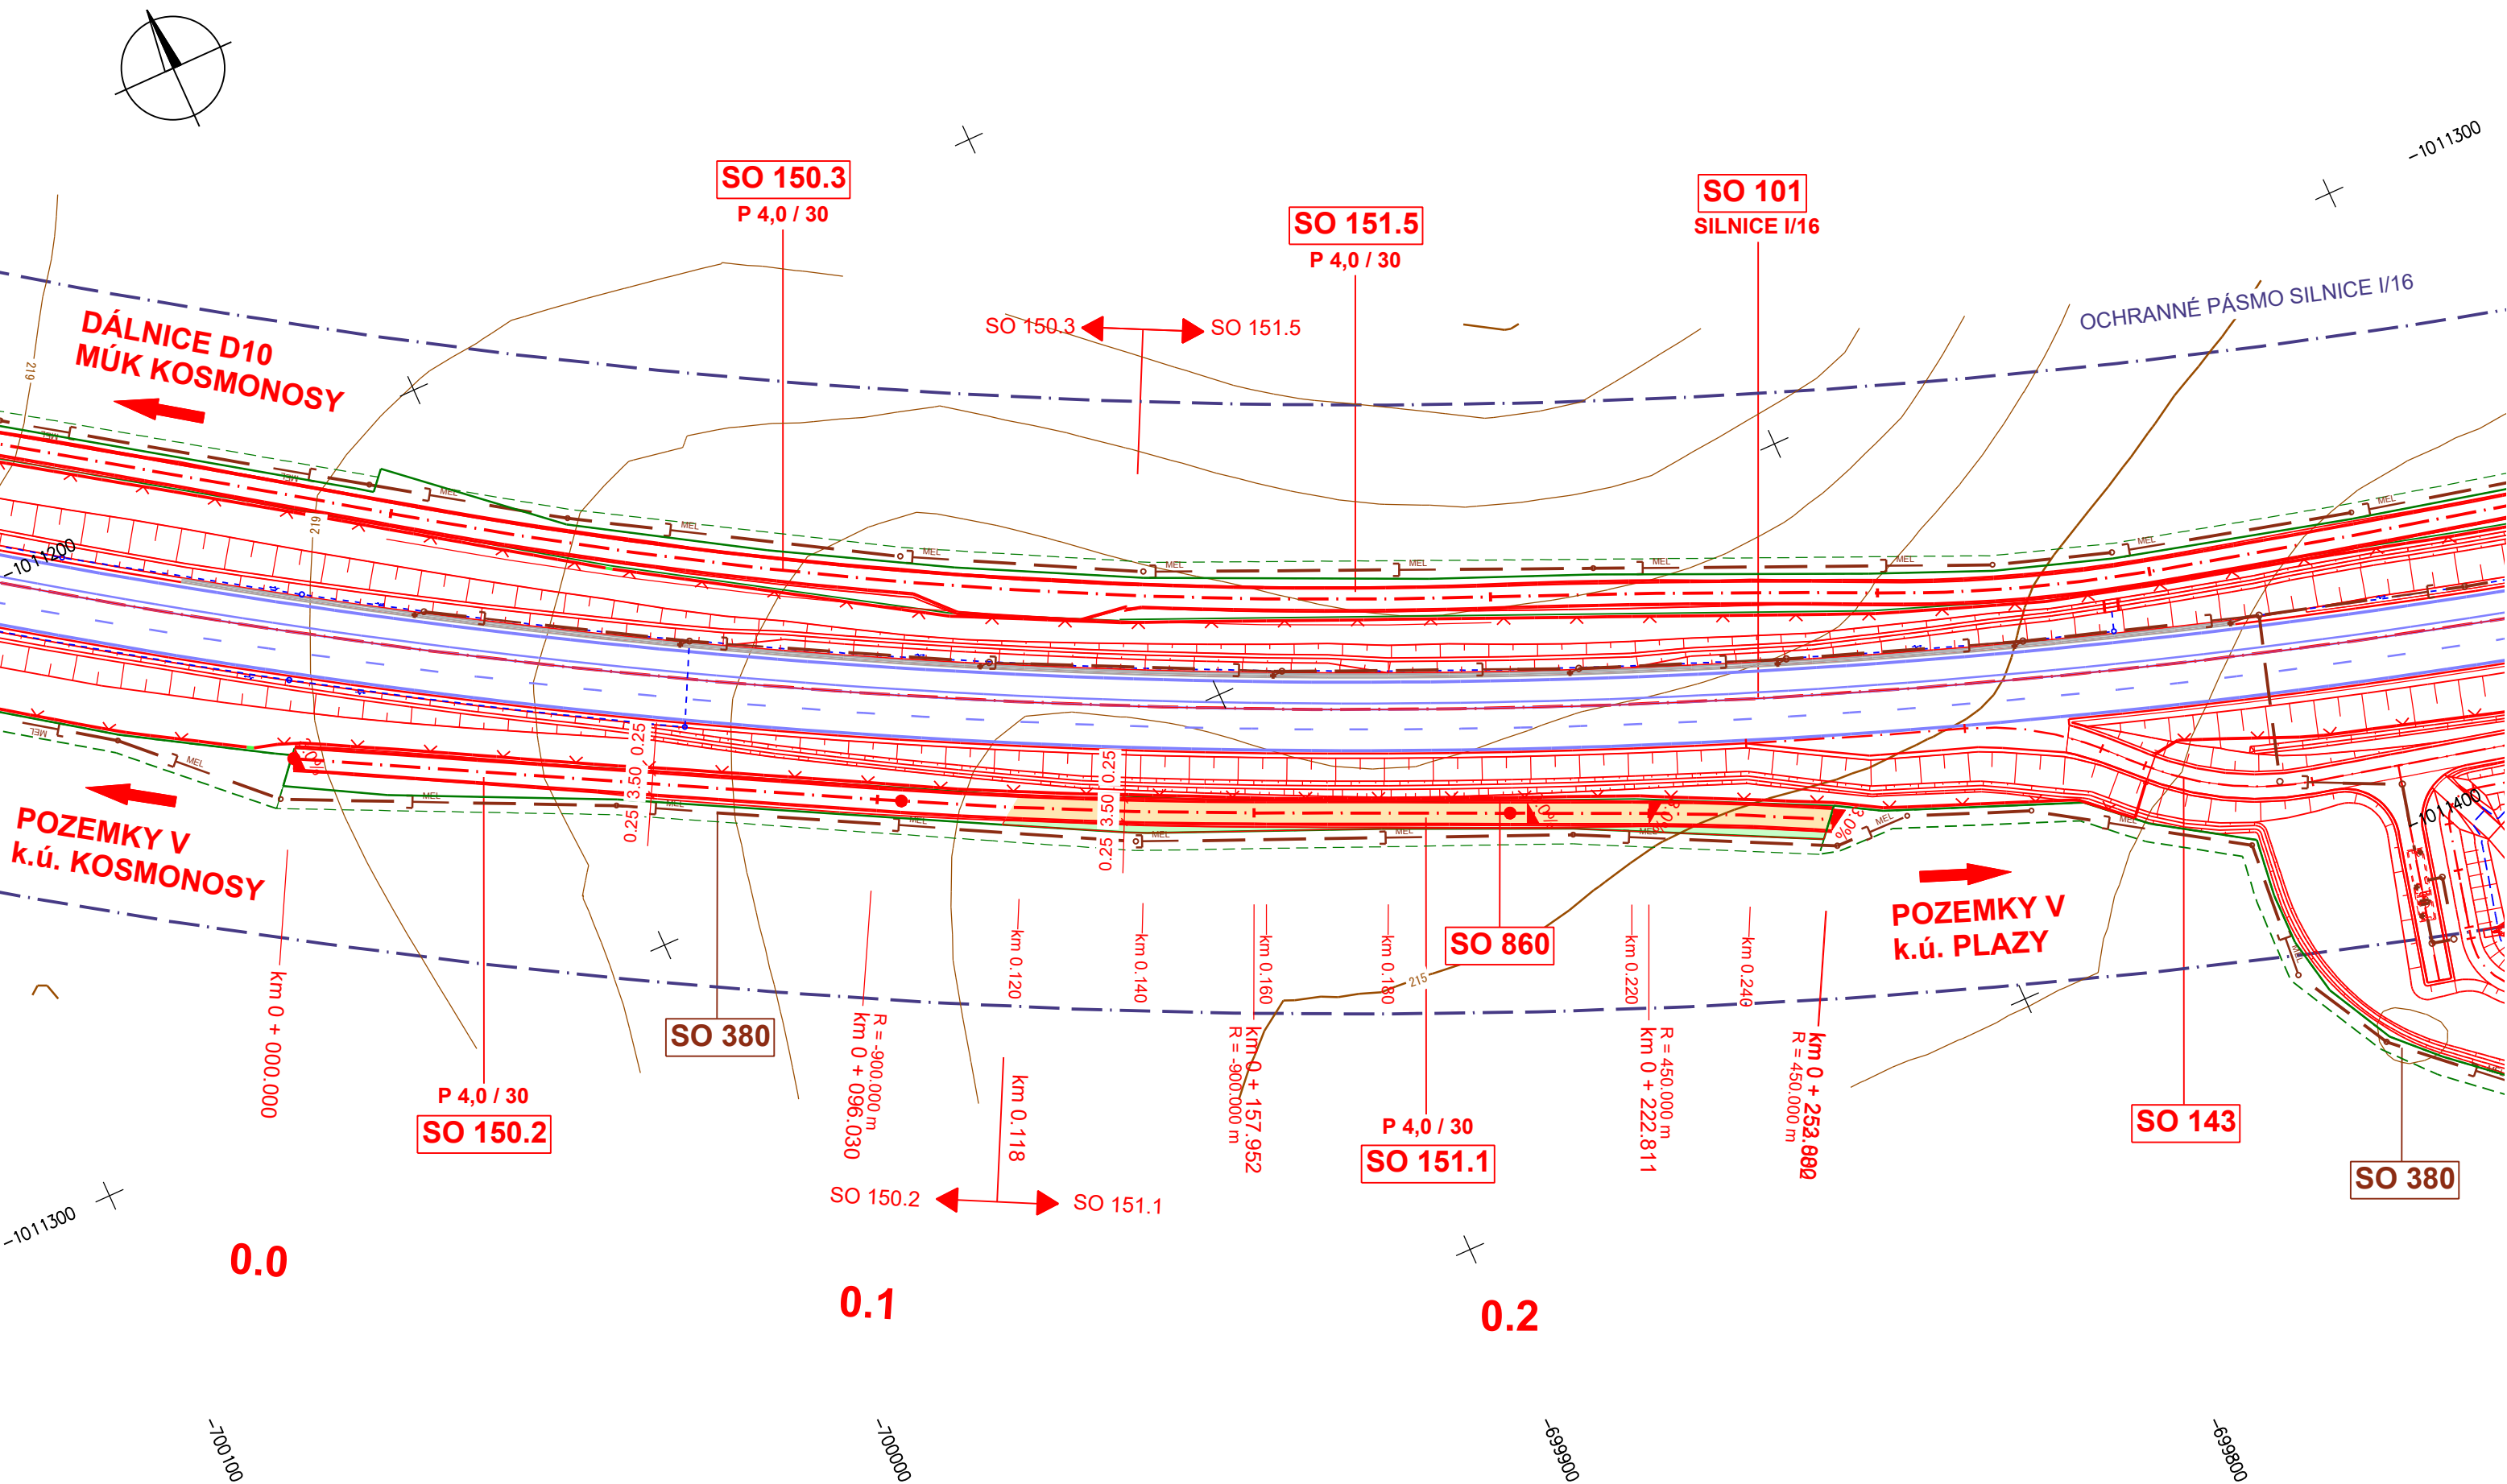

LEGENDA:

PLOCHY

VOZOVKA - ASFALTOVÝ KRYT

VOZOVKA - FRÉZOVANÁ

VOZOVKA - POLNÍ CESTY

CHODNÍK

DLAŽBA VOZOVKY

SVAHY VÝKOPU

SVAHY NÁSYPU

VEGETAČNÍ ÚPRAVY

OBVOD STAVBY

TRVALÝ ZÁBOR

DOČASNÝ ZÁBOR

NOVÉ IS

DEŠŤOVÁ KANALIZACE

MELIORACE

VÝTLAK

VODOVOD

NADZEMNÍ VEDENÍ NN

NADZEMNÍ VEDENÍ VN

PODZEMNÍ VEDENÍ NN

PODZEMNÍ SDĚLOVACÍ VEDENÍ

PLYNOVOD - STL

STÁVAJÍCÍ IS - INFORMATIVNÍ ZÁKRES

PODZEMNÍ VEDENÍ NN

PODZEMNÍ VEDENÍ VN

NADZEMNÍ VEDENÍ NN

NADZEMNÍ VEDENÍ VN

NADZEMNÍ VEDENÍ VVN

DEŠŤOVÁ KANALIZACE

PLYNOVOD - STL

PODZEMNÍ SDĚLOVACÍ VEDENÍ

VODOVOD

Souřadnicový systém: S-JSTK
Výškový systém Bpv

SO 151 Přístupy na pozemky k.ú. Plazy

Objednatel:

**Ředitelství
silnic
a dálnic**

Ředitelství silnic a dálnic s. p.
Čerčanská 2023/12, Krč, 140 00 Praha 4

Zhotovitel:

Valbek, spol. s r.o.
Vaňurova 505/17
460 07 Liberec 3

HIP:

ING. T. KLIMENT

	Vypracoval	ING. A. DUMANSKA		Zak. číslo	21-LI13-001
	Zodp. projektant	ING. T. KLIMENT		Datum	02/2025
	Tech. kontrola	ING. M. HANŽL		Stupeň	PDPS
	Akce I/16 MLADÁ BOLESLAV - MARTINOVICE			Počet formátů	3 x A4
				Měřítko	1 : 1 000
Zhotovitel: Valbek, spol. s r.o. Vaňurova 505/17 460 07 Liberec 3			Č. přílohy	Paré	
			2.1		
Příloha SITUACE SO 151.1					