


SO 151 - PŘÍSTUPY NA POZEMKY k.ú. PLAZY
SITUACE SO 151.2, M 1 : 1000

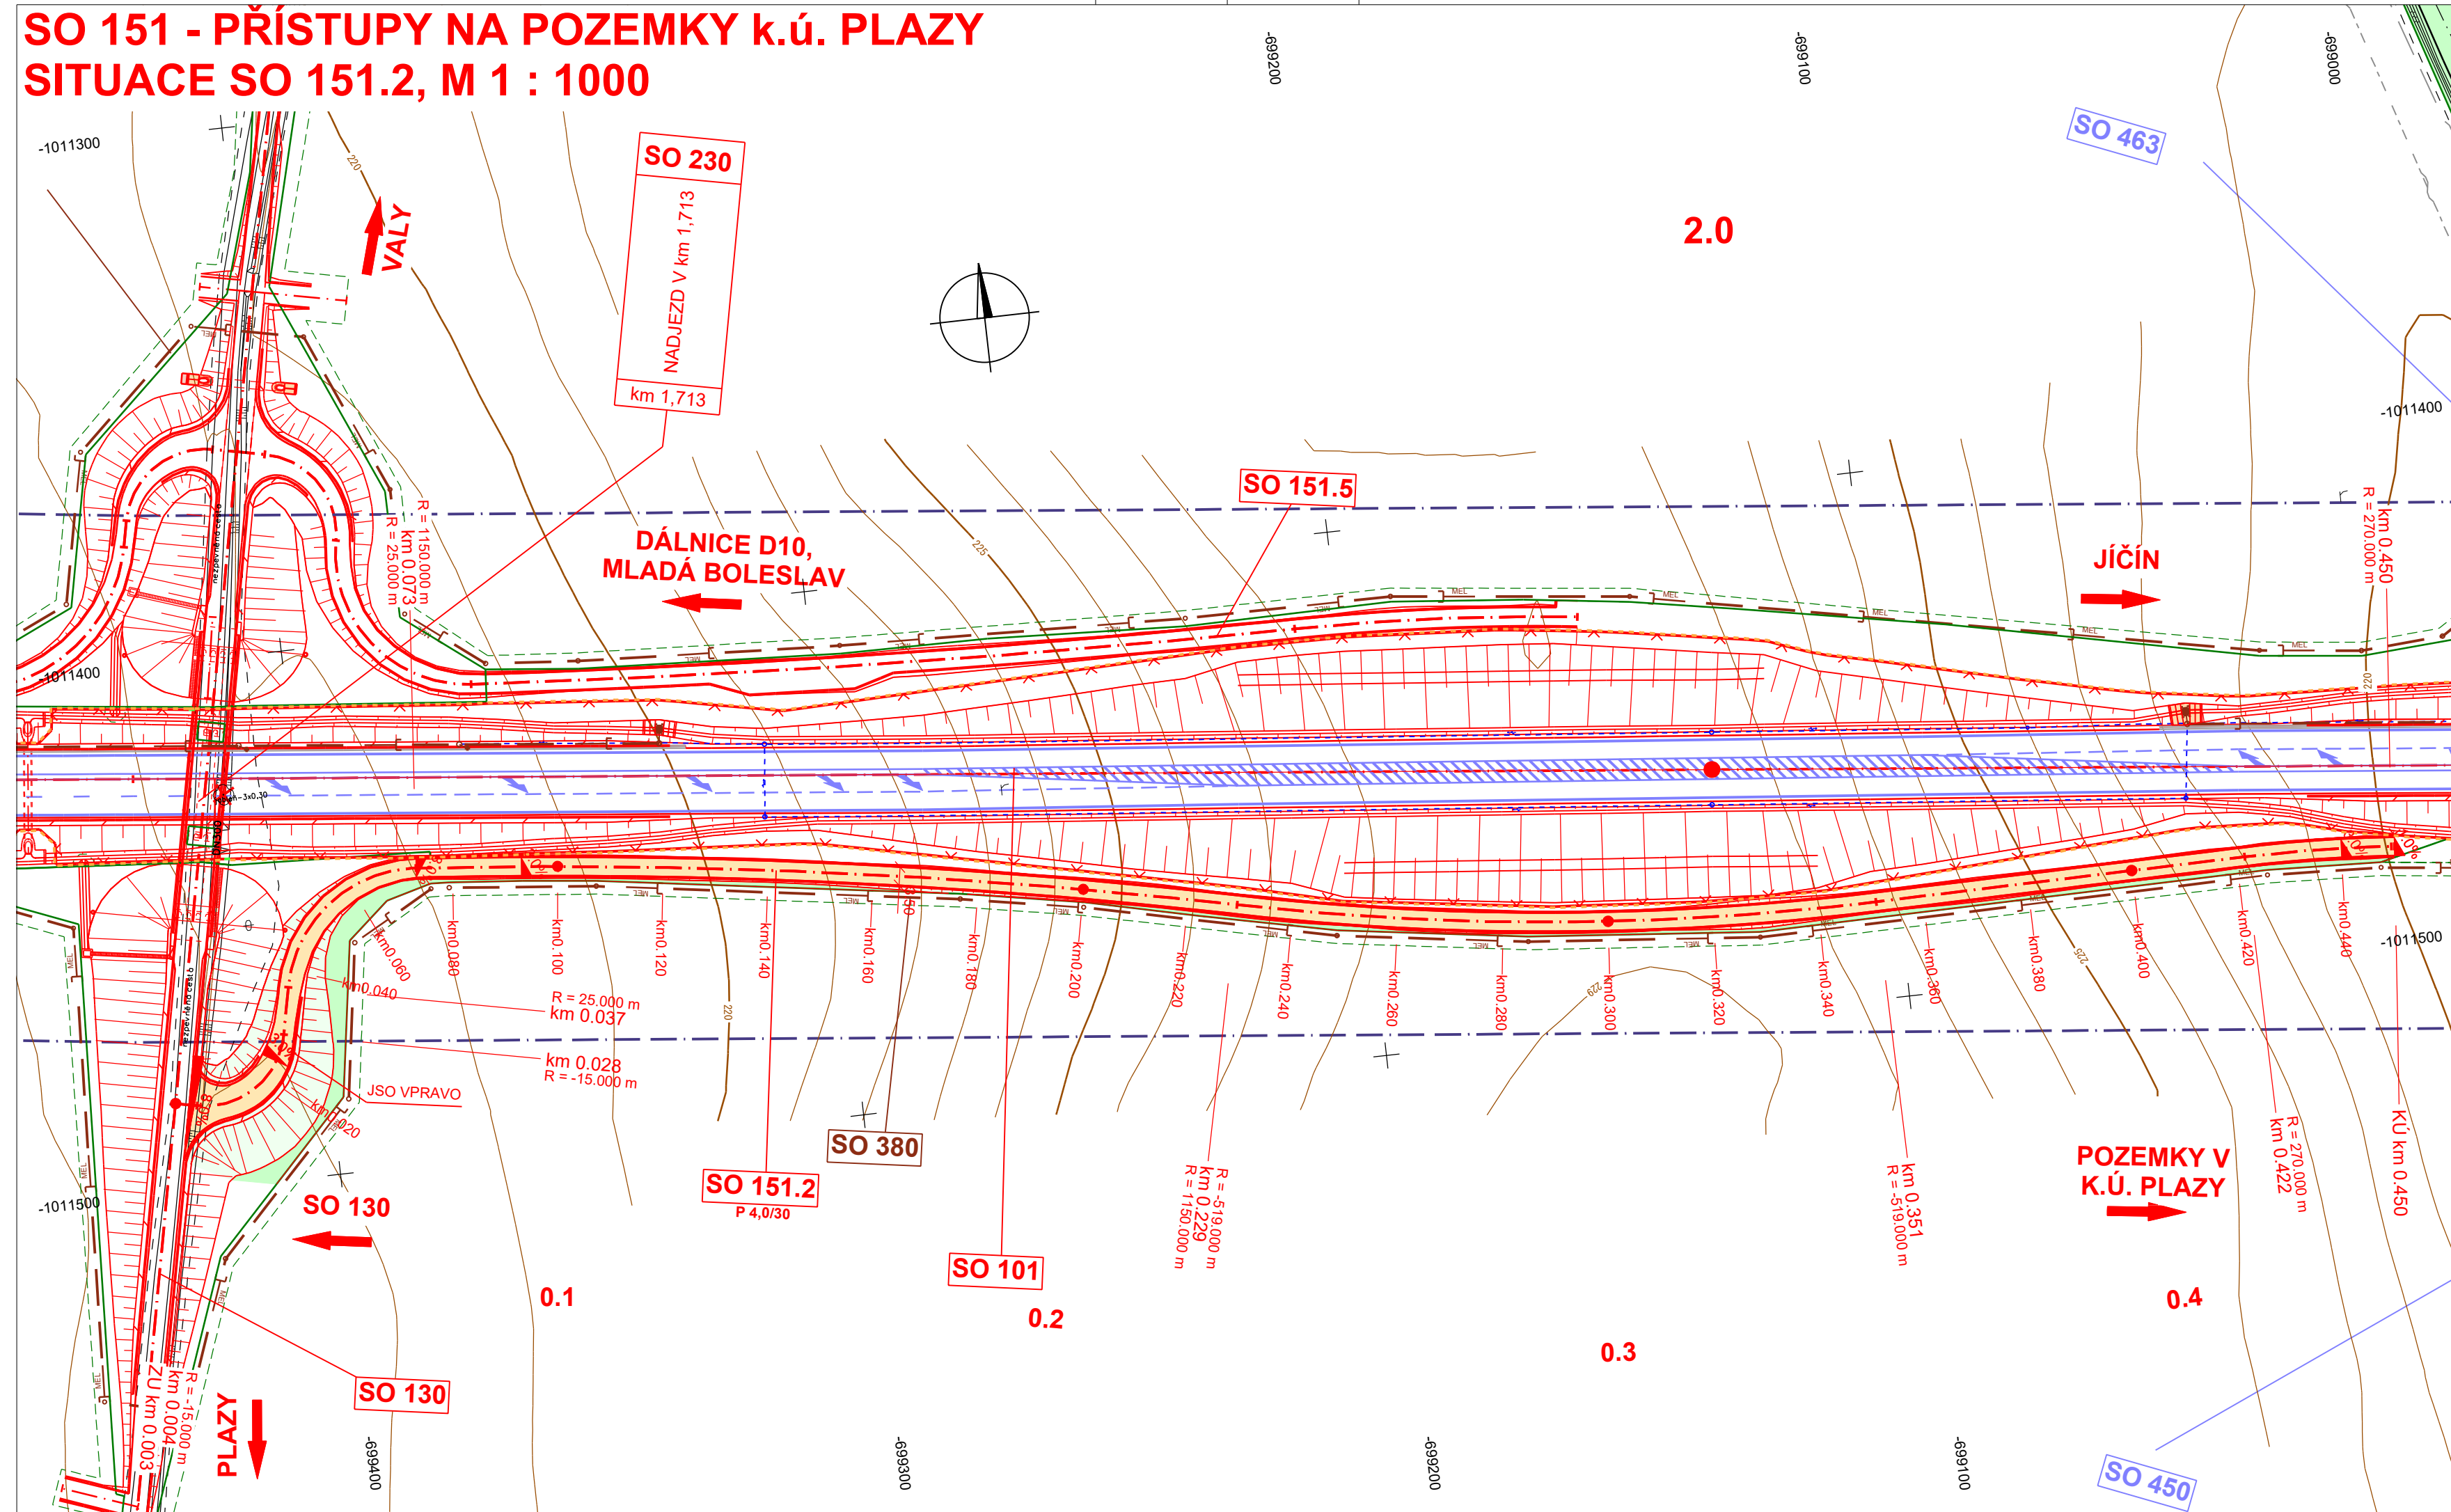

LEGENDA:

PLOCHY

- | | |
|---|-----------------------|
|  | VOZOVKA - POLNÍ CESTY |
|  | SVAHY VÝKOPU |
|  | SVAHY NÁSYPU |
|  | VEGETAČNÍ ÚPRAVY |

KATASTR NEMOVITOSTÍ

- | | |
|---|----------------|
|  | HRANICE K.Ú. |
|  | HRANICE PARCEL |
|  | TRVALÝ ZÁBOR |
|  | DOČASNÝ ZÁBOR |

NOVÉ IS

- | | |
|---|---------------------------|
|  | DEŠŤOVÁ KANALIZACE |
|  | MELIORACE |
|  | VÝTLAK |
|  | VODOVOD |
|  | NADZEMNÍ VEDENÍ NN |
|  | NADZEMNÍ VEDENÍ VN |
|  | PODZEMNÍ VEDENÍ NN |
|  | PODZEMNÍ SĎĚLOVACÍ VEDENÍ |
|  | PLYNOVOD - STL |

STÁVAJÍCÍ IS - INFORMATIVNÍ ZÁKRES

- | | |
|--|---------------------------|
| | PODZEMNÍ VEDENÍ NN |
| | PODZEMNÍ VEDENÍ VN |
| | NADZEMNÍ VEDENÍ NN |
| | NADZEMNÍ VEDENÍ VN |
| | NADZEMNÍ VEDENÍ VVN |
| | DEŠŤOVÁ KANALIZACE |
| | PLYNOVOD - STL |
| | PODZEMNÍ SDĚLOVACÍ VEDENÍ |
| | VODOVOD |

Souřadnicový systém: S-JTSK

Výškový systém: Bpv

SO 151 Přístupy na pozemky k.ú. Plazy

Objednatel:

ŘEDITELSTVÍ SILNIC A DÁLNIC

Ředitelství silnic a dálnic s. p.
Čerčanská 2023/12, Krč, 140 00 Praha 4

Zhotovitel:

**Valbek, spol. s r.o.**

Vaňurova 505/17
460 07 Liberec 3

	Vypracoval Ing. T. Kliment	P. Bartusek		Zak. číslo 02/2025	21-LI13-001
	Zodp. projektant Ing. M. Hanžl	ING. T. KLIMENT		Datum PDPS	02/2025
	Tech. kontrola Akce	ING. M. HANŽL		Stupeň Počet formátů	PDPS 4 x A4
	I/16 MLADÁ BOLESLAV - MARTINOVICE			Měřítko 1 : 1 000	Paré
				Č. přílohy 2.2	
Zhotovitel: Valbek, spol. s r.o. Vafíurova 505/17 460 07 Liberec 3	Příloha SITUACE SO 151.2				