


SO 151 - PŘÍSTUPY NA POZEMKY k.ú. PLAZY
SITUACE - SO 151.3, M 1 : 1 000

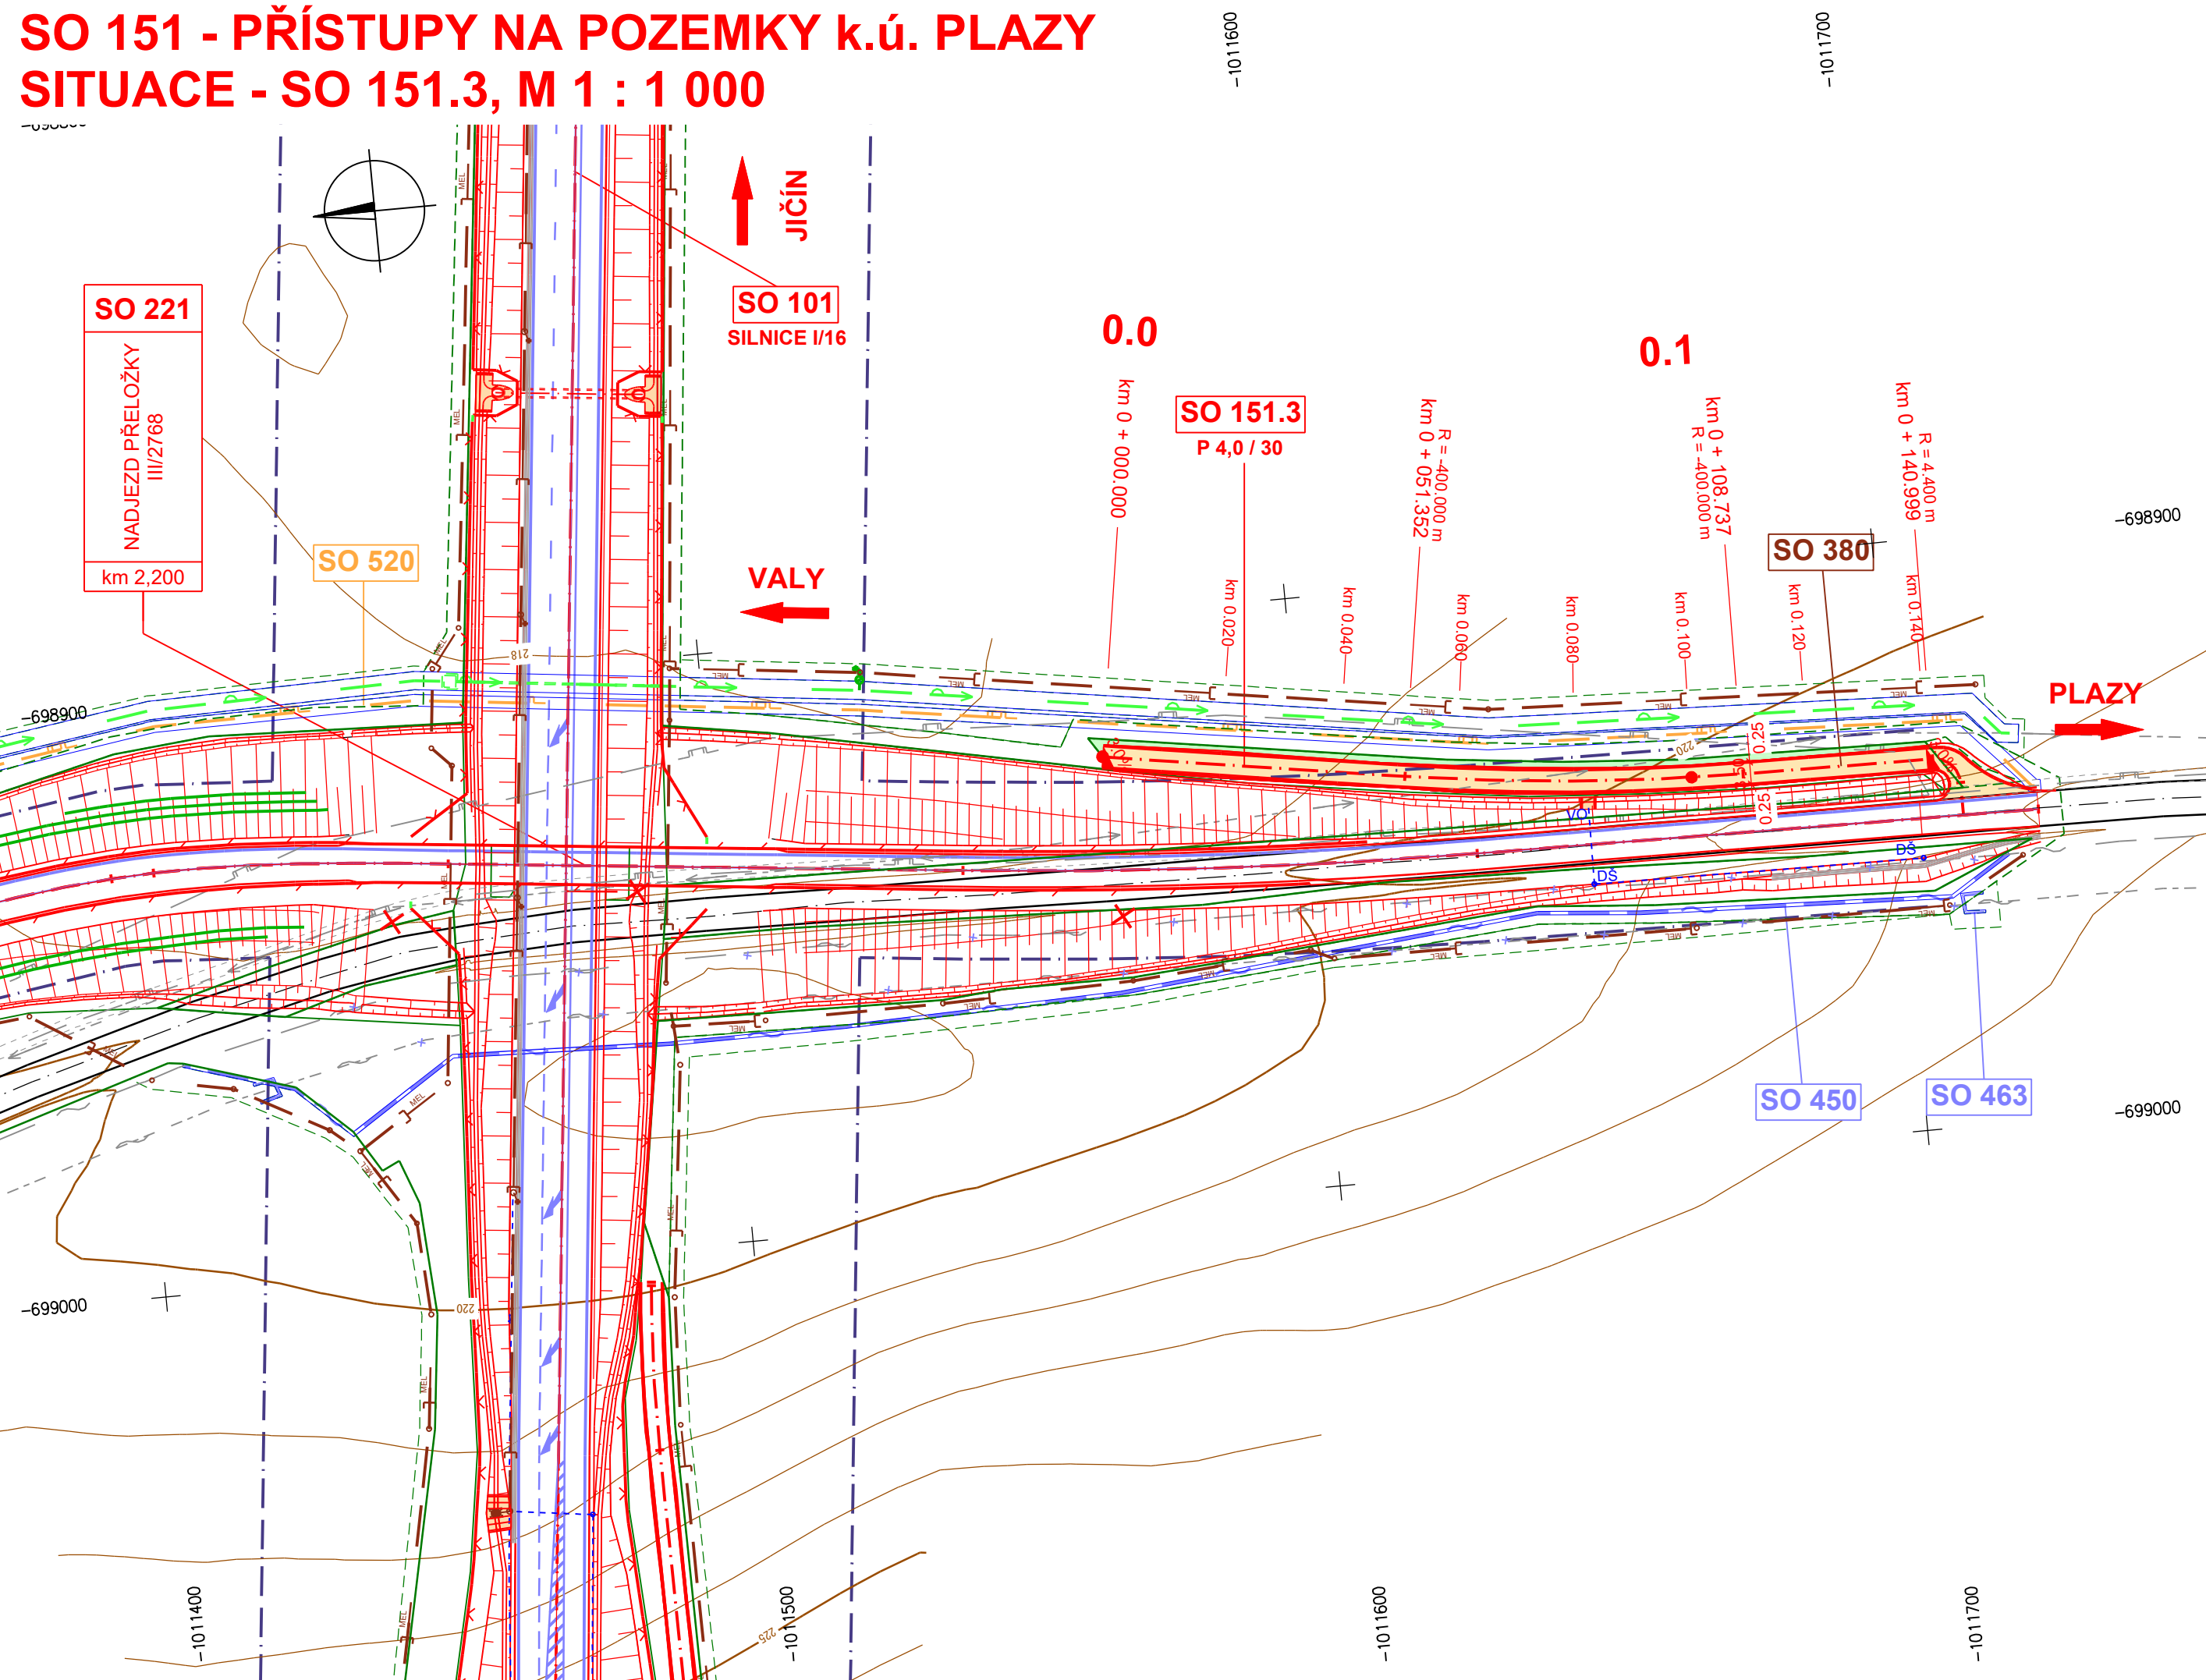

LEGENDA:

PLOCHY

[Pink Box]	VOZOVKA - ASFALTOVÝ KRYT
[Light Pink Box]	VOZOVKA - FRÉZOVANÁ
[Orange Box]	VOZOVKA - POLNÍ CESTY
[Yellow Box]	CHODNÍK
[Light Blue Box]	DLAŽBA VOZOVKY
[Light Orange Box]	SWAHY VÝKOPU
[Light Green Box]	SWAHY NÁSYPU
[Green Box]	VEGETAČNÍ ÚPRAVY

OBVOD STAVBY

[Solid Green Line]	TRVALÝ ZÁBOR
[Dashed Green Line]	DOČASNÝ ZÁBOR

NOVÉ IS

[Brown Line]	DEŠŤOVÁ KANALIZACE
[Brown Line with MEL]	MELIORACE
[Brown Line with Arrow]	VÝTLAK
[Green Line]	VODOVOD
[Dashed Green Line]	NADZEMNÍ VEDENÍ NN
[Dashed Green Line with Arrow]	NADZEMNÍ VEDENÍ VN
[Dashed Green Line with Arrow]	PODZEMNÍ VEDENÍ NN
[Dashed Green Line with Arrow]	PODZEMNÍ SDĚLOVACÍ VEDENÍ
[Orange Line]	PLYNOVOD - STL

STÁVAJÍCÍ IS - INFORMATIVNÍ ZÁKRES

[Dashed Green Line]	PODZEMNÍ VEDENÍ NN
[Dashed Green Line]	PODZEMNÍ VEDENÍ VN
[Dashed Green Line]	NADZEMNÍ VEDENÍ NN
[Dashed Green Line]	NADZEMNÍ VEDENÍ VN
[Dashed Green Line]	NADZEMNÍ VEDENÍ VVN
[Brown Line]	DEŠŤOVÁ KANALIZACE
[Brown Line]	PLYNOVOD - STL
[Dashed Green Line]	PODZEMNÍ SDĚLOVACÍ VEDENÍ
[Green Line]	VODOVOD

Souřadnicový systém: S-JSTK
Výškový systém BpV

SO 151

Přístupy na pozemky k.ú. Plazy

Objednatel:



**ŘEDITELSTVÍ
SILNIC
A DÁLNIC**

Ředitelství silnic a dálnic s. p.
Čerčanská 2023/12, Krč, 140 00 Praha 4

Zhotovitel:



Valbek

Valbek, spol. s r.o.
Vaňurova 505/17
460 07 Liberec 3

HIP:

ING. T. KLIMENT



Valbek

Vypracoval	ING. A. DUMANSKA	Zak. číslo	21-L113-001
Zodp. projektant	ING. T. KLIMENT	Datum	02/2025
Tech. kontrola	ING. M. HANŽL	Stupeň	PDPS
Akce I/16 MLADÁ BOLESLAV - MARTINOVICE		Počet formátů	4 x A4
		Měřítko	1 : 1 000
		Č. přílohy	Paré

Zhotovitel:
Valbek, spol. s r.o.
Vaňurova 505/17
460 07 Liberec 3

Příloha
SITUACE - SO 151.3

2.3