
SO 151 - PŘÍSTUPY NA POZEMKY k.ú. PLAZY
SITUACE - SO 151.4, M 1 : 1 000

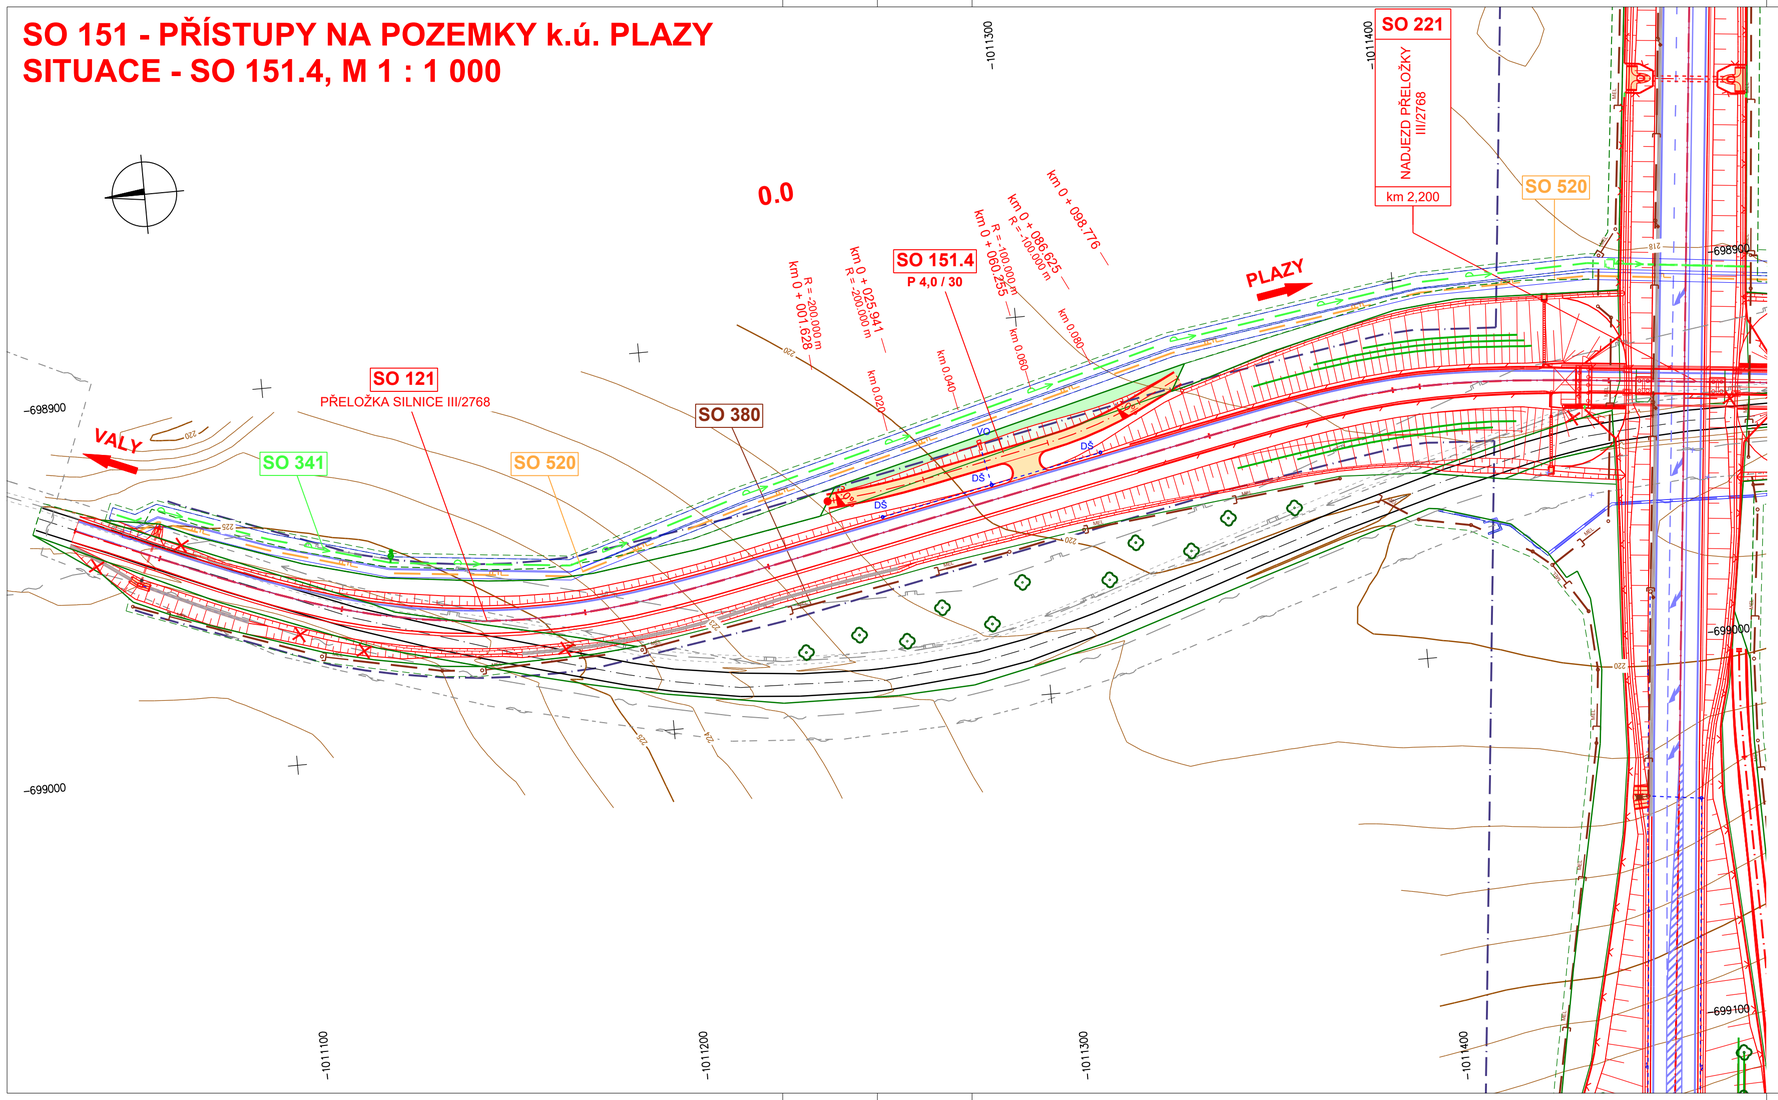

LEGENDA:

PLOCHY

- VOZOVKA - ASFALTOVÝ KRYT
- VOZOVKA - FRÉZOVANÁ
- VOZOVKA - POLNÍ CESTY
- CHODNÍK
- DLAŽBA VOZOVKY
- SVAHY VÝKOPU
- SVAHY NÁSYPU
- VEGETAČNÍ ÚPRAVY

OBVOD STAVBY

- TRVALÝ ZÁBOR
- DOČASNÝ ZÁBOR

NOVÉ IS

- DEŠŤOVÁ KANALIZACE
- MELIORACE
- VÝTLAK
- VODOVOD
- NADZEMNÍ VEDENÍ NN
- NADZEMNÍ VEDENÍ VN
- PODZEMNÍ VEDENÍ NN
- PODZEMNÍ SDĚLOVACÍ VEDENÍ
- PLYNOVOD - STL

STÁVAJÍCÍ IS - INFORMATIVNÍ ZÁKRES

- PODZEMNÍ VEDENÍ NN
- PODZEMNÍ VEDENÍ VN
- NADZEMNÍ VEDENÍ NN
- NADZEMNÍ VEDENÍ VN
- NADZEMNÍ VEDENÍ VVN
- DEŠŤOVÁ KANALIZACE
- PLYNOVOD - STL
- PODZEMNÍ SDĚLOVACÍ VEDENÍ
- VODOVOD

Souřadnicový systém: S-JSTK
Výškový systém Bpv

SO 151 Přístupy na pozemky k.ú. Plazy

Objednatel:

ŘEDITELSTVÍ SILNIC A DÁLNIC

Ředitelství silnic a dálnic s. p.
Čerčanská 2023/12, Krč, 140 00 Praha 4

Zhotovitel:		HIP:
Valbek	**Valbek, spol. s r.o.** Vaňurova 505/17 460 07 Liberec 3	ING. T. KLIMENT

Valbek	**Vypracoval**	ING. A. DUMANSKA		**Zak. číslo**	**21-LI13-001**
	Zodp. projektant	ING. T. KLIMENT		**Datum**	**02/2025**
	Tech. kontrola	ING. M. HANŽL		**Stupeň**	**PDPS**
	Akce	**I/16 MLADÁ BOLESLAV - MARTINOVICE**		**Počet formátů**	**3 x A4**
				Měřítko	**1 : 1 000**
				Č. přílohy	**Paré**
Zhotovitel: Valbek, spol. s r.o. Vaňurova 505/17 460 07 Liberec 3	**Příloha**	SITUACE SO 151.4			**2.4**