


SO 151 - PŘÍSTUPY NA POZEMKY k.ú. PLAZY
SITUACE SO 151.5, M 1 : 1000

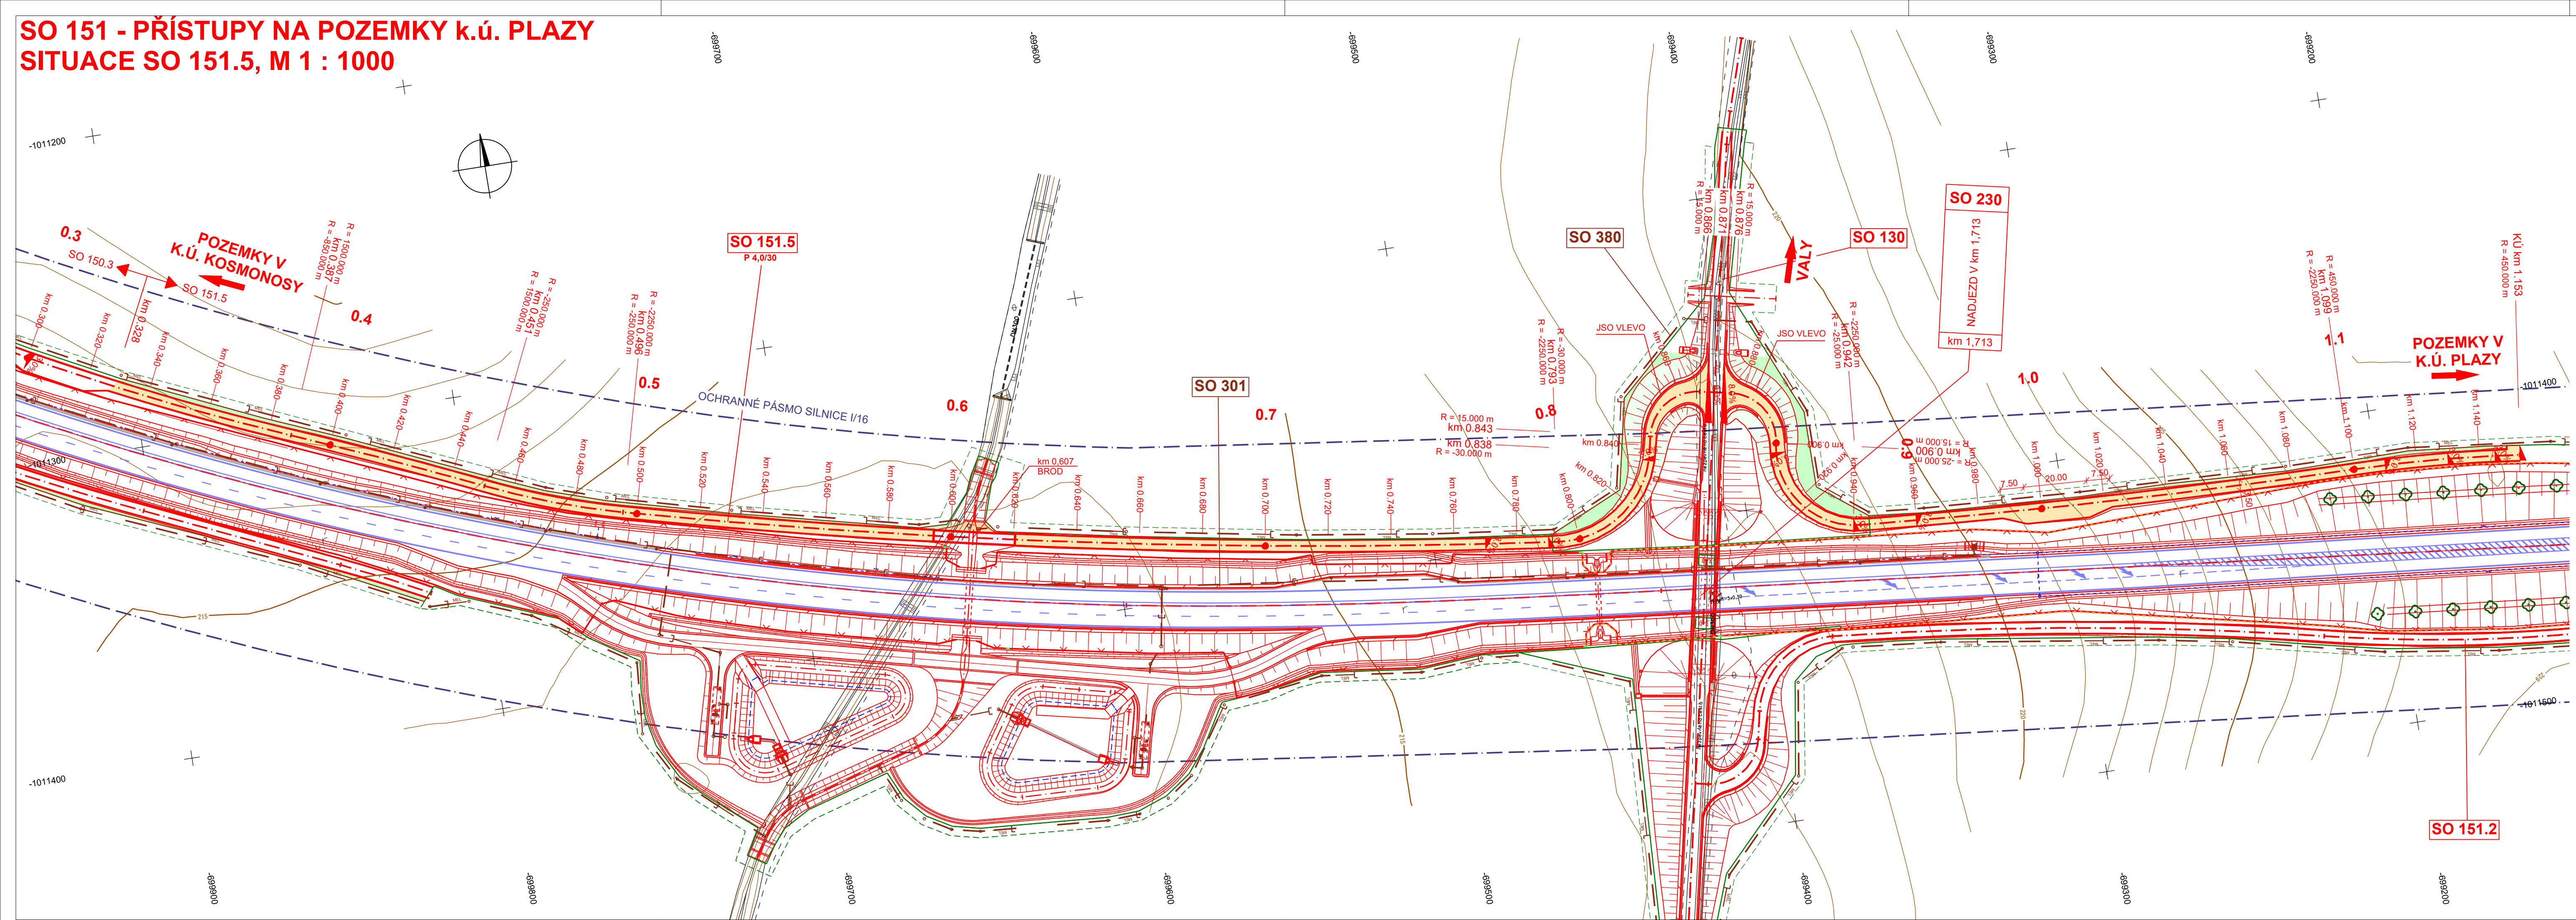

LEGENDA:

PLOCHY

- VOZOVKA - POLNÍ CESTY
- SVAHY VÝKOPU
- SVAHY NÁSYPU
- VEGETAČNÍ ÚPRAVY

KATASTR NEMOVITOSTÍ

- HRANICE K.Ú.
- HRANICE PARCEL
- TRVALÝ ZÁBOR
- DOČASNÝ ZÁBOR

NOVÉ IS

- DEŠŤOVÁ KANALIZACE
- MELIORACE
- VÝTLAK
- VODOVOD
- NADZEMNÍ VEDENÍ NN
- NADZEMNÍ VEDENÍ VN
- PODZEMNÍ VEDENÍ NN
- PODZEMNÍ SDĚLOVACÍ VEDENÍ
- PLYNOVOD - STL

STÁVAJÍCÍ IS - INFORMATIVNÍ ZÁKRES

- PODZEMNÍ VEDENÍ NN
- PODZEMNÍ VEDENÍ VN
- NADZEMNÍ VEDENÍ NN
- NADZEMNÍ VEDENÍ VN
- NADZEMNÍ VEDENÍ VVN
- DEŠŤOVÁ KANALIZACE
- PLYNOVOD - STL
- PODZEMNÍ SDĚLOVACÍ VEDENÍ
- VODOVOD

Souřadnicový systém: S-JTSK
Výškový systém: Bpv

SO 151 Přístupy na pozemky k.ú.Plazy

Objednatel:

**ŘEDITELSTVÍ
SILNIC
A DÁLNIC**

Ředitelství silnic a dálnic s. p.
Čerčanská 2023/12, Krč, 140 00 Praha 4

Zhotovitel:

Valbek

Valbek, spol. s r.o.
Vaňurova 505/17
460 07 Liberec 3

Valbek

Vypracoval	P. BARTUSEK	Zak. číslo	21-LI13-001
Zodp. projektant	ING. T. KLIMENT	Datum	02/2025
Tech. kontrola	ING. M. HANŽL	Stupeň	PDPS
Akce	I/16 MLADÁ BOLESLAV - MARTINOVICE	Počet formátů	5 x A4
		Měřítko	1 : 1 000
		Č. přílohy	Paré

Zhotovitel:
Valbek, spol. s r.o.
Vaňurova 505/17
460 07 Liberec 3

Příloha

SITUACE SO 151.5

2.5