SO 151 - PŘÍSTUP NA POZEMKY k.ú. PLAZY
PODÉLNÝ PROFIL SO 151.3, M 1 : 1 000 / 100

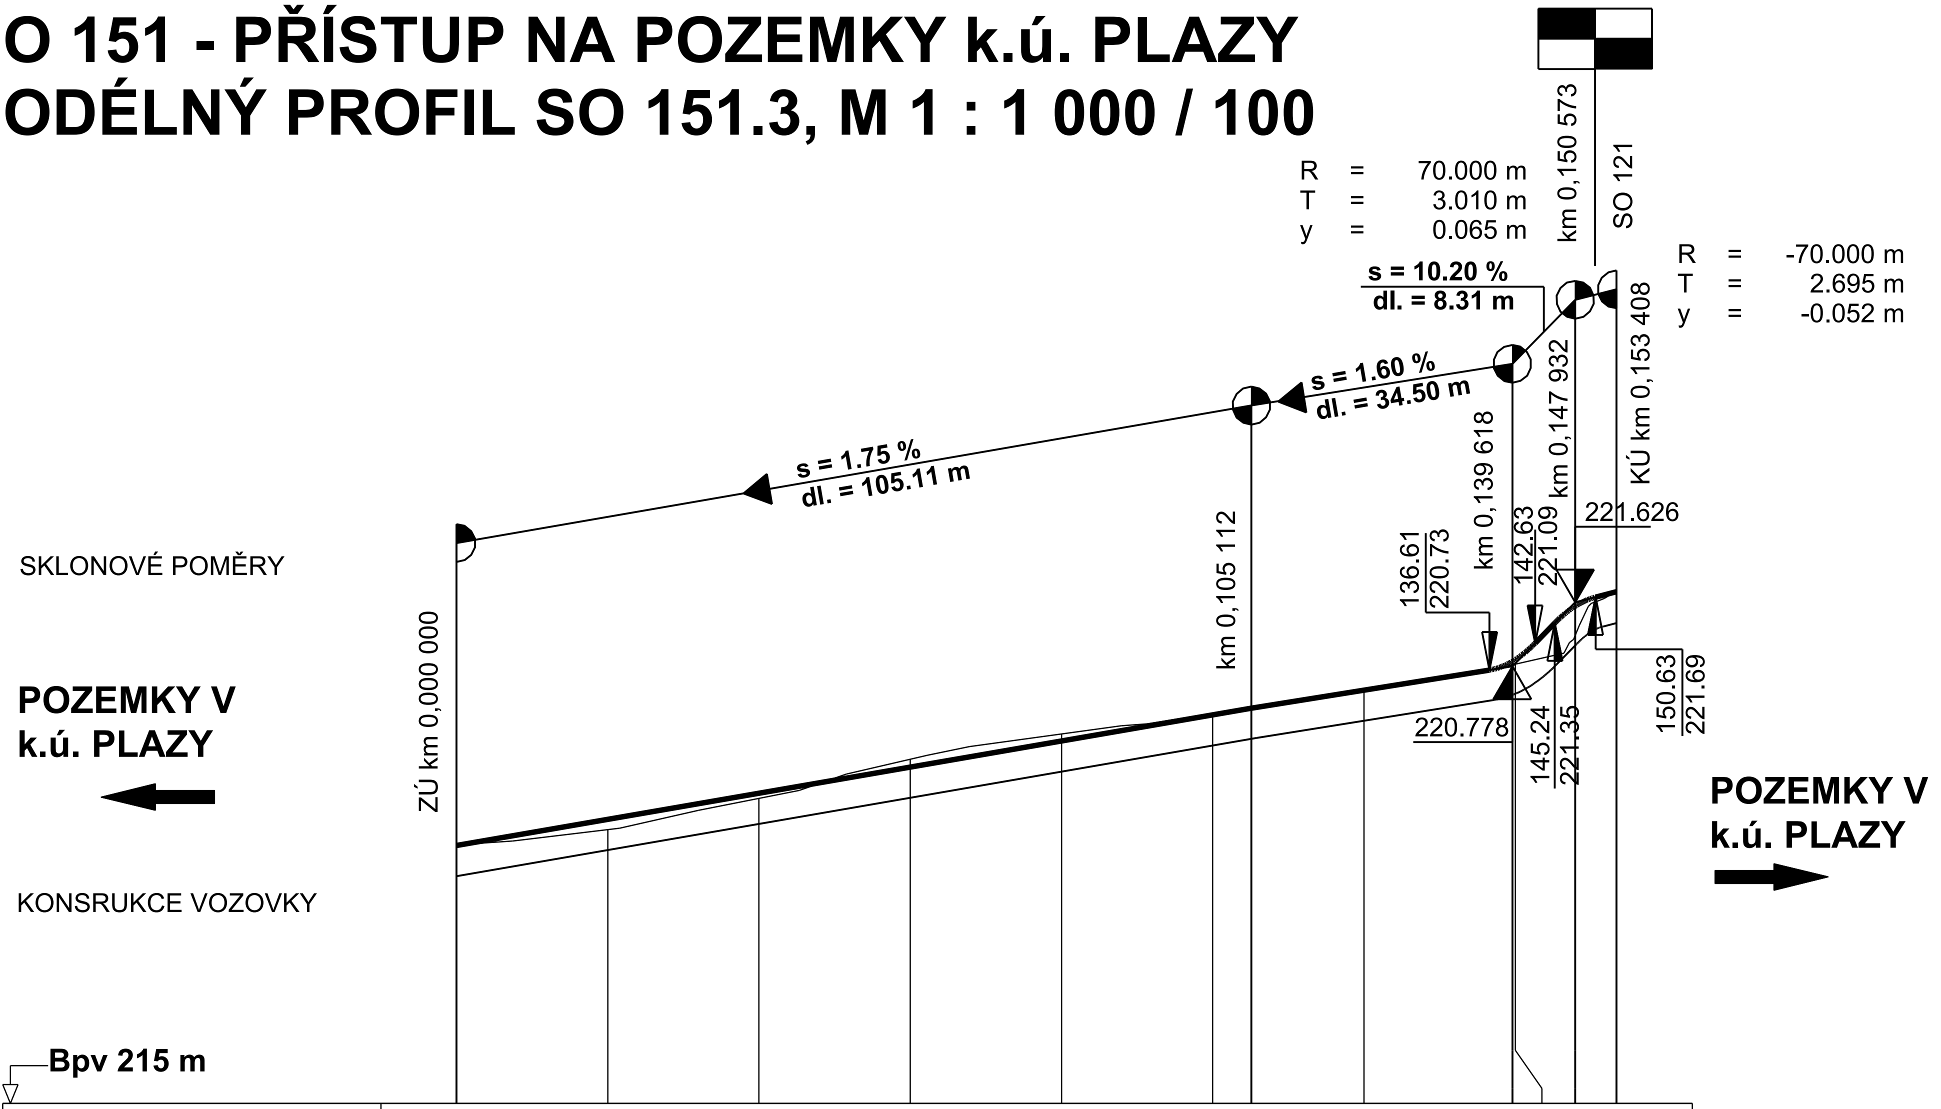
R = 70.000 m
T = 3.010 m
y = 0.065 m
km 0,150 573
SO 121
R = -70.000 m
T = 2.695 m
y = -0.052 m
s = 10.20 %
dl. = 8.31 m
s = 1.60 %
dl. = 34.50 m
s = 1.75 %
dl. = 105.11 m
SKLONOVÉ POMĚRY
POZEMKY V k.ú. PLAZY
KONSRUKCE VOZOVKY
ZÚ km 0,000 000
km 0,105 112
136.61
220.73
km 0,139 618
142.63
221.09
km 0,147 932
KÚ km 0,153 408
221.626
220.778
145.24
221.35
150.63
221.69
POZEMKY V k.ú. PLAZY
Bpv 215 m

KÓTY NIVELETY	218.41	218.75	219.10	219.45	219.79	220.14	220.23	220.46	220.84	220.87	221.57	221.76
KÓTY TERÉNU	218.42	218.62	219.03	219.55	219.88	220.16		220.46	220.80	220.81	221.19	
STANIČENÍ	0.00	20.00	40.00	60.00	80.00	100.00	105.11	120.00	139.62	140.00	147.93	153.41

km **0+000** **0+100**

VPRAVO
SMĚROVÉ POMĚRY
MĚŘÍTKO 4/R (cm)
VLEVO

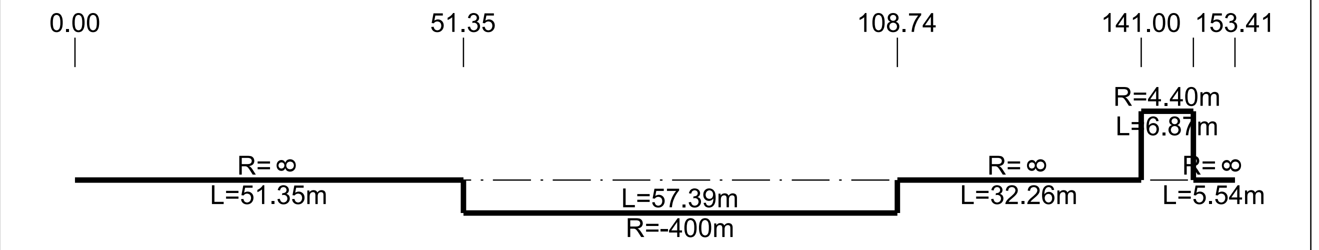
0.00
51.35
108.74
141.00
153.41
R=∞
L=51.35m
L=57.39m
R=-400m
R=∞
L=32.26m
R=4.40m
L=6.87m
R=∞
L=5.54m

KLOPENÍ
MĚŘÍTKO 1 : 20
– – – LEVÁ HRANA
——— PRAVÁ HRANA

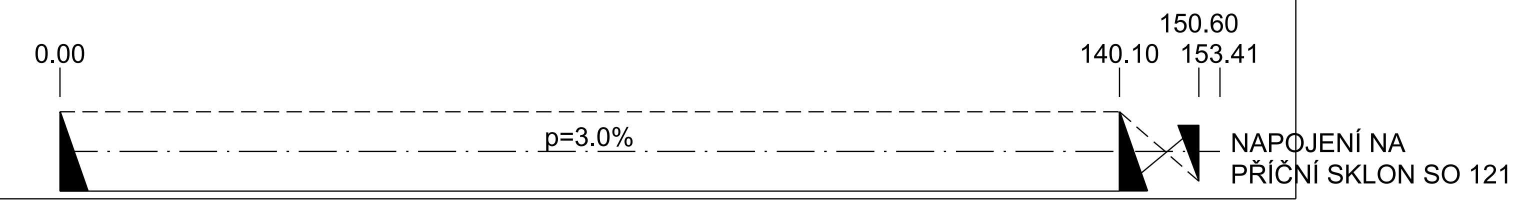
0.00
140.10
150.60
153.41
p=3.0%
NAPOJENÍ NA PŘÍČNÍ SKLON SO 121

Výškový systém Bpv

SO 151 Přístupy na pozemky k.ú. Plazy

Objednatel:

Ředitelství silnic a dálnic s. p.
Čerčanská 2023/12, Krč, 140 00 Praha 4

Zhotovitel:

Valbek, spol. s r.o.
Vaňurova 505/17
460 07 Liberec 3

HIP: ING. T. KLIMENT

Vypracoval	ING. A. DUMANSKA		**Zak. číslo**	**21-LI13-001**
Zodp. projektant	ING. T. KLIMENT		**Datum**	**02/2025**
Tech. kontrola	ING. M. HANŽL		**Stupeň**	**PDPS**
Akce			**Počet formátů**	**3 x A4**
I/16 MLADÁ BOLESLAV - MARTINOVICE			**Měřítko**	**1 : 1000/100**
			Č. přílohy	**Paré**
Příloha PODÉLNÝ PROFIL SO 151.3			**3.3**	

Zhotovitel:
Valbek, spol. s r.o.
Vaňurova 505/17
460 07 Liberec 3