
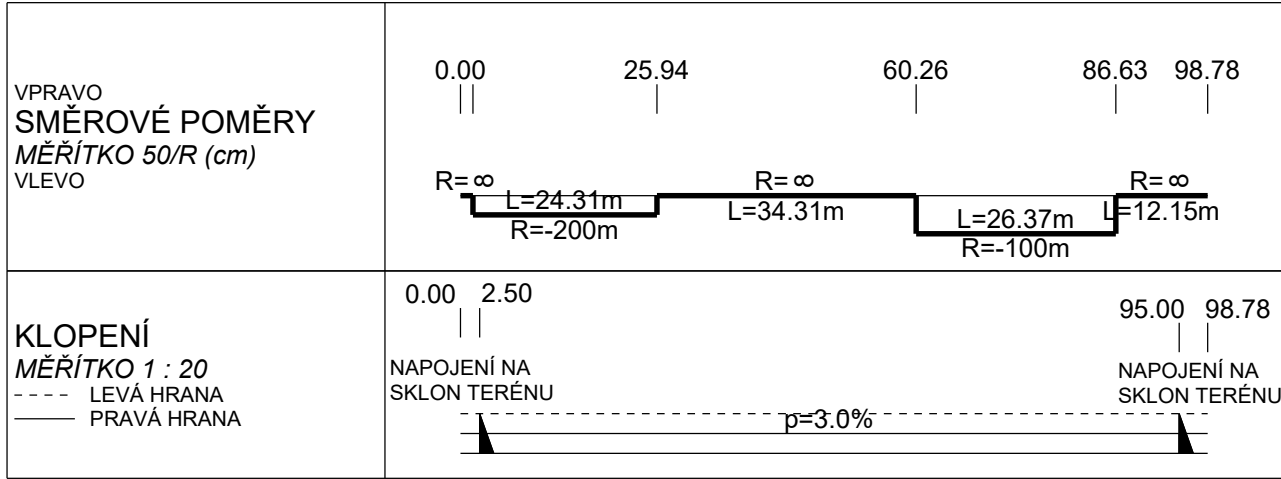


SO 151 - PŘÍSTUP NA POZEMKY k.ú. PLAZY
PODÉLNÝ PROFIL SO 151.4, M 1 : 1 000 / 100

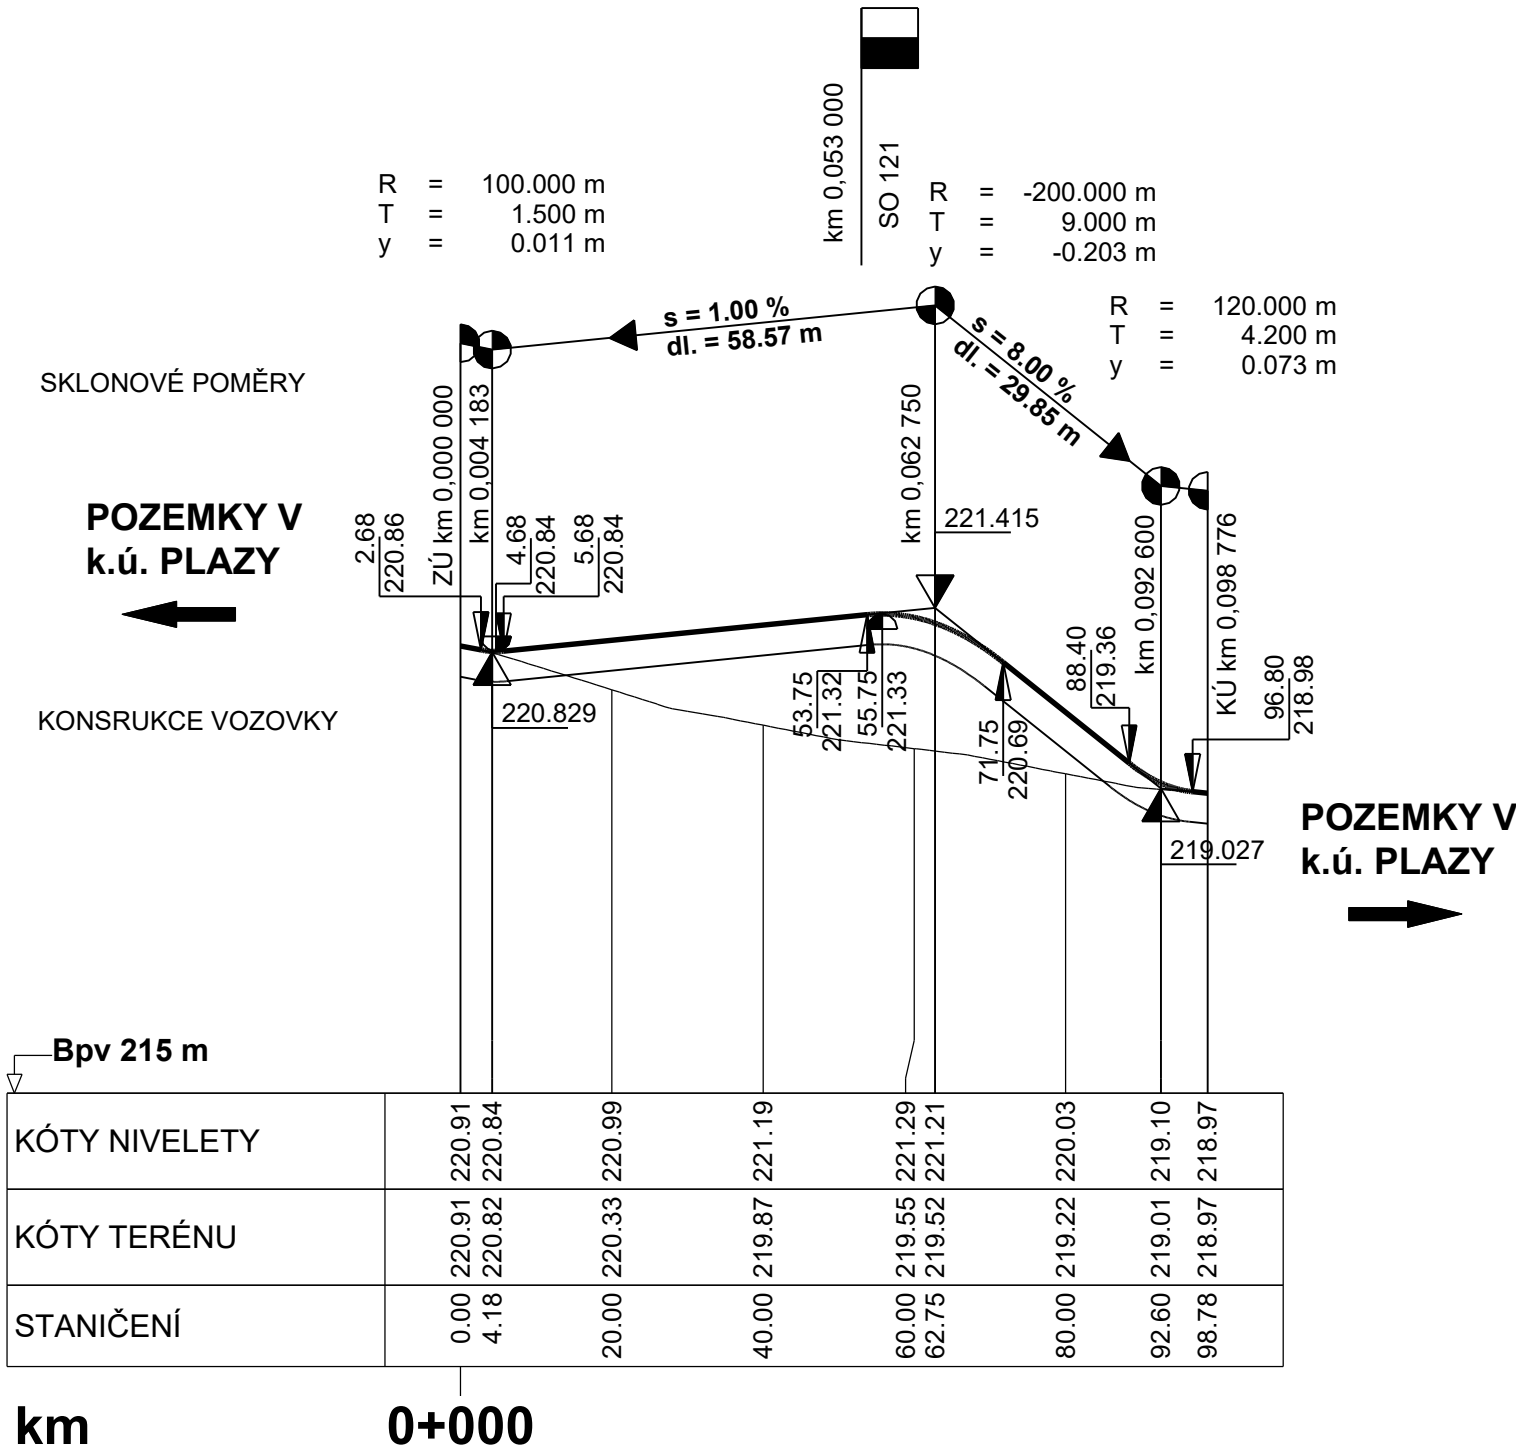

Výškový systém Bpv

SO 151 Přístupy na pozemky k.ú. Plazy

Objednatel:

 **ŘEDITELSTVÍ SILNIC A DÁLNIC**

Ředitelství silnic a dálnic s. p.
Čerčanská 2023/12, Krč, 140 00 Praha 4

Zhotovitel:

 **Valbek, spol. s r.o.**
Vaňurova 505/17
460 07 Liberec 3

HIP:

ING. T. KLIMENT

 **Valbek**

Vypracoval	ING. A. DUMANSKA	Zak. číslo	21-LI13-001
Zodp. projektant	ING. T. KLIMENT	Datum	02/2025
Tech. kontrola	ING. M. HANŽL	Stupeň	PDPS
Akce I/16 MLADÁ BOLESLAV - MARTINOVICE		Počet formátů	3 x A4
		Měřítko	1 : 1000/100
		Č. přílohy	Paré
Zhotovitel: Valbek, spol. s r.o. Vaňurova 505/17 460 07 Liberec 3	Příloha PODÉLNÝ PROFIL SO 151.4	3.4	