
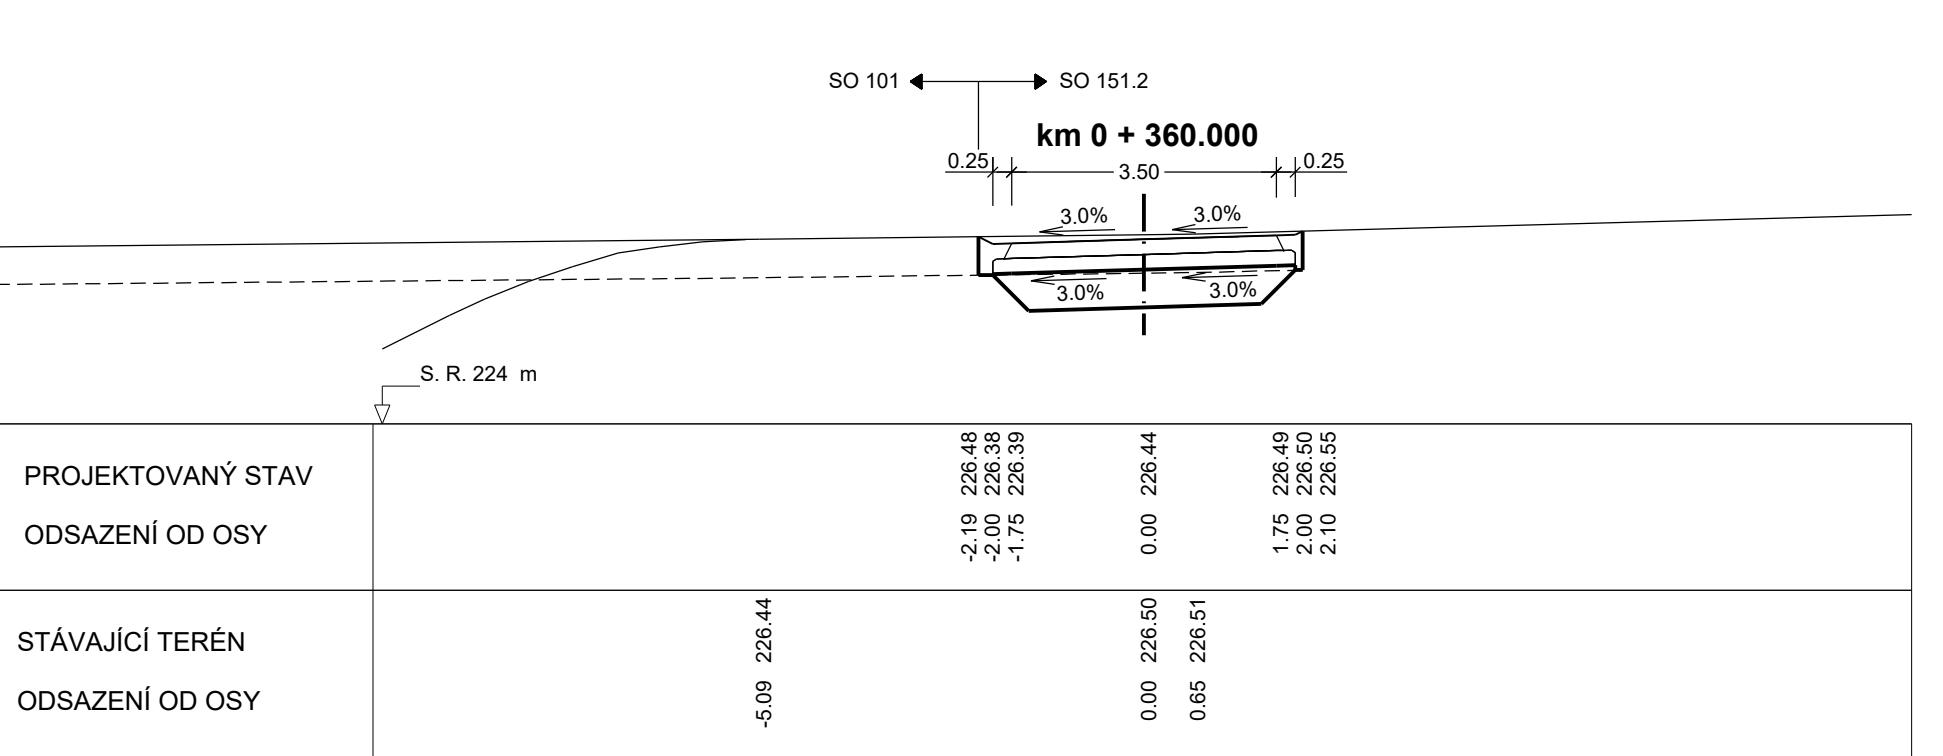
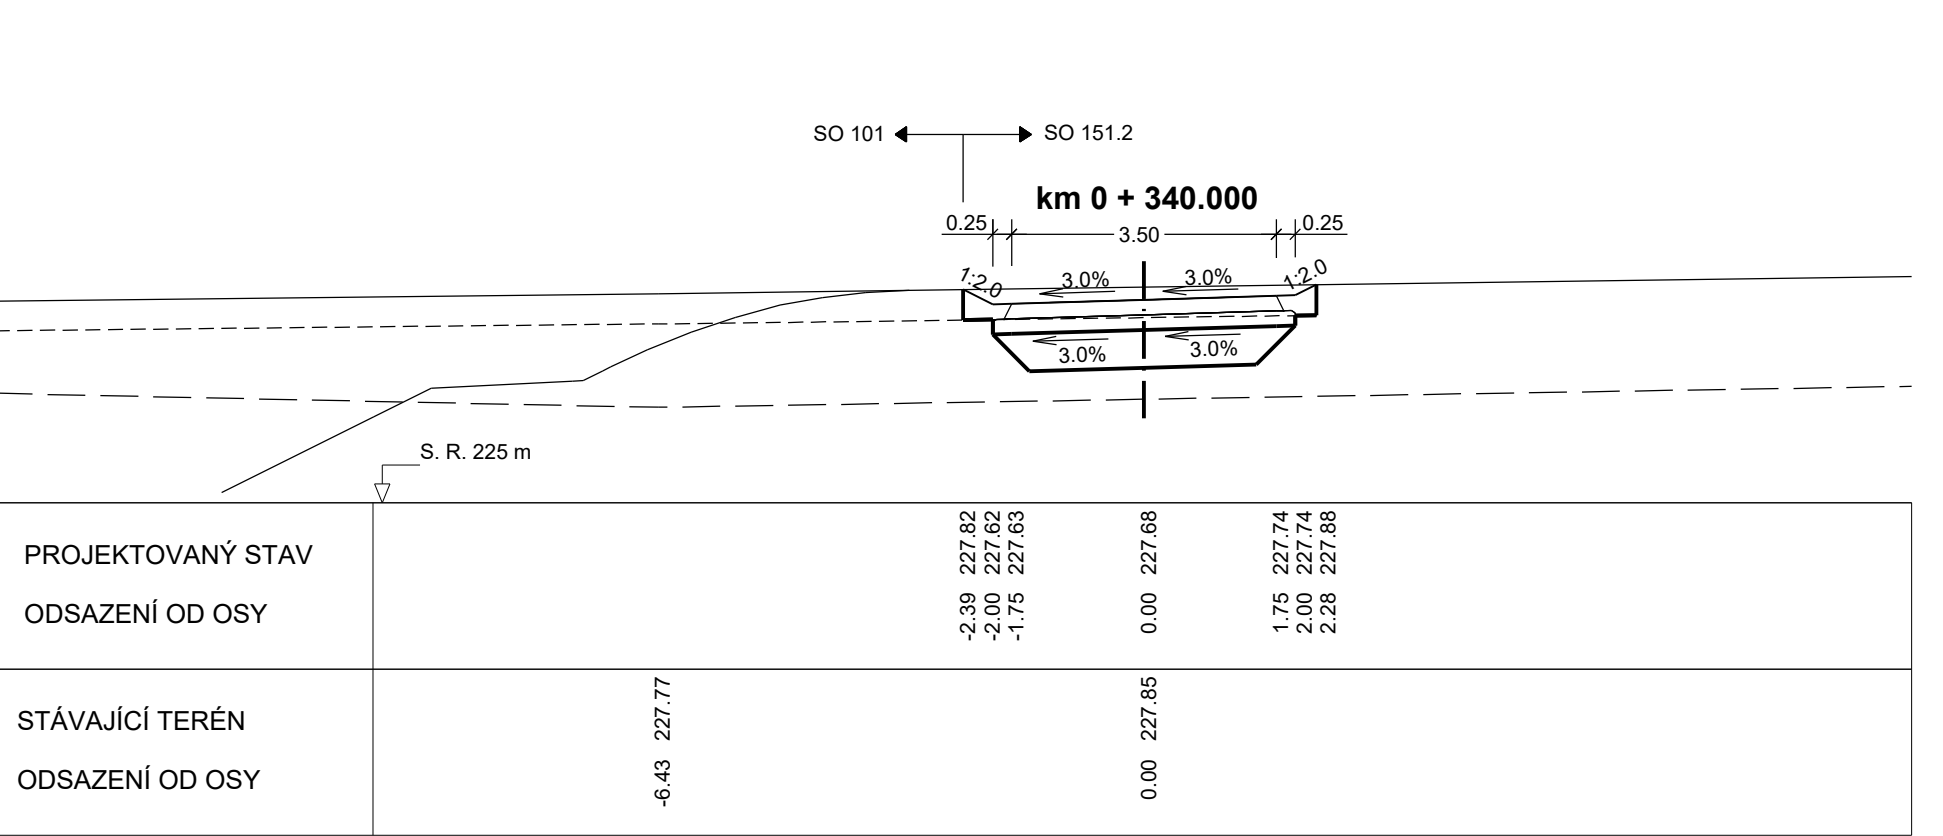
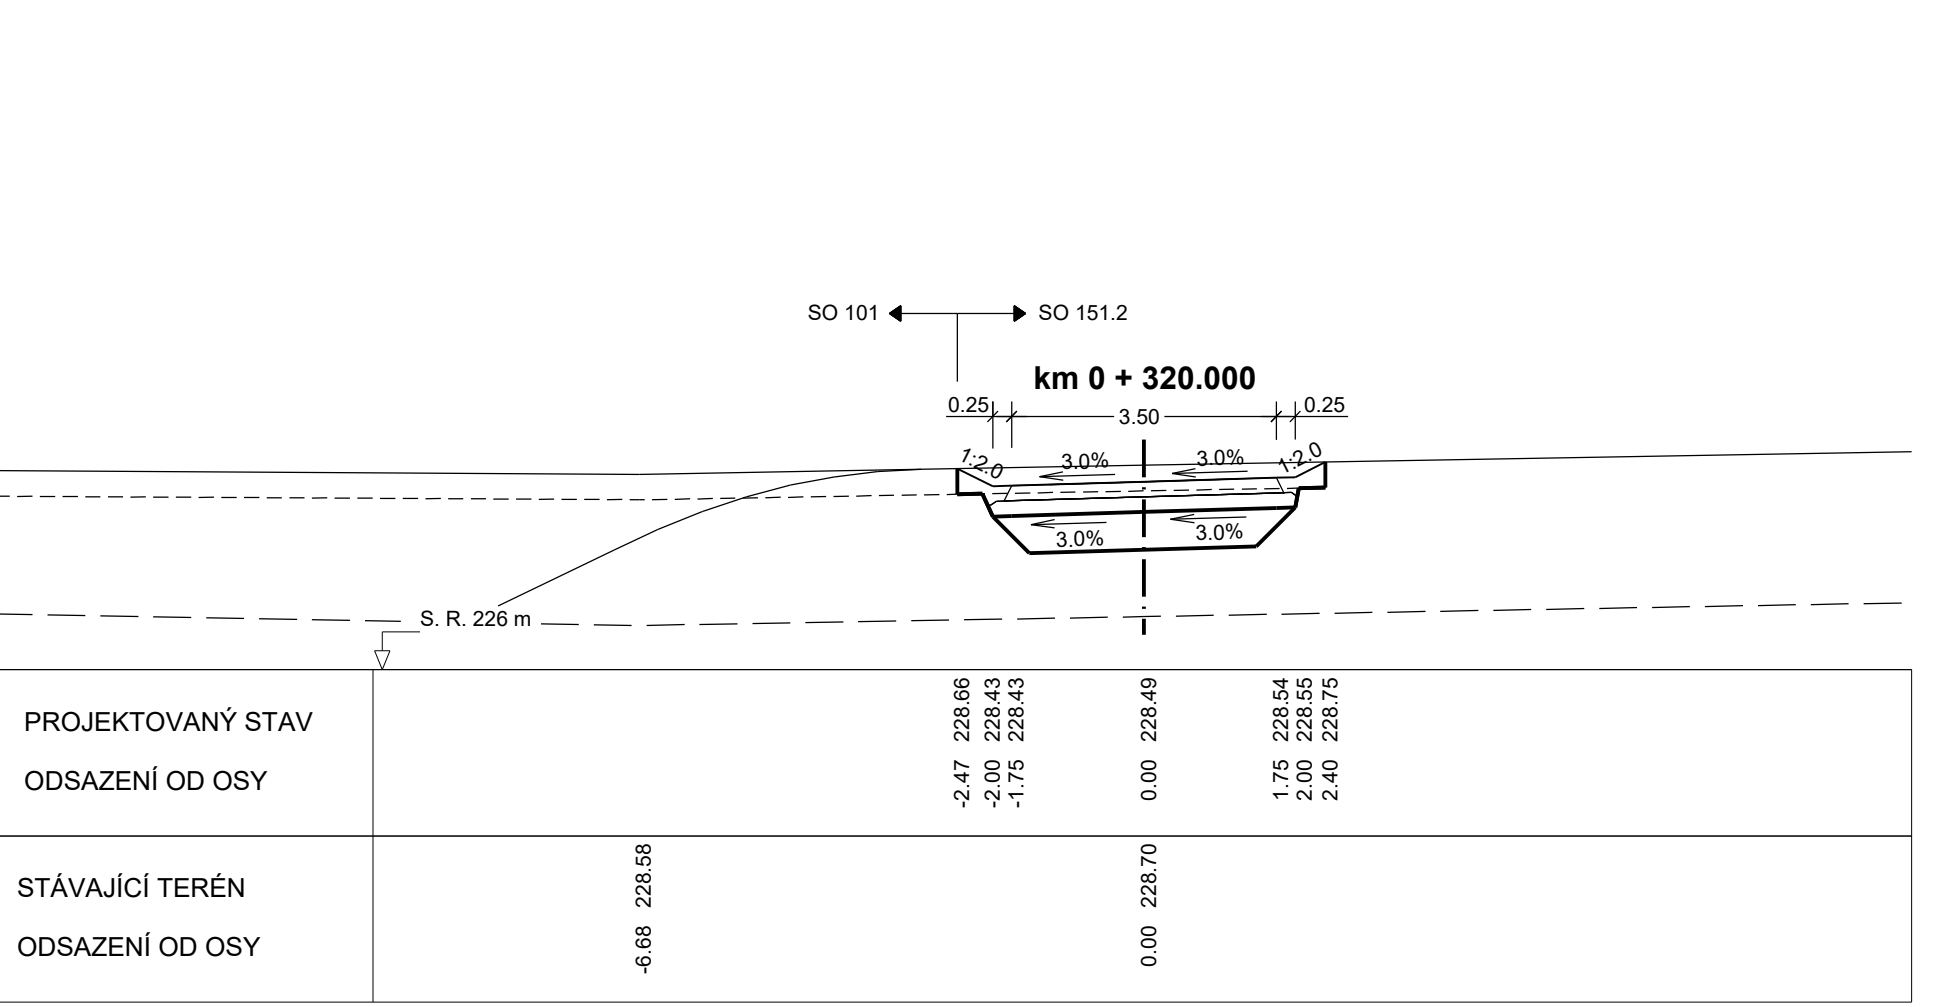
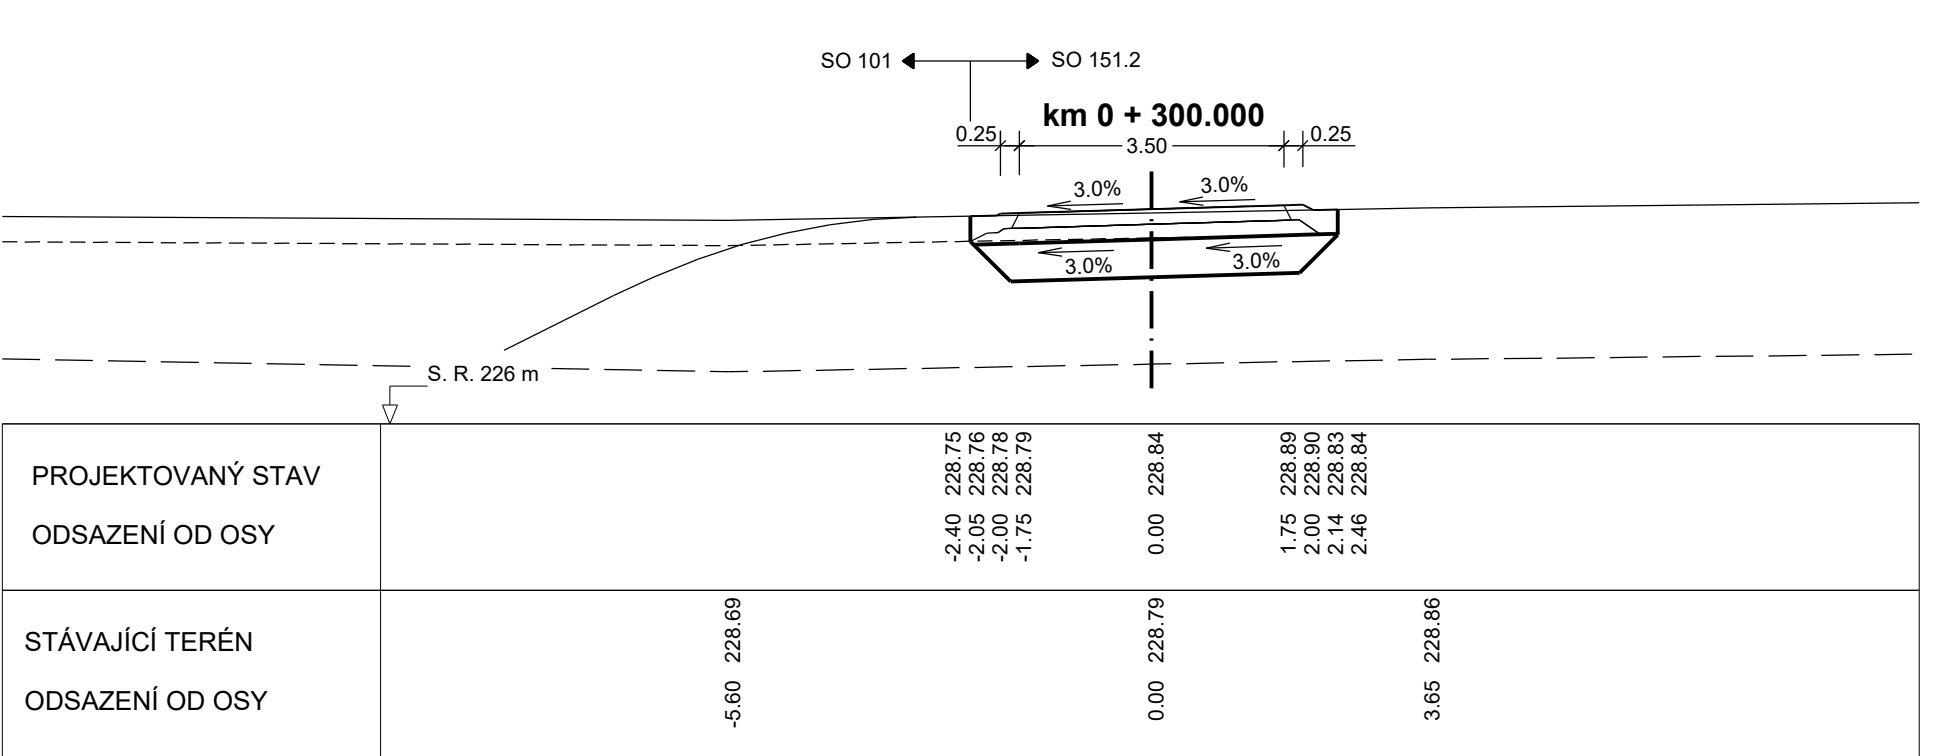
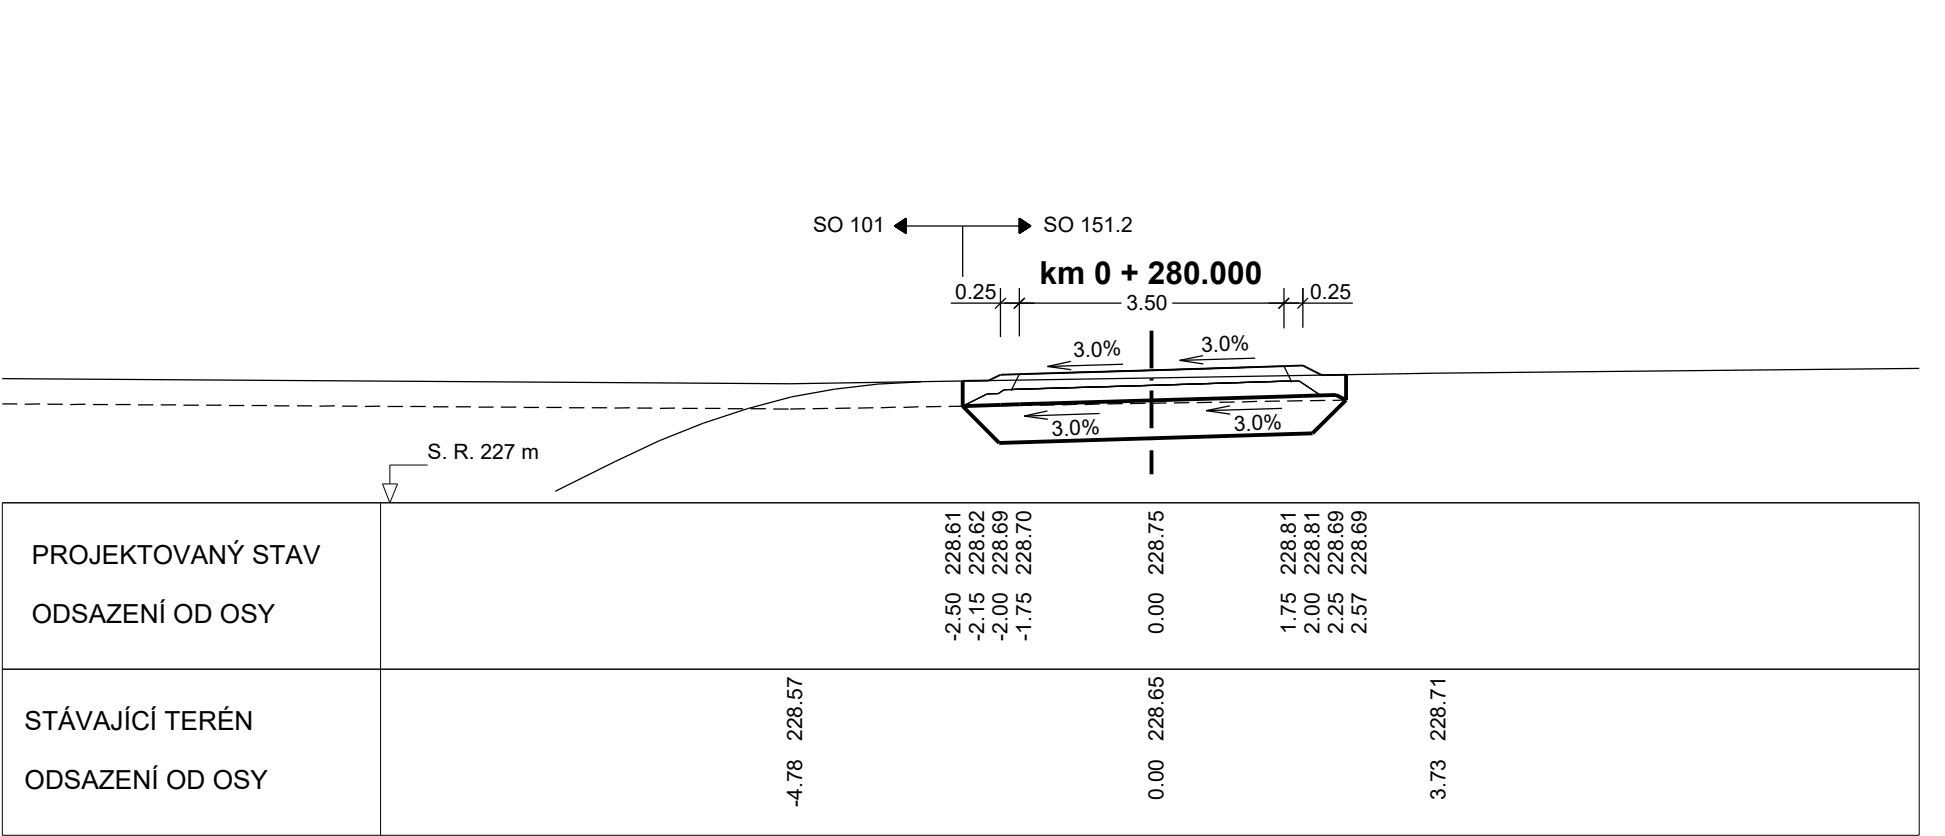
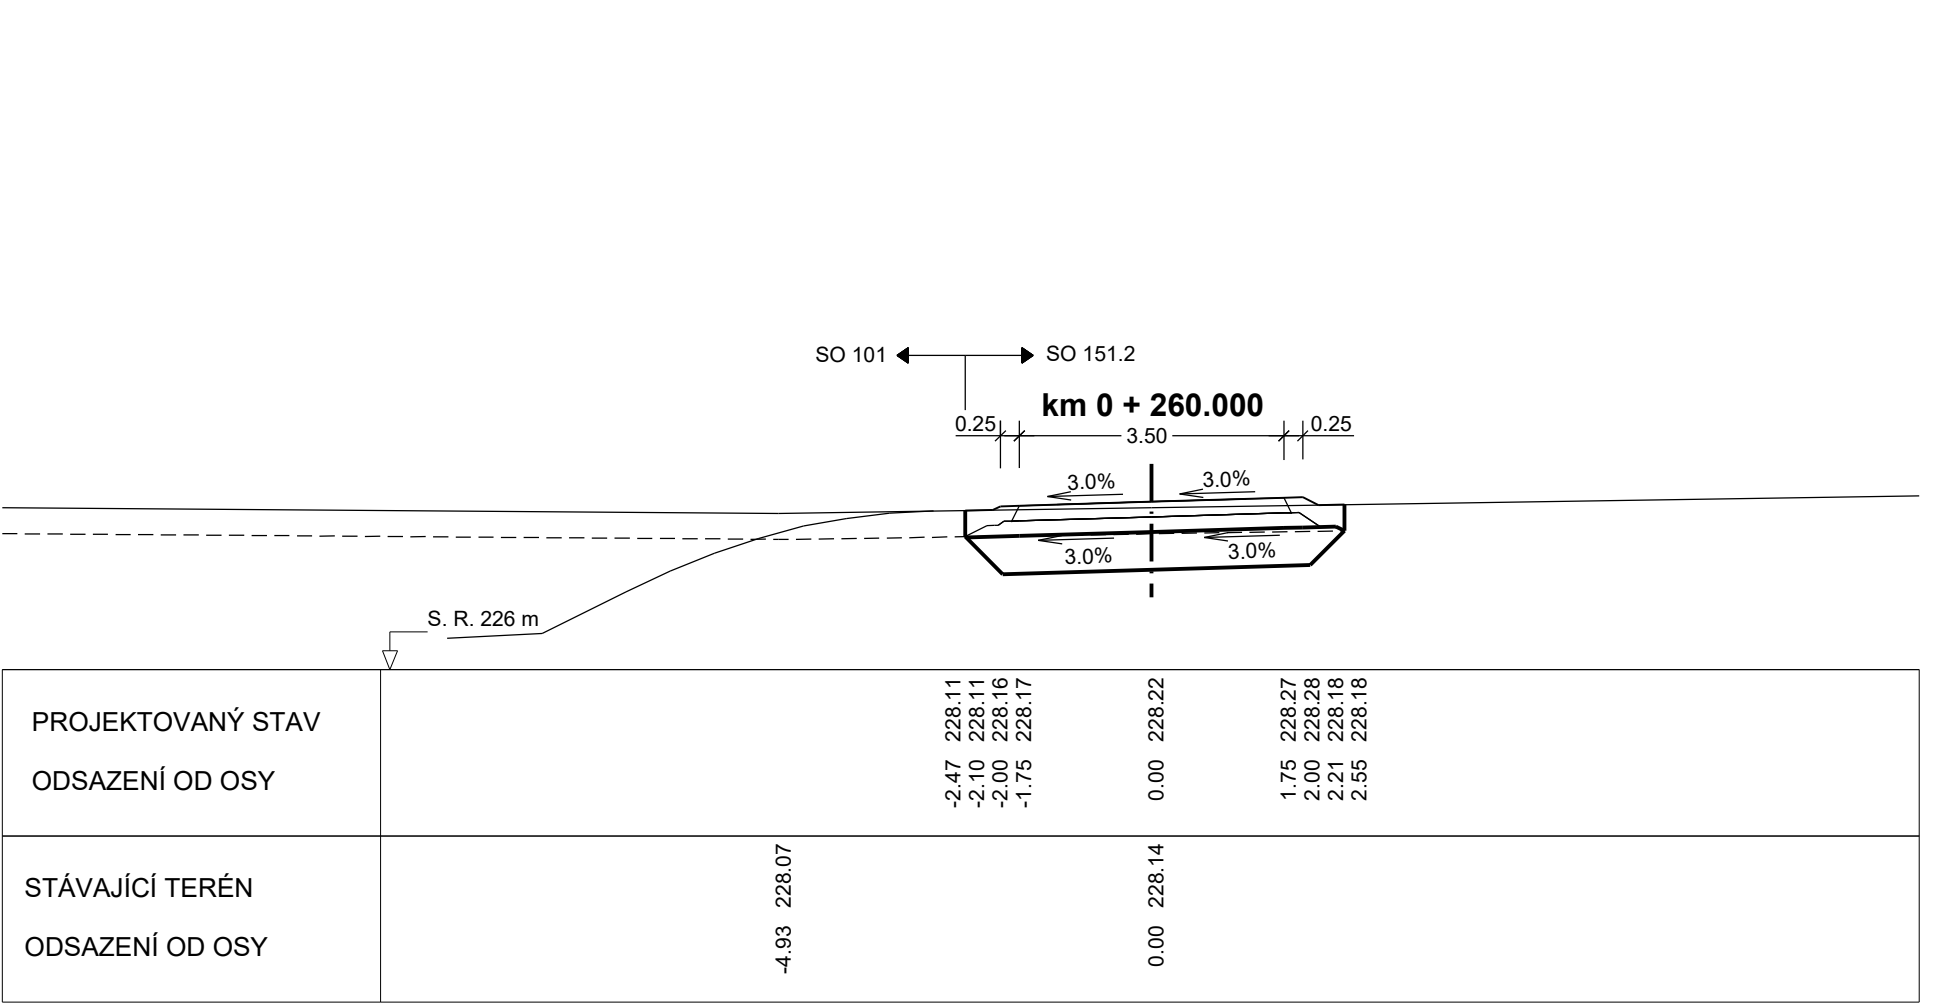
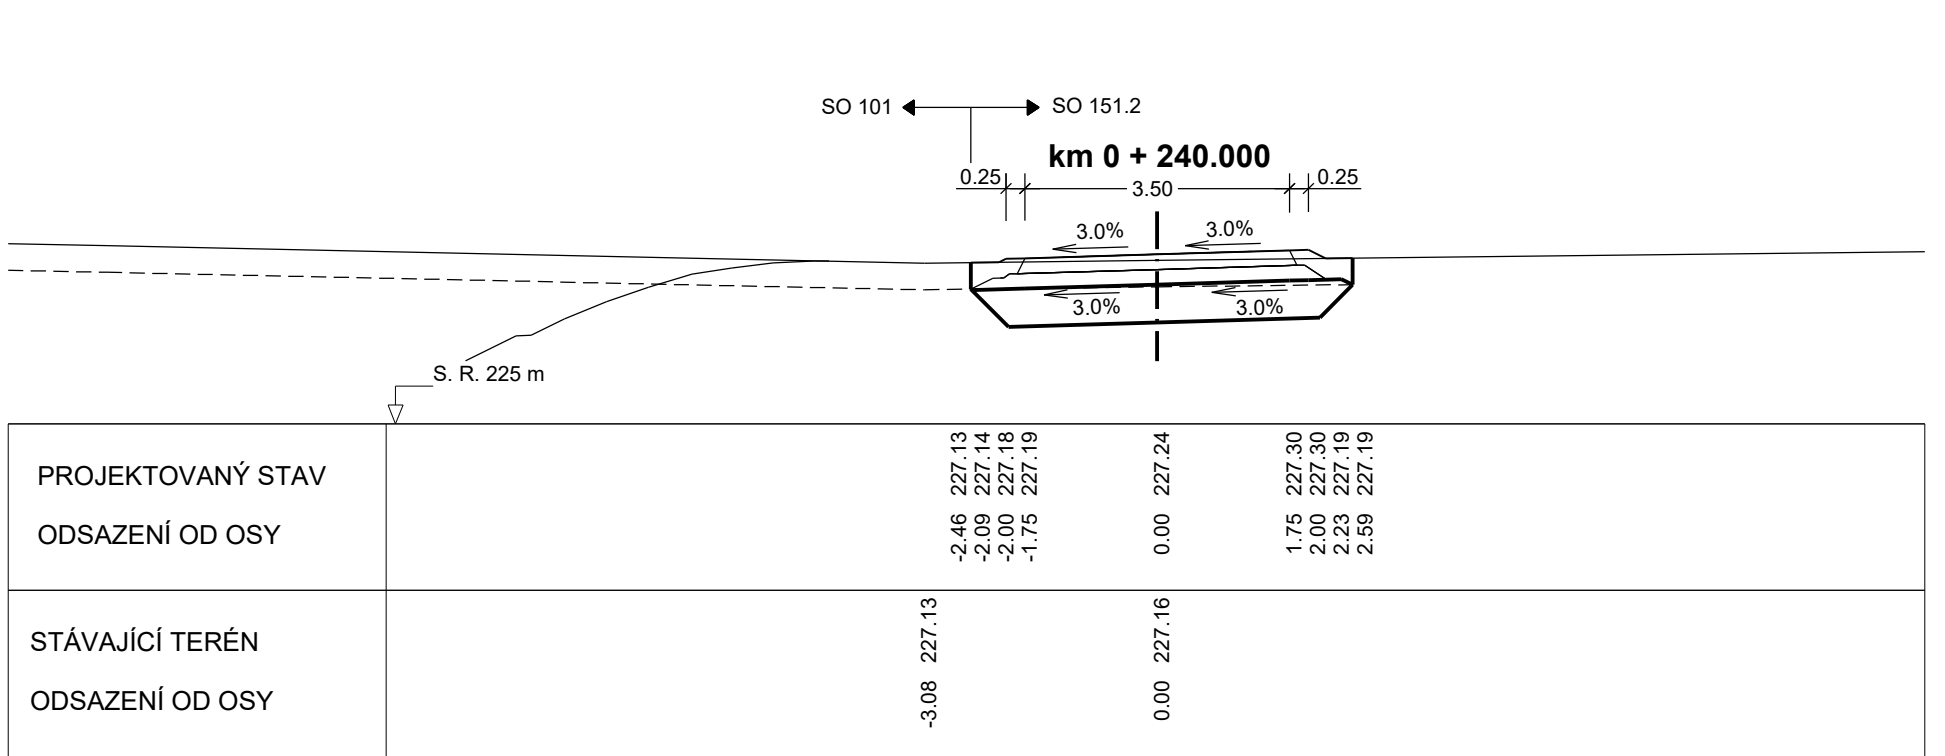
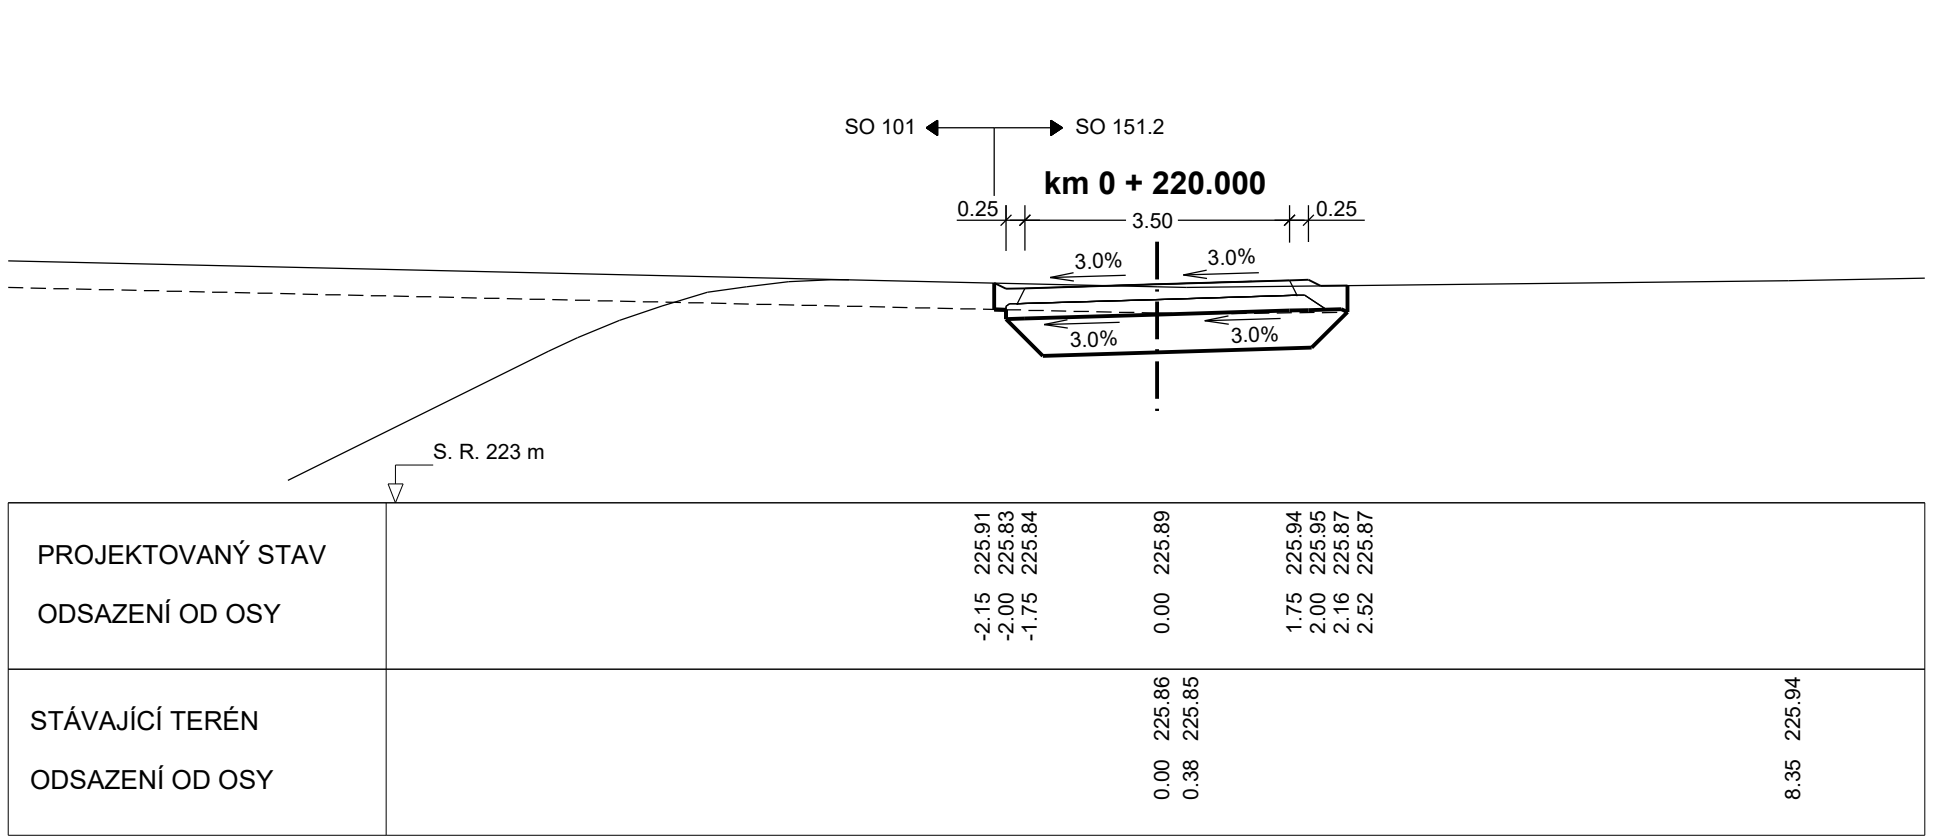
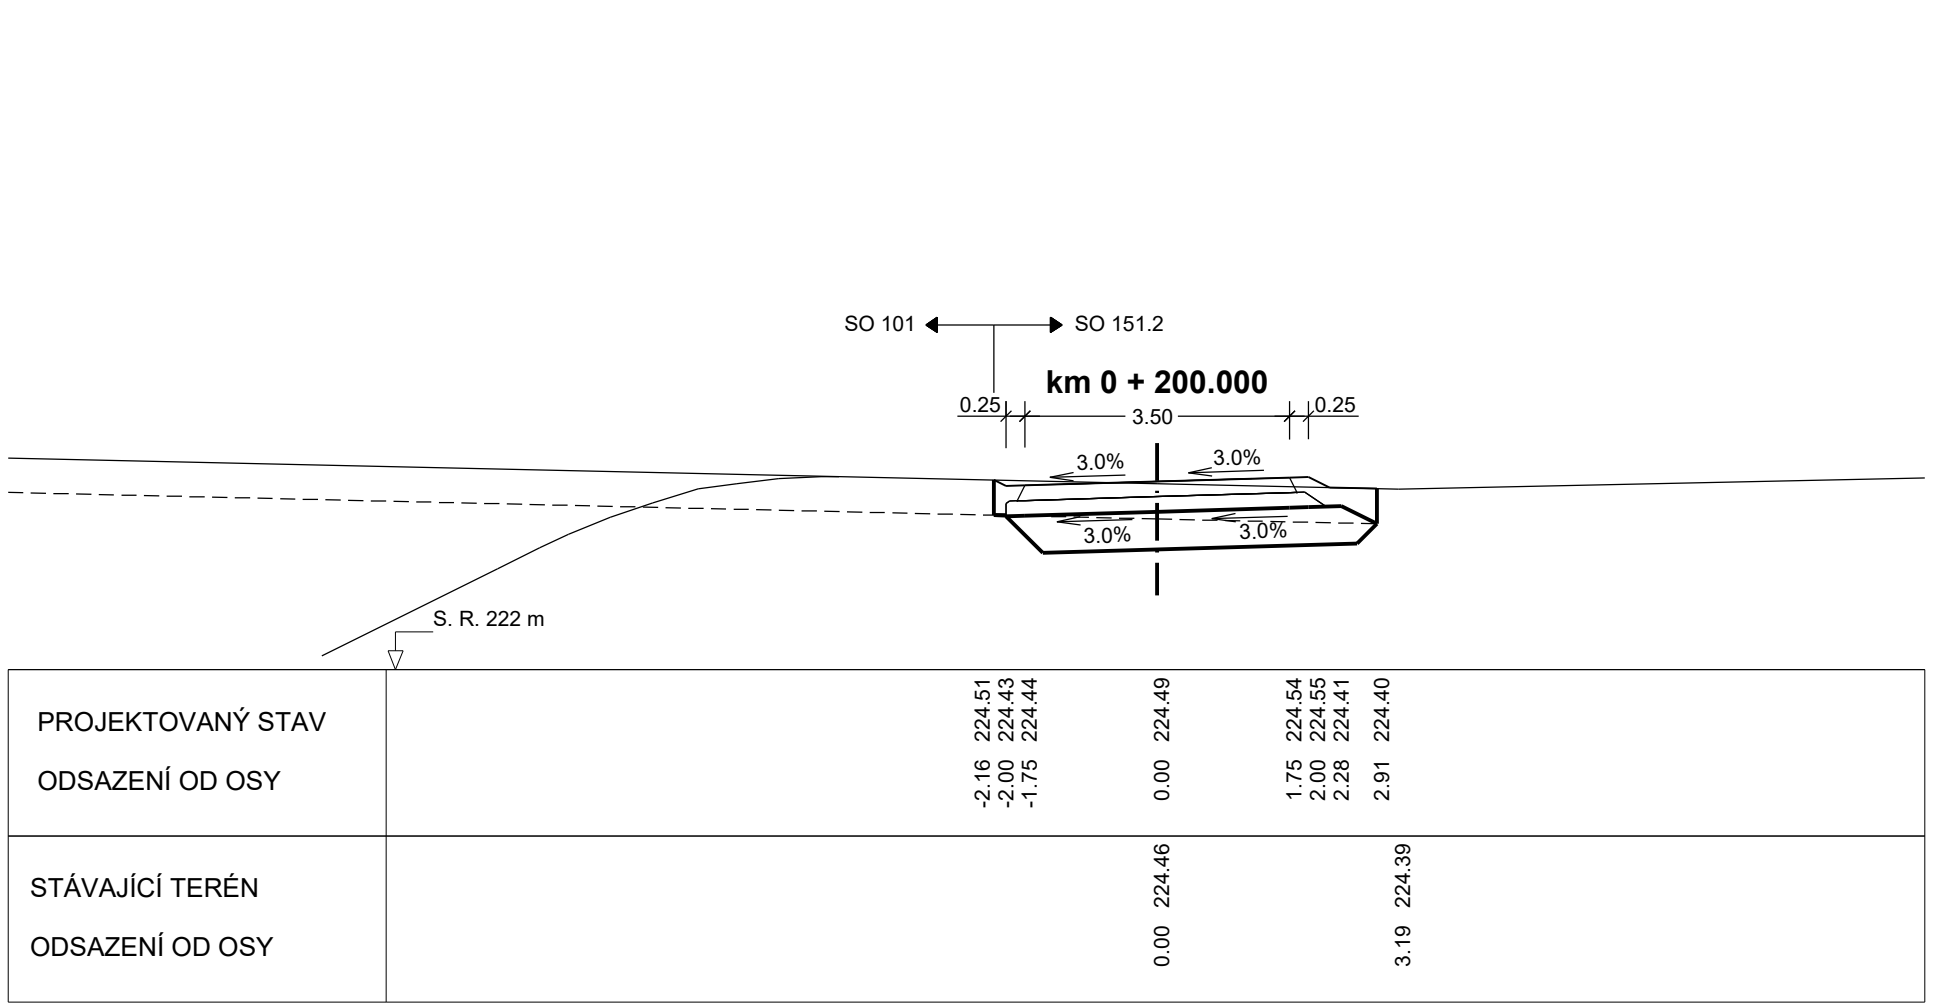
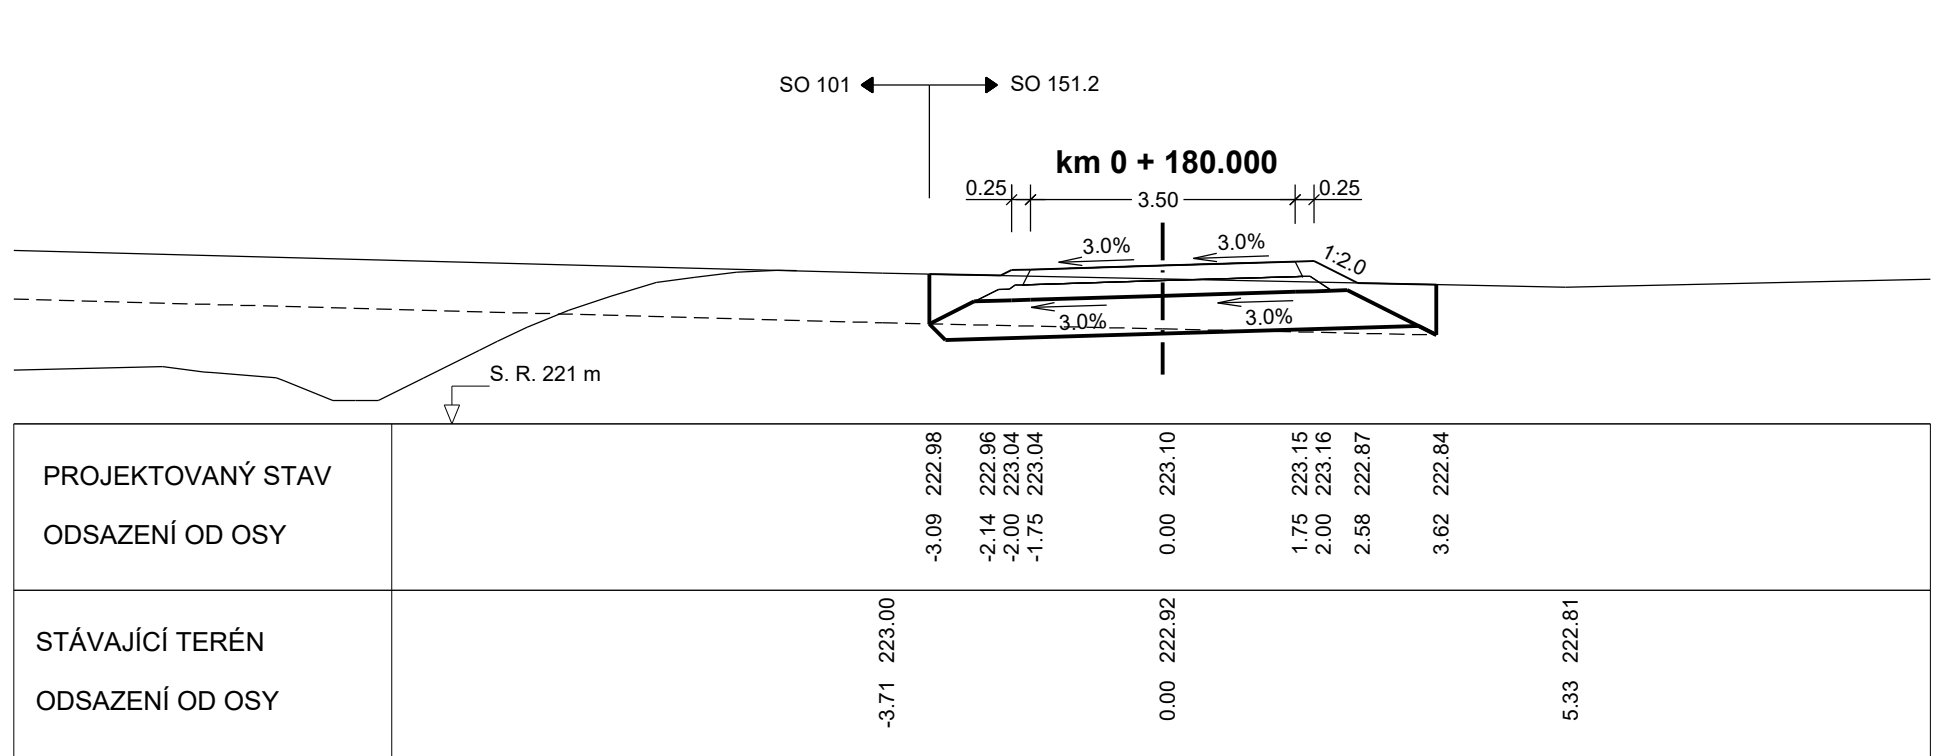
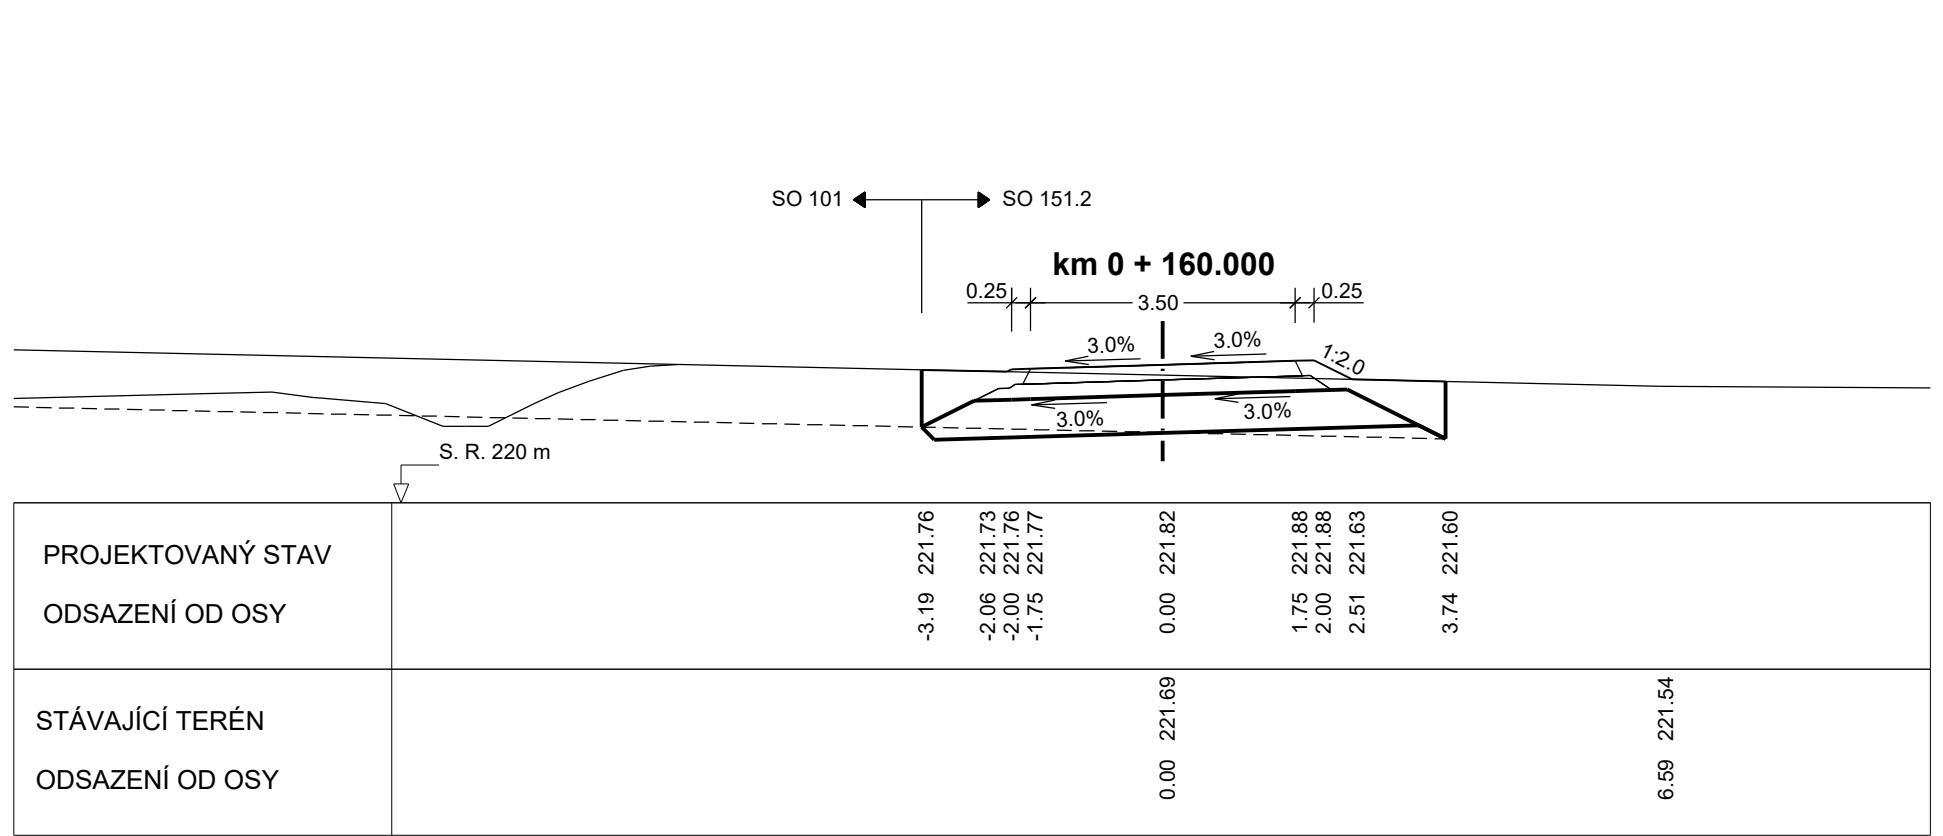
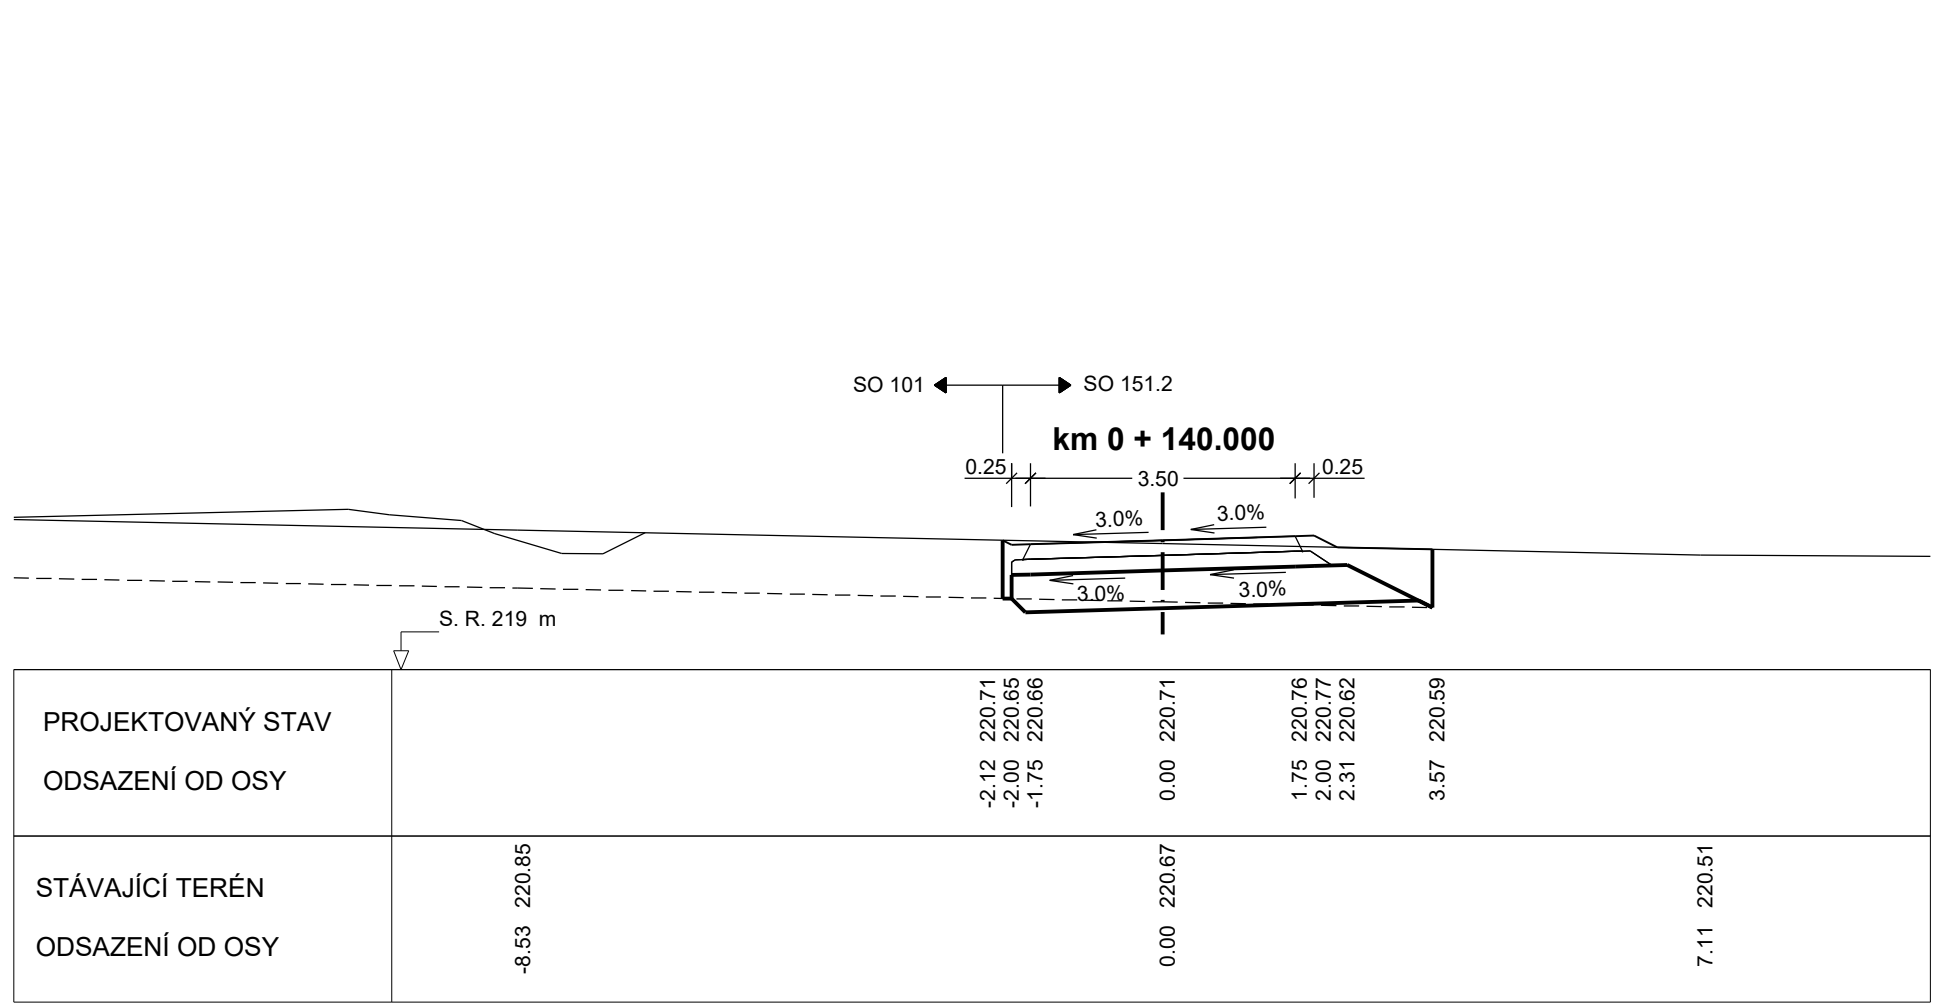
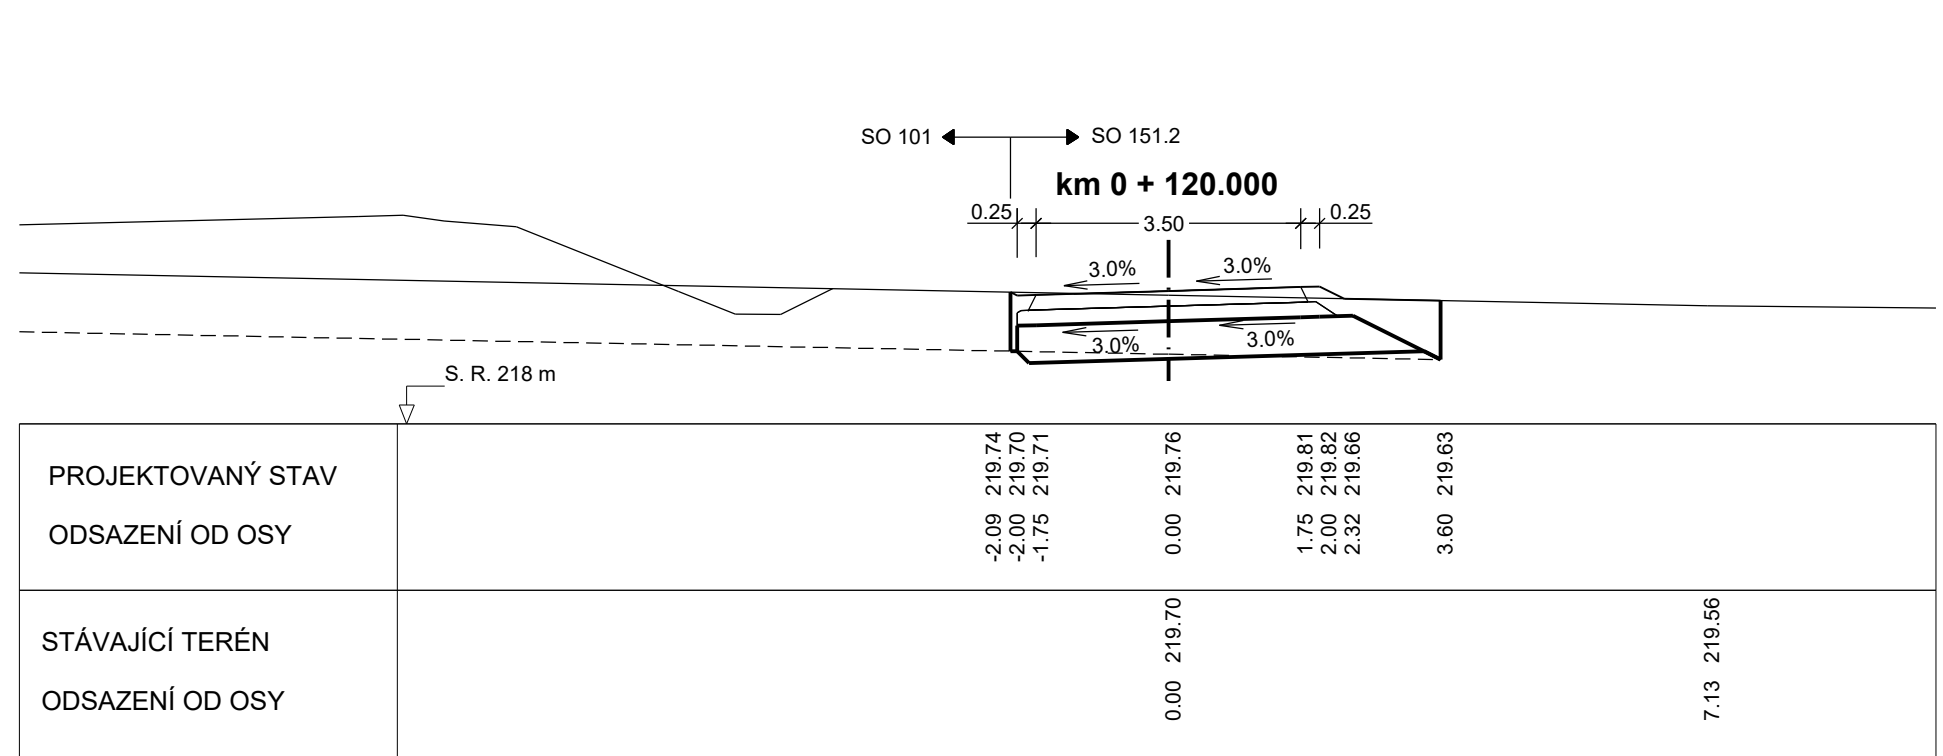
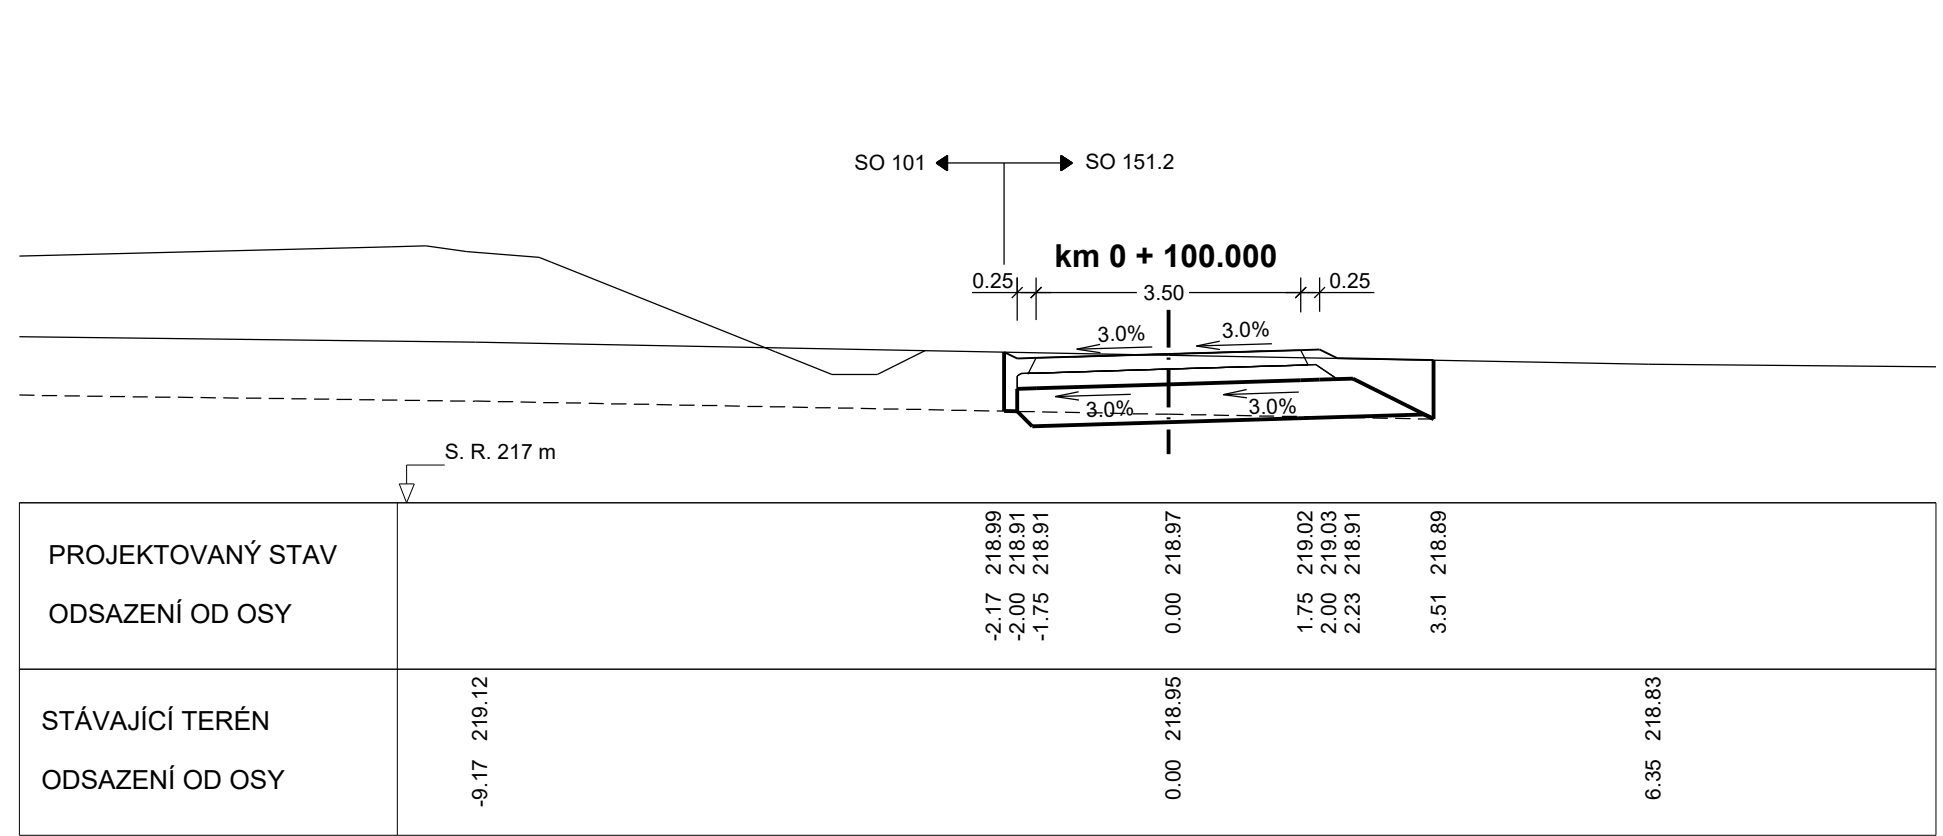
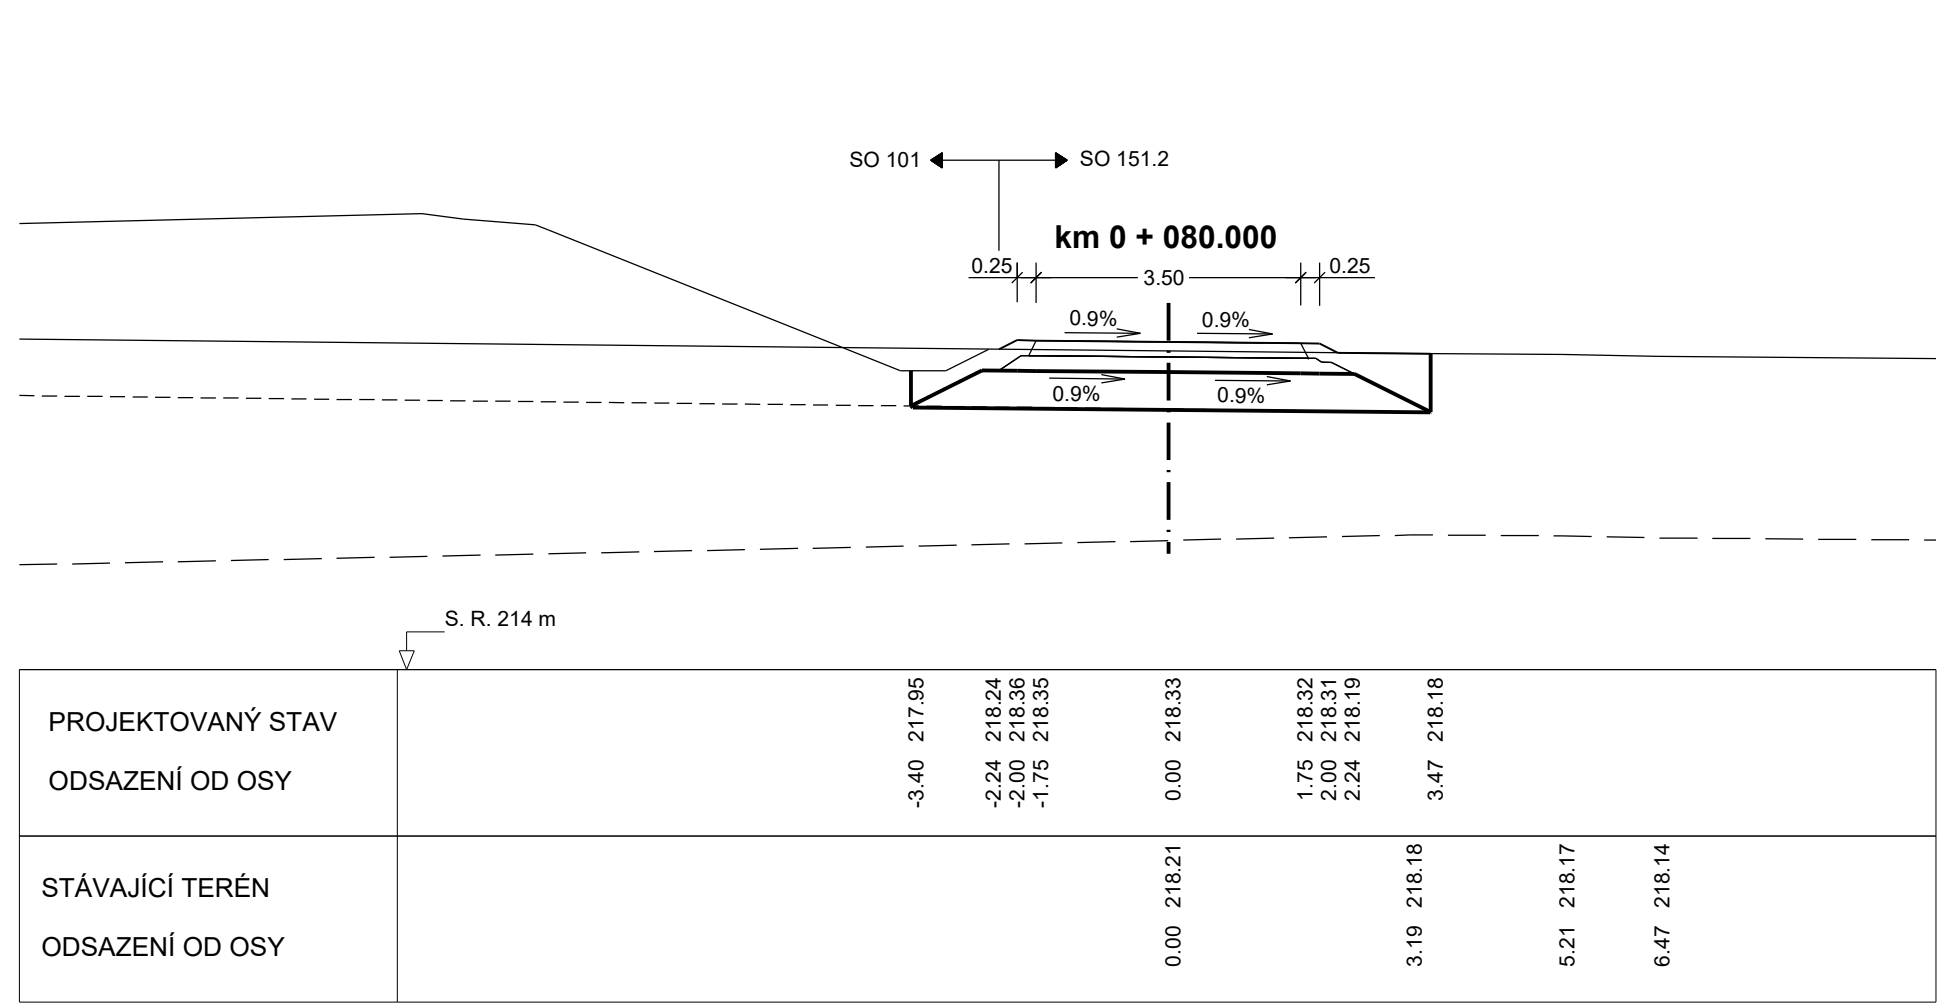
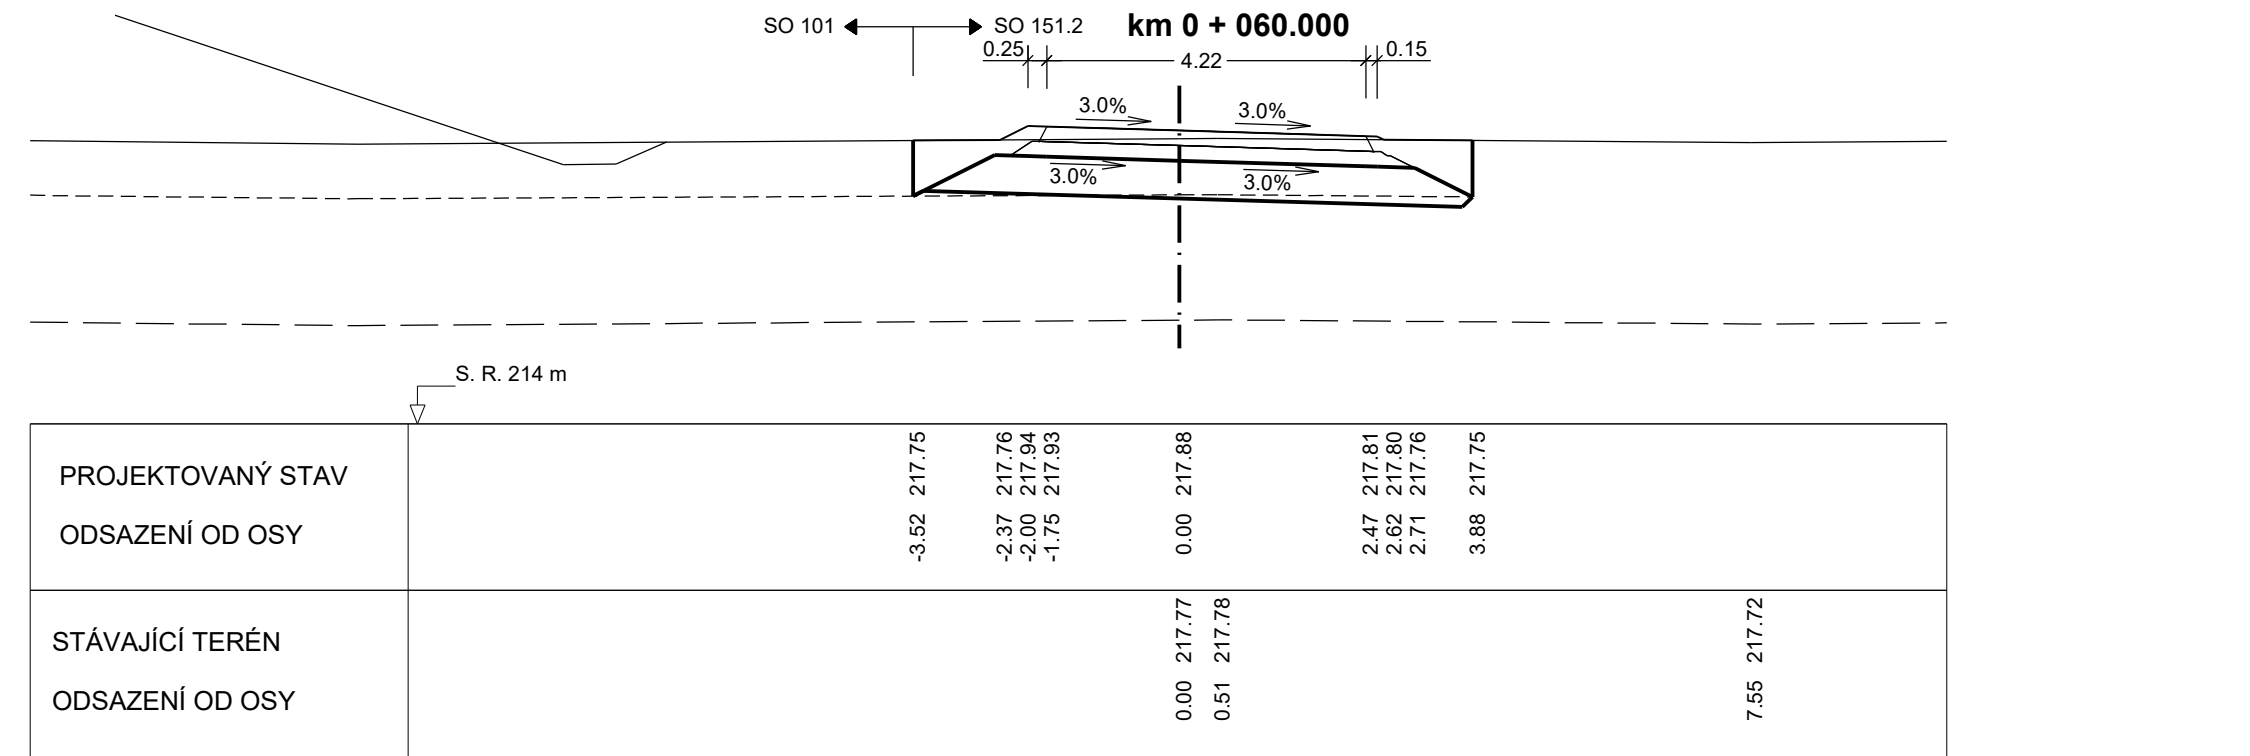
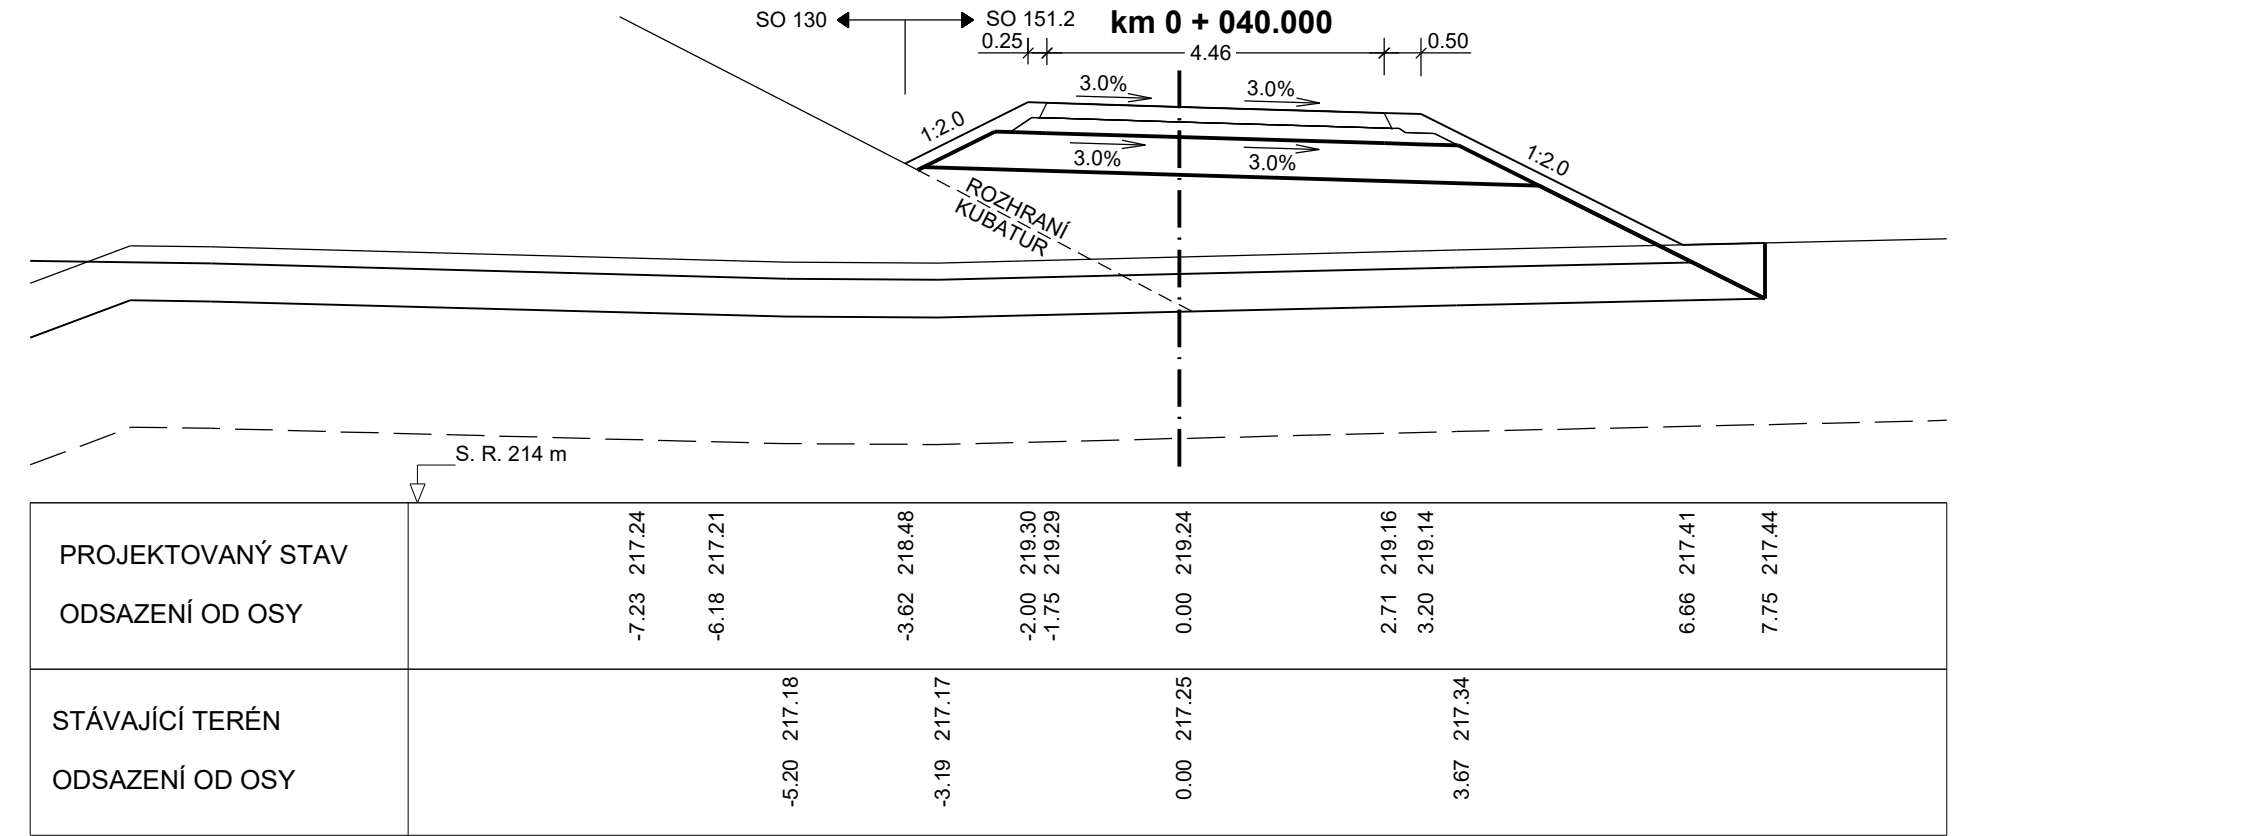


SO 151 - PŘÍSTUPY NA POZEMKY k.ú. PLAZY
PŘÍČNÉ ŘEZY SO 151.2 - km 0,020 - 0,360, M 1 : 100

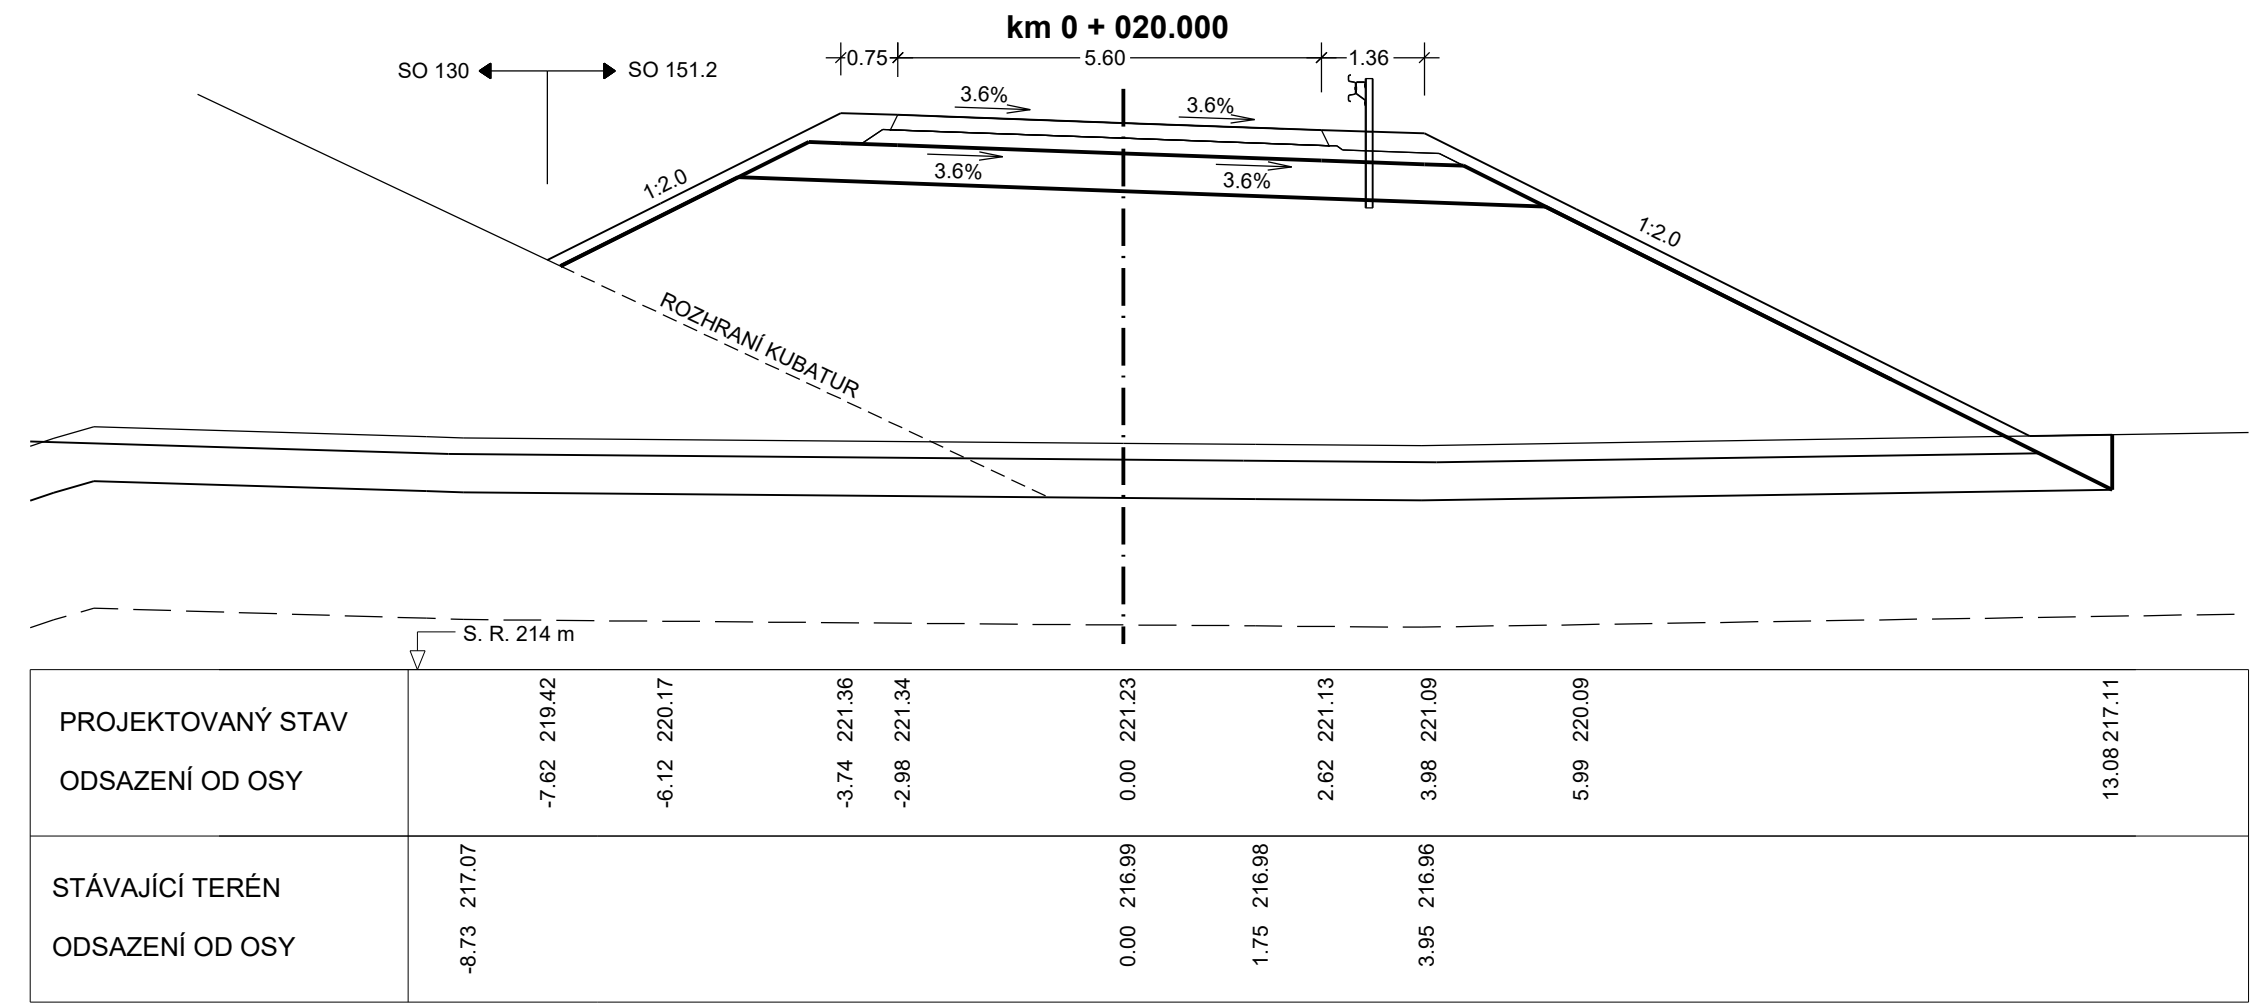

Výškový systém: Bpv

SO 151 Přístupy na pozemky k.ú. Plazy

Objednatel: Ředitelství silnic a dálnic
Ředitelství silnic a dálnic s. p.
Čerťanská 2023/12, Krč, 140 00 Praha 4

Zhotovitel: Valbek
Valbek, spol. s r.o.
Vaňurova 505/17
460 07 Liberec 3

Vypracoval: P. BARTUSEK
Zodp. projektant: ING. T. KLIMENT
Tech. kontrola: ING. M. HANŽL
Akce: I/16 MLADÁ BOLESLAV - MARTINOVICE
Příloha: PŘÍČNÉ ŘEZY SO 151 - km 0,020 - 0,360
Zak. číslo: 21.1115-001
Datum: 02/2025
Stupeň: PDPS
Počet formátů: 18 x A4
Měřítko: 1:100
Č. plochy: Paré
5.2.1