



SO 151 - PŘÍSTUP YNA POZEMKY k.ú. PLAZY


PŘÍČNÉ ŘEZY SO 151.2 - km 0,380 - 0,440, M 1 : 100

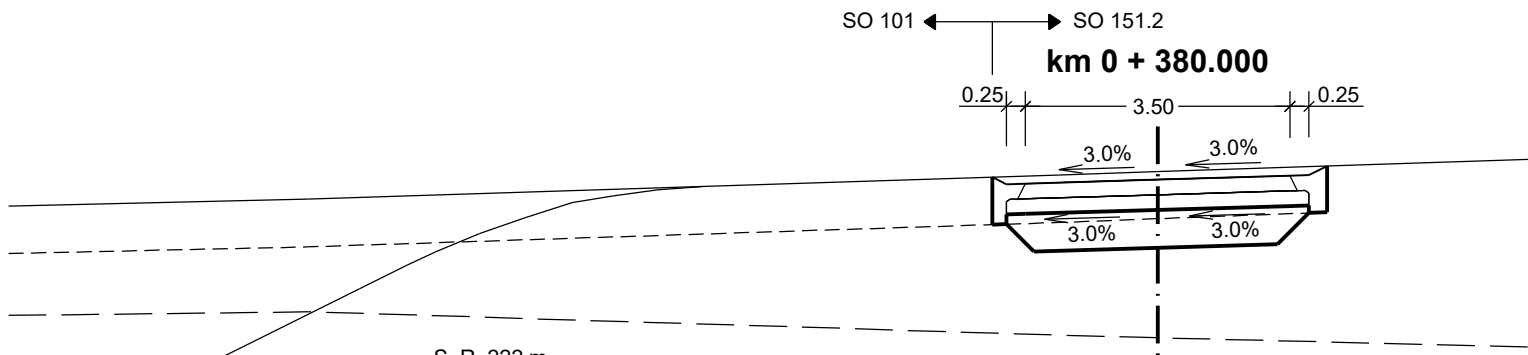


PROJEKTOVANÝ STAV									
ODSAZENÍ OD OSY									
STÁVAJÍCÍ TERÉN									
ODSAZENÍ OD OSY									

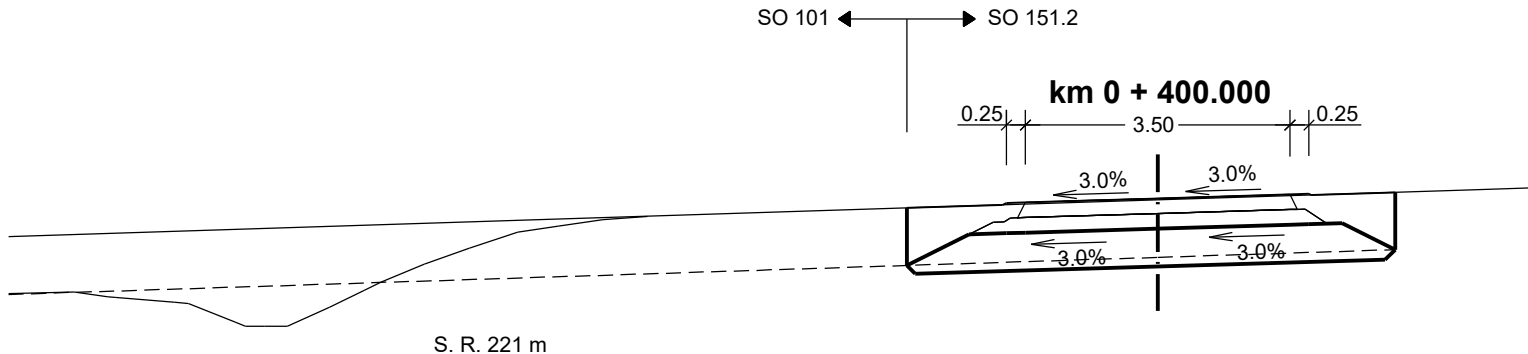

PROJEKTOVANÝ STAV									
ODSAZENÍ OD OSY									
STÁVAJÍCÍ TERÉN									
ODSAZENÍ OD OSY									

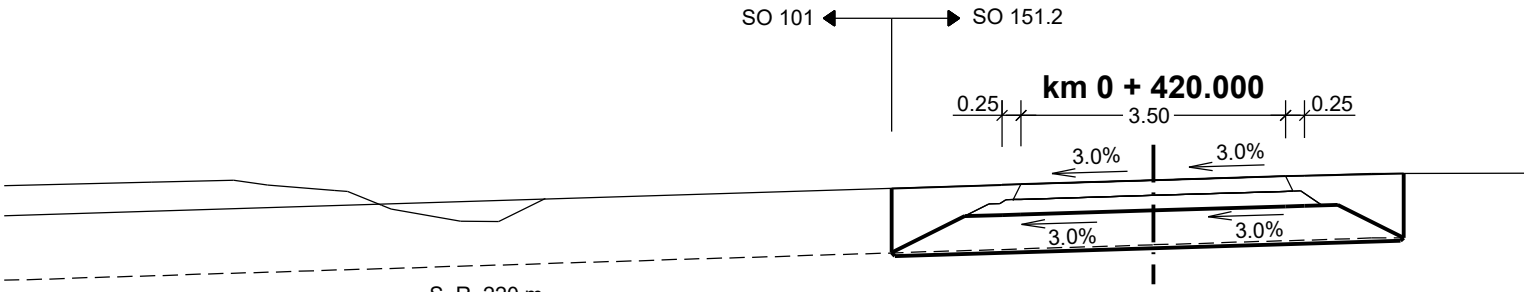

PROJEKTOVANÝ STAV									
ODSAZENÍ OD OSY									
STÁVAJÍCÍ TERÉN									
ODSAZENÍ OD OSY									

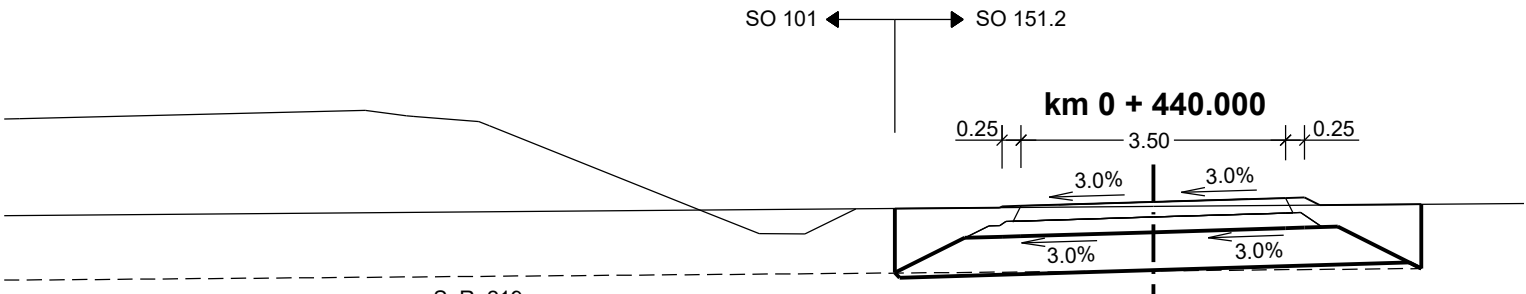

PROJEKTOVANÝ STAV									
ODSAZENÍ OD OSY									
STÁVAJÍCÍ TERÉN									
ODSAZENÍ OD OSY									

Výškový systém: Bpv

SO 151 Přístupy na pozemky k.ú. Plazy

Objednatel:



**ŘEDITELSTVÍ
SILNIC
A DÁLNIC**

Ředitelství silnic a dálnic s. p.
Čerčanská 2023/12, Krč, 140 00 Praha 4

Zhotovitel:



Valbek, spol. s r.o.
Vaňurova 505/17
460 07 Liberec 3

	Vypracoval	P. BARTUSEK	Zak. číslo	21-L113-001
	Zodp. projektant	ING .T. KLIMENT	Datum	02/2025
	Tech. kontrola	ING .M. HANŽL	Stupeň	PDPS
	Akce I/16 MLADÁ BOLESLAV - MARTINOVICE		Počet formátů	3 x A4
			Měřítko	
Zhotovitel: Valbek, spol. s r.o. Vaňurova 505/17 460 07 Liberec 3	Příloha PŘÍČNÉ ŘEZY SO 151.2 - km 0,380 - 0,440		Č. přílohy	Paré