


SO 151 - PŘÍSTUPY NA POZEMKY k.ú. PLAZY

PŘÍČNÉ ŘEZY SO 151.4, M 1 : 100


km 0 + 020.000

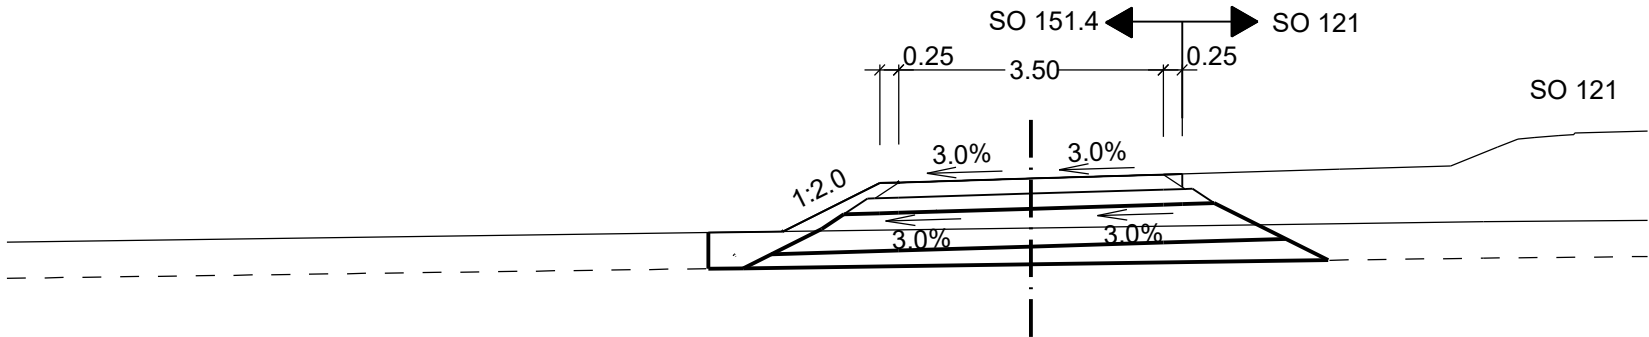

S. R. 217 m

PROJEKTOVANÝ STAV	
-------------------	--	--	


km 0 + 040.000

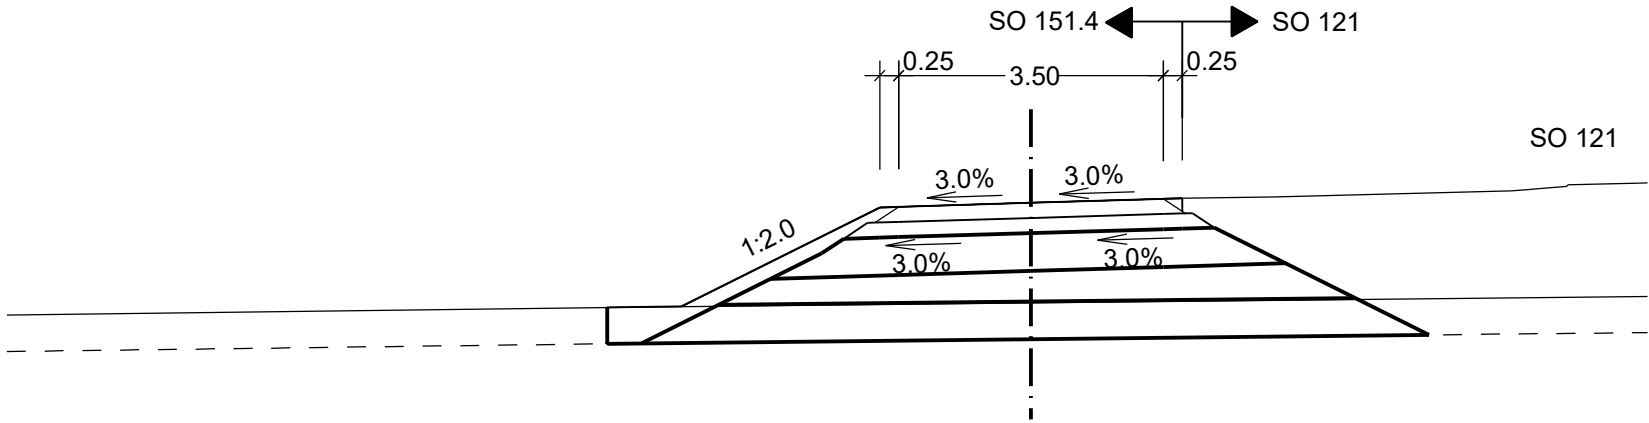

S. R. 217 m

PROJEKTOVANÝ STAV	
-------------------	--	--	


km 0 + 060.000

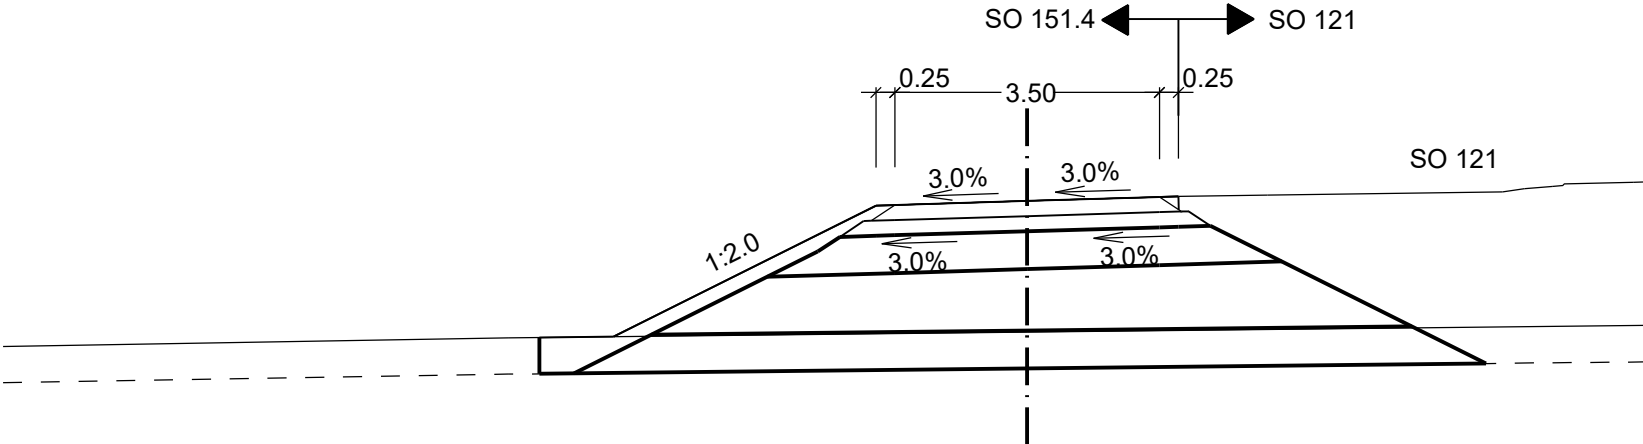

S. R. 216 m

PROJEKTOVANÝ STAV	
-------------------	--	--	

km 0 + 080.000

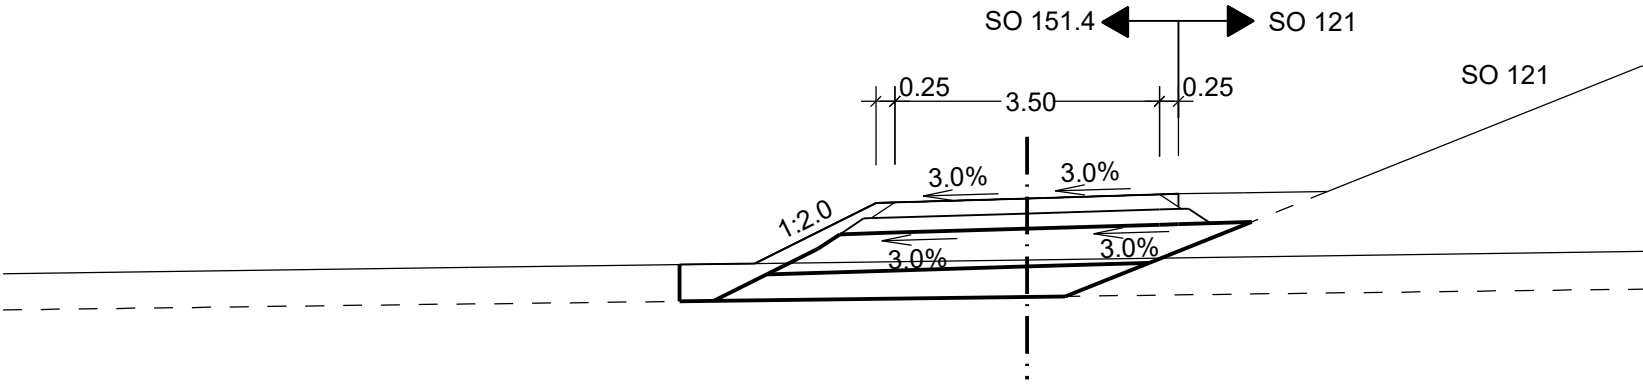

S. R. 216 m

PROJEKTOVANÝ STAV	
-------------------	--	--	

Výškový systém: Bpv

SO 151 Přístupy na pozemky k.ú. Plazy

Objednatel:



**Ředitelství
silnic
a dálnic**

Ředitelství silnic a dálnic s. p.
Čerčanská 2023/12, Krč, 140 00 Praha 4

Zhotovitel:	Valbek, spol. s r.o. Vaňurova 505/17 460 07 Liberec 3	HIP:
		ING. T. KLIMENT

	Vypracoval	ING. A. DUMANSKA		Zak. číslo	21-L113-001
	Zodp. projektant	ING. T. KLIMENT		Datum	02/2025
	Tech. kontrola	ING. M. HANŽL		Stupeň	PDPS
	Akce I/16 MLADÁ BOLESLAV - MARTINOVICE			Počet formátů	4 x A4
				Měřítko	1 : 100
Zhotovitel: Valbek, spol. s r.o. Vaňurova 505/17 460 07 Liberec 3	Příloha	PŘÍČNÉ ŘEZY SO 151.4			Č. přílohy 5.4 Paré