




SO 151 - PŘÍSTUPY NA POZEMKY K.Ú. PLAZY
PŘÍČNÉ ŘEZY SO 151.5 - km 0,340 - 0,740, M 1 : 100

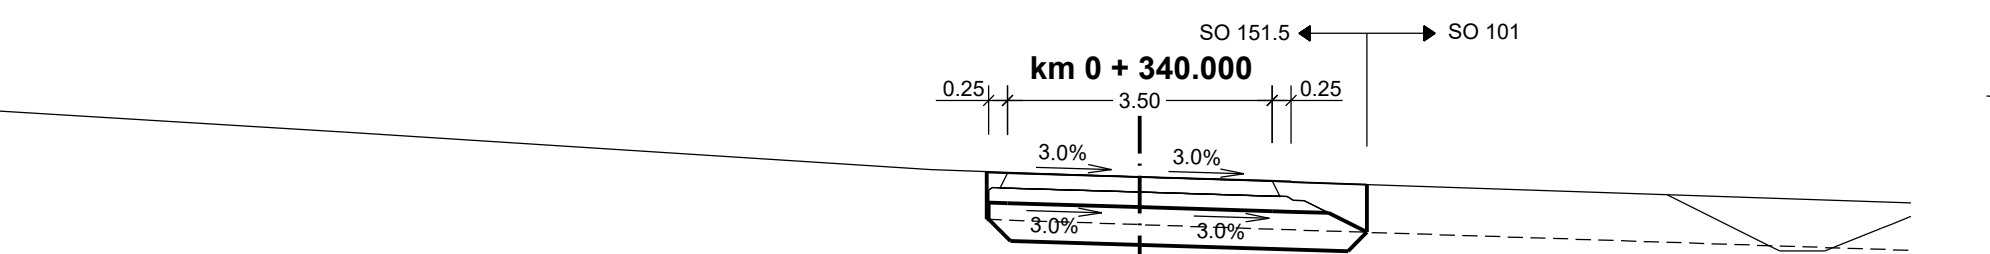


PROJEKTOVANÝ STAV	S. R. 215 m
ODSAZENÍ OD OSY	-2.25 216.94 -2.02 217.05 -2.00 216.93 -1.75 216.82 0.00 216.87 1.75 216.82 2.00 216.80 2.00 216.80 3.00 216.77
STÁVAJÍCÍ TERÉN	-2.75 216.97 -1.10 216.91 0.00 216.87
ODSAZENÍ OD OSY	

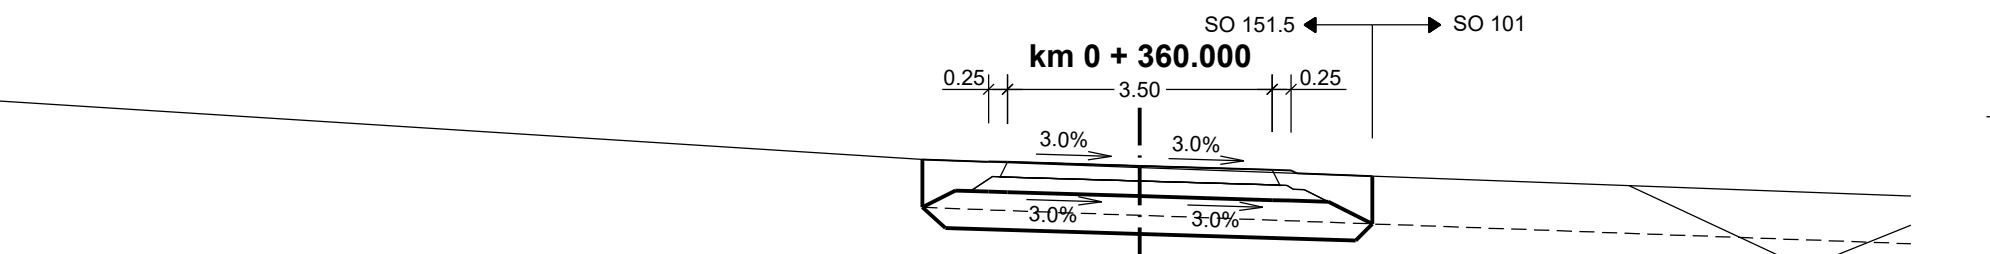


PROJEKTOVANÝ STAV	S. R. 215 m
ODSAZENÍ OD OSY	-2.67 217.13 -2.02 217.08 -2.00 217.08 -1.75 217.08 0.00 217.03 1.75 216.98 2.00 216.93 2.00 216.93 3.00 216.89
STÁVAJÍCÍ TERÉN	-2.85 217.11 0.00 217.01
ODSAZENÍ OD OSY	

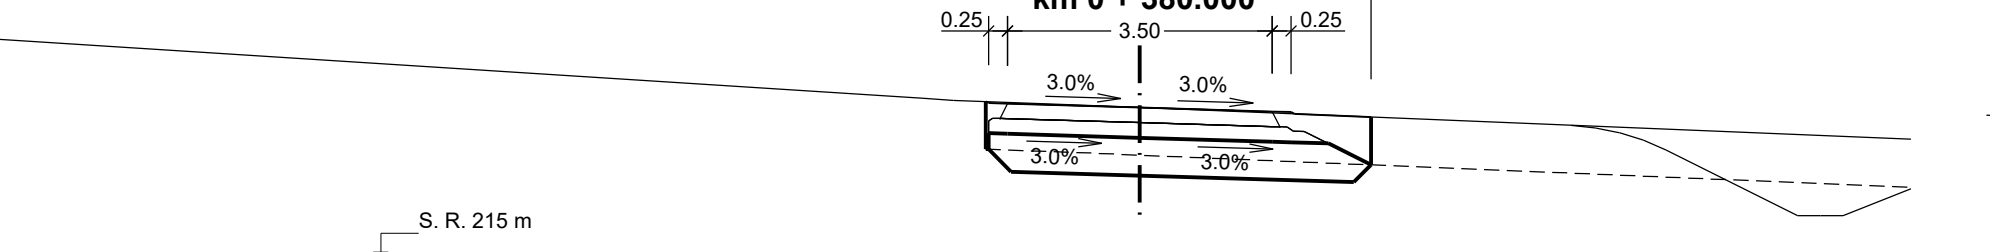


PROJEKTOVANÝ STAV	S. R. 215 m
ODSAZENÍ OD OSY	-2.98 217.28 -2.47 217.26 -2.00 217.22 -1.75 217.21 -0.85 217.20 0.00 217.16 1.75 217.11 2.00 217.08 2.00 217.08 3.00 217.04
STÁVAJÍCÍ TERÉN	-2.98 217.28 -2.47 217.26 -0.85 217.20 0.00 217.16
ODSAZENÍ OD OSY	

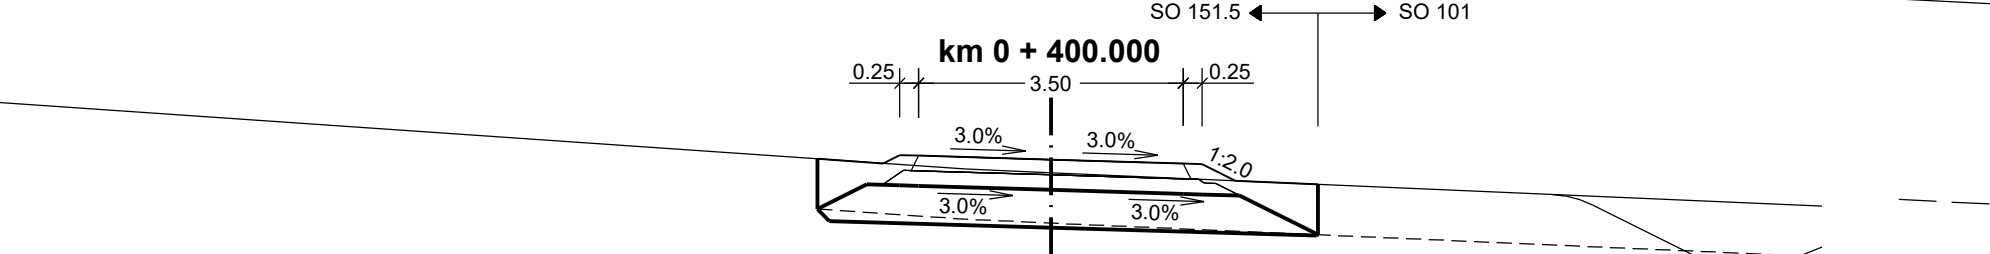


PROJEKTOVANÝ STAV	S. R. 215 m
ODSAZENÍ OD OSY	-3.00 217.11 -2.22 217.05 -2.00 217.05 -1.75 217.15 0.00 217.10 1.75 217.05 2.00 217.04 2.44 216.82 3.00 216.77
STÁVAJÍCÍ TERÉN	-1.13 216.97 0.00 216.93 0.00 216.87
ODSAZENÍ OD OSY	

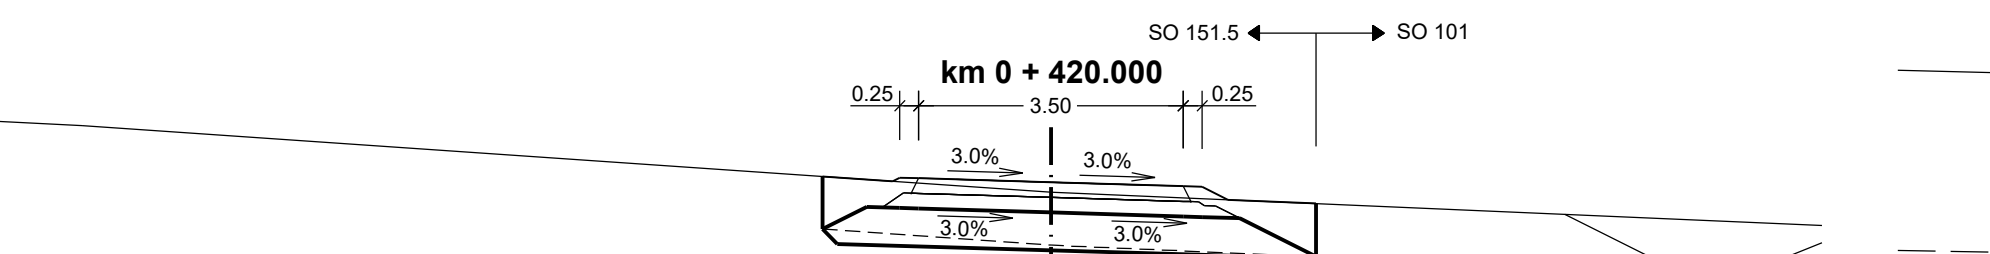


PROJEKTOVANÝ STAV	S. R. 215 m
ODSAZENÍ OD OSY	-3.02 216.89 -2.00 216.83 -2.00 217.08 -1.75 216.87 0.00 216.81 1.75 216.75 2.00 216.75 2.00 216.53 3.00 216.50
STÁVAJÍCÍ TERÉN	0.00 216.88 0.00 217.01
ODSAZENÍ OD OSY	

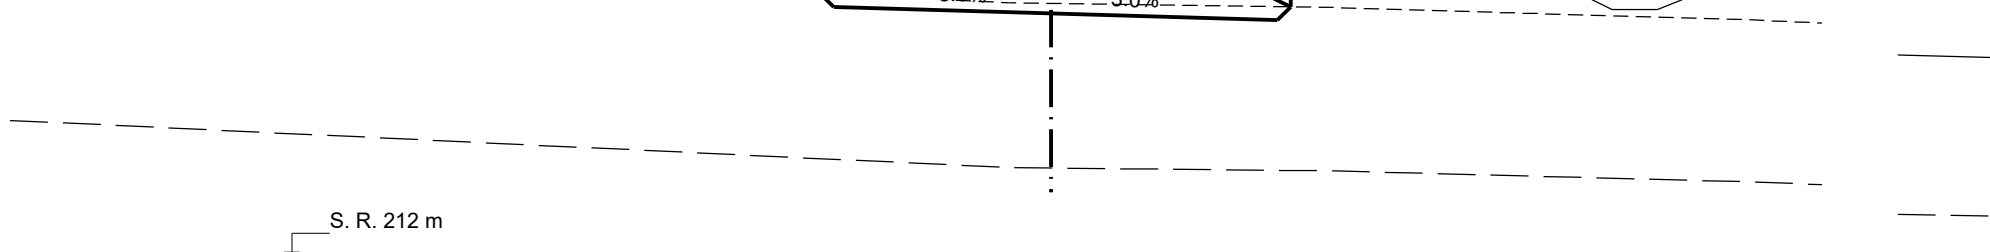


PROJEKTOVANÝ STAV	S. R. 212 m
ODSAZENÍ OD OSY	-3.05 216.39 -2.00 216.34 -2.00 217.22 -1.75 216.36 -0.50 216.27 0.00 216.31 1.75 216.25 2.00 216.25 2.00 216.23 3.17 216.21
STÁVAJÍCÍ TERÉN	-0.50 216.27 0.00 216.26
ODSAZENÍ OD OSY	

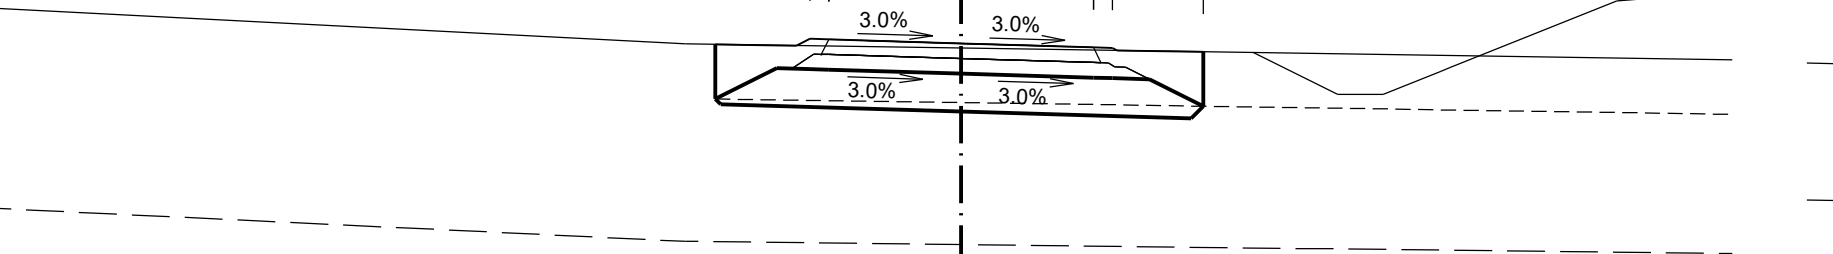


PROJEKTOVANÝ STAV	S. R. 212 m
ODSAZENÍ OD OSY	-3.20 215.62 -2.10 215.61 -2.00 215.70 -1.75 215.89 0.00 215.64 1.75 215.58 2.00 215.54 2.00 215.54 3.21 215.53
STÁVAJÍCÍ TERÉN	-3.65 215.63 0.00 215.57
ODSAZENÍ OD OSY	

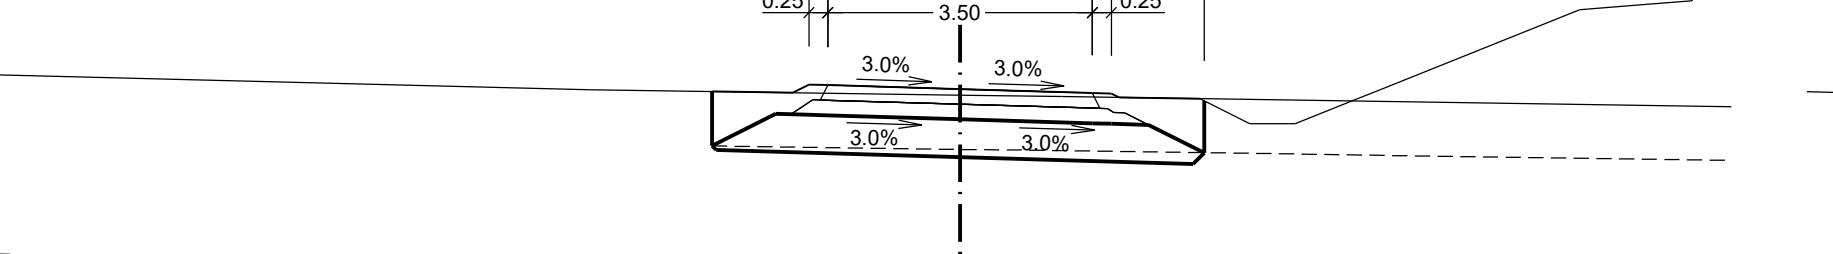


PROJEKTOVANÝ STAV	S. R. 212 m
ODSAZENÍ OD OSY	-3.28 215.01 -2.22 215.00 -2.00 215.11 -1.75 215.10 0.00 215.05 1.75 214.98 2.00 214.98 2.10 214.93 3.23 214.92
STÁVAJÍCÍ TERÉN	-4.89 215.04 0.00 214.97
ODSAZENÍ OD OSY	

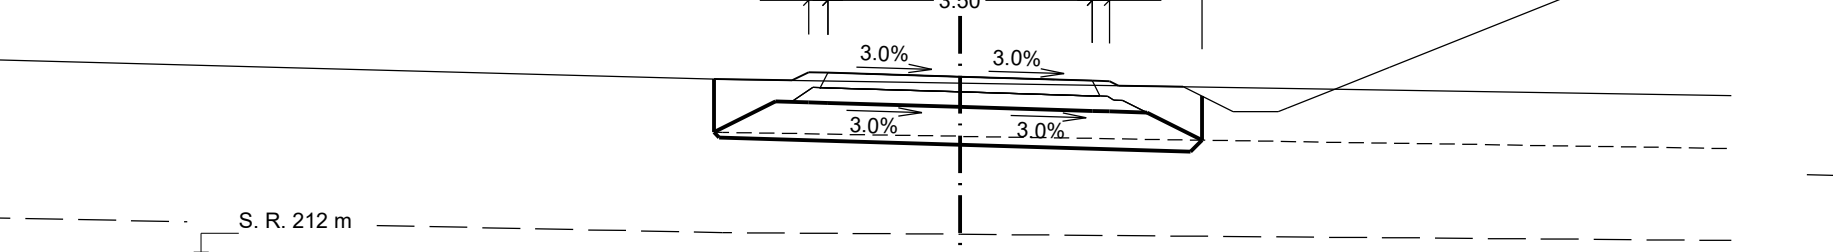


PROJEKTOVANÝ STAV	S. R. 212 m
ODSAZENÍ OD OSY	-3.14 214.54 -2.22 214.52 -2.00 214.63 -1.75 214.52 0.00 214.49 1.75 214.52 2.00 213.77 2.00 214.45 3.20 214.43
STÁVAJÍCÍ TERÉN	-3.14 214.54 0.00 214.49
ODSAZENÍ OD OSY	

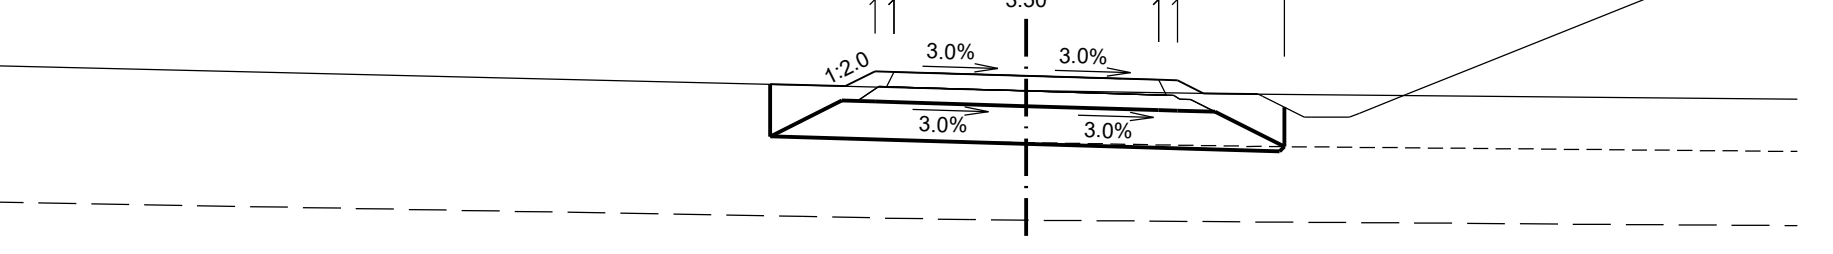


PROJEKTOVANÝ STAV	S. R. 211 m
ODSAZENÍ OD OSY	-3.30 214.10 -2.00 214.07 -2.00 214.26 -1.75 214.26 0.00 214.21 1.75 214.15 2.00 214.15 2.00 213.95 3.41 213.95
STÁVAJÍCÍ TERÉN	-2.97 214.09 -0.75 214.03 0.00 214.01
ODSAZENÍ OD OSY	

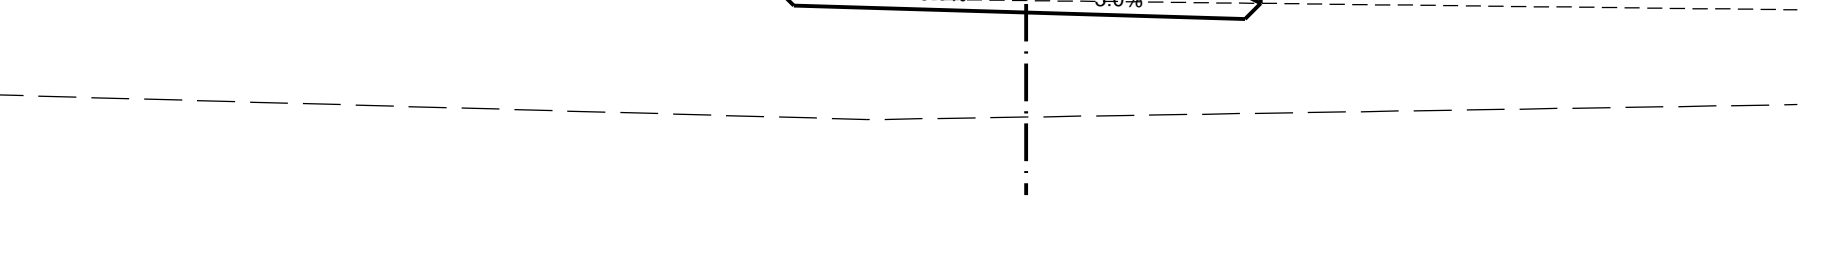


PROJEKTOVANÝ STAV	S. R. 209 m
ODSAZENÍ OD OSY	-3.18 213.95 -2.00 213.94 -2.00 213.25 -1.75 214.01 0.00 213.96 1.75 213.91 2.00 213.90 2.00 213.88 3.10 213.87
STÁVAJÍCÍ TERÉN	-2.12 213.93 0.00 213.91
ODSAZENÍ OD OSY	

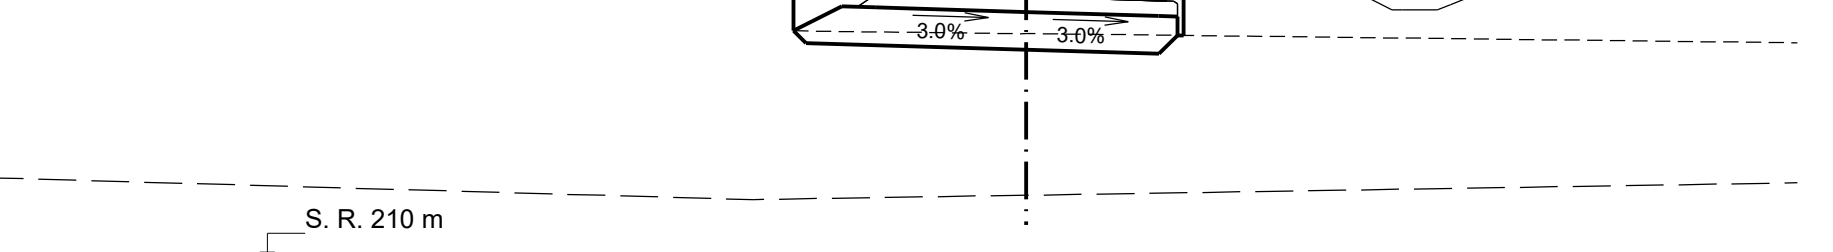


PROJEKTOVANÝ STAV	S. R. 210 m
ODSAZENÍ OD OSY	-3.00 213.97 -2.00 213.96 -2.00 213.77 -1.75 213.98 0.00 213.93 1.75 213.77 2.00 213.77 2.00 213.91 3.20 214.43
STÁVAJÍCÍ TERÉN	-3.00 213.96 0.00 213.93
ODSAZENÍ OD OSY	

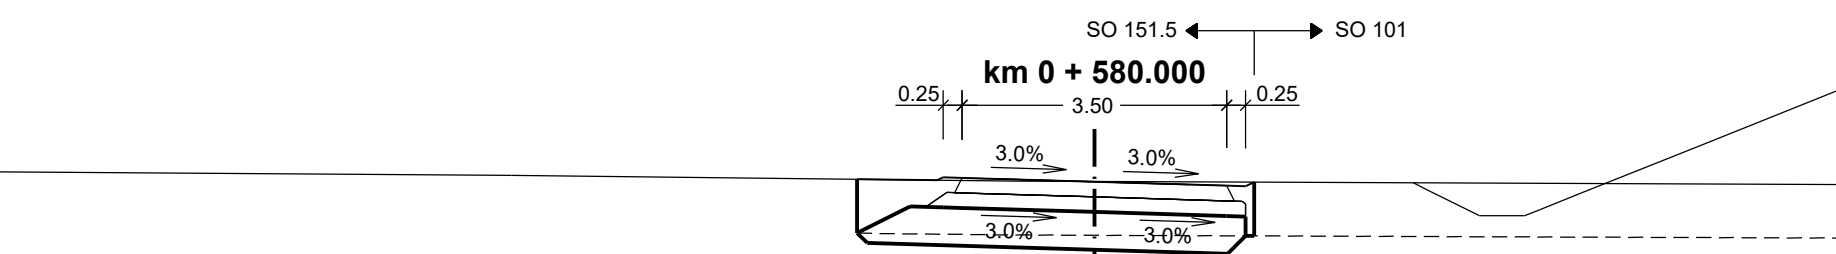


PROJEKTOVANÝ STAV	S. R. 212 m
ODSAZENÍ OD OSY	-3.14 213.84 -2.00 213.83 -2.00 213.87 -1.75 213.80 0.00 213.81 1.75 213.75 2.00 213.80 2.11 213.80
STÁVAJÍCÍ TERÉN	-2.71 213.88
ODSAZENÍ OD OSY	

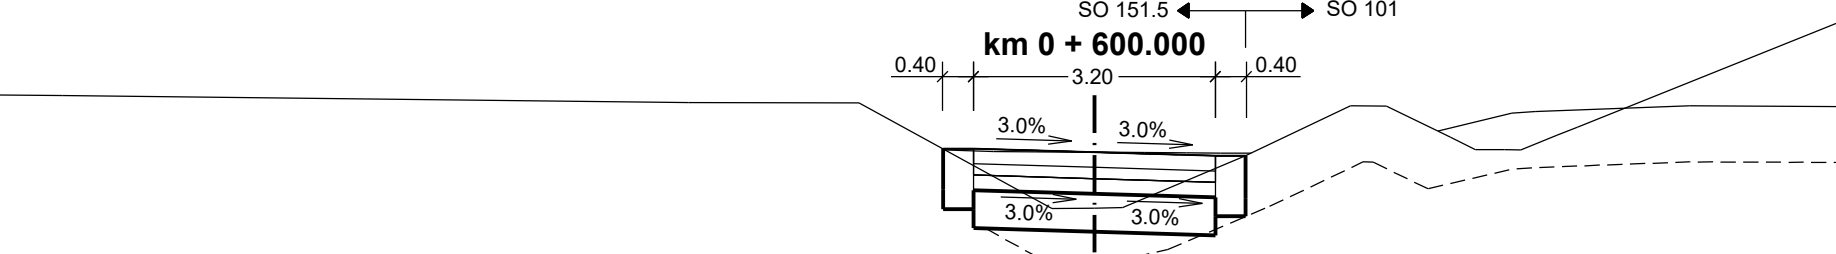


PROJEKTOVANÝ STAV	S. R. 211 m
ODSAZENÍ OD OSY	-2.48 213.02 -2.00 213.25 -2.00 213.25 -1.60 213.25 0.00 213.21 1.00 213.15 2.00 213.15 2.00 213.15 2.40 212.97
STÁVAJÍCÍ TERÉN	-5.36 213.87 -3.30 213.29 -0.50 212.46 0.00 212.46 5.52 213.73 5.50 213.73
ODSAZENÍ OD OSY	

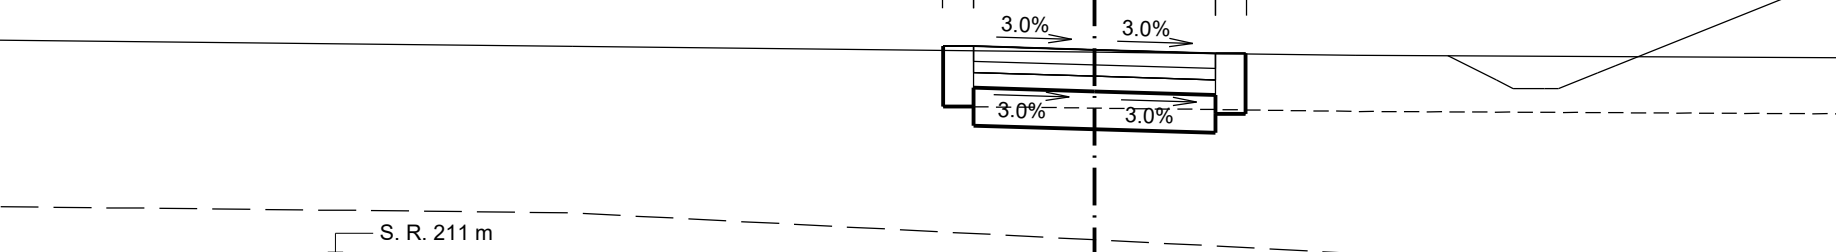


PROJEKTOVANÝ STAV	S. R. 211 m
ODSAZENÍ OD OSY	-2.12 213.02 -2.00 213.02 -2.00 213.02 -1.60 213.07 0.00 213.03 1.00 213.05 2.00 213.05 2.00 213.07 3.40 213.85
STÁVAJÍCÍ TERÉN	-4.89 213.97
ODSAZENÍ OD OSY	

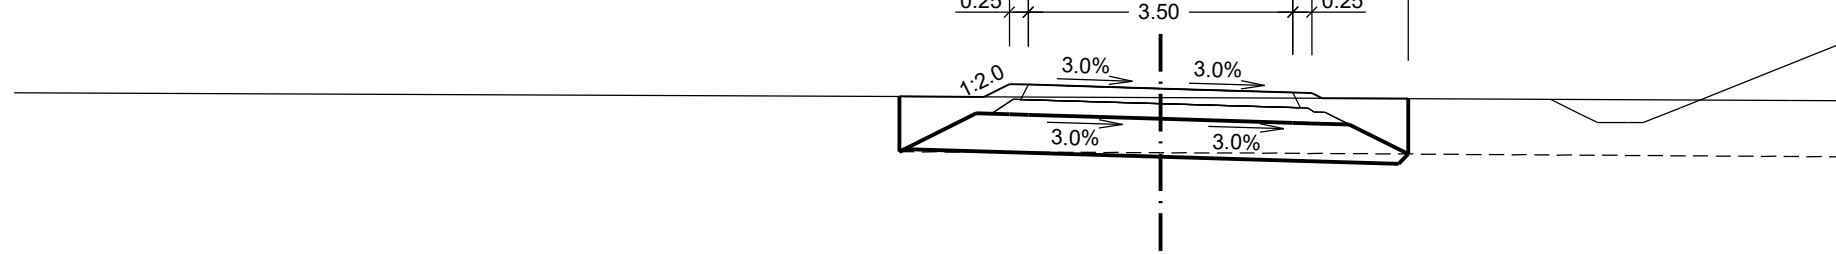


PROJEKTOVANÝ STAV	S. R. 211 m
ODSAZENÍ OD OSY	-3.42 213.93 -2.00 213.93 -2.00 214.09 -1.75 214.09 0.00 214.04 1.75 213.98 2.00 213.98 2.11 213.91 3.30 213.91
STÁVAJÍCÍ TERÉN	6.34 213.88
ODSAZENÍ OD OSY	

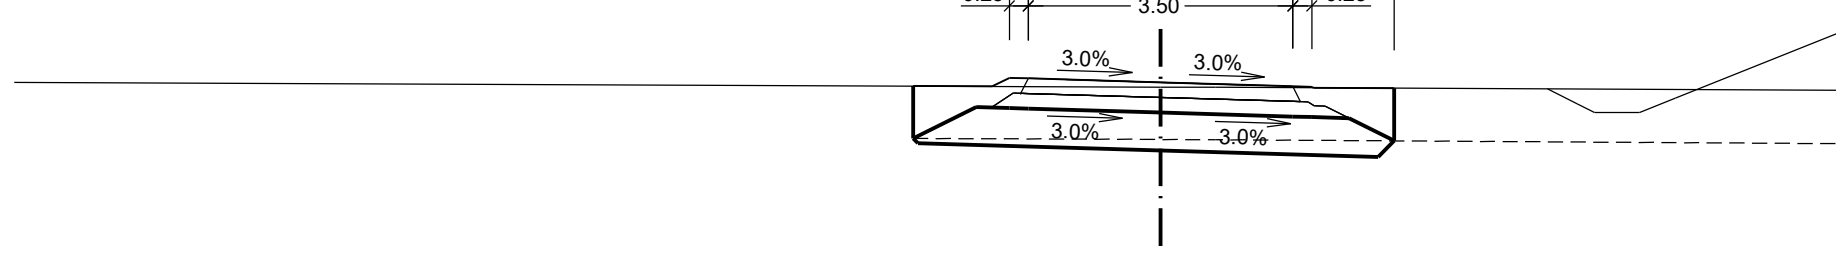


PROJEKTOVANÝ STAV	S. R. 211 m
ODSAZENÍ OD OSY	-3.27 214.09 -2.00 214.08 -2.00 214.08 -1.75 214.19 0.00 214.13 1.75 214.08 2.00 214.07 2.00 214.06 3.09 214.06
STÁVAJÍCÍ TERÉN	0.00 214.07 0.72 214.07
ODSAZENÍ OD OSY	

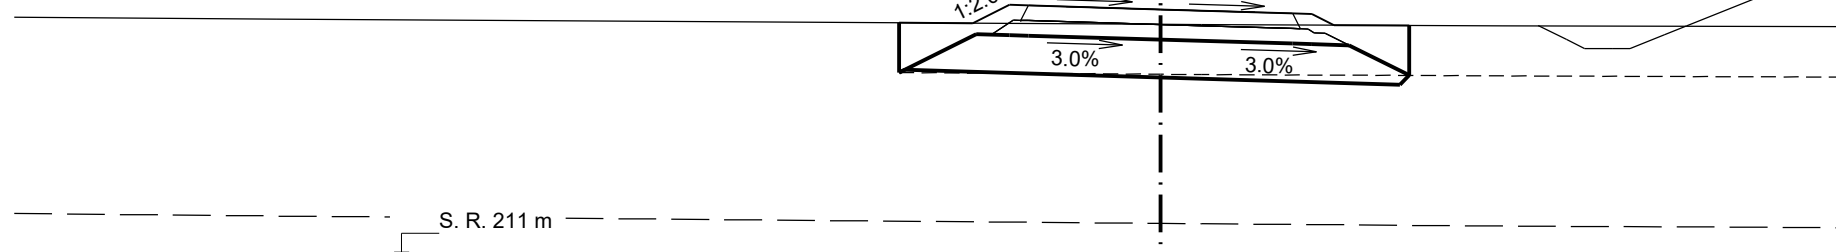


PROJEKTOVANÝ STAV	S. R. 211 m
ODSAZENÍ OD OSY	-3.46 214.28 -2.00 214.28 -2.00 214.28 -1.75 214.31 0.00 214.46 1.75 214.41 2.00 214.40 2.00 214.25 3.39 214.25
STÁVAJÍCÍ TERÉN	0.00 214.26 0.04 214.26
ODSAZENÍ OD OSY	

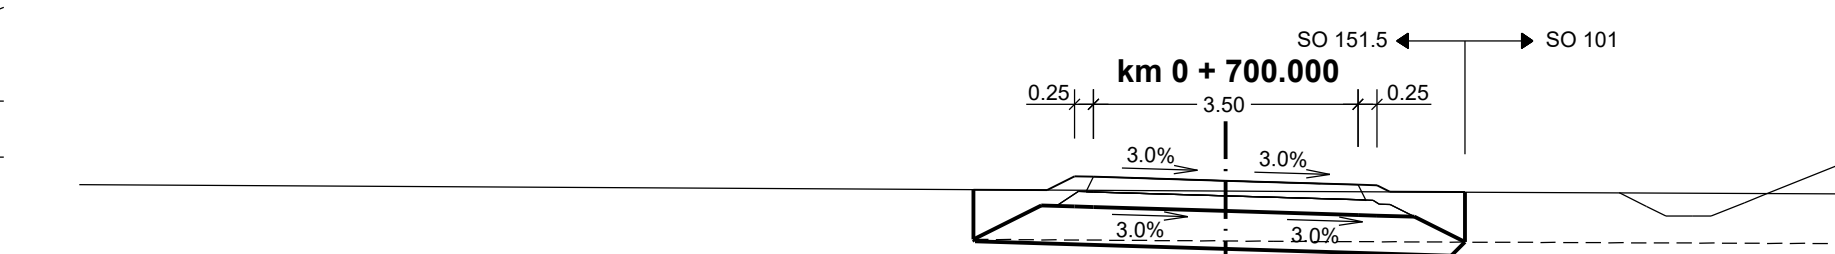

PROJEKTOVANÝ STAV	S. R. 213 m
ODSAZENÍ OD OSY	-3.30 214.70 -2.30 214.70 -2.00 214.68 -1.75 214.67 0.00 214.62 1.75 214.77 2.00 214.67 2.17 214.67 3.16 214.67
STÁVAJÍCÍ TERÉN	0.00 214.68 0.64 214.68
ODSAZENÍ OD OSY	

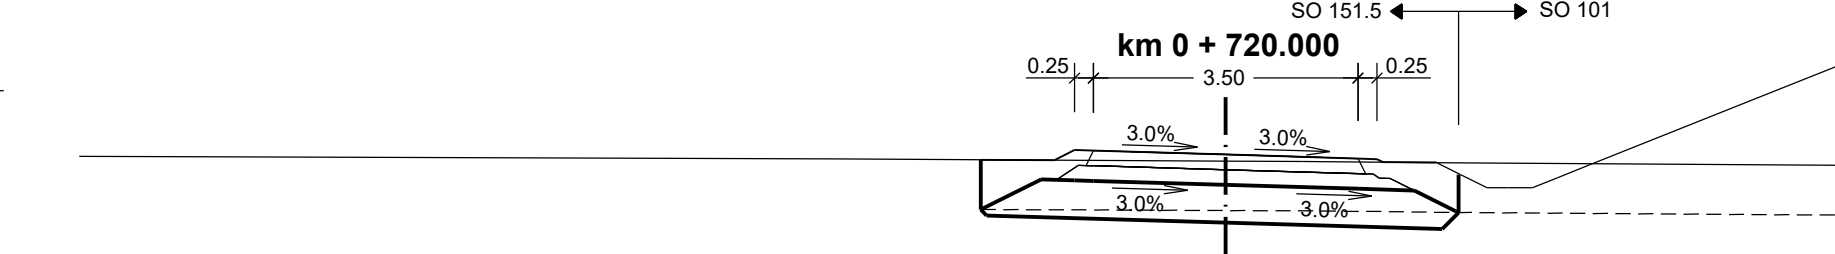

PROJEKTOVANÝ STAV	S. R. 213 m
ODSAZENÍ OD OSY	-3.24 215.11 -2.27 215.11 -2.00 215.24 -1.75 215.24 0.00 215.18 1.75 215.13 2.00 215.08 2.00 215.08 3.08 215.07
STÁVAJÍCÍ TERÉN	-5.11 215.12 0.00 215.09 1.02 215.08
ODSAZENÍ OD OSY	

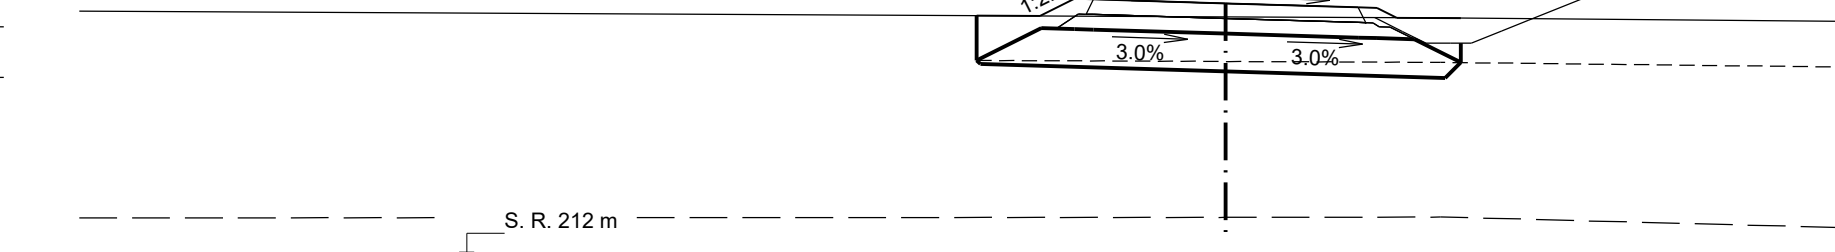

PROJEKTOVANÝ STAV	S. R. 212 m
ODSAZENÍ OD OSY	-3.29 215.36 -2.46 215.37 -2.00 215.60 -1.75 215.39 0.00 215.34 1.75 215.49 2.00 215.49 2.00 215.35 3.11 215.34
STÁVAJÍCÍ TERÉN	0.00 215.36 2.84 215.35
ODSAZENÍ OD OSY	

Výškový systém: BpV

SO 151 Přístupy na pozemky k.ú. Plazy

Objednatel: Ředitelství silnic a dálnic
Ředitelství silnic a dálnic s. p.
Čerčanská 203/12, Krč, 140 00 Praha 4

Zhotovitel: Valbek
Valbek, spol. s r.o.
Vaňurova 505/17
460 07 Liberec 3

Valbek	Vypracoval: P. BARTUSEK Zodp. projektant: ING. T. KLIMENT Tech. kontrola: ING. M. HANŽL	Zak. číslo: 21-L13-001 Datum: 02/2025 Stupeň: PDPS Počet formátů: 20 x A4 Měřítko: 1:100 Č. přílohy: Paré
Zhotovitel: Valbek, spol. s r.o. Vaňurova 505/17 460 07 Liberec 3	Příloha: PŘÍČNÉ ŘEZY SO 151.5 - km 0,340 - 0,740	5.5.1