




SO 151 - PŘÍSTUPY NA POZEMKY K.Ú. PLAZY
PŘÍČNÉ ŘEZY SO 151.5 - km 0,760 - 1,140, M 1 : 100

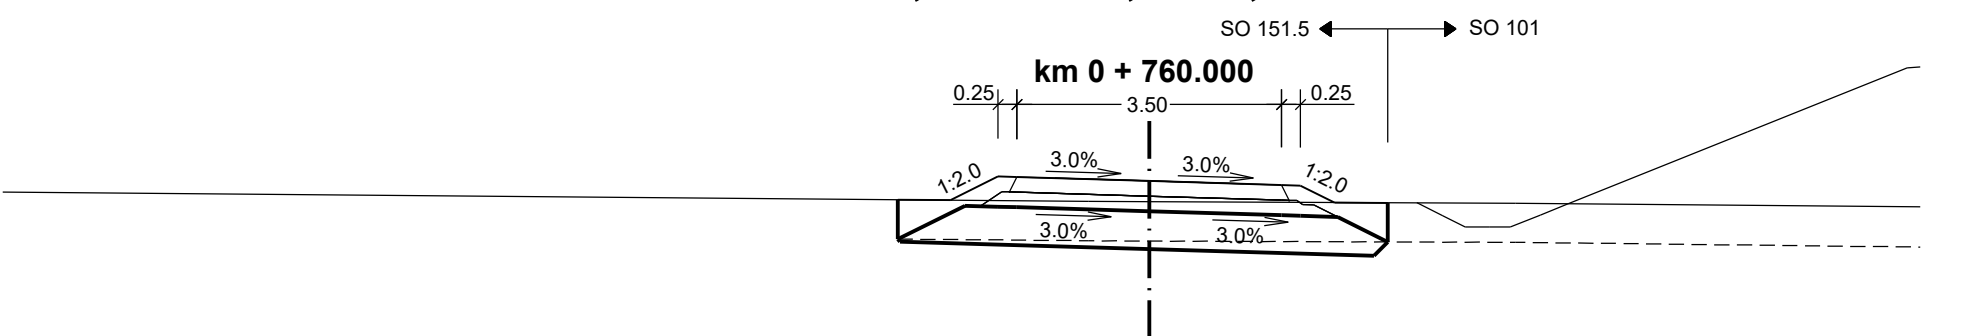


PROJEKTOVANÝ STAV	
ODSAZENÍ OD OSY	-3.33 215.65 -2.63 215.65 -2.00 215.96 -1.75 215.95 -0.81 215.93 0.00 215.90 1.75 215.85 2.00 215.84 2.54 215.81 3.16 215.61 4.85 215.60
STÁVAJÍCÍ TERÉN	
ODSAZENÍ OD OSY	

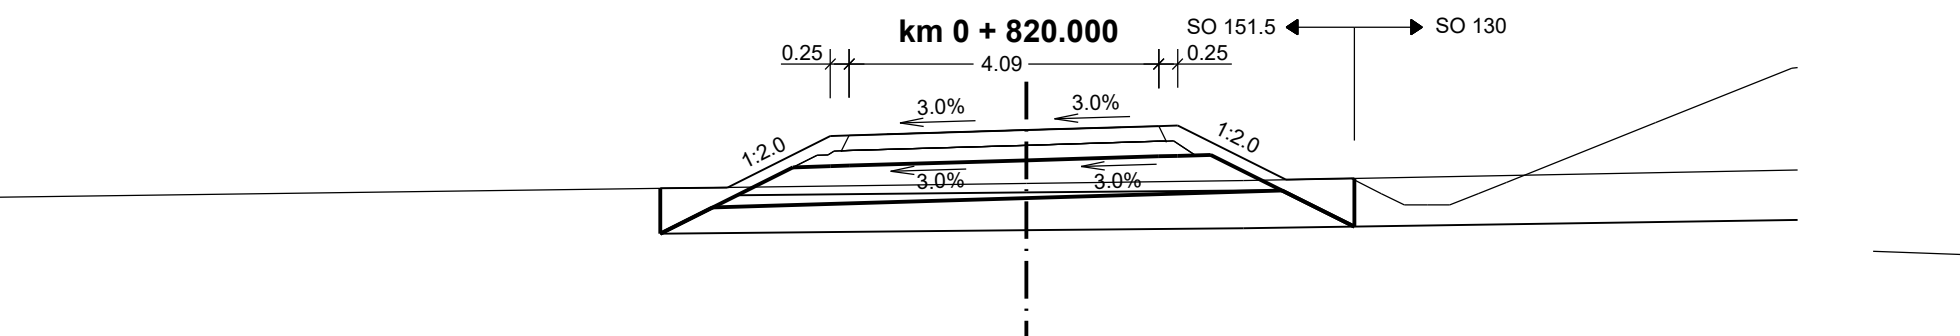


PROJEKTOVANÝ STAV	
ODSAZENÍ OD OSY	-4.84 216.60 -3.86 216.81 -2.89 217.45 -2.34 217.90 0.00 217.57 1.75 217.03 2.00 217.03 2.54 216.92 3.16 216.92 4.85 216.93
STÁVAJÍCÍ TERÉN	
ODSAZENÍ OD OSY	

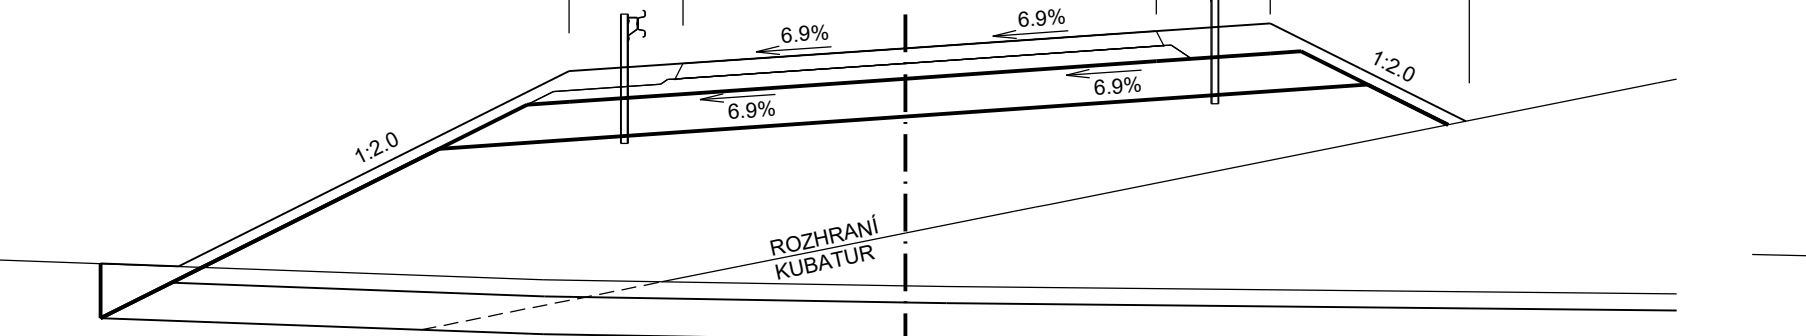


PROJEKTOVANÝ STAV	
ODSAZENÍ OD OSY	-9.02 218.77 -4.45 221.35 -2.85 221.46 0.00 221.65 3.32 221.88 4.83 221.98 6.02 221.39 7.20 218.56
STÁVAJÍCÍ TERÉN	
ODSAZENÍ OD OSY	

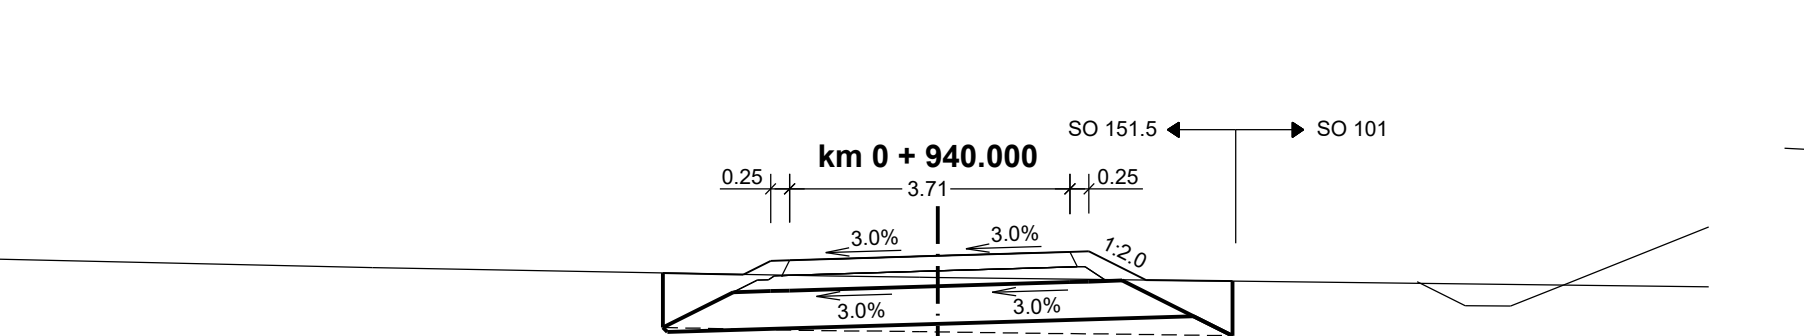


PROJEKTOVANÝ STAV	
ODSAZENÍ OD OSY	-3.84 218.68 -2.87 218.45 -2.21 218.84 -1.86 218.85 0.00 218.91 1.75 218.96 2.00 218.97 2.54 218.59 3.16 218.56
STÁVAJÍCÍ TERÉN	
ODSAZENÍ OD OSY	

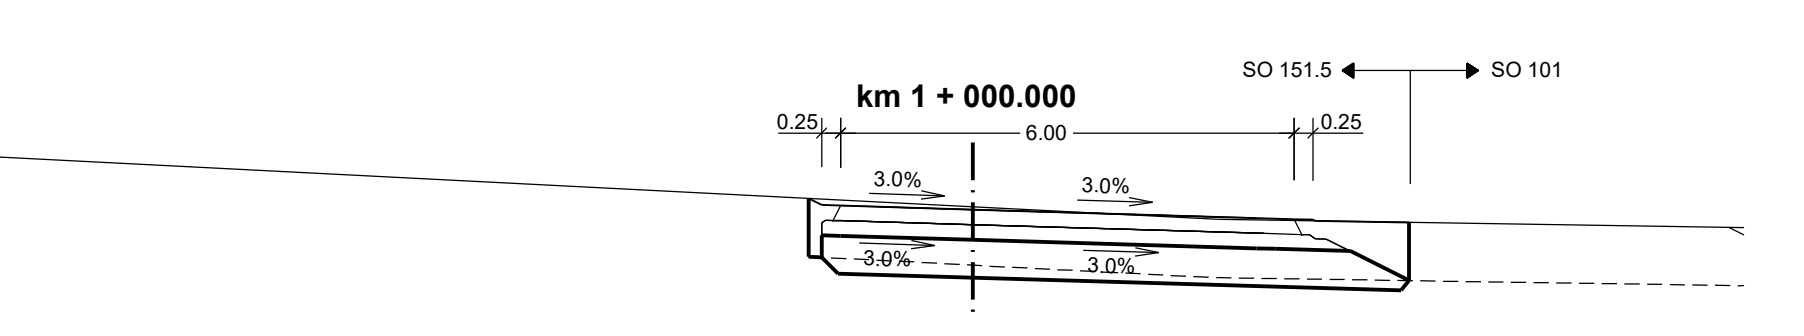


PROJEKTOVANÝ STAV	
ODSAZENÍ OD OSY	-2.17 221.67 -2.07 221.99 -2.00 221.99 -1.75 221.97 0.00 221.52 4.25 221.39 4.80 221.39 4.80 221.39 5.77 221.35 7.20 218.56
STÁVAJÍCÍ TERÉN	
ODSAZENÍ OD OSY	

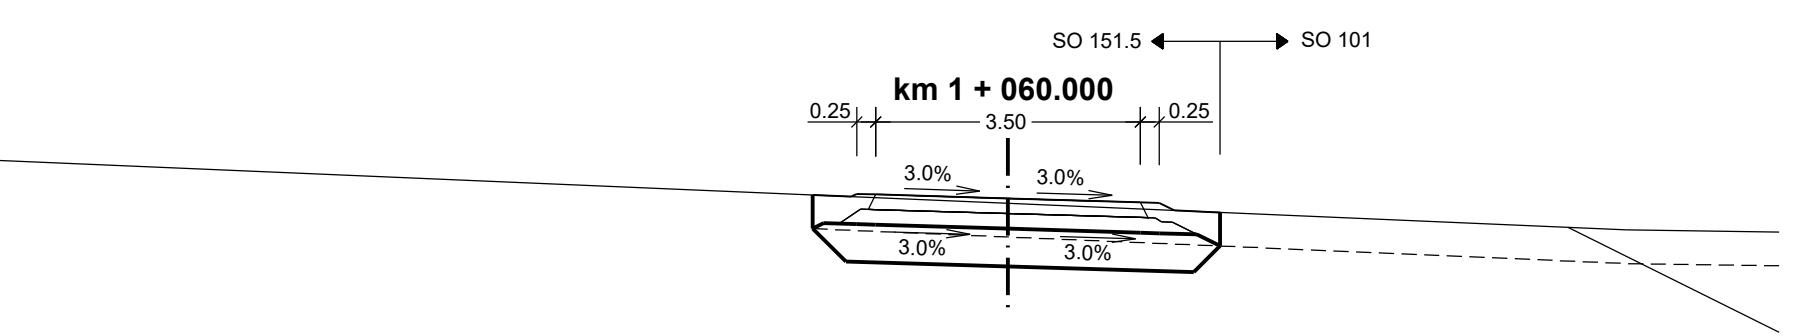


PROJEKTOVANÝ STAV	
ODSAZENÍ OD OSY	-2.85 225.71 -2.07 225.69 -2.00 225.73 -1.75 225.72 0.00 225.67 1.75 225.62 2.00 225.61 2.54 225.46 3.16 225.46 4.85 225.46
STÁVAJÍCÍ TERÉN	
ODSAZENÍ OD OSY	

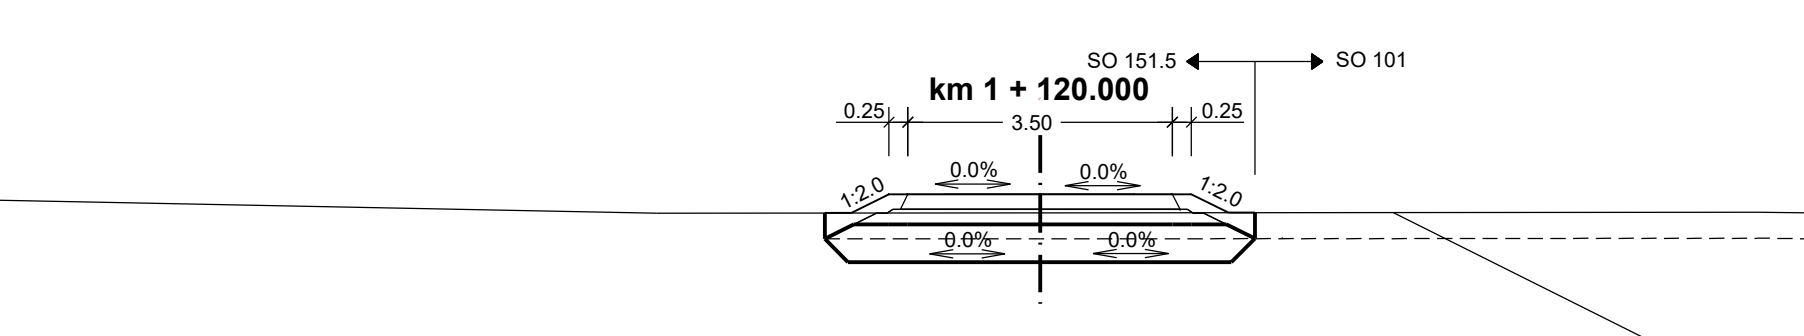


PROJEKTOVANÝ STAV	
ODSAZENÍ OD OSY	-2.85 226.46 -2.07 226.46 -2.00 226.73 -1.75 226.73 0.00 226.73 1.75 226.73 2.00 226.73 2.54 226.46 3.16 226.46 4.85 226.46
STÁVAJÍCÍ TERÉN	
ODSAZENÍ OD OSY	

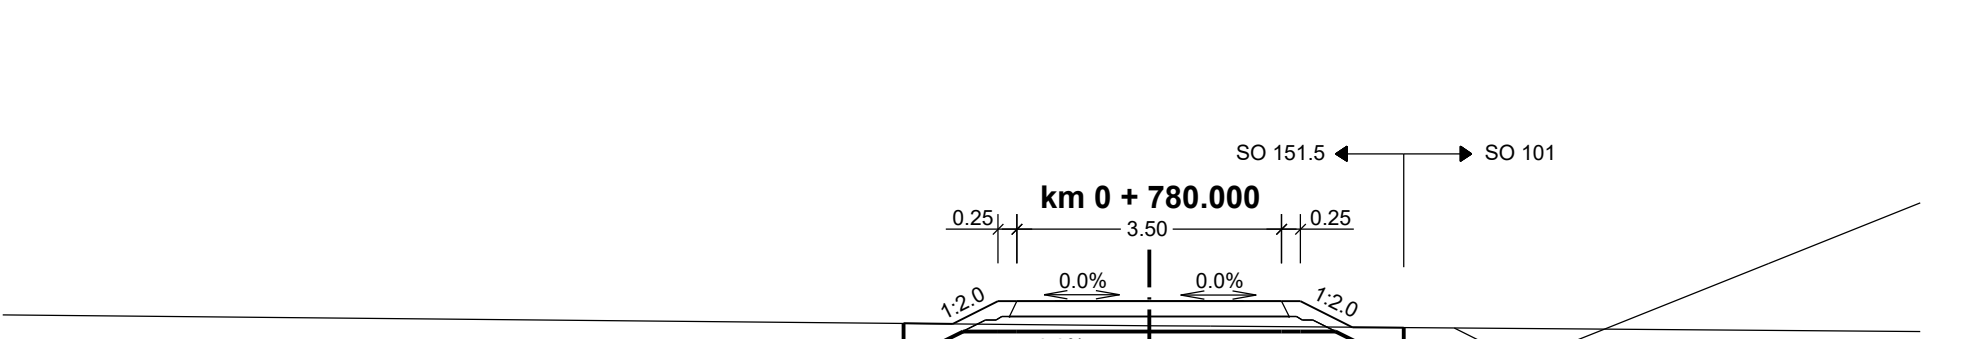


PROJEKTOVANÝ STAV	
ODSAZENÍ OD OSY	-3.25 215.97 -2.00 215.96 -1.75 216.28 0.00 216.28 1.75 216.28 2.00 216.28 2.54 215.92 3.16 215.91 4.85 215.90
STÁVAJÍCÍ TERÉN	
ODSAZENÍ OD OSY	

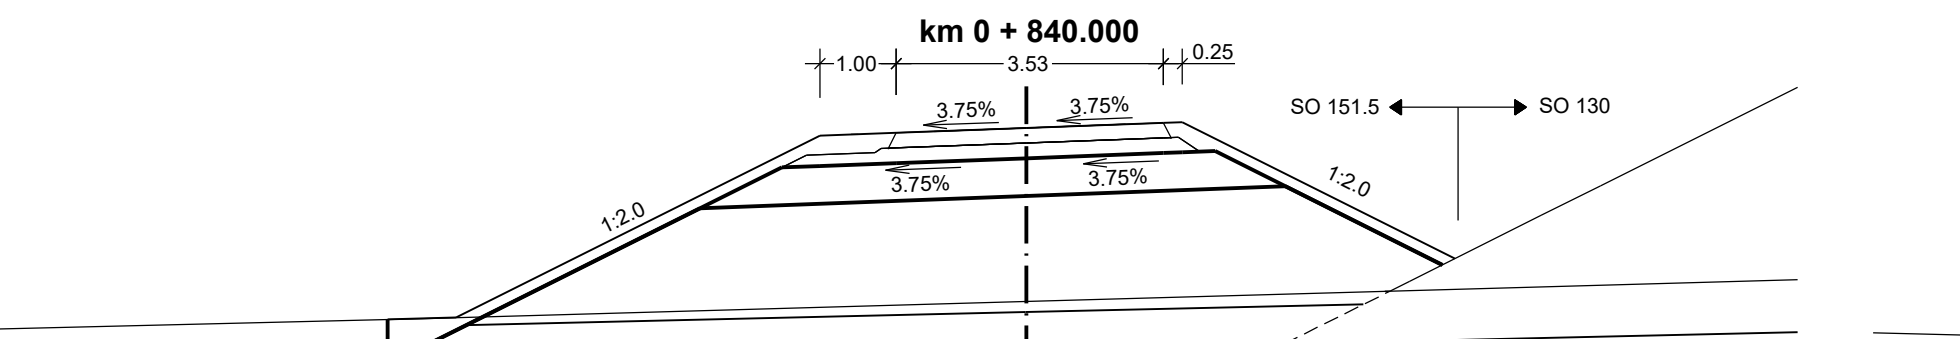


PROJEKTOVANÝ STAV	
ODSAZENÍ OD OSY	-8.45 217.02 -7.54 217.04 -2.73 219.45 -1.72 219.49 0.00 219.55 1.75 219.45 2.00 219.43 2.54 219.43 3.16 217.44 4.85 217.47
STÁVAJÍCÍ TERÉN	
ODSAZENÍ OD OSY	

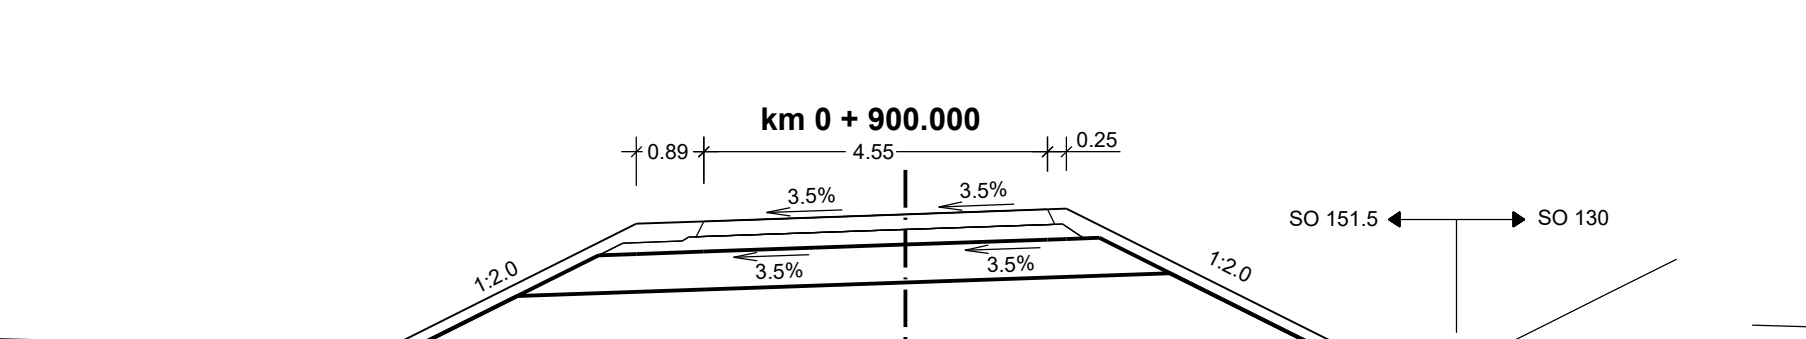


PROJEKTOVANÝ STAV	
ODSAZENÍ OD OSY	-7.92 218.66 -4.89 218.93 -3.56 220.28 -2.67 220.32 0.00 220.41 1.88 220.48 2.13 220.48 6.42 218.34 7.51 218.34
STÁVAJÍCÍ TERÉN	
ODSAZENÍ OD OSY	

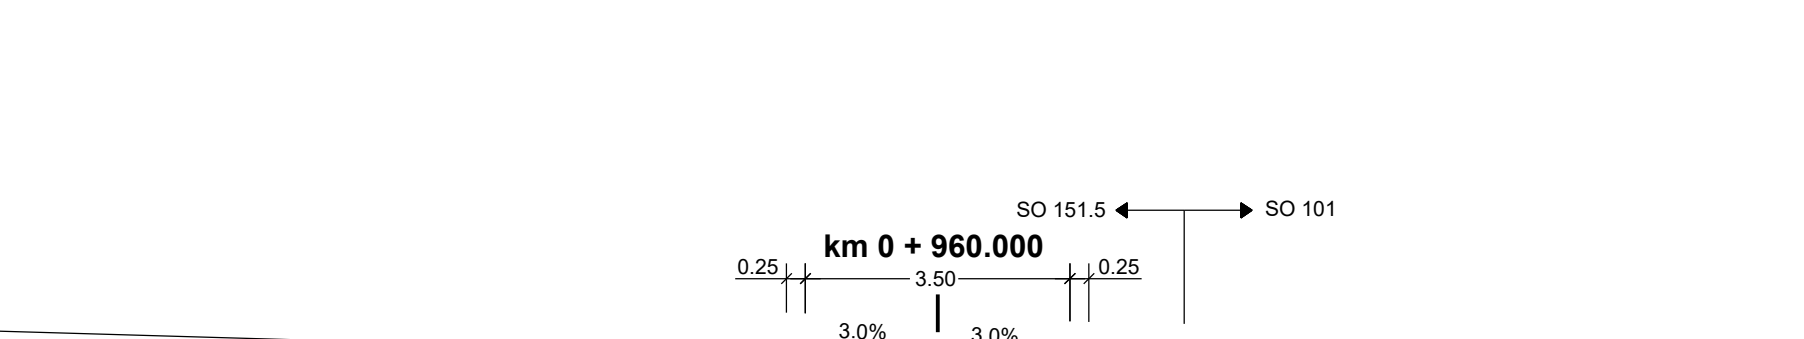


PROJEKTOVANÝ STAV	
ODSAZENÍ OD OSY	-3.18 219.60 -2.09 219.56 -2.00 219.60 -1.75 219.60 0.00 219.55 1.75 219.49 2.00 219.49 2.54 219.47 3.16 219.46
STÁVAJÍCÍ TERÉN	
ODSAZENÍ OD OSY	

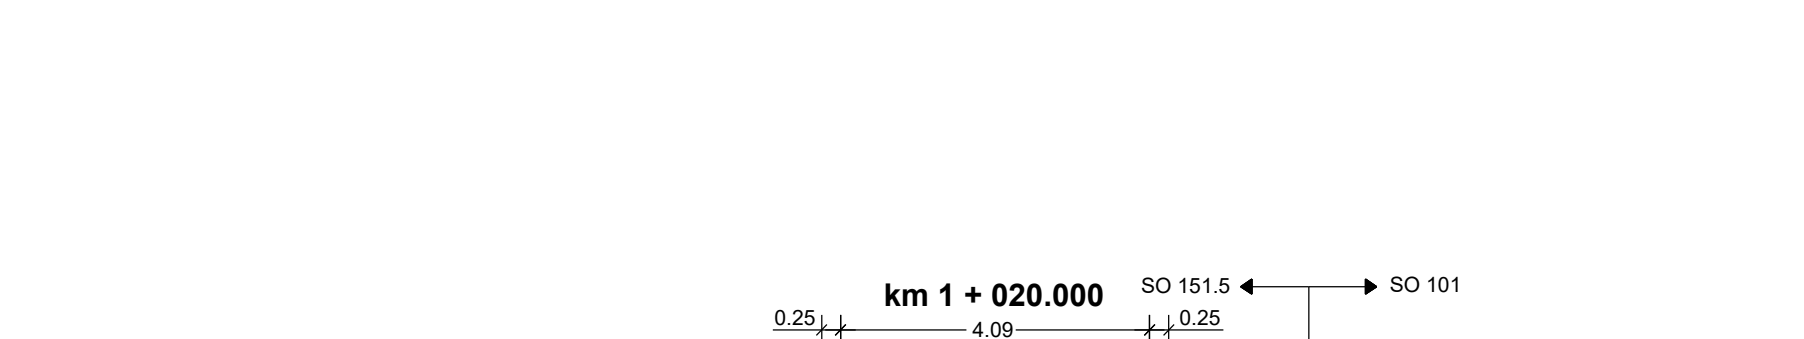


PROJEKTOVANÝ STAV	
ODSAZENÍ OD OSY	-2.42 222.82 -2.09 223.71 -2.00 223.83 -1.75 223.82 0.00 222.87 1.75 222.87 2.00 222.87 2.54 222.87 3.16 222.45 4.85 222.45
STÁVAJÍCÍ TERÉN	
ODSAZENÍ OD OSY	

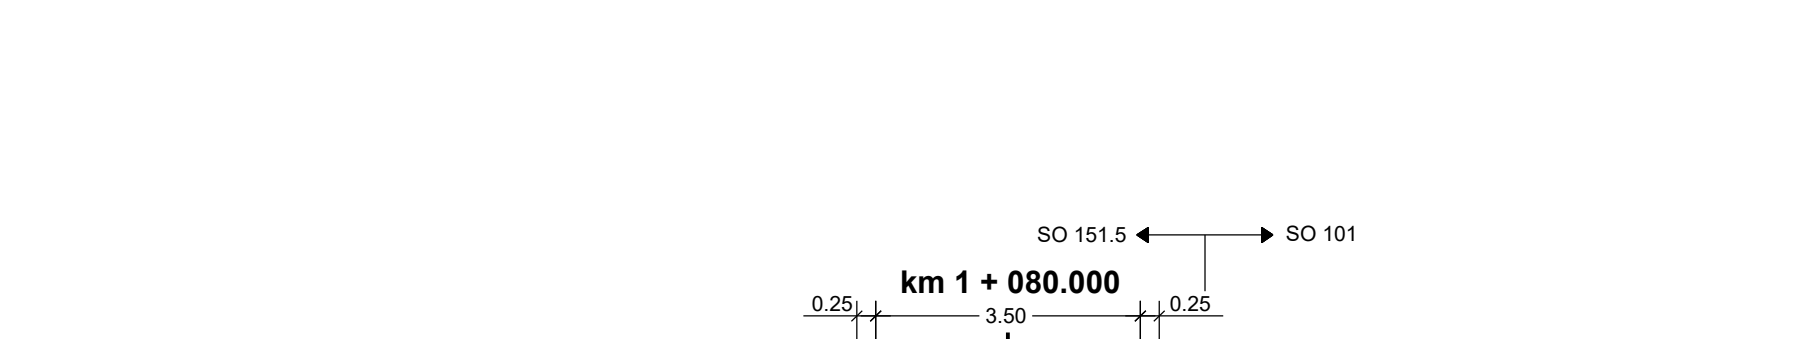


PROJEKTOVANÝ STAV	
ODSAZENÍ OD OSY	-2.42 227.08 -2.09 227.07 -2.00 228.83 -1.75 227.11 0.00 227.05 1.75 227.00 2.00 226.99 2.54 226.97 3.16 226.97 4.85 226.97
STÁVAJÍCÍ TERÉN	
ODSAZENÍ OD OSY	

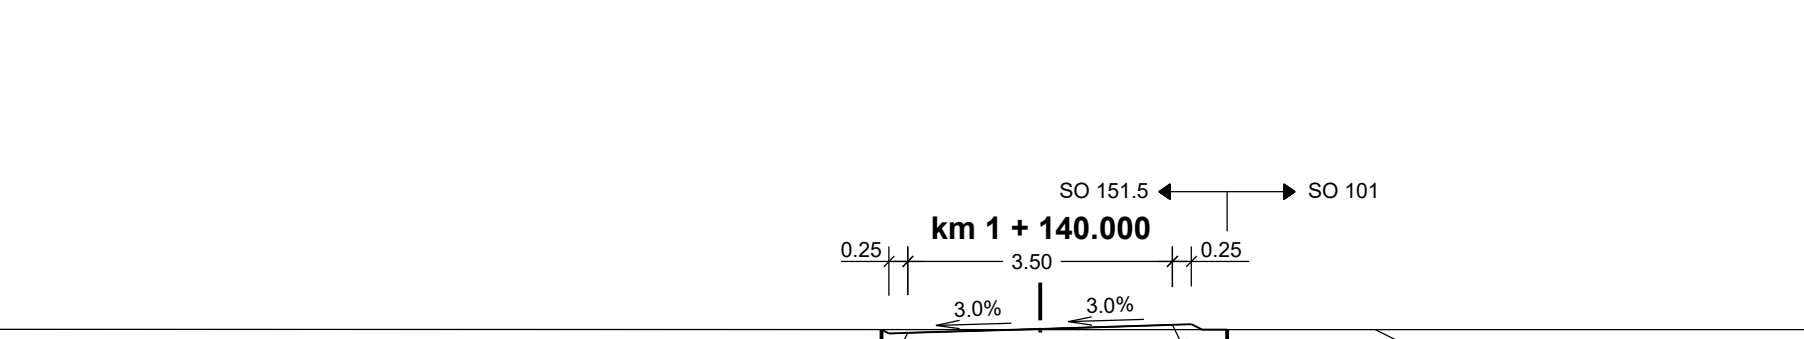


PROJEKTOVANÝ STAV	
ODSAZENÍ OD OSY	-2.10 226.89 -2.00 228.83 -1.75 226.84 0.00 226.89 1.75 226.85 2.00 226.85 2.54 226.85 3.16 226.85 4.85 226.85
STÁVAJÍCÍ TERÉN	
ODSAZENÍ OD OSY	

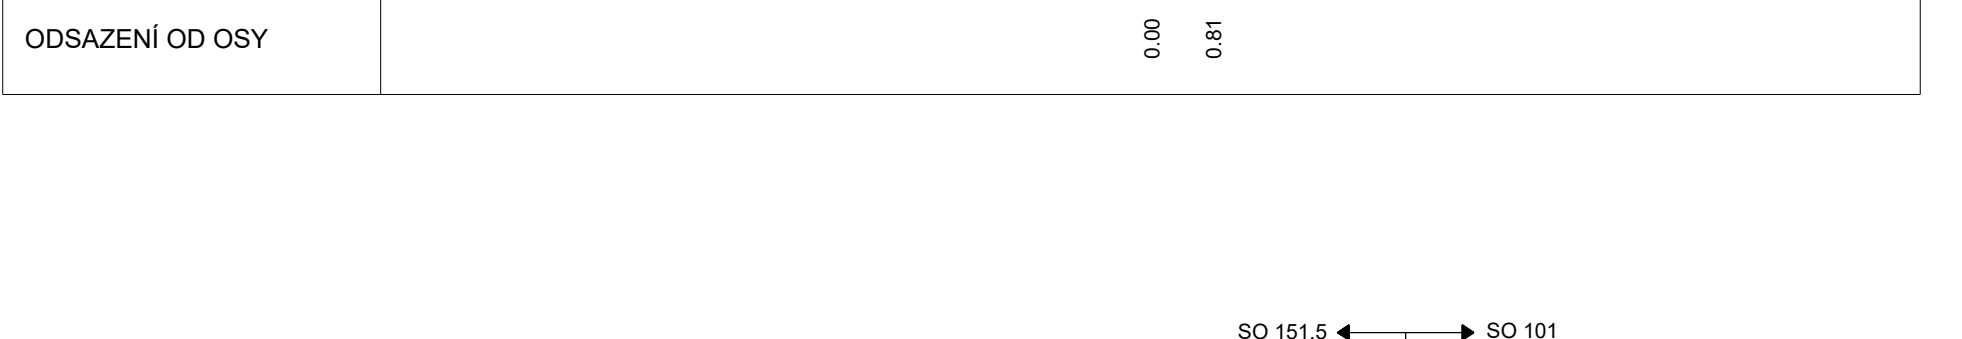


PROJEKTOVANÝ STAV	
ODSAZENÍ OD OSY	-3.47 216.35 -2.75 216.36 -2.00 216.35 -1.75 216.35 0.00 216.36 1.75 216.37 2.00 216.37 2.54 216.37 3.16 216.37 4.85 216.36
STÁVAJÍCÍ TERÉN	
ODSAZENÍ OD OSY	

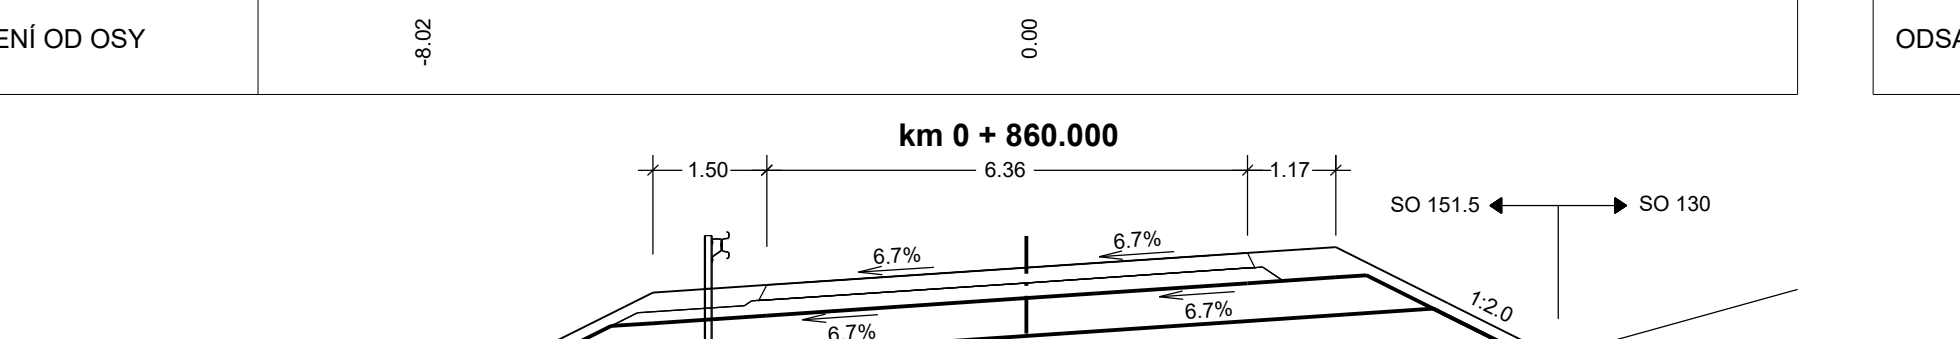


PROJEKTOVANÝ STAV	
ODSAZENÍ OD OSY	-4.31 220.71 -4.39 220.90 -3.43 221.00 0.00 221.22 2.39 221.42 4.09 221.49 5.59 220.75 7.51 218.17
STÁVAJÍCÍ TERÉN	
ODSAZENÍ OD OSY	

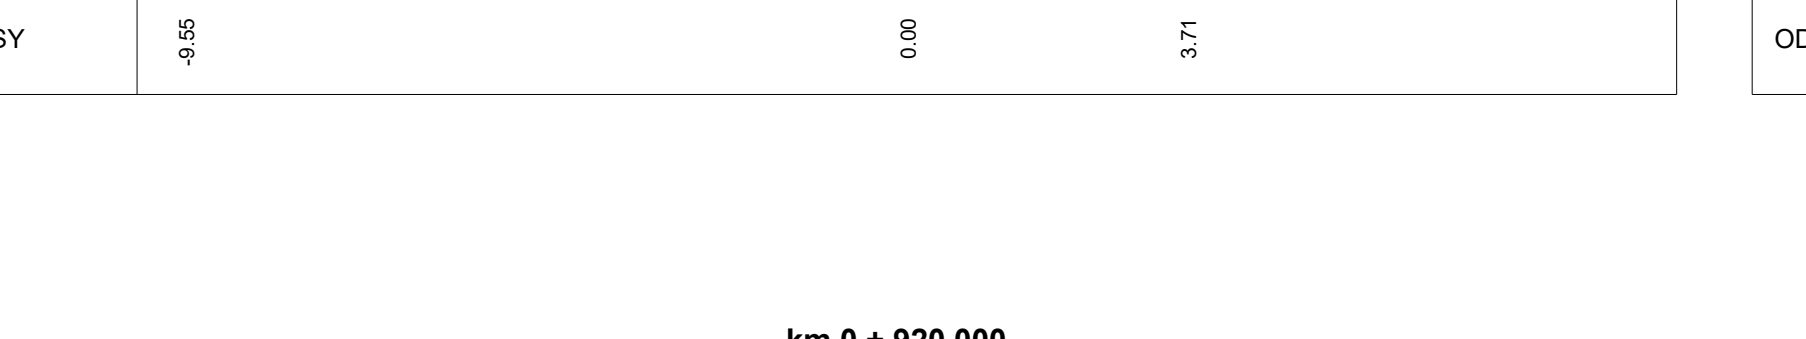

PROJEKTOVANÝ STAV	
ODSAZENÍ OD OSY	-4.59 216.45 -3.55 216.42 -2.75 216.83 -2.75 216.83 0.00 220.41 1.75 216.87 2.00 216.87 2.54 216.87 3.16 216.20 4.85 218.17
STÁVAJÍCÍ TERÉN	
ODSAZENÍ OD OSY	

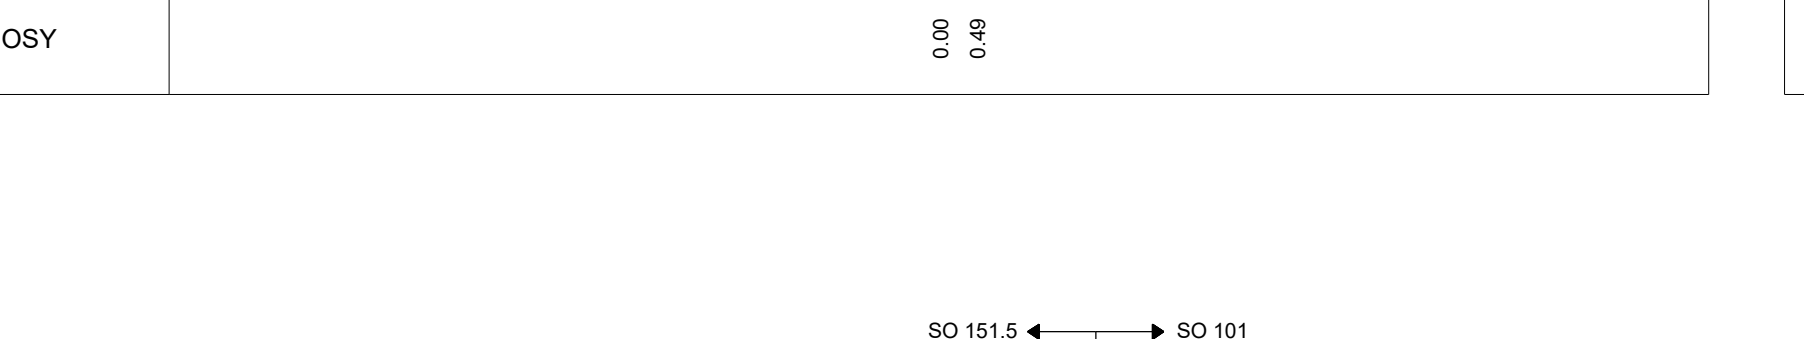


PROJEKTOVANÝ STAV	
ODSAZENÍ OD OSY	-2.05 220.49 -2.05 220.43 -1.75 220.46 0.00 220.41 1.75 220.36 2.00 220.35 2.54 220.35 3.16 220.36 4.85 220.36
STÁVAJÍCÍ TERÉN	
ODSAZENÍ OD OSY	

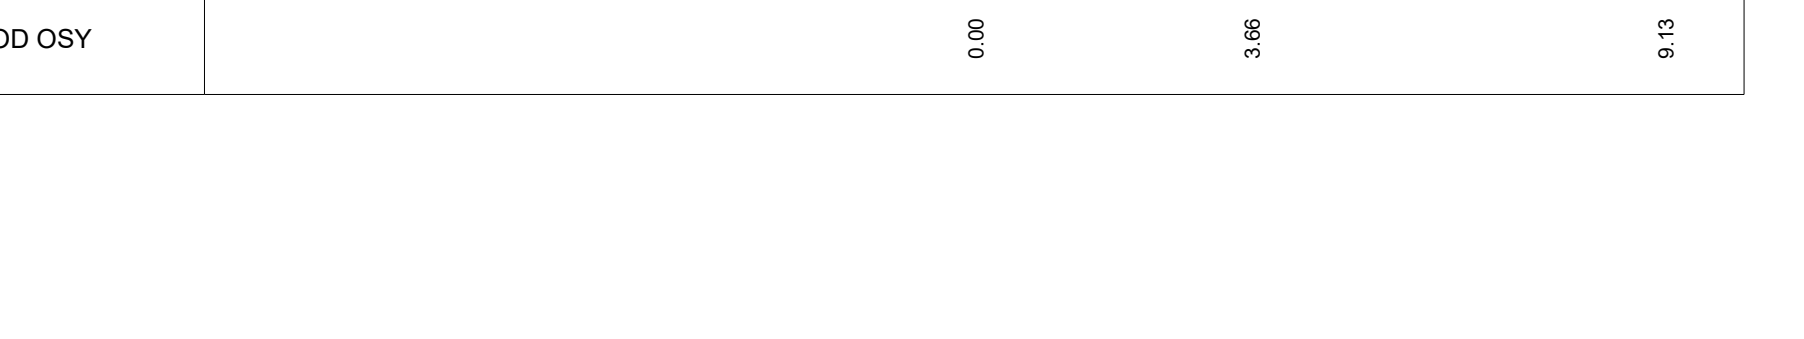

PROJEKTOVANÝ STAV	
ODSAZENÍ OD OSY	-3.21 224.18 -3.37 224.14 -2.50 224.33 -1.75 224.32 0.00 224.27 1.75 224.22 2.00 224.22 2.54 223.95 3.16 223.89 4.85 223.80
STÁVAJÍCÍ TERÉN	
ODSAZENÍ OD OSY	



PROJEKTOVANÝ STAV	
ODSAZENÍ OD OSY	-2.05 228.20 -2.05 228.15 -1.75 228.15 0.00 228.11 1.75 228.06 2.00 228.05 2.54 228.07 3.16 227.83 4.85 227.83
STÁVAJÍCÍ TERÉN	
ODSAZENÍ OD OSY	

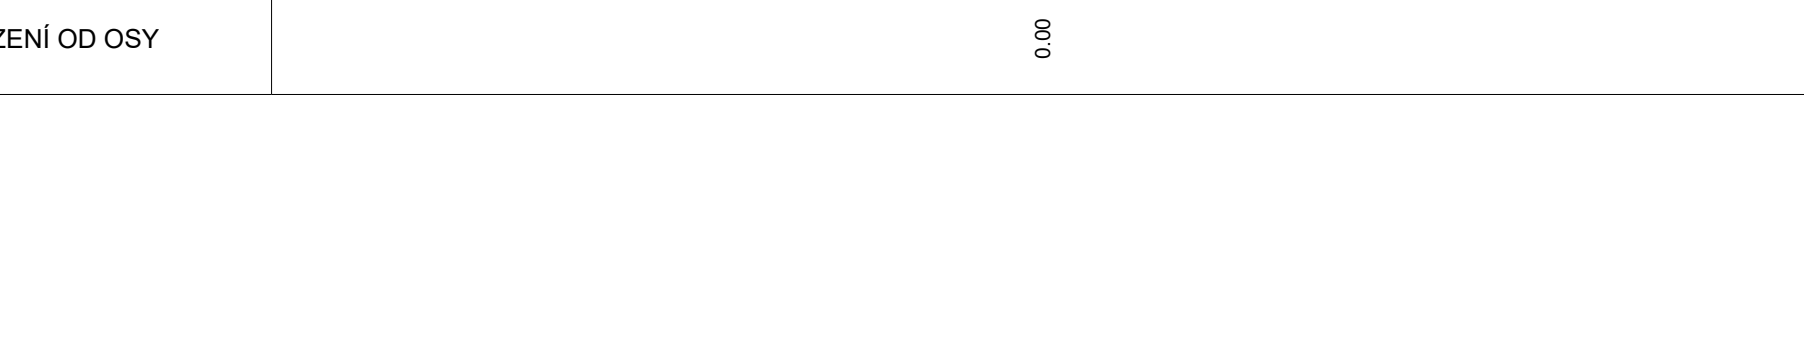


PROJEKTOVANÝ STAV	
ODSAZENÍ OD OSY	-2.05 228.20 -2.05 228.15 -1.75 228.15 0.00 228.11 1.75 228.06 2.00 228.05 2.54 228.07 3.16 227.83 4.85 227.83
STÁVAJÍCÍ TERÉN	
ODSAZENÍ OD OSY	

Výškový systém: Bpv

SO 151 Přístupy na pozemky k.ú. Plazy

Objednatel:

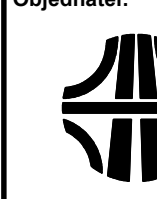

Ředitelství silnic a dálnic s. p.
Čerčanská 2023/12, Krč, 140 00 Praha 4

Zhotovitel:



Valbek, spol. s r.o.
Vaňurova 505/17
460 07 Liberec 3



Vypracoval: P. BARTUSEK
Zodp. projektant: ING. T. KLIMENT
Tech. kontrola: ING. M. HANŽL
I/16 MLADÁ BOLESLAV - MARTINOVICE

Zak. číslo: 21-LH13-001
Datum: 02/2025
Stupeň: PDP5
Počet formátů: 20 x A4
Měřítko: 1 : 100
Č. přílohy: Paré

Zhotovitel: Valbek, spol. s r.o.
Vaňurova 505/17
460 07 Liberec 3

Příloha: PŘÍČNÉ ŘEZY SO 151.5 - km 0,760 - 1,140

5.5.2