


SO 151 - PŘÍSTUPY NA POZEMKY k.ú. PLAZY
PODÉLNÝ PROFIL SO 151.2, M 1 : 1 000/100

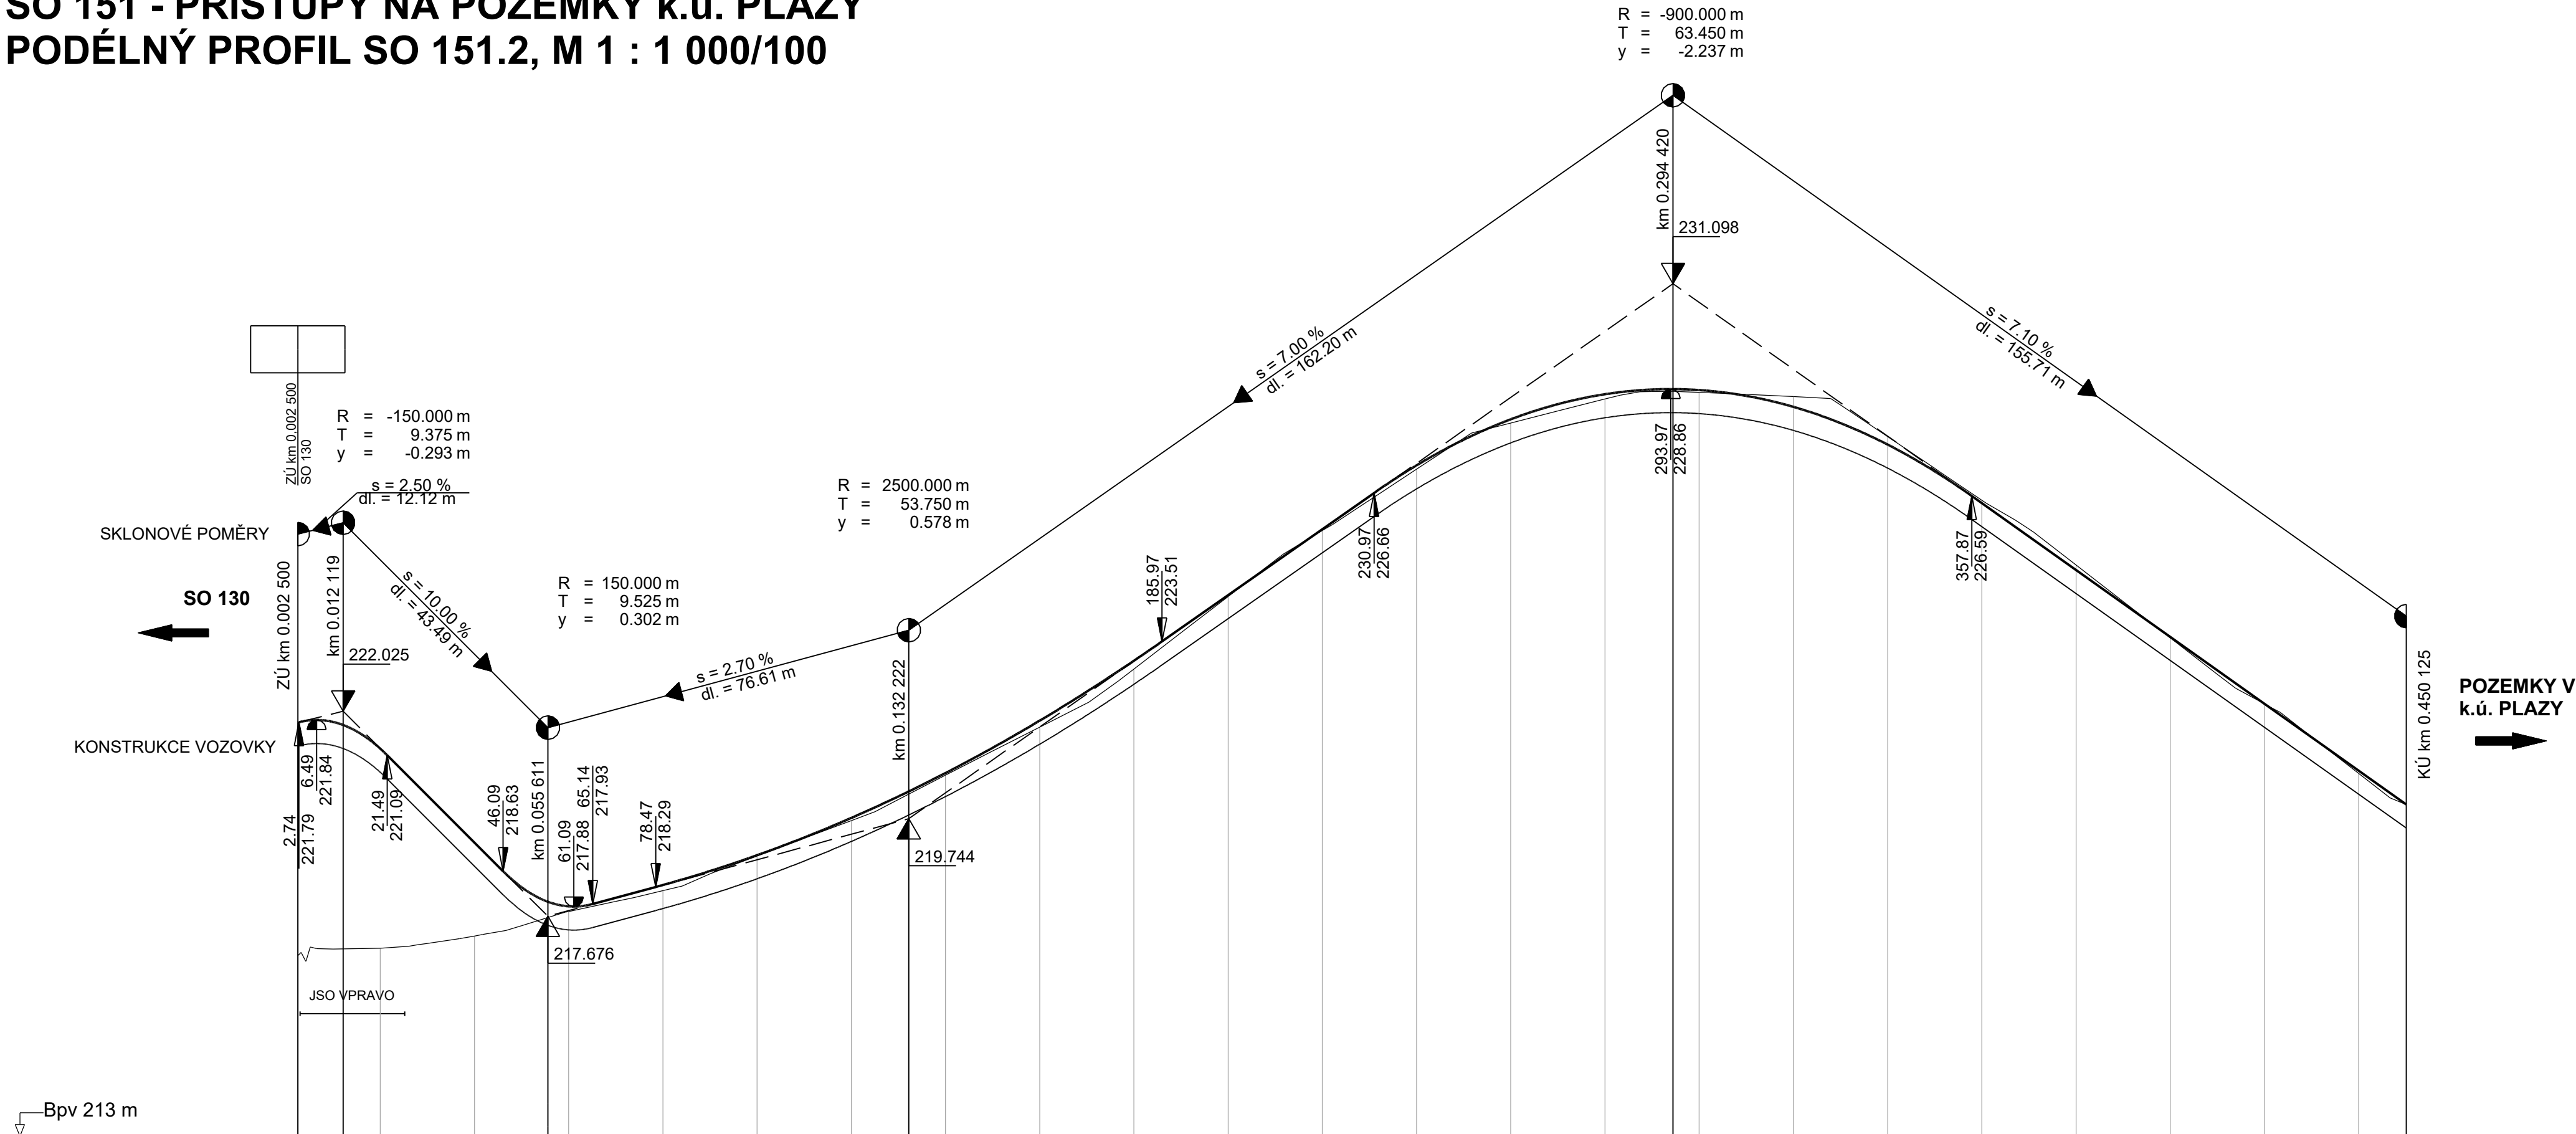

KÓTY NIVELETY	02.50	216.84	221.78	12.12	216.98	221.73	20.00	216.99	221.23	40.00	217.25	219.24	55.61	217.64	217.98	60.00	217.77	217.88	80.00	218.21	218.33	100.00	218.95	218.97	120.00	219.70	219.76	132.22	220.27	220.32	140.00	220.67	220.71	160.00	221.69	221.82	180.00	222.92	223.10	200.00	224.46	224.49	220.00	225.86	225.89	240.00	227.16	227.24	260.00	228.14	228.22	280.00	228.65	228.75	294.42	228.81	228.86	300.00	228.79	228.84	320.00	228.70	228.49	340.00	227.85	227.68	360.00	226.50	226.44	380.00	225.13	225.02	400.00	223.58	223.60	420.00	222.18	222.18	440.00	220.70	220.76	450.13	220.04	220.04
KÓTY TERÉNU	02.50	216.84	221.78	12.12	216.98	221.73	20.00	216.99	221.23	40.00	217.25	219.24	55.61	217.64	217.98	60.00	217.77	217.88	80.00	218.21	218.33	100.00	218.95	218.97	120.00	219.70	219.76	132.22	220.27	220.32	140.00	220.67	220.71	160.00	221.69	221.82	180.00	222.92	223.10	200.00	224.46	224.49	220.00	225.86	225.89	240.00	227.16	227.24	260.00	228.14	228.22	280.00	228.65	228.75	294.42	228.81	228.86	300.00	228.79	228.84	320.00	228.70	228.49	340.00	227.85	227.68	360.00	226.50	226.44	380.00	225.13	225.02	400.00	223.58	223.60	420.00	222.18	222.18	440.00	220.70	220.76	450.13	220.04	220.04
STANIČENÍ	02.50	216.84	221.78	12.12	216.98	221.73	20.00	216.99	221.23	40.00	217.25	219.24	55.61	217.64	217.98	60.00	217.77	217.88	80.00	218.21	218.33	100.00	218.95	218.97	120.00	219.70	219.76	132.22	220.27	220.32	140.00	220.67	220.71	160.00	221.69	221.82	180.00	222.92	223.10	200.00	224.46	224.49	220.00	225.86	225.89	240.00	227.16	227.24	260.00	228.14	228.22	280.00	228.65	228.75	294.42	228.81	228.86	300.00	228.79	228.84	320.00	228.70	228.49	340.00	227.85	227.68	360.00	226.50	226.44	380.00	225.13	225.02	400.00	223.58	223.60	420.00	222.18	222.18	440.00	220.70	220.76	450.13	220.04	220.04

km


0+000

0+100

0+200

0+300

0+400

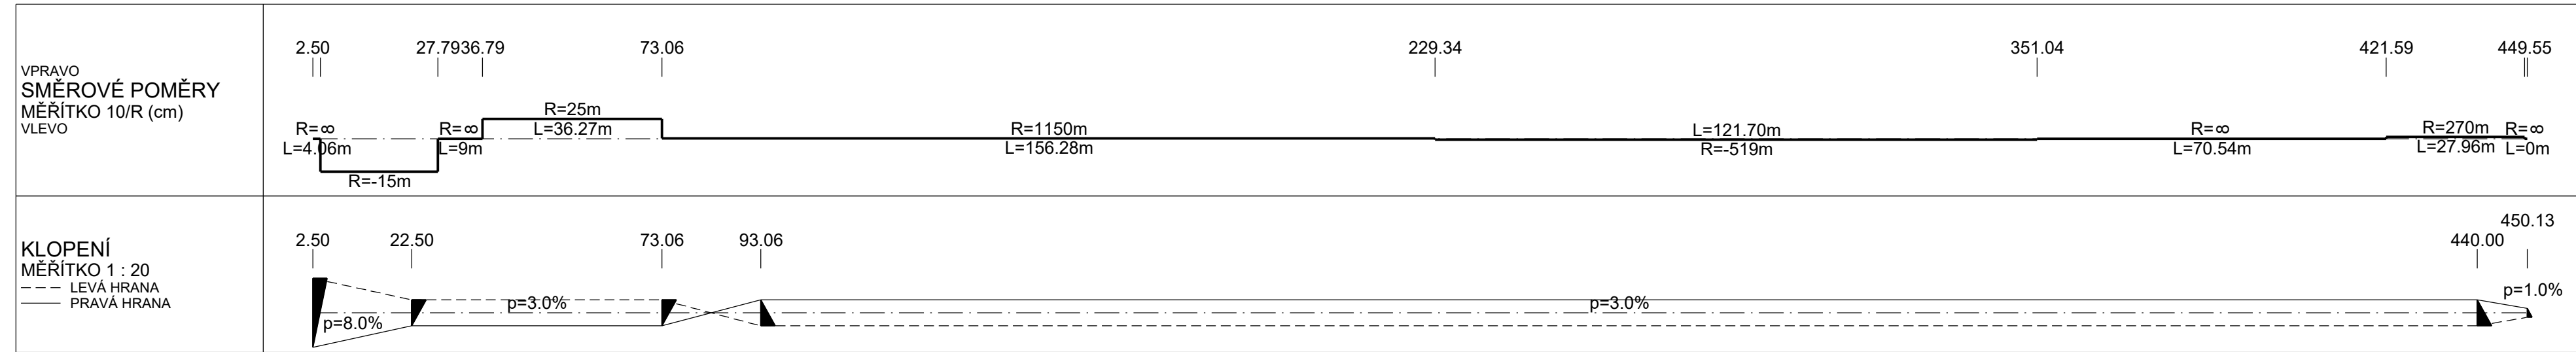

Výškový systém: Bpv

SO 151

Přístupy na pozemky k.ú. Plazy

Objednatel:



ŘEDITELSTVÍ
SILNIC
A DÁLNIC

Ředitelství silnic a dálnic s. p.
Čerčanská 2023/12, Krč, 140 00 Praha 4

Zhotovitel:



Valbek, spol. s r.o.

Vaňurova 505/17
460 07 Liberec 3



Vypracoval	P. BARTUSEK	Zak. číslo	21-LI13-001
Zodp. projektant	ING. T. KLIMENT	Datum	02/2025
Tech. kontrola	ING. M. HANŽL	Stupeň	PDPS
Akce	I/16 MLADÁ BOLESLAV - MARTINOVICE	Počet formátů	8 x A4
		Měřítko	1 : 1 000/100
Zhotovitel: Valbek, spol. s r.o. Vaňurova 505/17 460 07 Liberec 3	Příloha PODÉLNÝ PROFIL SO 151.2	Č. přílohy	Paré

3.2