


SO 151 - PŘÍSTUPY NA POZEMKY k.ú. PLAZY
PODÉLNÝ PROFIL SO 151.5, M 1 : 1 000 / 100

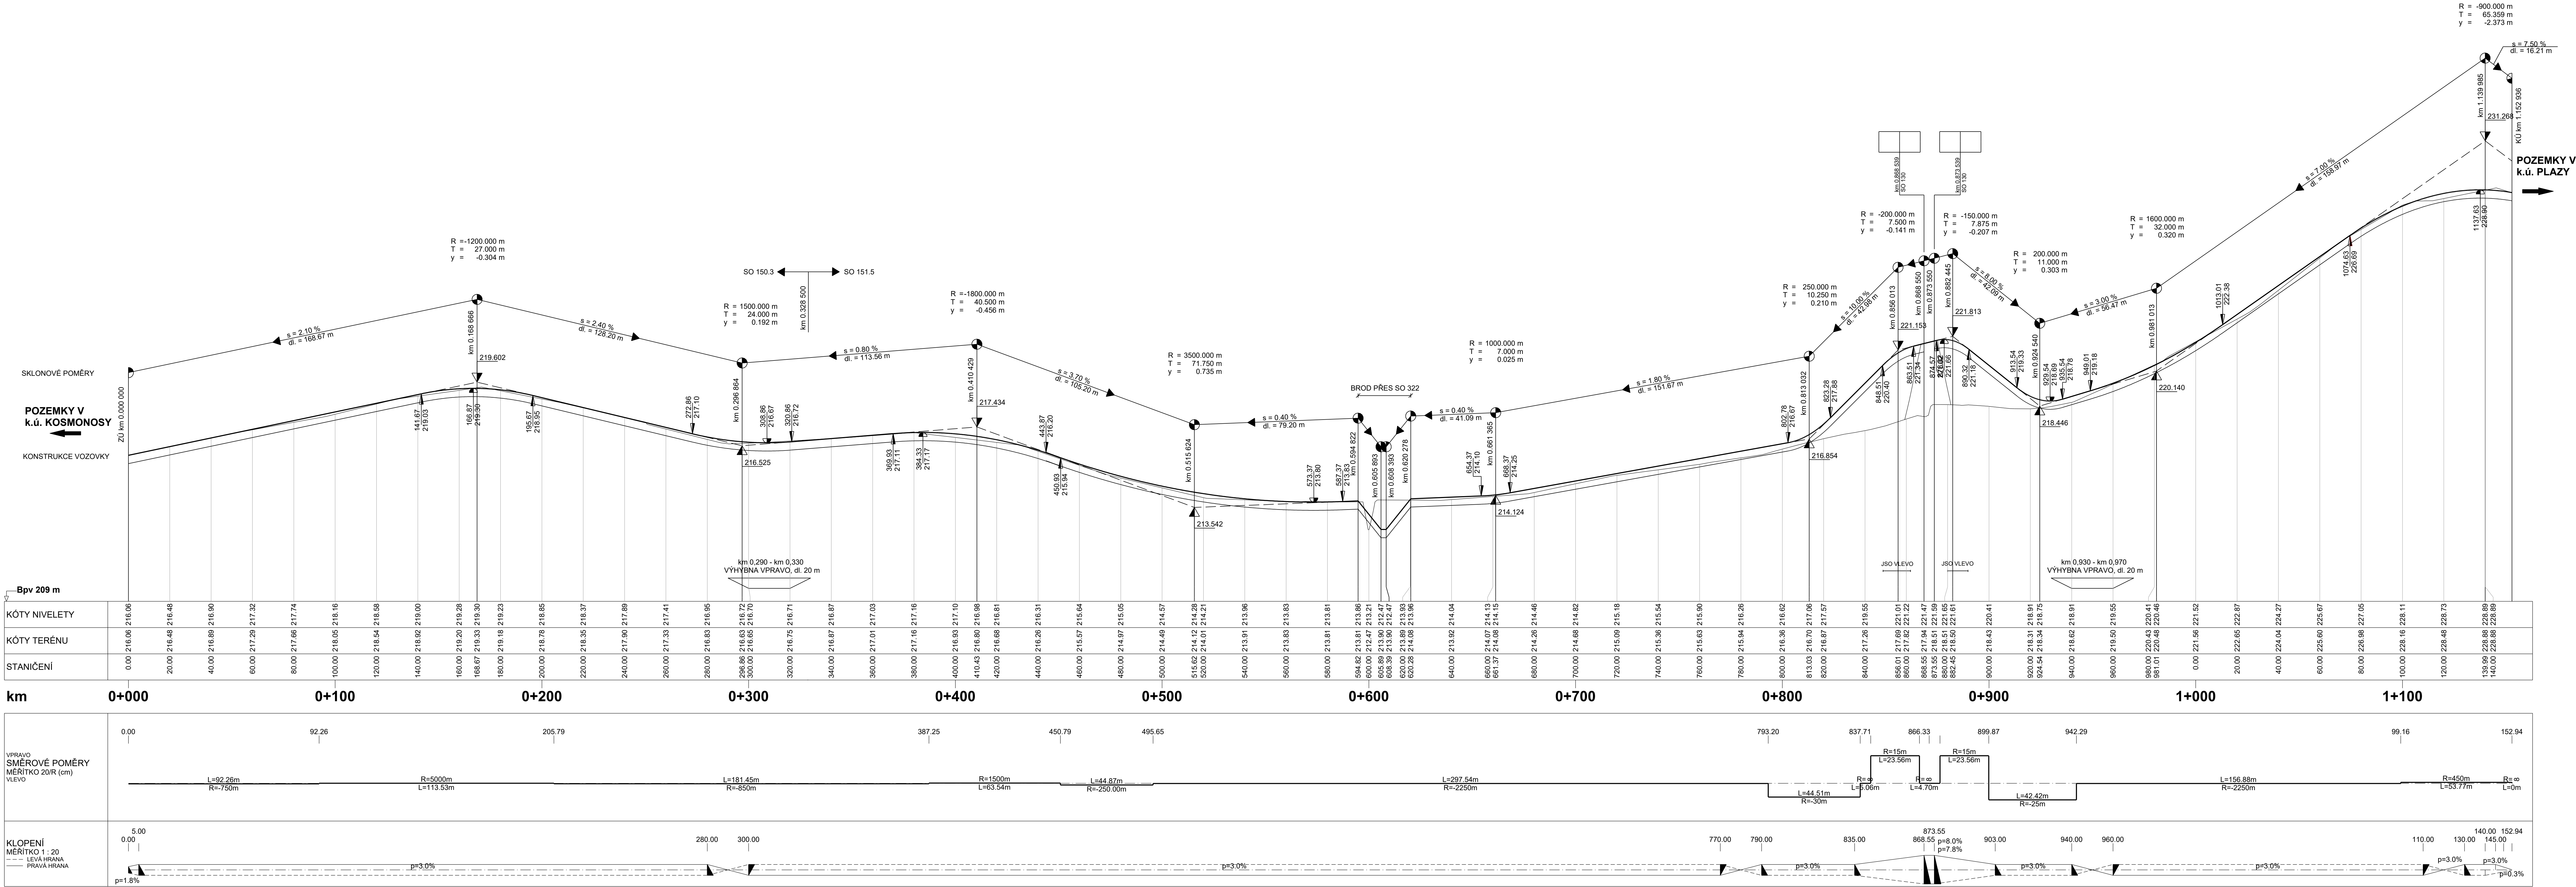

Výškový systém: Bpv

SO 151 Přístupy na pozemky k.ú. Plazy

Objednatel:



Ředitelství silnic a dálnic s. p.
Čerčanská 2023/12, Krč, 140 00 Praha 4

Zhotovitel:



Valbek, spol. s r.o.
Vaňurova 505/17
460 07 Liberec 3



Vypracoval	P. BARTUSEK	
Zodp. projektant	ING. T. KLIMENT	
Tech. kontrola	ING. M. HANŽL	

Akce

I/16 MI ADÁ BOJ ESI AV - MARTINOVIC

ak. číslo	21-LI13-0
datum	02/2025
tupeň	PDPS
počet formátů	7 x A4
měřítko	1 : 1 000/

Zhotovitel:

Příloha

PODÉLNÝ PROFIL SO 151

25

3.5