


SO 152 - PŘÍSTUPY NA POZEMKY k.ú. ŽIDNĚVES  
SITUACE SO 152.1, M 1 : 1000

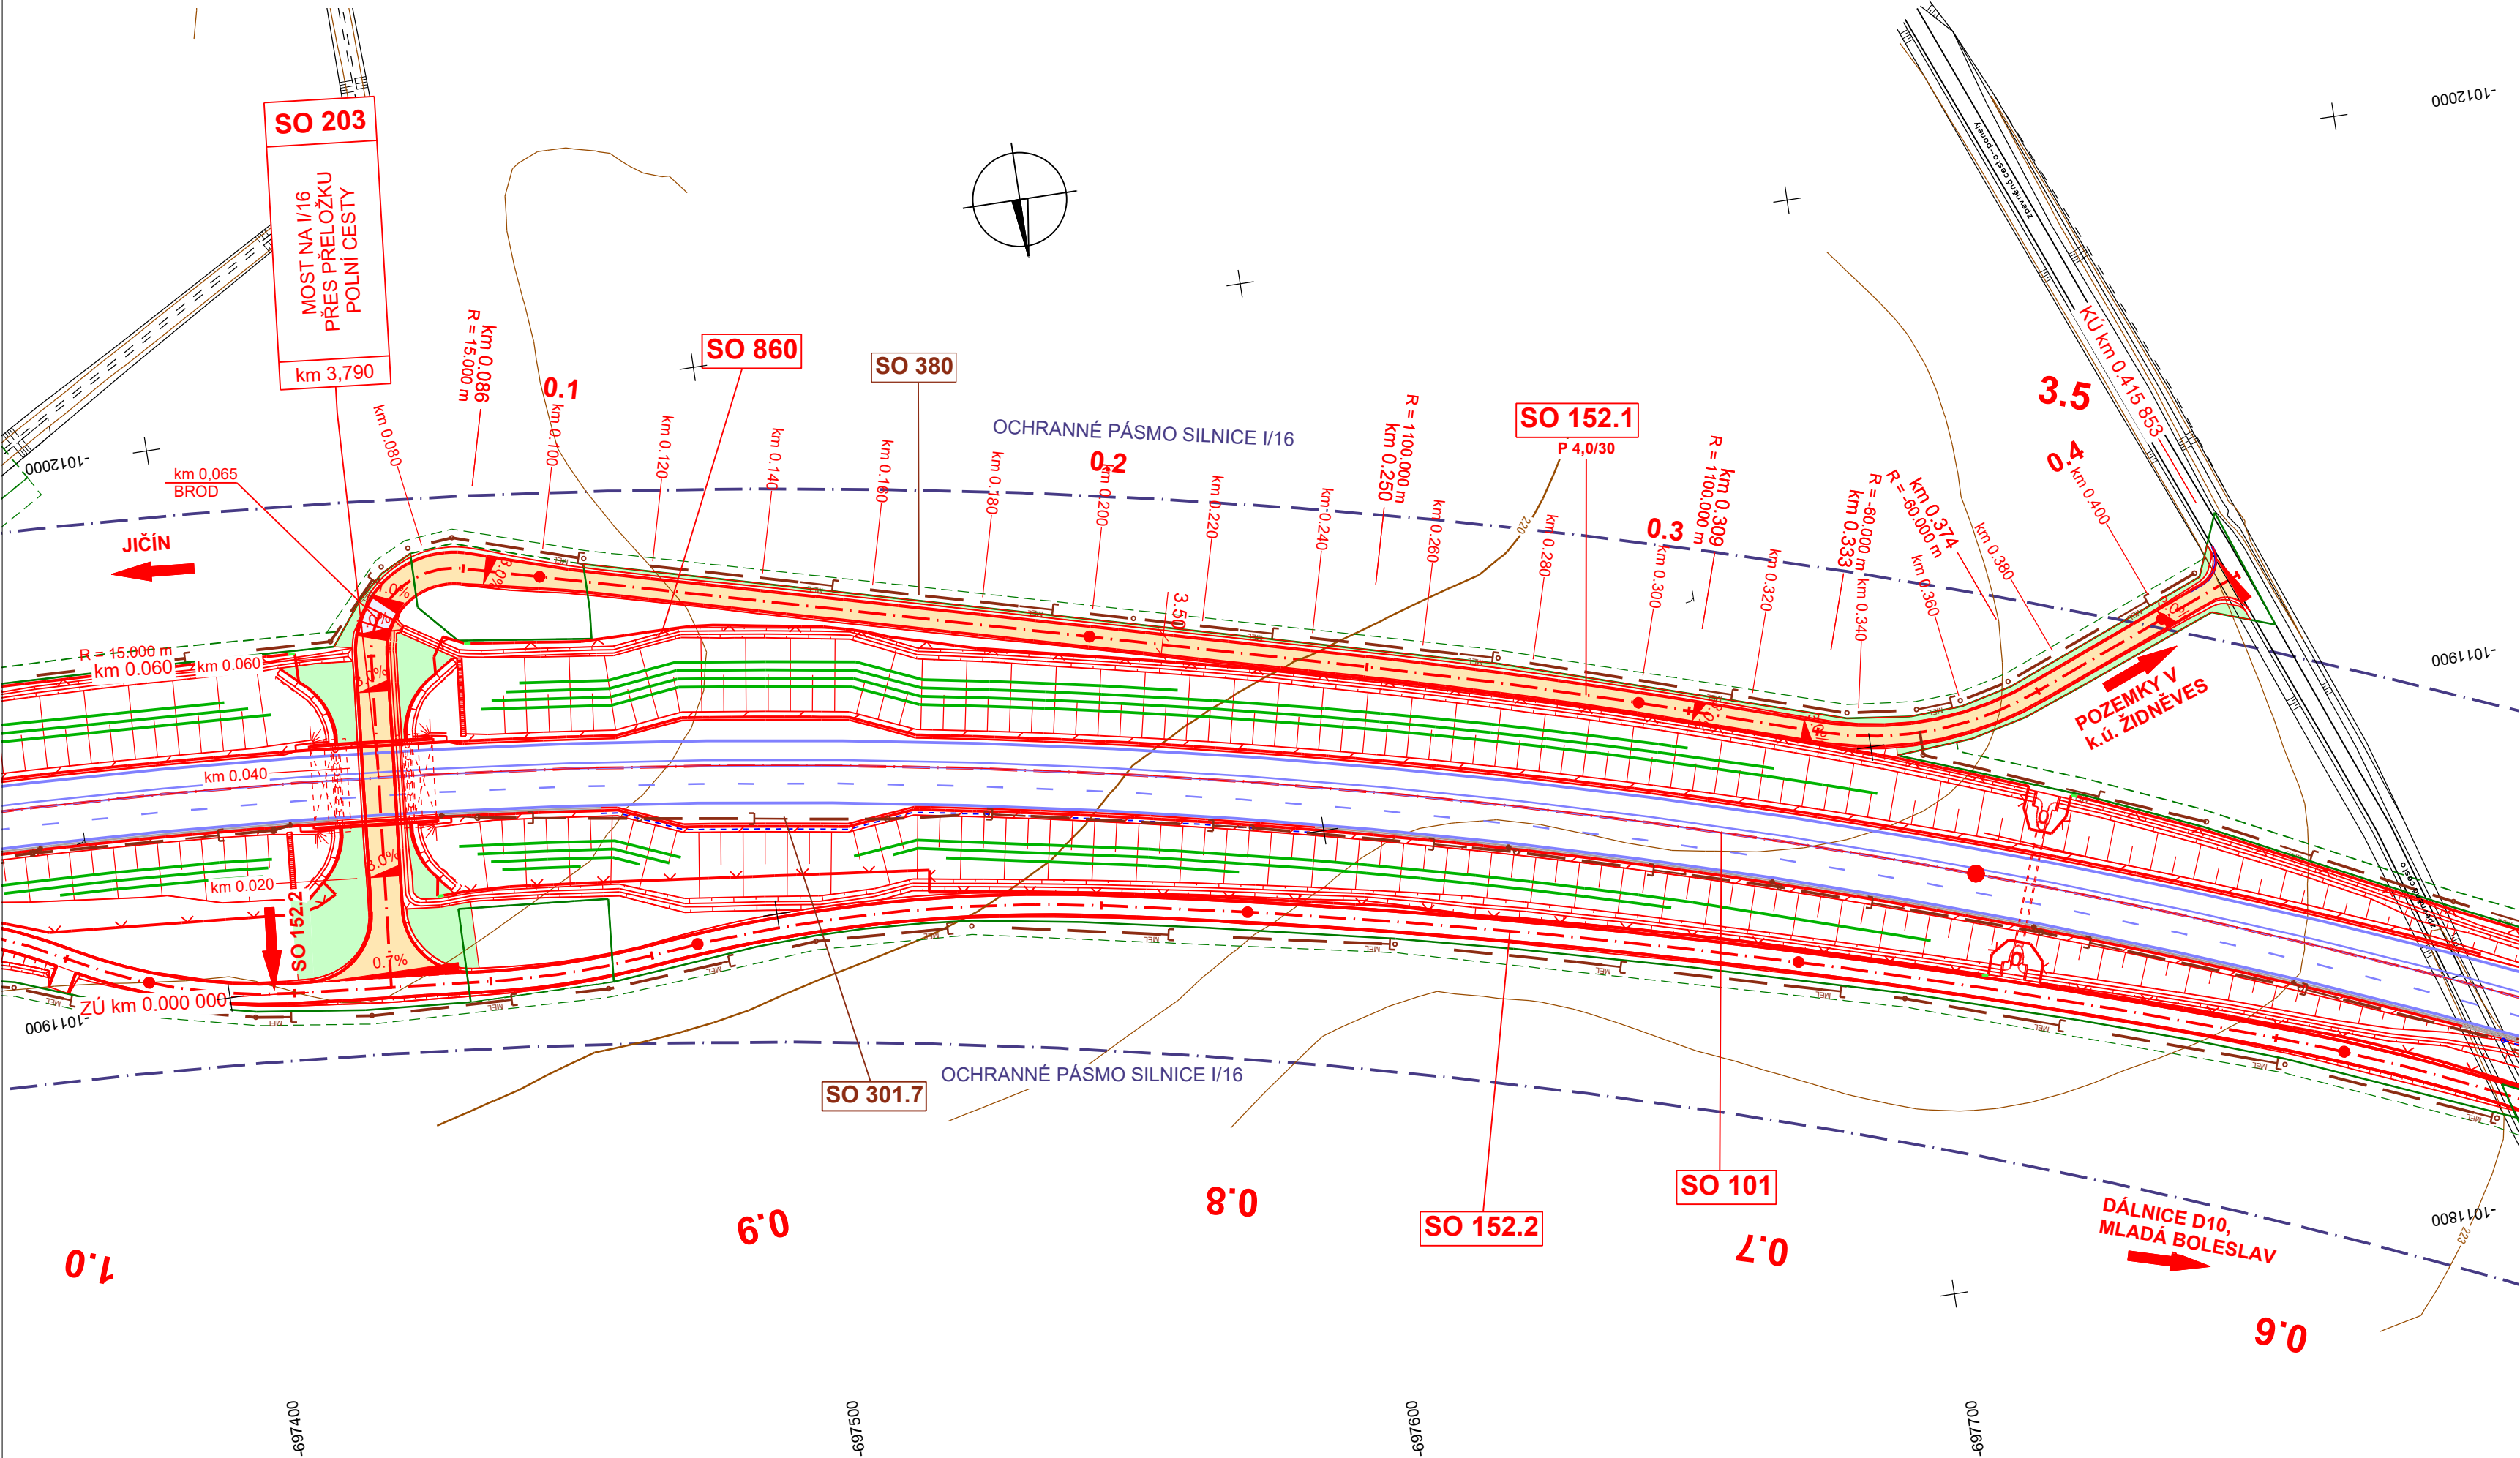

LEGENDA:

PLOCHY

- VOZOVKA - POLNÍ CESTY
- SVAHY VÝKOPU
- SVAHY NÁSYPU
- VEGETAČNÍ ÚPRAVY

KATASTR NEMOVITOSTÍ

- HRANICE K.Ú.
- HRANICE PARCEL
- TRVALÝ ZÁBOR
- DOČASNÝ ZÁBOR

NOVÉ IS

- DEŠŤOVÁ KANALIZACE
- MELIORACE
- VÝTLAK
- VODOVOD
- NADZEMNÍ VEDENÍ NN
- NADZEMNÍ VEDENÍ VN
- PODZEMNÍ VEDENÍ NN
- PODZEMNÍ SDĚLOVACÍ VEDENÍ
- PLYNOVOD - STL

STÁVAJÍCÍ IS - INFORMATIVNÍ ZÁKRES

- PODZEMNÍ VEDENÍ NN
- PODZEMNÍ VEDENÍ VN
- NADZEMNÍ VEDENÍ NN
- NADZEMNÍ VEDENÍ VN
- NADZEMNÍ VEDENÍ VVN
- DEŠŤOVÁ KANALIZACE
- PLYNOVOD - STL
- PODZEMNÍ SDĚLOVACÍ VEDENÍ
- VODOVOD

Souřadnicový systém: S-JTSK  
Výškový systém: Bpv

SO 152 Přístupy na pozemky k.ú. Židněves

Objednatel:



**Ředitelství silnic a dálnic s. p.**  
Čerčanská 2023/12, Krč, 140 00 Praha 4

Zhotovitel:



**Valbek, spol. s r.o.**  
Vaňurova 505/17  
460 07 Liberec 3

|                                                                                       |                                               |                 |  |               |             |
|---------------------------------------------------------------------------------------|-----------------------------------------------|-----------------|--|---------------|-------------|
|  | Vypracoval                                    | P. BARTUSEK     |  | Zak. číslo    | 21-LI13-001 |
|                                                                                       | Zodp. projektant                              | ING. T. KLIMENT |  | Datum         | 02/2025     |
|                                                                                       | Tech. kontrola                                | ING. M. HANŽL   |  | Stupeň        | PDPS        |
|                                                                                       | Akce<br><br>I/16 MLADÁ BOLESLAV - MARTINOVICE |                 |  | Počet formátů | 4 x A4      |
|                                                                                       |                                               |                 |  | Měřítko       | 1 : 1 000   |
| Zhotovitel:<br>Valbek, spol. s r.o.<br>Vaňurova 505/17<br>460 07 Liberec 3            | Příloha<br><br>SITUACE SO 152.1               |                 |  | Č. přílohy    | Paré        |
|                                                                                       |                                               |                 |  |               |             |