
# SO 152 - PŘÍSTUPY NA POZEMKY k.ú. ŽIDNĚVES
# SITUACE SO 152.2 - km 0,000 - 1,200, M 1 : 1000

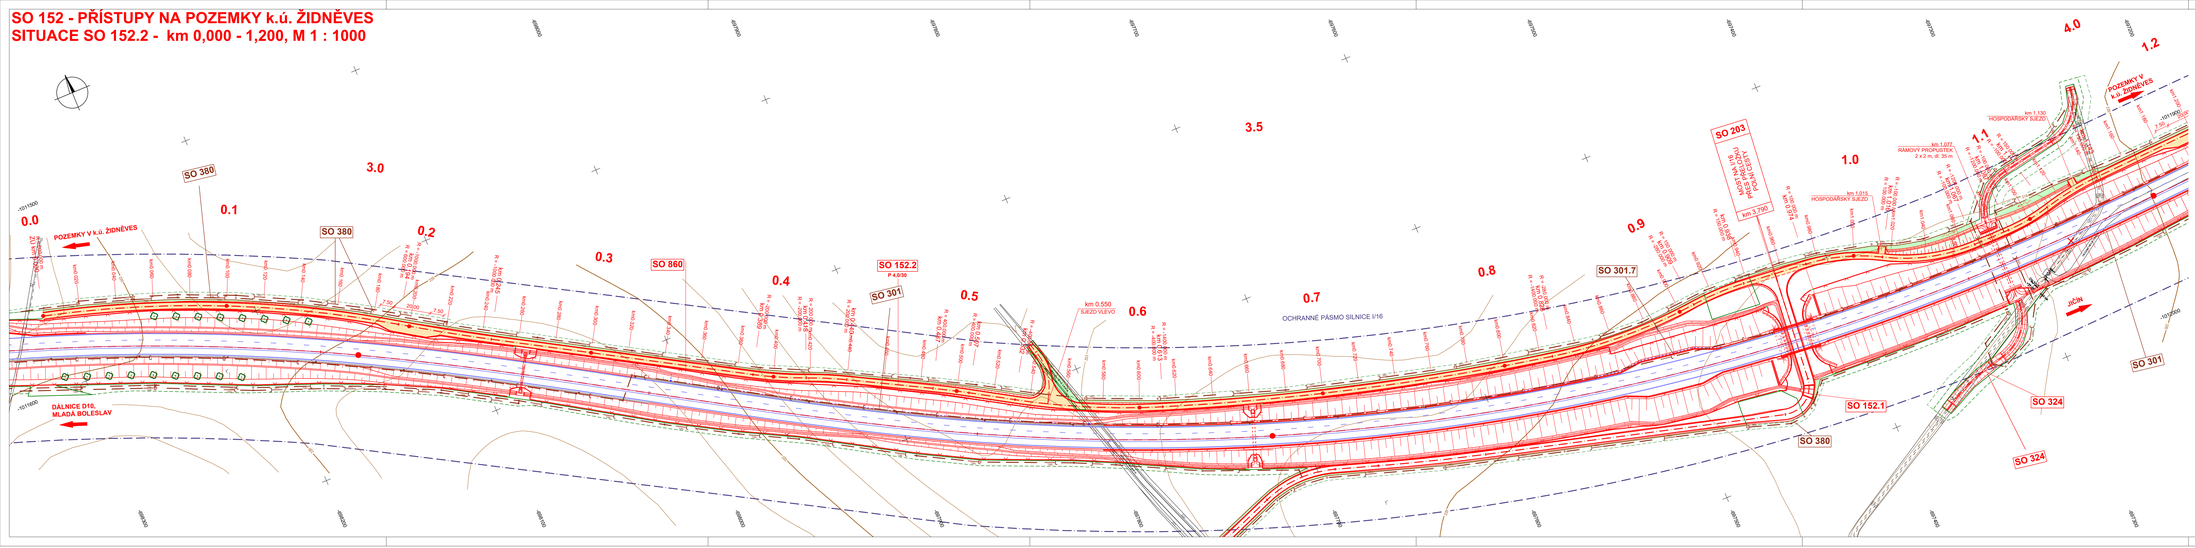


**LEGENDA:**

PLOCHY
- VOZOVKA - POLNÍ CESTY
- SVAHY VÝKOPU
- SVAHY NÁSYPU
- VEGETAČNÍ ÚPRAVY

KATASTR NEMOVITOSTÍ
- HRANICE K.Ú.
- HRANICE PARCEL
- TRVALÝ ZÁBOR
- DOČASNÝ ZÁBOR

NOVÉ IS
- DEŠŤOVÁ KANALIZACE
- MELIORACE
- VÝTLAK
- VODOVOD
- NADZEMNÍ VEDENÍ NN
- NADZEMNÍ VEDENÍ VN
- PODZEMNÍ VEDENÍ NN
- PODZEMNÍ SDĚLOVACÍ VEDENÍ
- PLYNOVOD - STL

STÁVAJÍCÍ IS - INFORMATIVNÍ ZÁKRES
- PODZEMNÍ VEDENÍ NN
- PODZEMNÍ VEDENÍ VN
- NADZEMNÍ VEDENÍ NN
- NADZEMNÍ VEDENÍ VVN
- DEŠŤOVÁ KANALIZACE
- PLYNOVOD - STL
- PODZEMNÍ SDĚLOVACÍ VEDENÍ
- VODOVOD

Souřadnicový systém: S-JTSK
Výškový systém: Bpv

**SO 152** Přístupy na pozemky k.ú. Židněves

Objednatel:
ŘEDITELSTVÍ SILNIC A DÁLNIC
**Ředitelství silnic a dálnic s. p.**
Čerčanská 2023/12, Kríč, 140 00 Praha 4

Zhotovitel:
**Valbek, spol. s r.o.**
Vaňurova 505/17
460 07 Liberec 3

| | | | | | |
|---|---|---|---|---|---|
| Valbek | Vypracoval | P. BARTUŠEK | | Zak. číslo | 21-LI13-001 |
| | Zodp. projektant | ING. T. KLIMENT | | Datum | 02/2025 |
| | Tech. kontrola | ING. M. HANZL | | Stupeň | PDPS |
| | Akce | I/16 MLADÁ BOLESLAV - MARTINOVICE | | Počet formátů | 7 x A4 |
| | | | | Měřítko | 1 : 1 000 |
| Zhotovitel: Valbek, spol. s r.o. Vaňurova 505/17 460 07 Liberec 3 | Příloha | SITUACE SO 152.2 - km 0,000 - 1,200 | | Č. přílohy | Paré |
| | | | | 2.2.1 | |