


SO 152 - PŘÍSTUPY NA POZEMKY k.ú. ŽIDNĚVES
SITUACE SO 152.2 - km 1,200 - 2,101, M 1 : 1 000

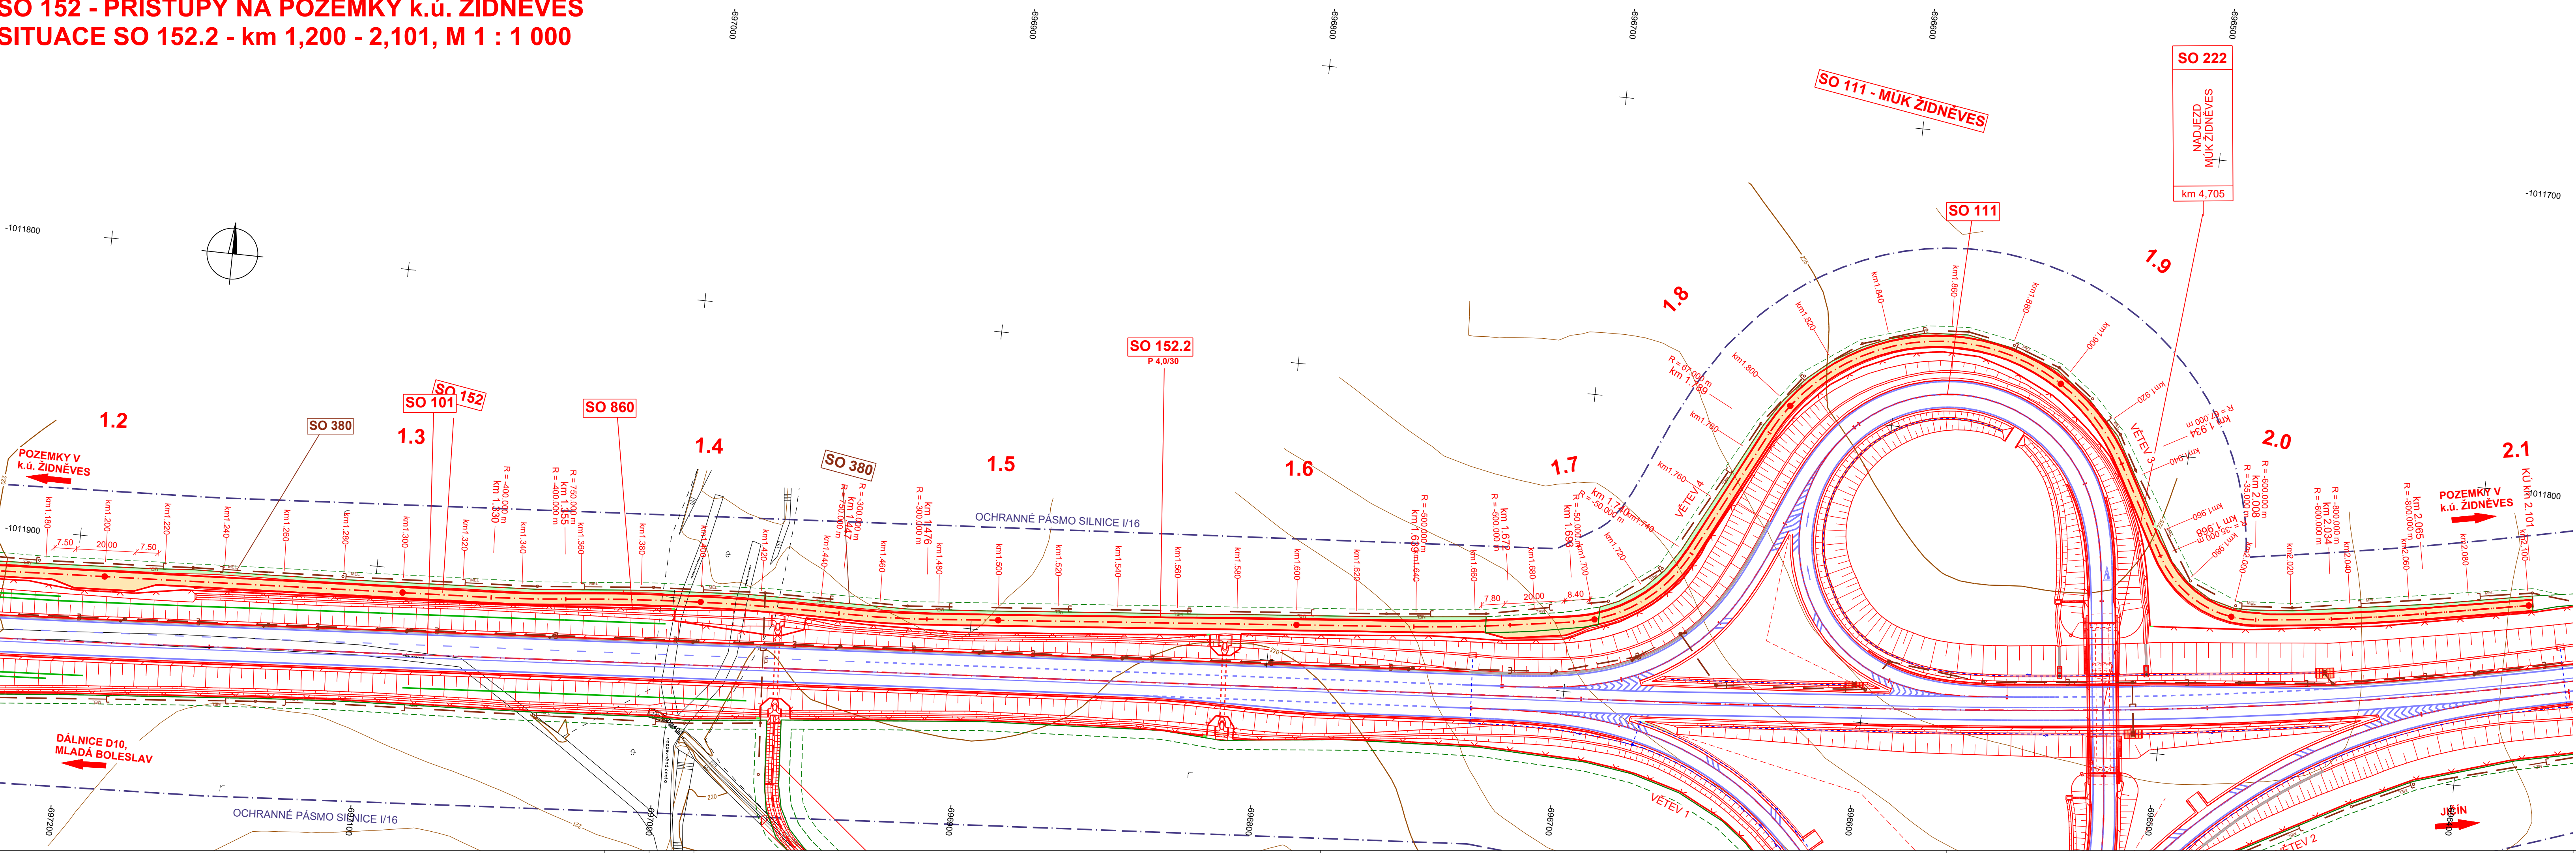

LEGENDA:

PLOCHY

- VOZOVKA - POLNÍ CESTY
- SVAHY VÝKOPU
- SVAHY NÁSYPU
- VEGETAČNÍ ÚPRAVY

NOVÉ IS

- DEŠŤOVÁ KANALIZACE
- MELIORACE
- VÝTLAK
- VODOVOD
- NADZEMNÍ VEDENÍ NN
- NADZEMNÍ VEDENÍ VN
- PODZEMNÍ VEDENÍ NN
- PODZEMNÍ SDĚLOVACÍ VEDENÍ
- PLYNOVOD - STL

KATASTR NEMOVITOSTÍ

- HRANICE K.Ú.
- HRANICE PARCEL
- TRVALÝ ZÁBOR
- DOČASNÝ ZÁBOR

STÁVAJÍCÍ IS - INFORMATIVNÍ ZÁKRES

- PODZEMNÍ VEDENÍ NN
- PODZEMNÍ VEDENÍ VN
- NADZEMNÍ VEDENÍ NN
- NADZEMNÍ VEDENÍ VN
- NADZEMNÍ VEDENÍ VVN
- DEŠŤOVÁ KANALIZACE
- PLYNOVOD - STL
- PODZEMNÍ SDĚLOVACÍ VEDENÍ
- VODOVOD

Souřadnicový systém: S-JTSK
Výškový systém: Bpv

SO 152 Přístupy na pozemky k.ú. Židněves

Objednatel:

ŘEDITELSTVÍ SILNIC A DÁLNIC

Ředitelství silnic a dálnic s. p.
Čerčanská 2023/12, Krč, 140 00 Praha 4

Zhotovitel:

Valbek, spol. s r.o.
Vaňurova 505/17
460 07 Liberec 3

	Vypracoval	P. BARTUSEK	Zak. číslo	21-L113-001
	Zodp. projektant	ING. T. KLIMENT	Datum	02/2025
	Tech. kontrola	ING. M. HANŽL	Stupeň	PDPS
	Akce		Počet formátů	6 x A4
	I/16 MLADÁ BOLESLAV - MARTINOVICE		Měřítka	Č. přílohy
Zhotovitel:	Příloha		2.2.2	
Valbek, spol. s r.o. Vaňurova 505/17 460 07 Liberec 3	SITUACE SO 152.2 - km 1,200 - 2,101			