
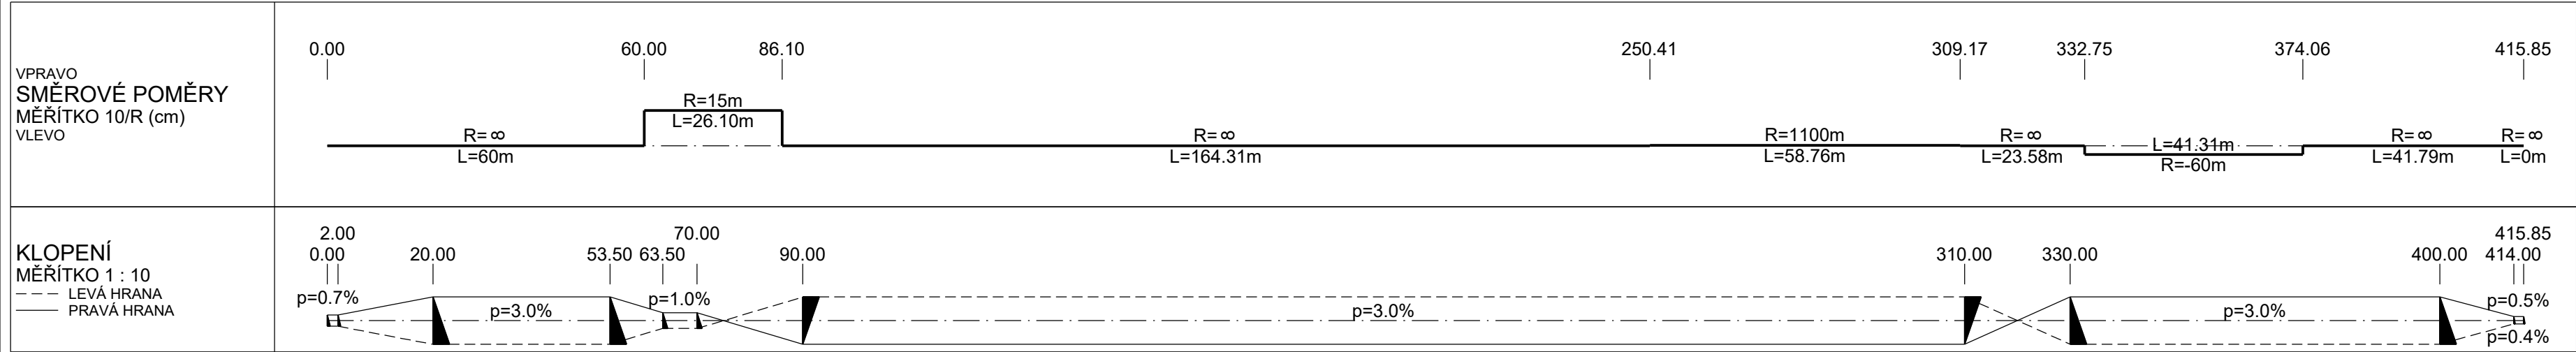


SO 152 - PŘÍSTUPY NA POZEMKY k.ú. ŽIDNĚVES
PODÉLNÝ PROFIL SO 152.1, M 1:1 000/100

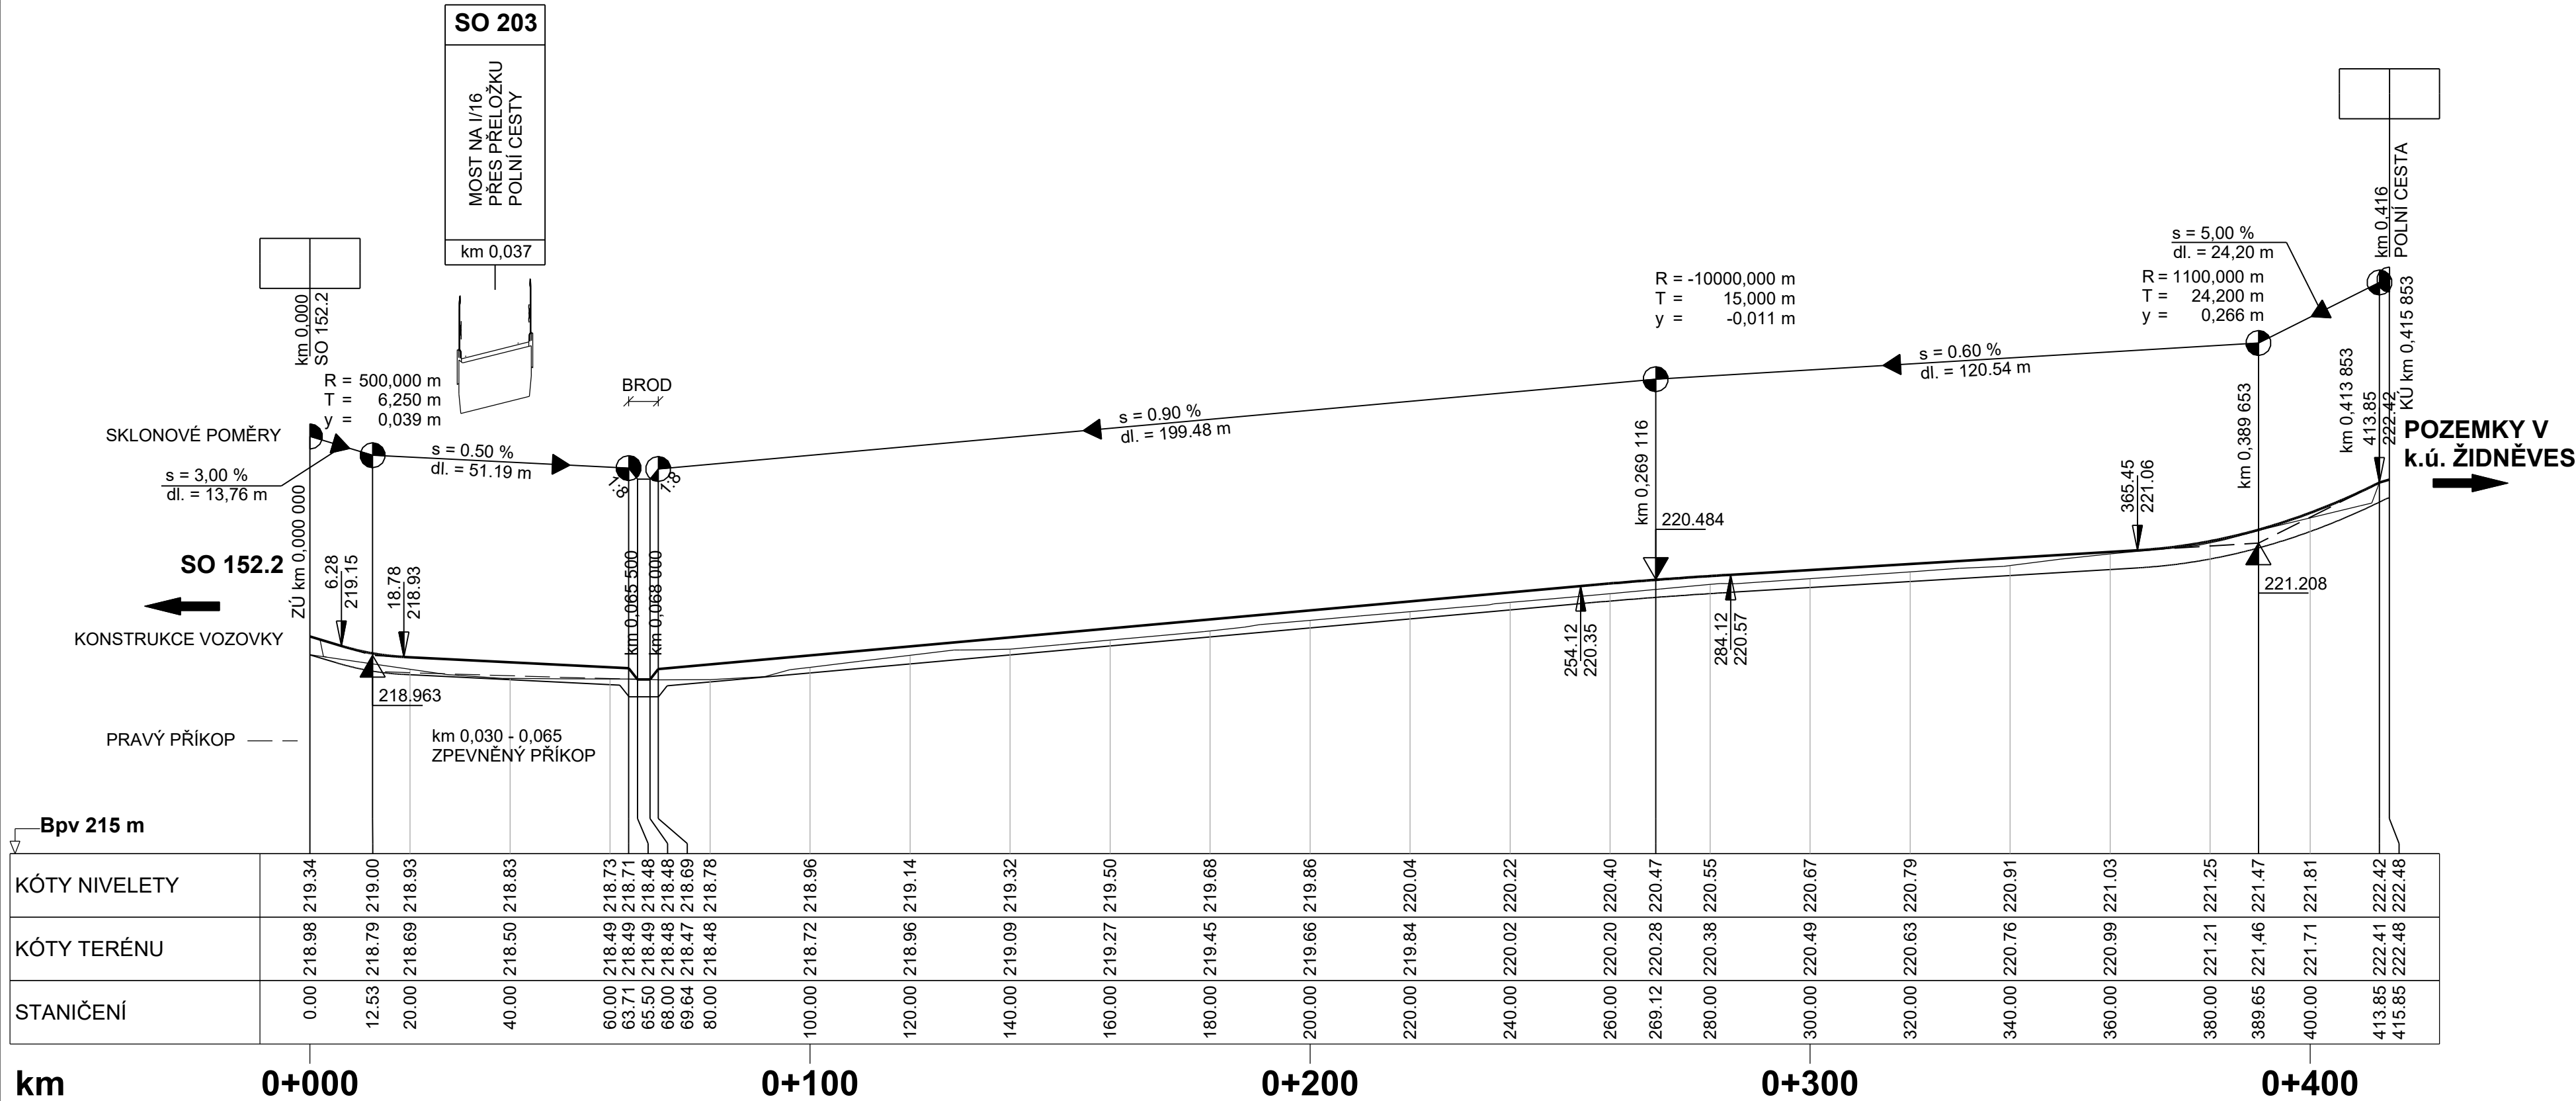

Výškový systém: Bpv

SO 152 Přístupy na pozemky k.ú. Židněves

Objednatel:

Ředitelství silnic a dálnic

Ředitelství silnic a dálnic s. p.
Čerčanská 2023/12, Krč, 140 00 Praha 4

Zhotovitel:

Valbek

Valbek, spol. s r.o.
Vaňurova 505/17
460 07 Liberec 3

	Vypracoval	P. BARTUSEK		Zak. číslo	21-LI13-001
	Zodp. projektant	ING. T. KLIMENT		Datum	02/2025
	Tech. kontrola	ING. M. HANŽL		Stupeň	PDPS
	Akce I/16 MLADÁ BOLESLAV - MARTINOVICE			Počet formátů	4 x A4
				Měřítko	1 : 1 000/100
Zhotovitel: Valbek, spol. s r.o. Vaškova 505/17 460 07 Liberec 3			Č. přílohy	Paré	
			3.1		
					Příloha PODÉLNÝ PROFIL SO 152.1