
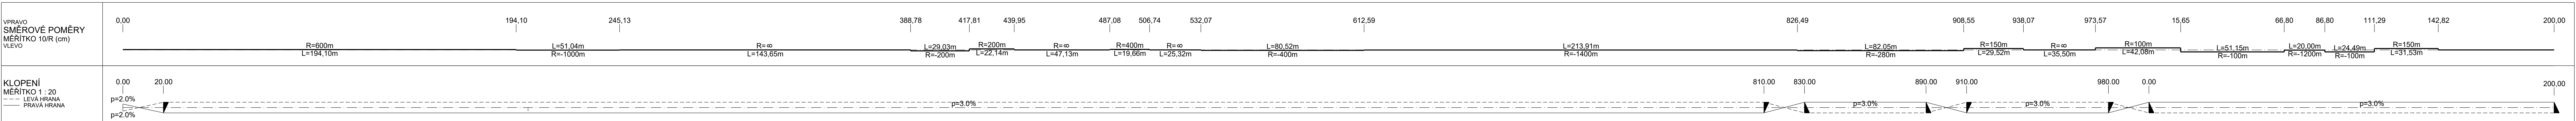


SO 152 - PŘÍSTUPY NA POZEMKY k.ú. ŽIDNĚVES
PODÉLNÝ PROFIL SO 152.2 - km 0,000 - 1,200, M 1 : 1000 / 100

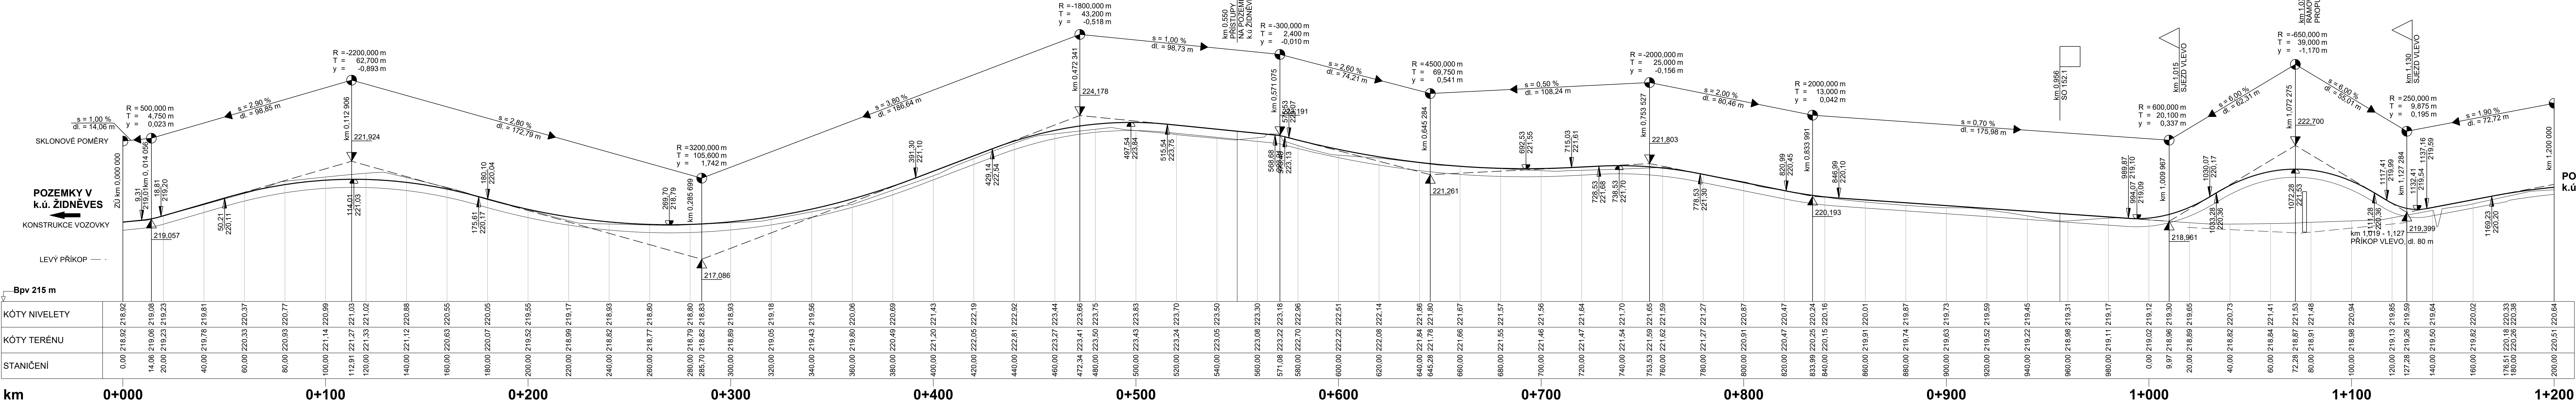

POZEMKY V
k.ú. ŽIDNĚVES

Výškový systém: Bpv

SO 152 Přístupy na pozemky k.ú. Židněves

Objednatel: Ředitelství silnic a dálnic s. p.
Čerčanská 2023/12, Krč, 140 00 Praha 4

Zhotovitel: Valbek spol. s r.o.
Vaňurova 505/17
460 07 Liberec 3

Valbek	Vypracoval	P. BARTUSEK	Zak. číslo	21-L113-001
	Zodp. projektant	ING. T. KLIMENT	Datum	02/2025
	Tech. kontrola	ING. M. HANŽL	Stupeň	PDPS
	Akce	I/16 MLADÁ BOLESLAV - MARTINOVICE		Počet formátů
Zhotovitel:		Příloha	Měřítko	1 : 1 000/100
Valbek spol. s r.o. Vaňurova 505/17 460 07 Liberec 3		PODÉLNÝ PROFIL SO 152.2 - km 0,000 - 1,200	C. přílohy	Paré