
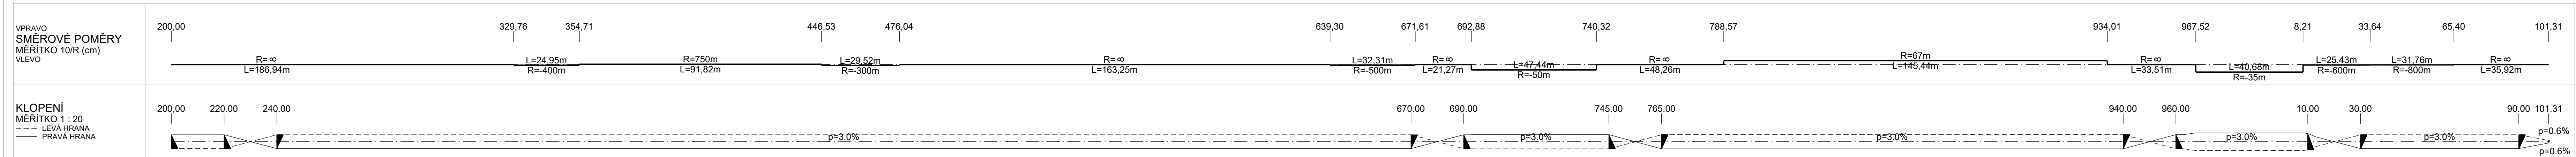


SO 152 - PŘÍSTUPY NA POZEMKY V k.ú. ŽIDNĚVES
PODELNÝ PROFIL SO 152.2 - km 1,200 - 2,101, M 1 : 1000 / 100

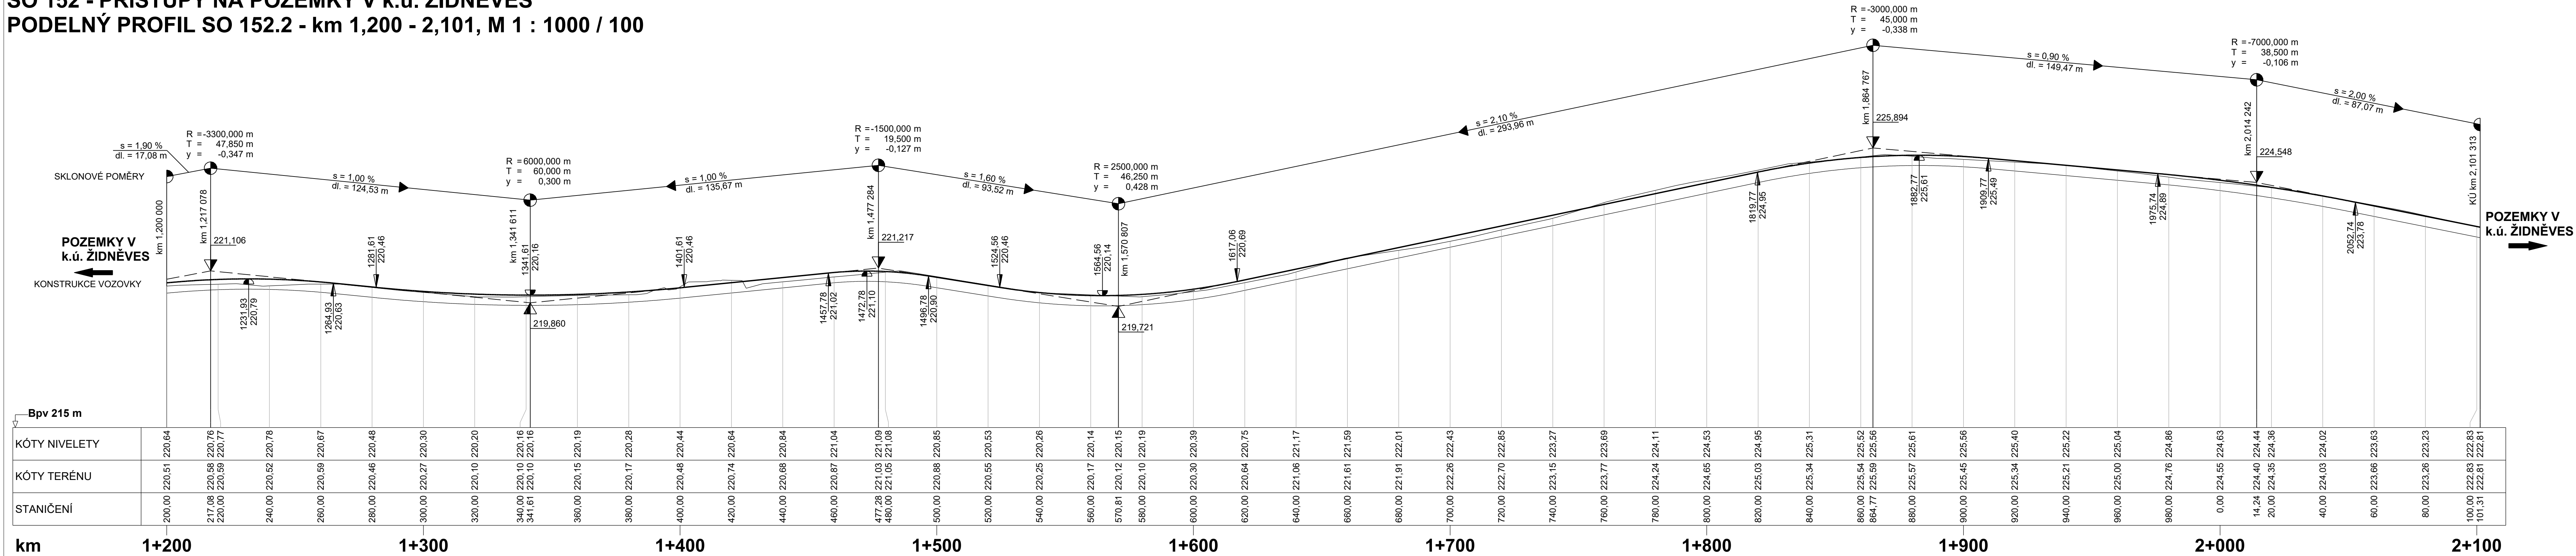

Výškový systém: Bpv

SO 152 Přístupy na pozemky k.ú. Židněves

Objednatel:

Ředitelství silnic a dálnic s. p.
Čerčanská 2023/12, Krč, 140 00 Praha 4

hotovitel:



Valbek, spol. s r.o.
Vaňurova 505/17
460 07 Liberec 3



hotovitel:

albek, spol. s r.o.
aňurova 505/17
30 07 Liberec 3

100% 90% 80% 70% 60% 50% 40% 30% 20% 10% 0%

Ypracoval	P. BARTUSEK	Zak. číslo	21-113-001
Zodp. projektant	ING. T. KLIMENT	Datum	02/2005
Tech. kontrola	ING. M. HANŽL	Stupeň	PDPS
Akce		Počet formátů	6 x A4
I/16 MLADÁ BOLESLAV - MARTINOVICE		Měřítko	1 : 1 000/100
		Č. přílohy	Paré
		3.2.2	
2Příloha PODELNÝ PROFIL SO 152.2 - km 1,200 - 2,101			