


SO 152 - PŘÍSTUP NA POZEMKY k.ú. ŽIDNĚVES
VZOROVÉ PŘÍČNÉ ŘEZY, M 1 : 50

KATEGORIE P 4,0/30
JEDNOPRUHOVÁ, OBOUSMĚRNÁ

TŘÍDA DOPRAVNÍHO ZATÍŽENÍ VI
NÁVRHOVÁ ÚROVEŇ PORUŠENÍ D2
TYP PODLOŽÍ PII (PN 6-5)

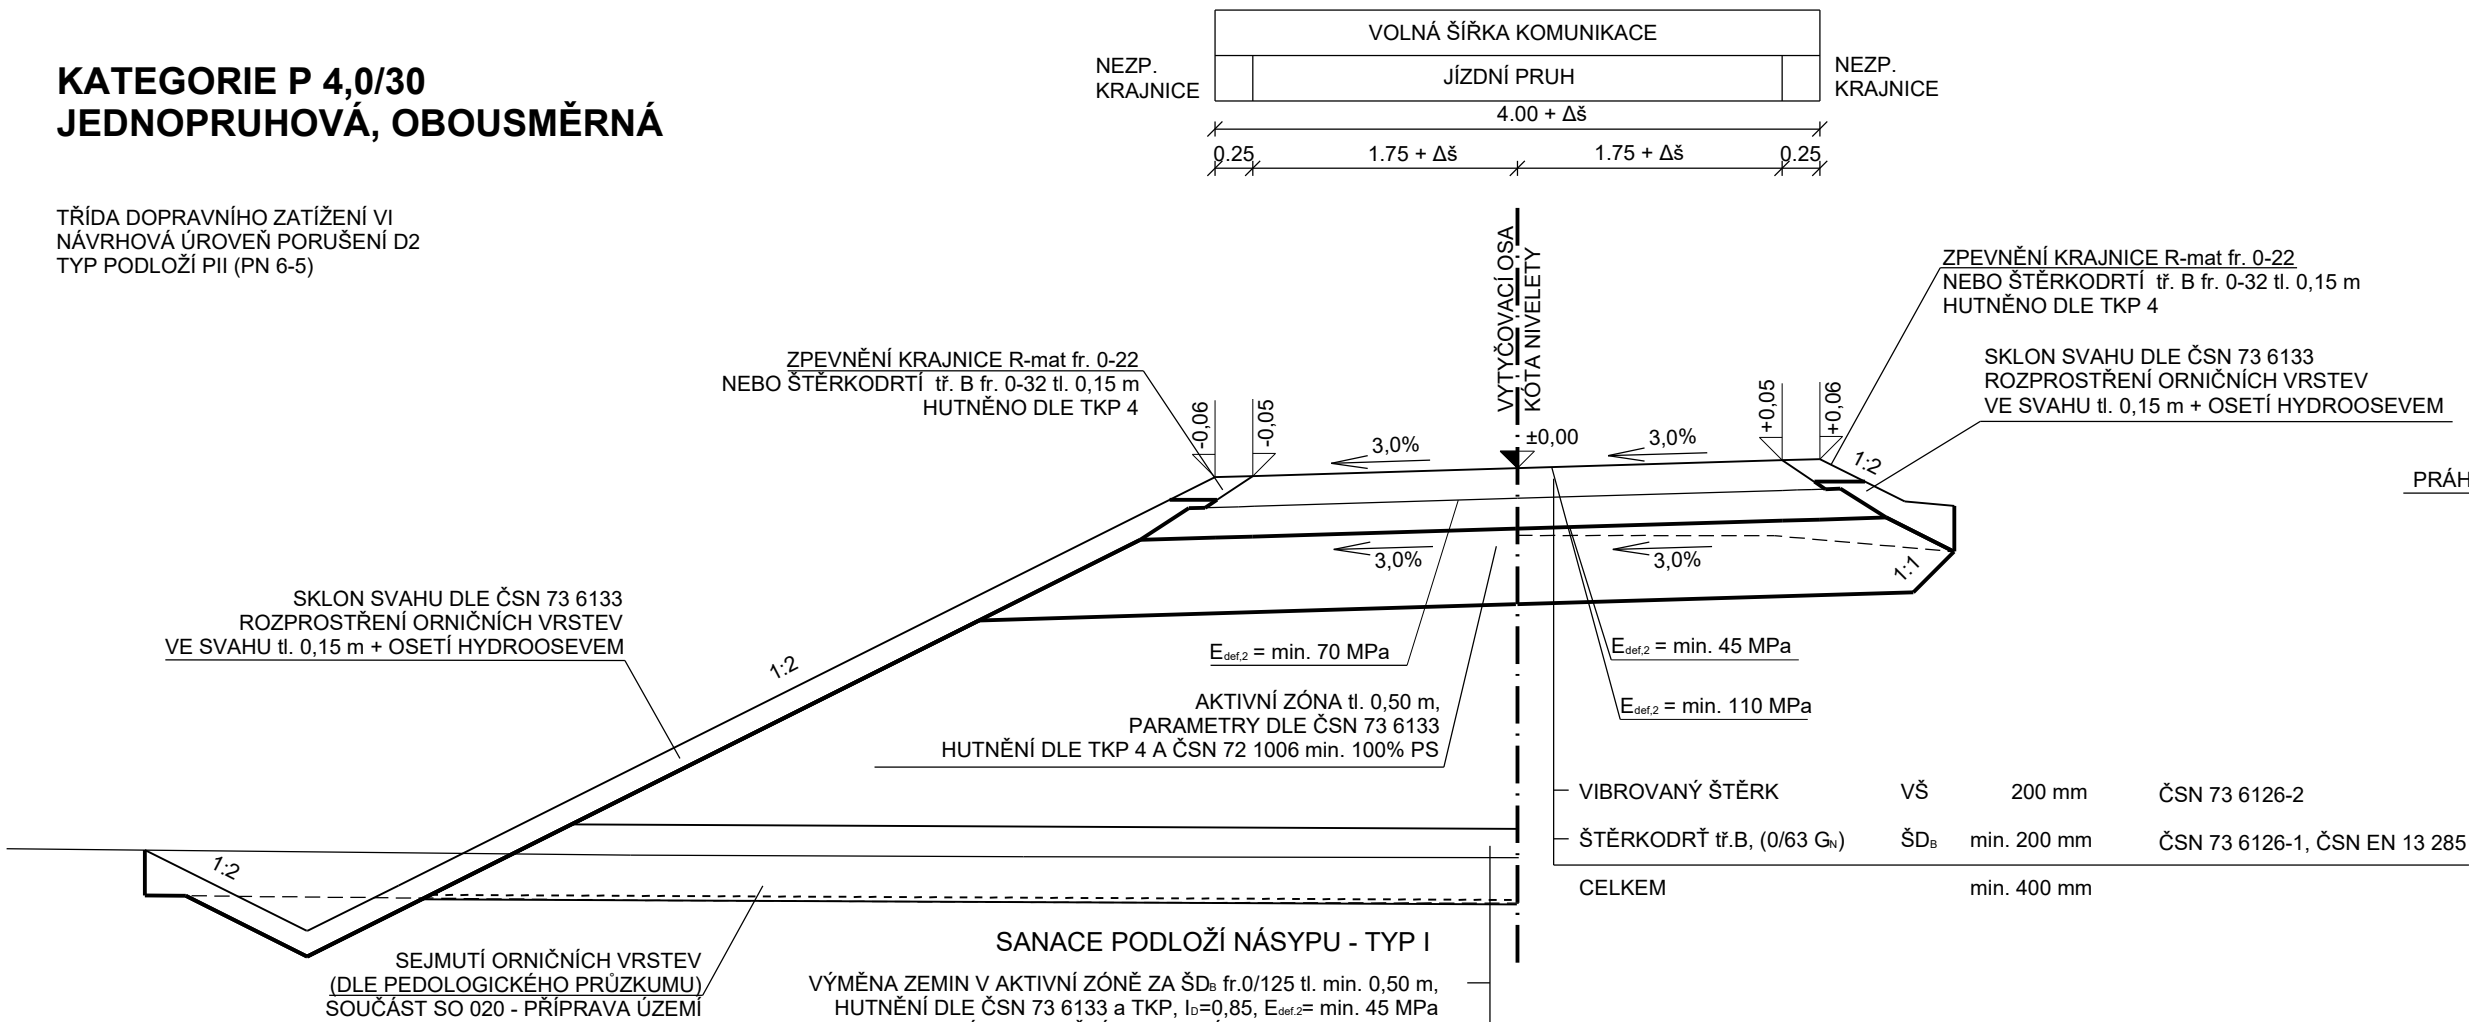

KATEGORIE P 4,0/30
JEDNOPRUHOVÁ, OBOUSMĚRNÁ

TŘÍDA DOPRAVNÍHO ZATÍŽENÍ VI
NÁVRHOVÁ ÚROVEŇ PORUŠENÍ D2
TYP PODLOŽÍ PII (PN 6-5)



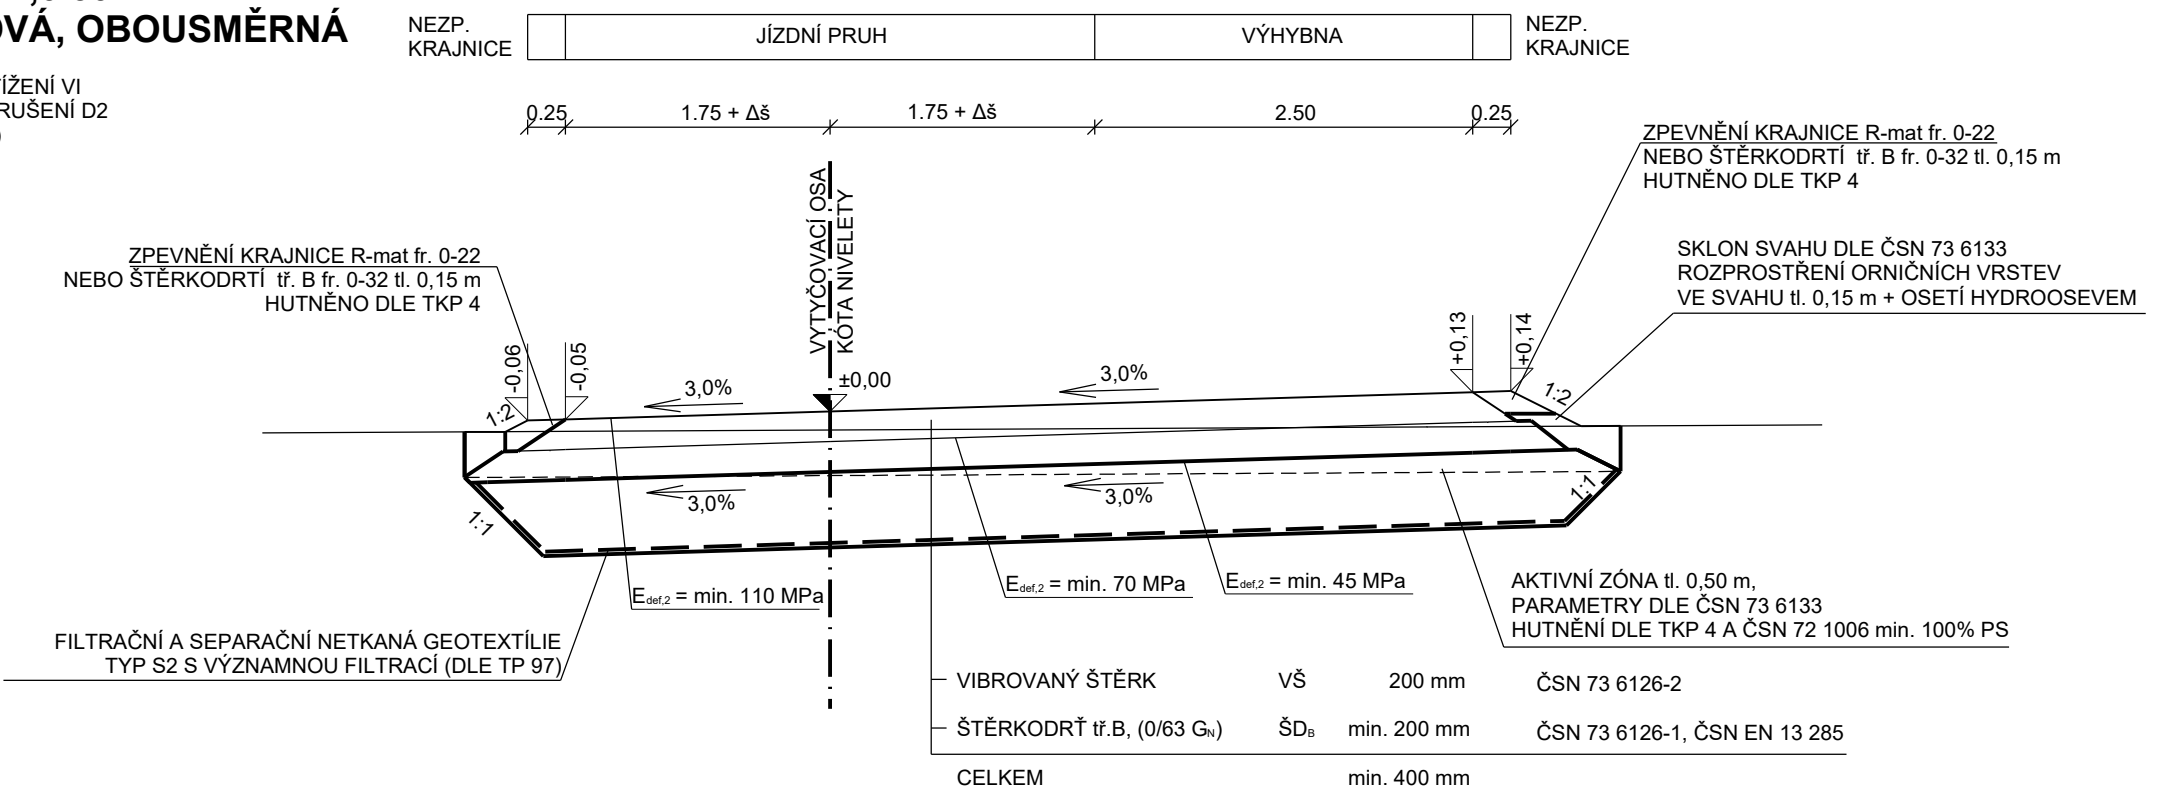



SCHÉMA BRODU V OSE
PŘÍSTUPOVÉ KOMUNIKACE, M 1 : 100

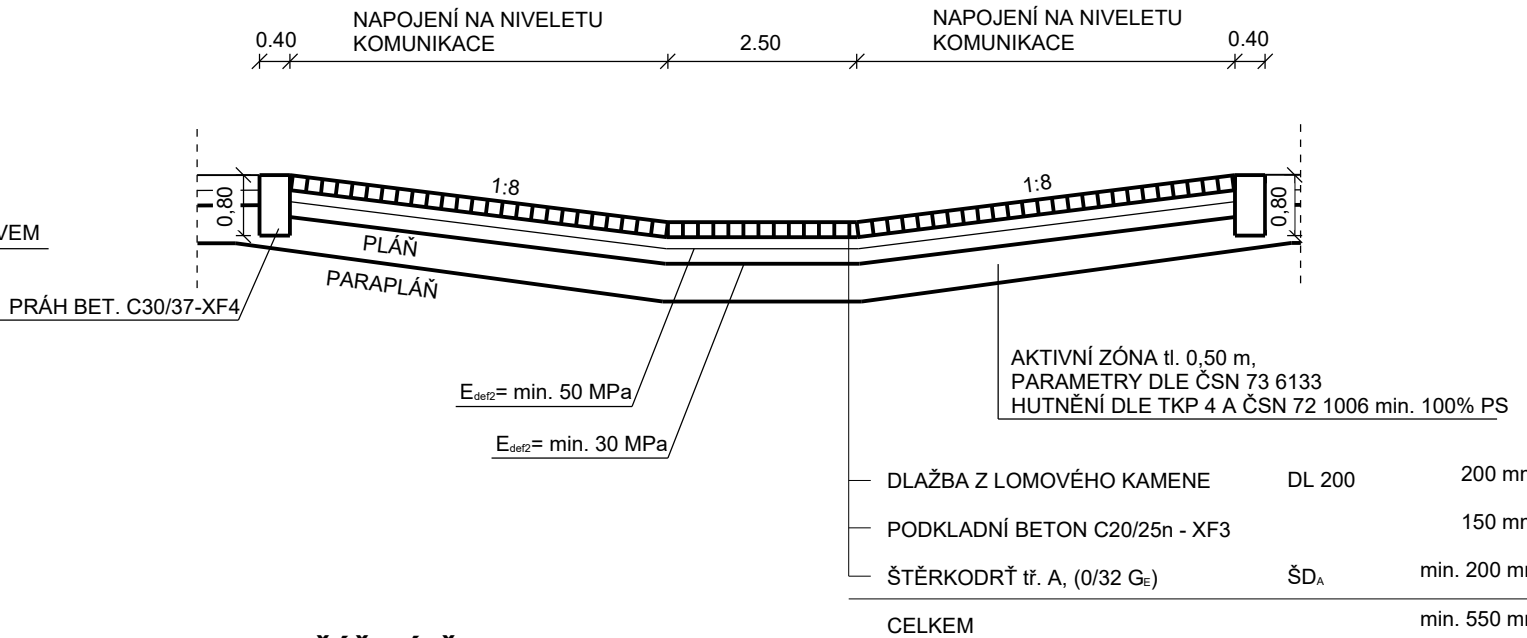

PŘÍČNÝ ŘEZ BRODEM

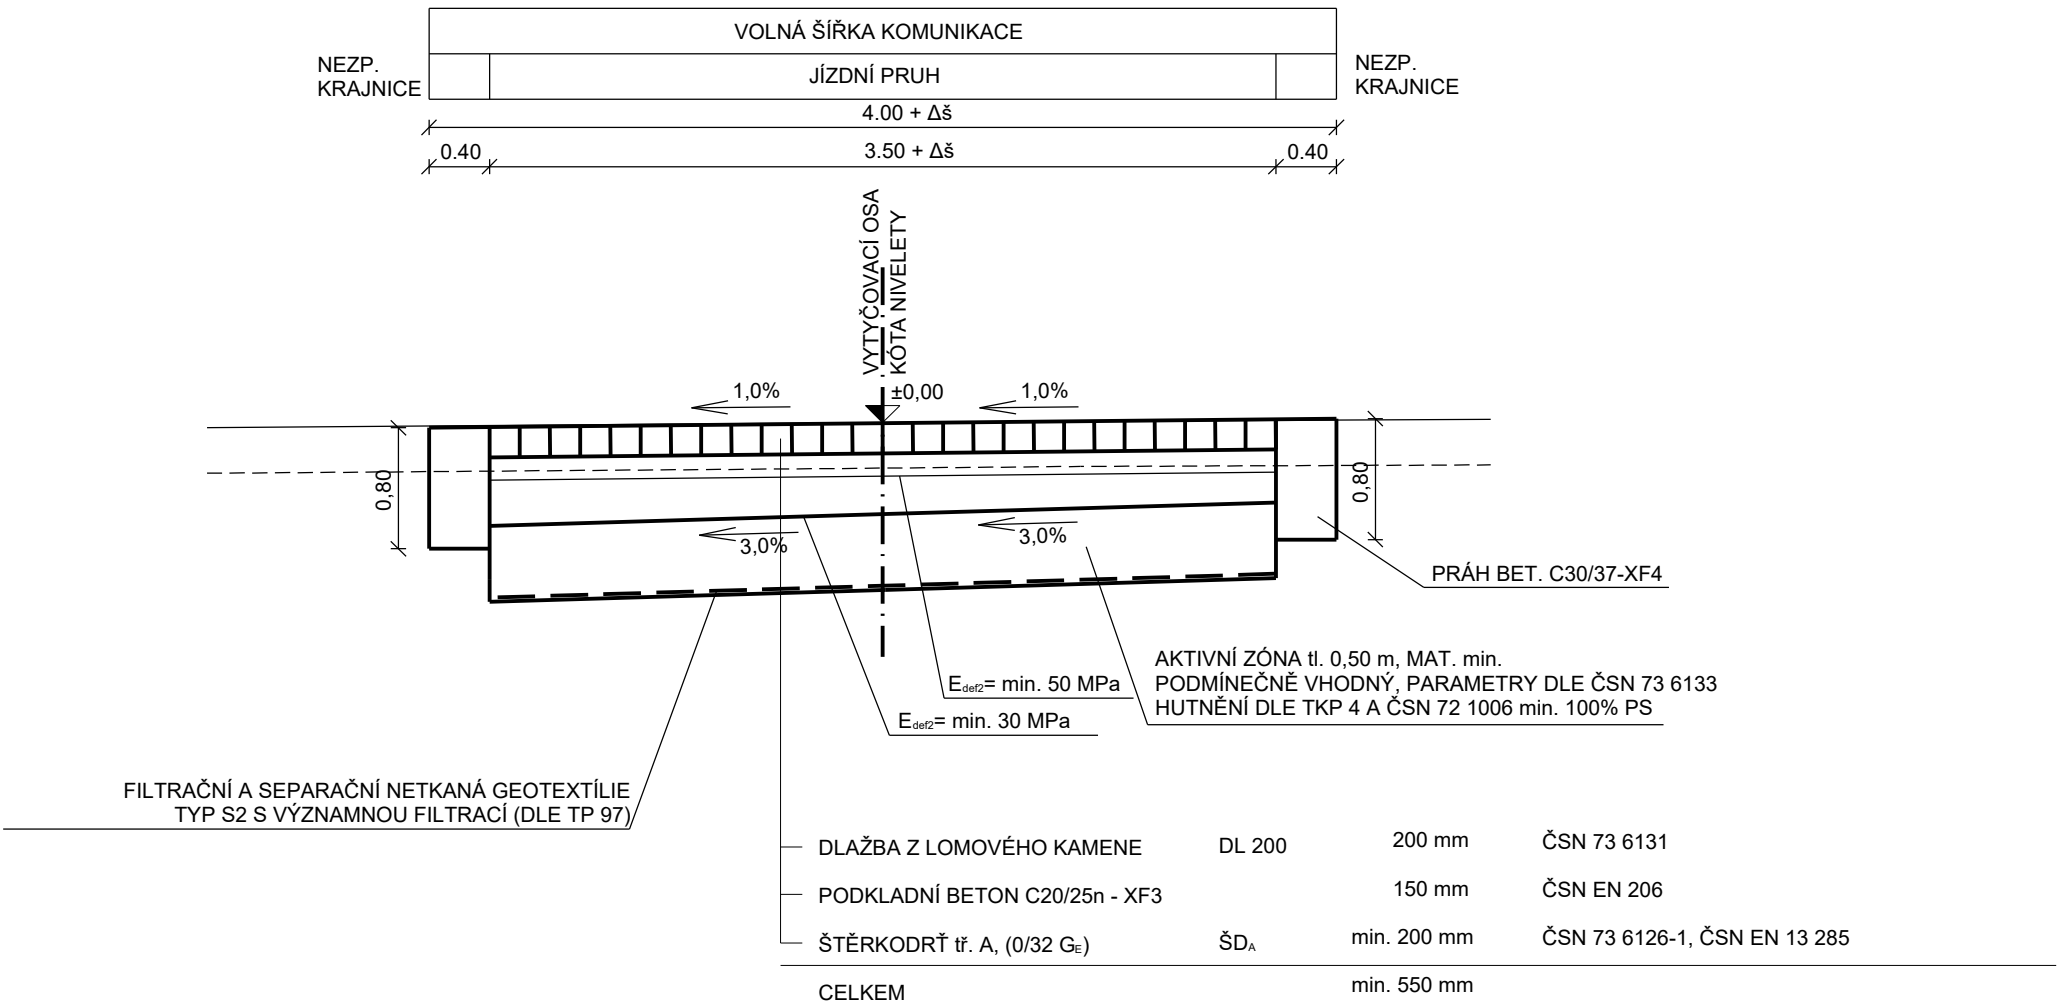

DETAIL DLÁŽDĚNÉHO PŘÍKOPU

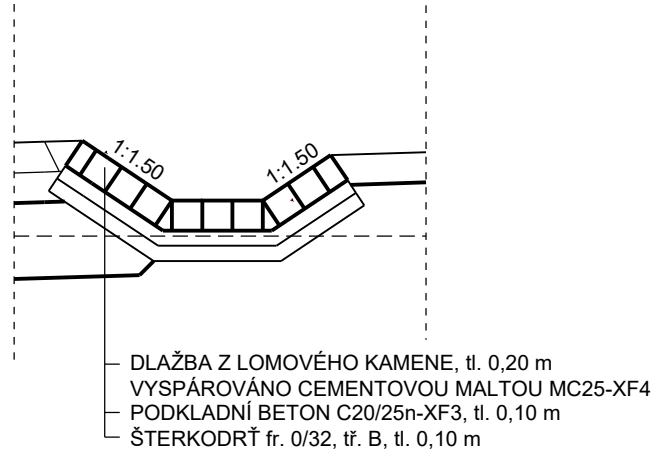

Výškový systém: Bpv

SO 152 Přístupy na pozemky k.ú. Židněves

Objednatel:



ŘEDITELSTVÍ
SILNIC
A DÁLNIC

Ředitelství silnic a dálnic s. p.
Čerčanská 2023/12, Krč, 140 00 Praha 4

Zhotovitel:



Valbek, spol. s r.o.
Vaňurova 505/17
460 07 Liberec 3



Zhotovitel:

Valbek, spol. s r.o.
Vaňurova 505/17
460 07 Liberec 3

Vypracoval	P. BARTUSEK	Zak. číslo	21-L113-001
Zodp. projektant	ING. T. KLIMENT	Datum	02/2025
Tech. kontrola	ING. M. HANŽL	Stupeň	PDPS
Akce I/16 MLADÁ BOLESLAV - MARTINOVICE		Počet formátů	4 x A4
		Měřítko	1 : 50
		Č. přílohy	Paré
Příloha		VZOROVÝ PŘÍČNÝ ŘEZ	

4