




SO 152 - PŘÍSTUPY NA POZEMKY k.ú. ŽIDNĚVES
PŘÍČNÉ ŘEZY SO 152.1, M 1 : 100

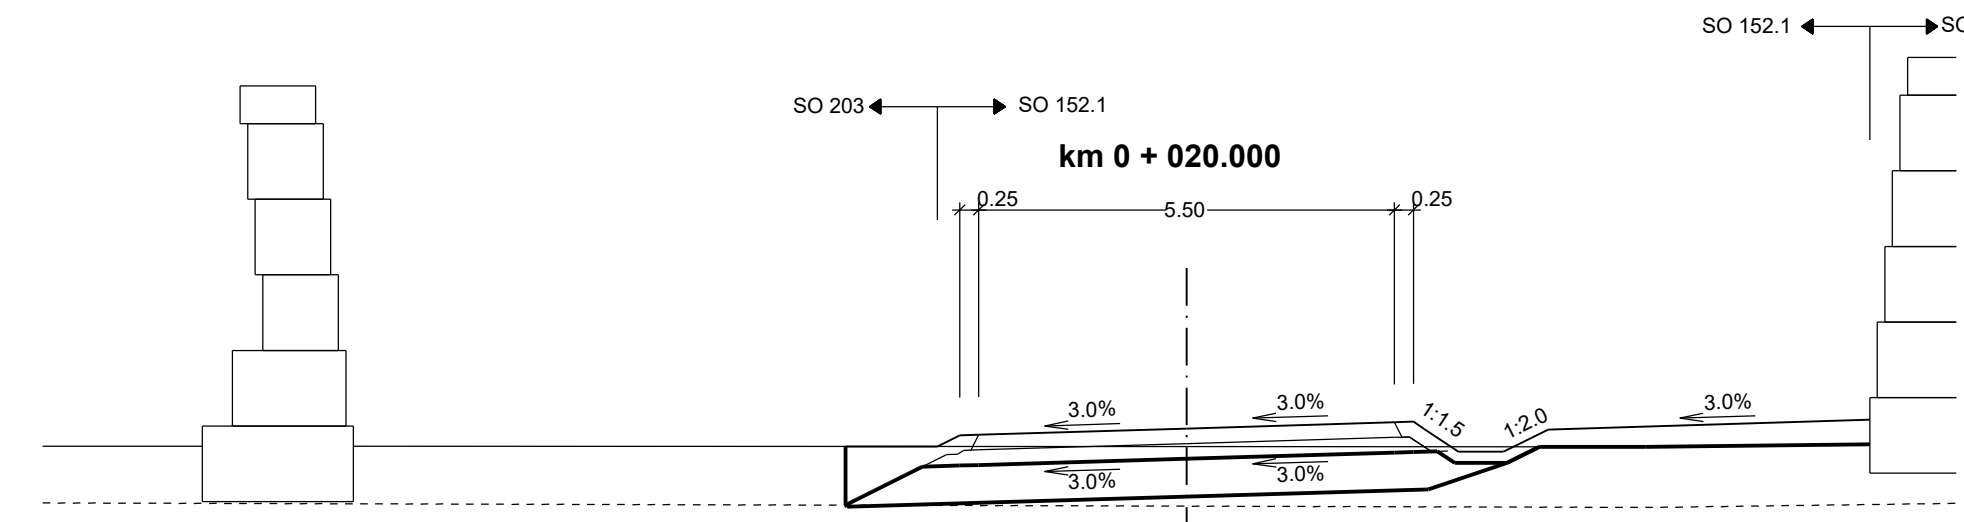


PROJEKTOVANÝ STAV	
ODSAZENÍ OD OSY	-4.51 216.00 -3.30 216.00 -2.75 216.04 0.00 216.03 2.75 216.01 3.00 216.02 3.30 216.04 4.10 216.02 4.80 216.02
STÁVAJÍCÍ TERÉN	
ODSAZENÍ OD OSY	6.07 216.08 9.04 216.04

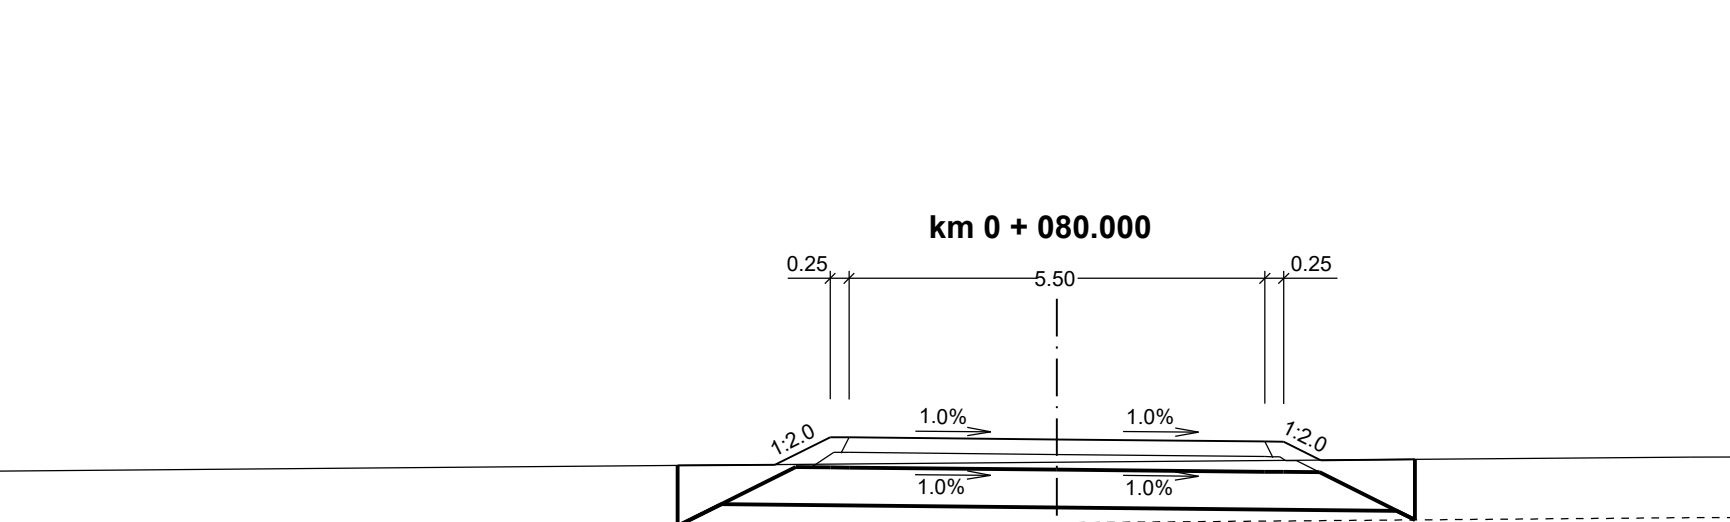


PROJEKTOVANÝ STAV	
ODSAZENÍ OD OSY	-6.02 216.44 -3.72 216.45 -2.75 216.01 0.00 216.79 2.75 216.72 3.00 216.72 3.40 216.51 4.71 216.52
STÁVAJÍCÍ TERÉN	
ODSAZENÍ OD OSY	8.37 216.55

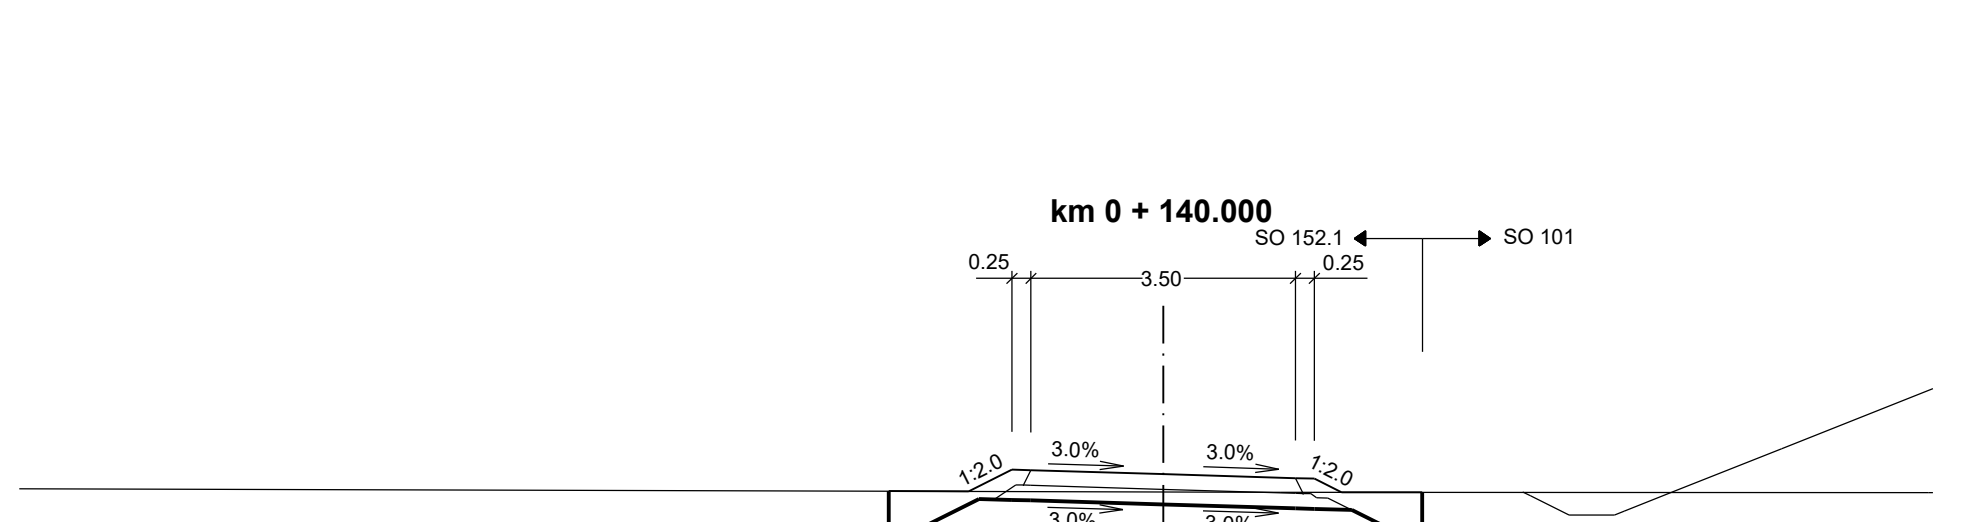


PROJEKTOVANÝ STAV	
ODSAZENÍ OD OSY	-3.63 216.10 -2.57 216.10 -2.00 216.38 -1.75 216.37 0.00 216.52 1.75 216.57 2.00 216.25 2.30 216.08 3.42 216.08
STÁVAJÍCÍ TERÉN	
ODSAZENÍ OD OSY	1.56 216.08

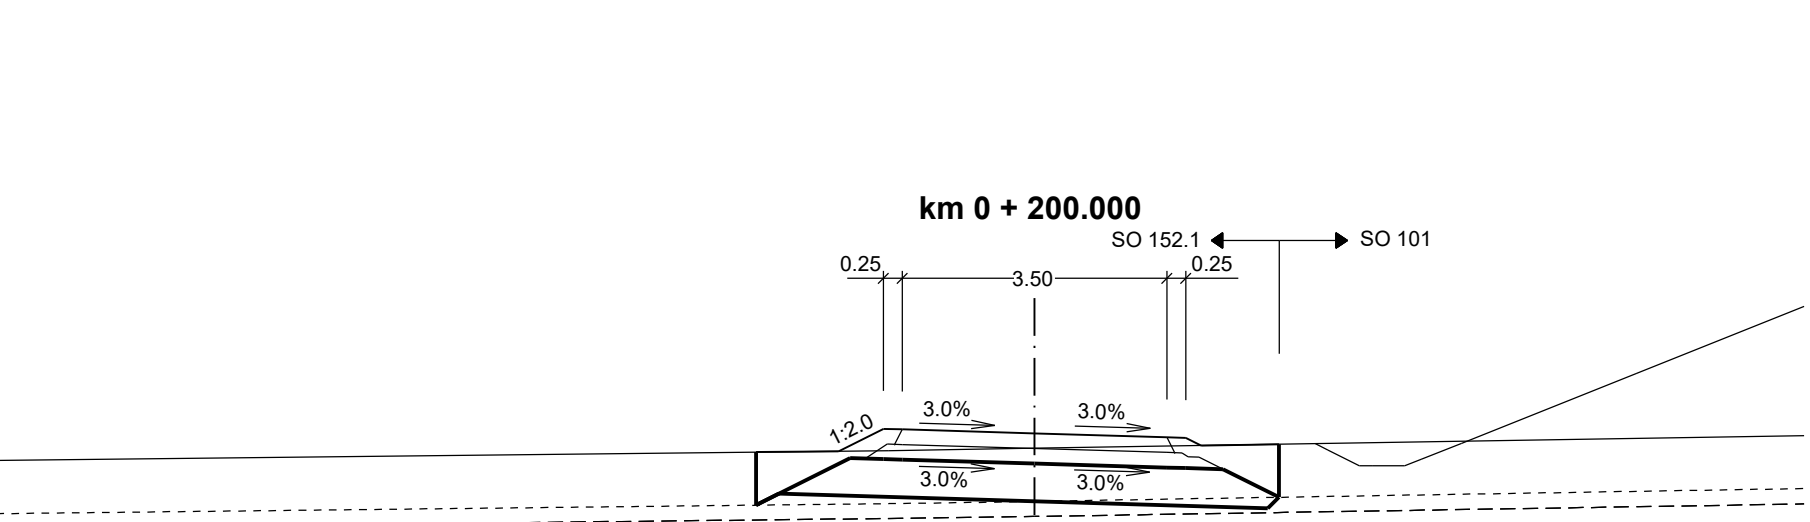


PROJEKTOVANÝ STAV	
ODSAZENÍ OD OSY	-3.80 216.01 -2.80 216.03 -2.00 216.42 -1.75 216.01 0.00 216.06 1.75 216.81 2.00 216.70 2.30 216.72
STÁVAJÍCÍ TERÉN	
ODSAZENÍ OD OSY	1.56 216.08

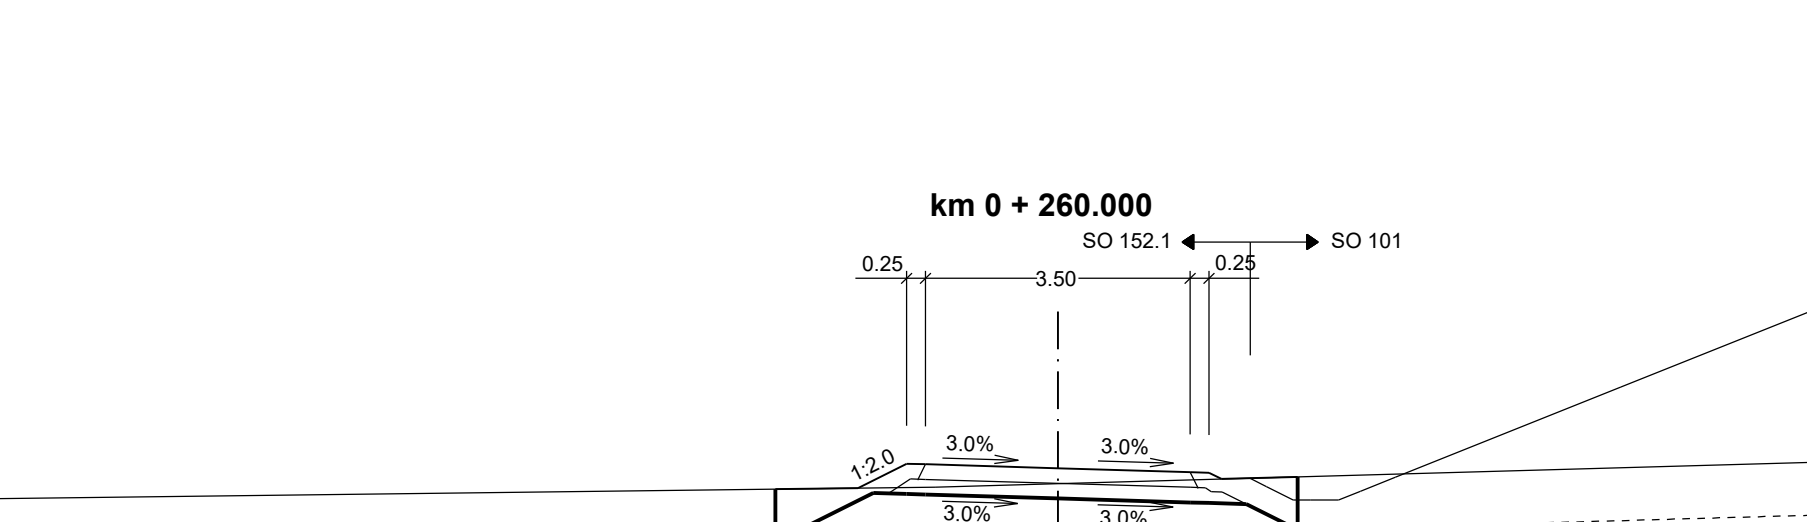


PROJEKTOVANÝ STAV	
ODSAZENÍ OD OSY	-3.74 220.12 -2.84 220.14 -2.00 220.48 -1.75 220.45 0.00 220.40 1.75 220.52 2.00 220.34 2.18 220.26 3.17 220.29
STÁVAJÍCÍ TERÉN	
ODSAZENÍ OD OSY	1.56 216.08

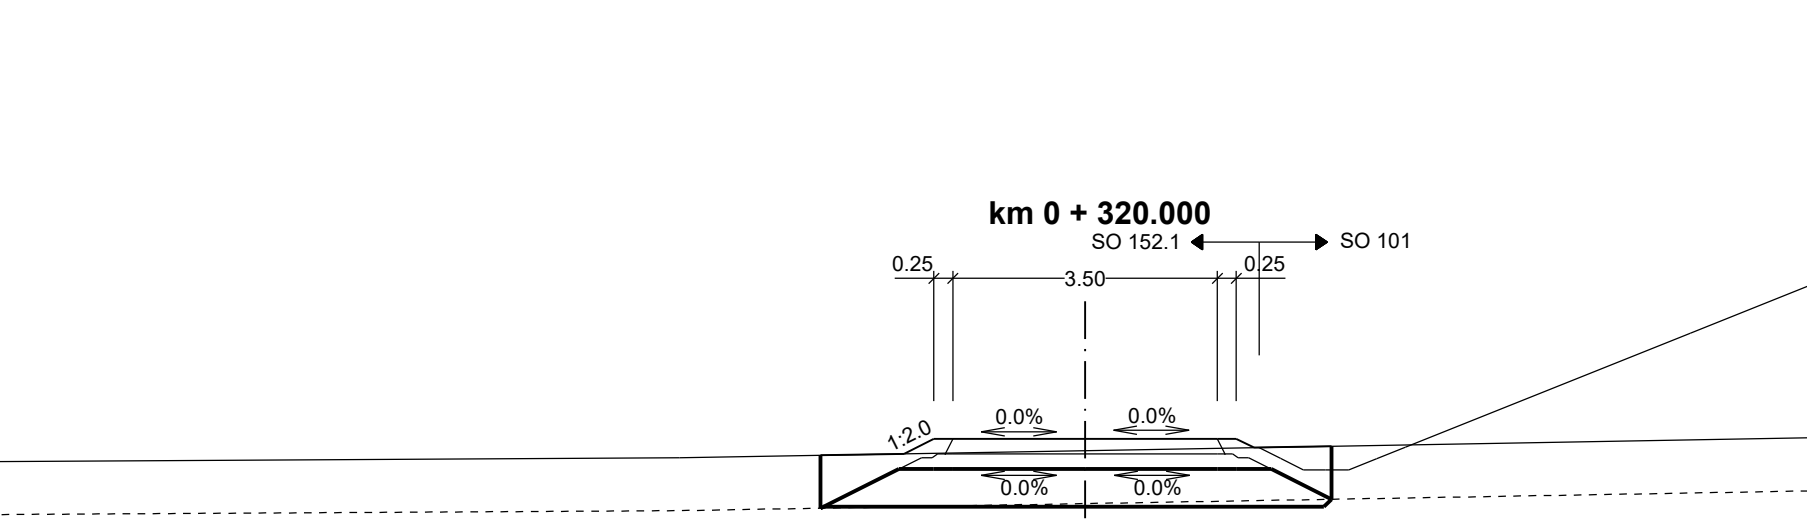


PROJEKTOVANÝ STAV	
ODSAZENÍ OD OSY	-3.60 226.67 -2.40 226.69 -2.00 226.79 -1.75 226.79 0.00 226.79 1.75 226.79 2.00 226.87 2.31 226.67 3.38 226.69
STÁVAJÍCÍ TERÉN	
ODSAZENÍ OD OSY	1.56 216.08

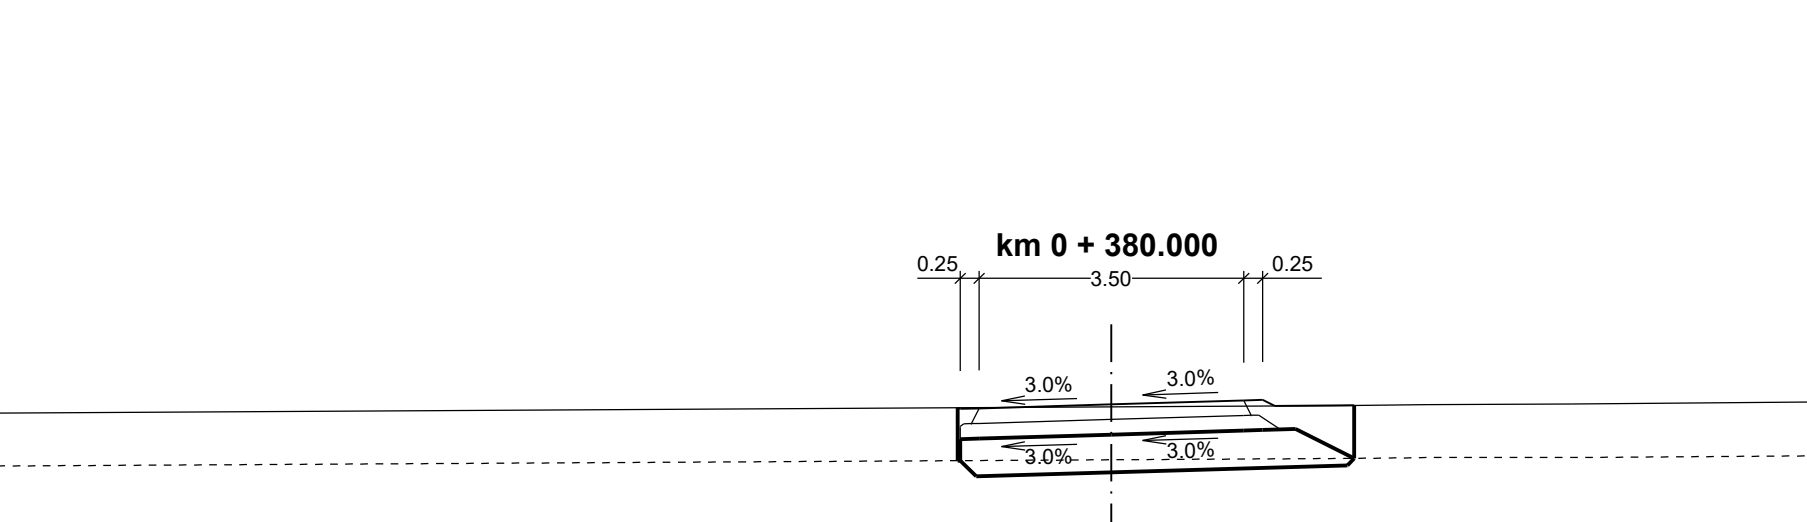


PROJEKTOVANÝ STAV	
ODSAZENÍ OD OSY	-2.03 221.20 -2.00 221.19 -1.75 221.19 0.00 221.25 1.75 221.30 2.00 221.31 2.16 221.23 3.21 221.23
STÁVAJÍCÍ TERÉN	
ODSAZENÍ OD OSY	1.56 216.08

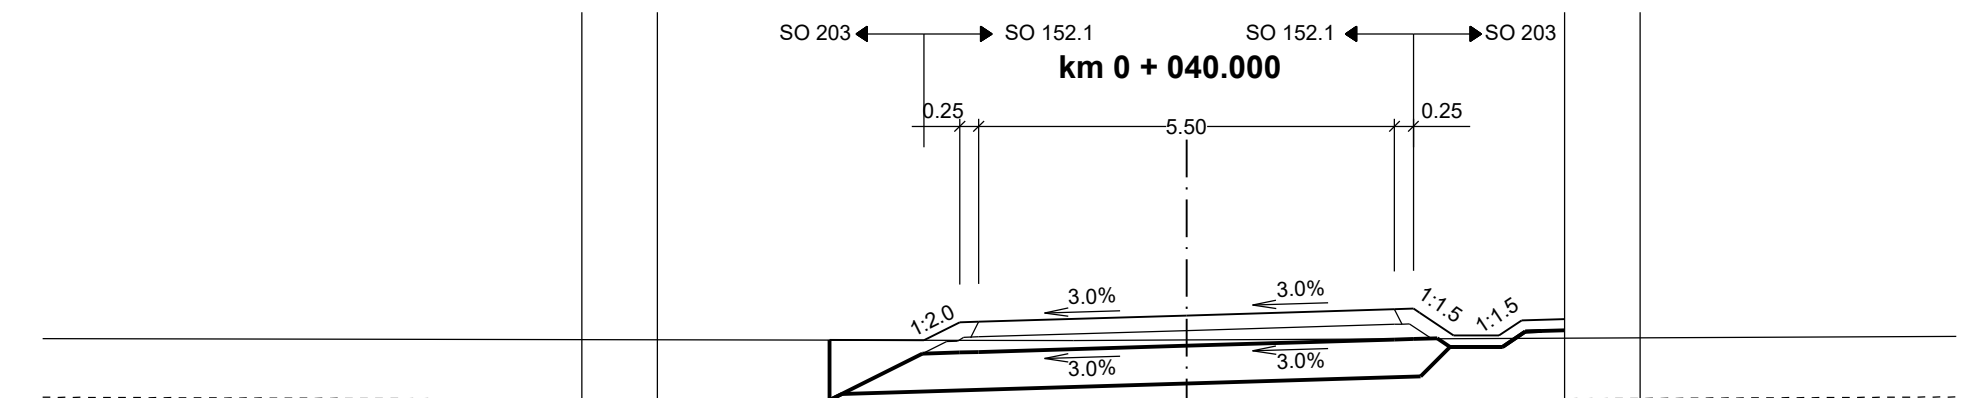


PROJEKTOVANÝ STAV	
ODSAZENÍ OD OSY	-4.72 216.50 -3.47 216.50 -2.75 216.74 -2.75 216.74 0.00 216.50 2.75 216.51 3.00 216.52 3.30 216.56 4.13 216.56 4.70 216.77
STÁVAJÍCÍ TERÉN	
ODSAZENÍ OD OSY	-1.49 216.50 0.00 216.50

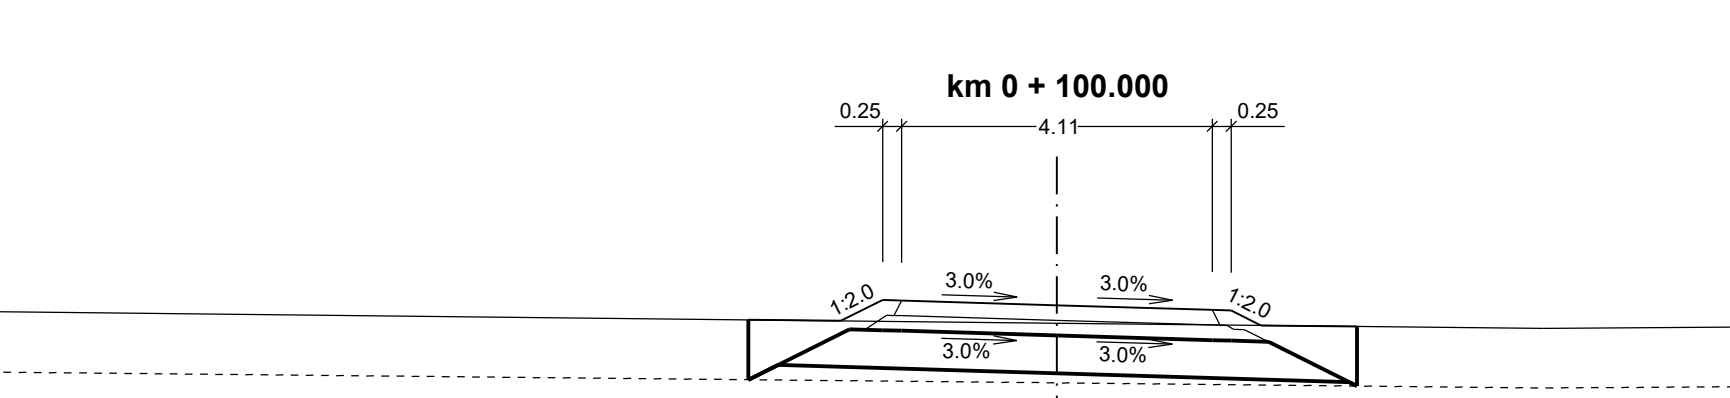


PROJEKTOVANÝ STAV	
ODSAZENÍ OD OSY	-4.68 216.77 -2.86 216.76 -2.00 216.03 -2.00 216.02 0.00 216.96 2.00 216.96 2.30 216.70 3.07 216.88
STÁVAJÍCÍ TERÉN	
ODSAZENÍ OD OSY	6.43 216.86

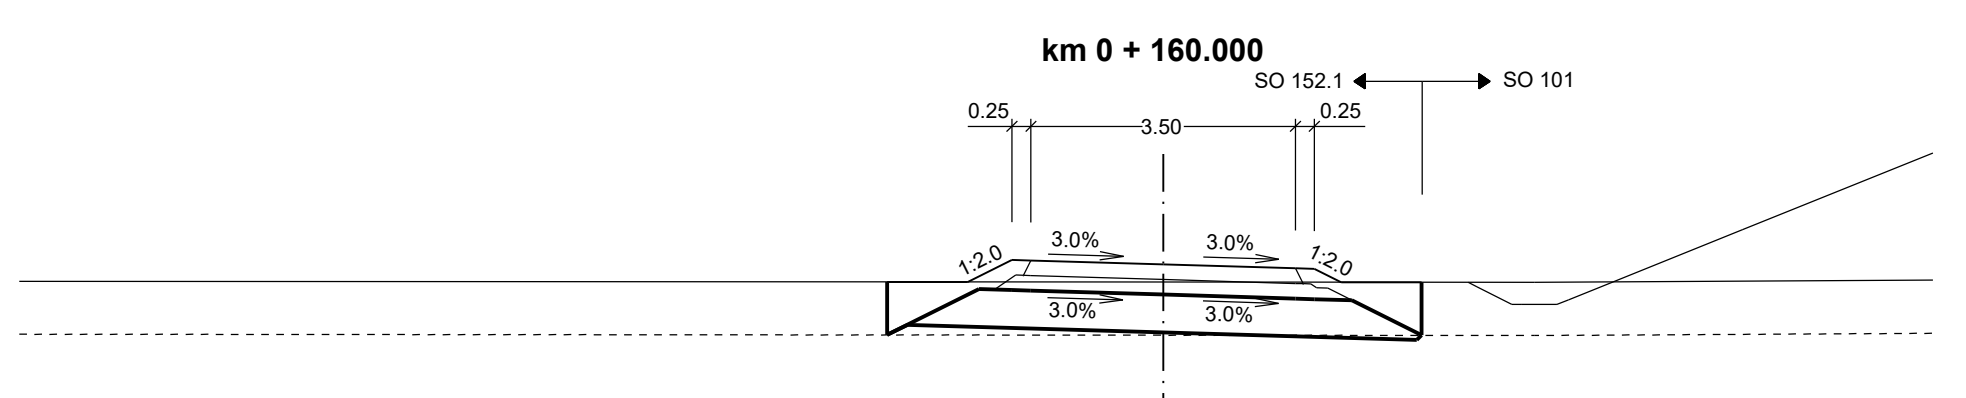


PROJEKTOVANÝ STAV	
ODSAZENÍ OD OSY	-3.65 219.27 -2.59 219.27 -2.00 219.56 -1.75 219.55 0.00 219.50 1.75 219.54 2.00 219.44 2.30 219.27 3.42 219.35
STÁVAJÍCÍ TERÉN	
ODSAZENÍ OD OSY	4.51 219.36

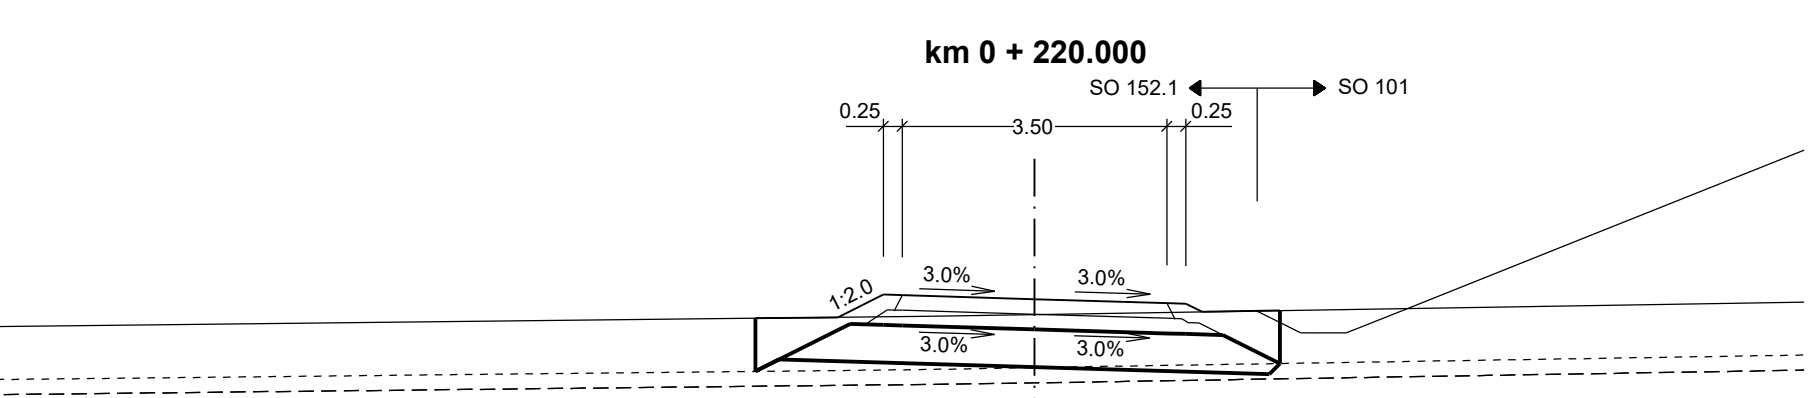


PROJEKTOVANÝ STAV	
ODSAZENÍ OD OSY	-3.69 220.30 -2.60 220.31 -2.00 220.61 -1.75 220.60 0.00 220.44 1.75 219.99 2.00 220.49 2.30 219.87 3.25 219.89
STÁVAJÍCÍ TERÉN	
ODSAZENÍ OD OSY	-1.35 219.82 0.00 219.84

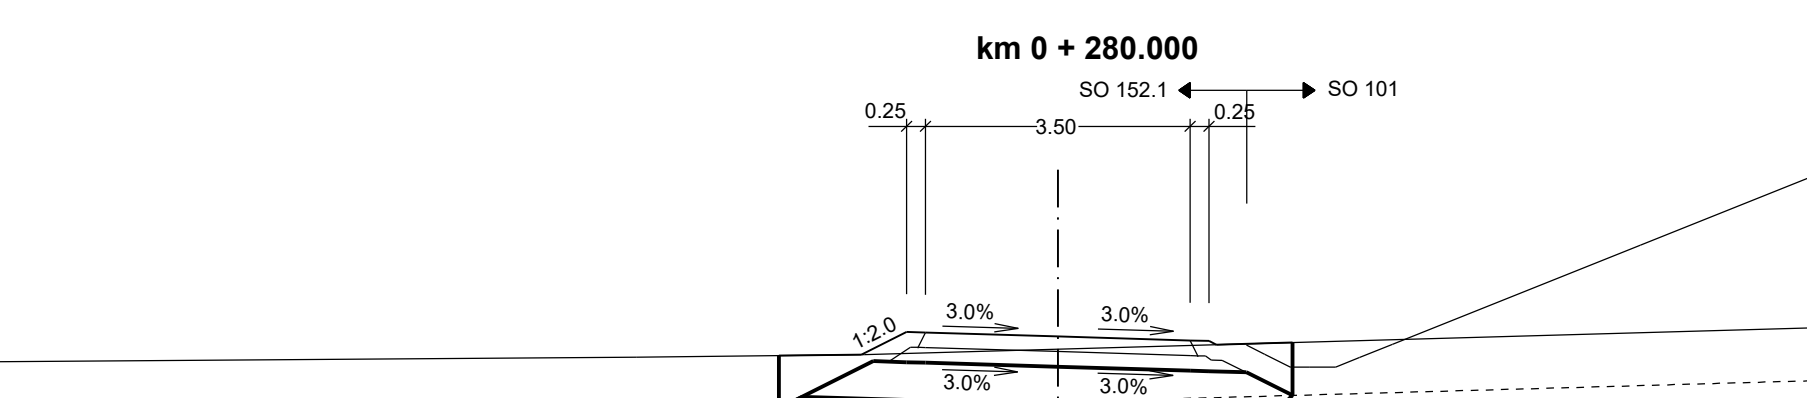


PROJEKTOVANÝ STAV	
ODSAZENÍ OD OSY	-3.69 220.30 -2.60 220.31 -2.00 220.61 -1.75 220.60 0.00 220.44 1.75 219.99 2.00 220.49 2.30 219.87 3.25 219.89
STÁVAJÍCÍ TERÉN	
ODSAZENÍ OD OSY	-5.57 220.27 -2.55 220.31 0.00 220.38 1.29 220.71

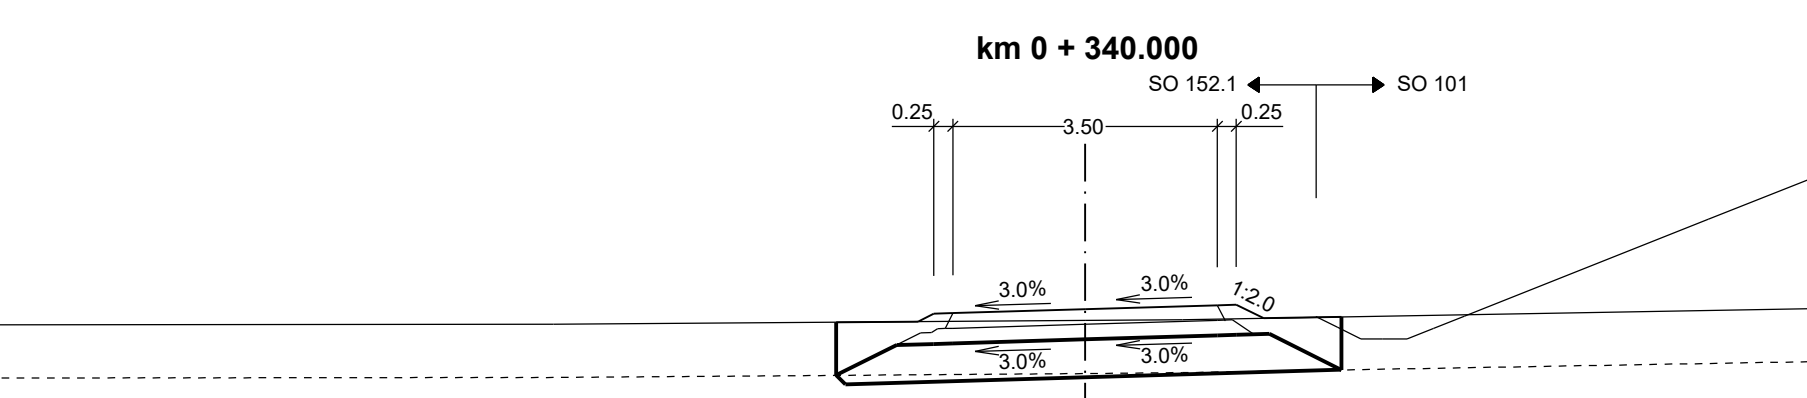


PROJEKTOVANÝ STAV	
ODSAZENÍ OD OSY	-3.59 220.74 -2.51 220.74 -2.00 220.96 -1.75 220.96 0.00 220.91 1.75 220.96 2.00 220.96 2.30 220.79 3.39 220.81
STÁVAJÍCÍ TERÉN	
ODSAZENÍ OD OSY	-7.03 220.71 0.00 220.76 1.29 220.77

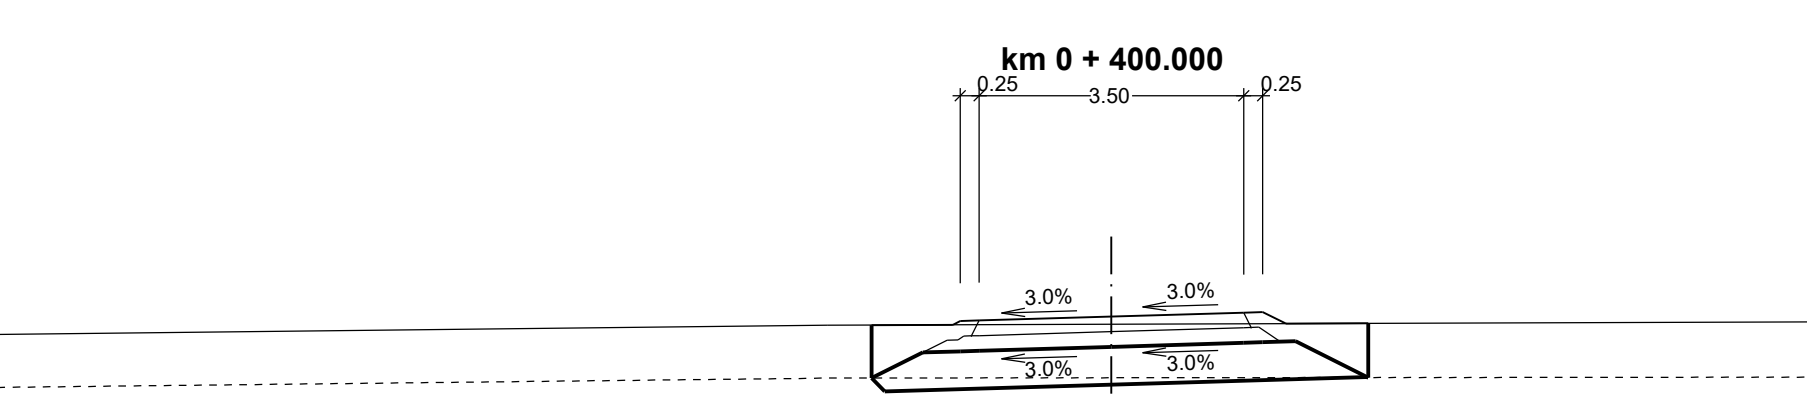


PROJEKTOVANÝ STAV	
ODSAZENÍ OD OSY	-3.17 221.70 -2.10 221.70 -2.00 221.75 -1.75 221.75 0.00 221.81 1.75 221.85 2.00 221.87 2.31 221.72 3.40 221.72
STÁVAJÍCÍ TERÉN	
ODSAZENÍ OD OSY	0.00 221.71

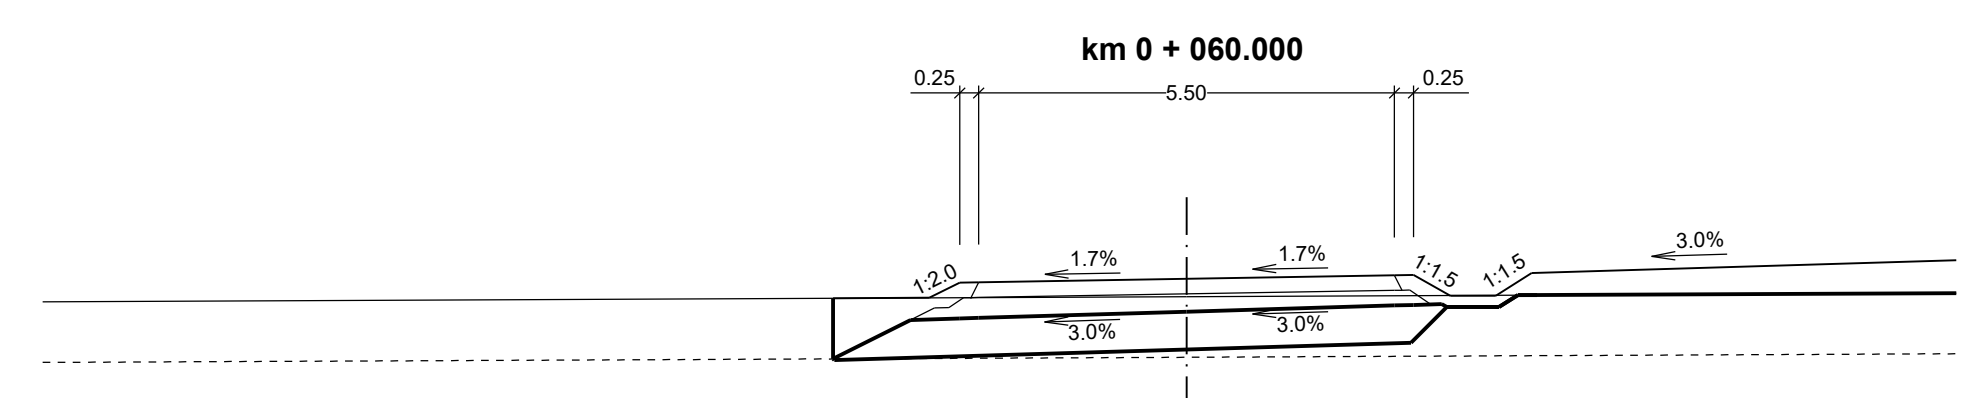


PROJEKTOVANÝ STAV	
ODSAZENÍ OD OSY	-4.68 216.47 -3.40 216.47 -2.75 216.88 -2.75 216.88 0.00 216.49 2.75 216.78 3.00 216.78 3.49 216.50 4.09 216.50 4.56 216.50
STÁVAJÍCÍ TERÉN	
ODSAZENÍ OD OSY	0.00 216.49

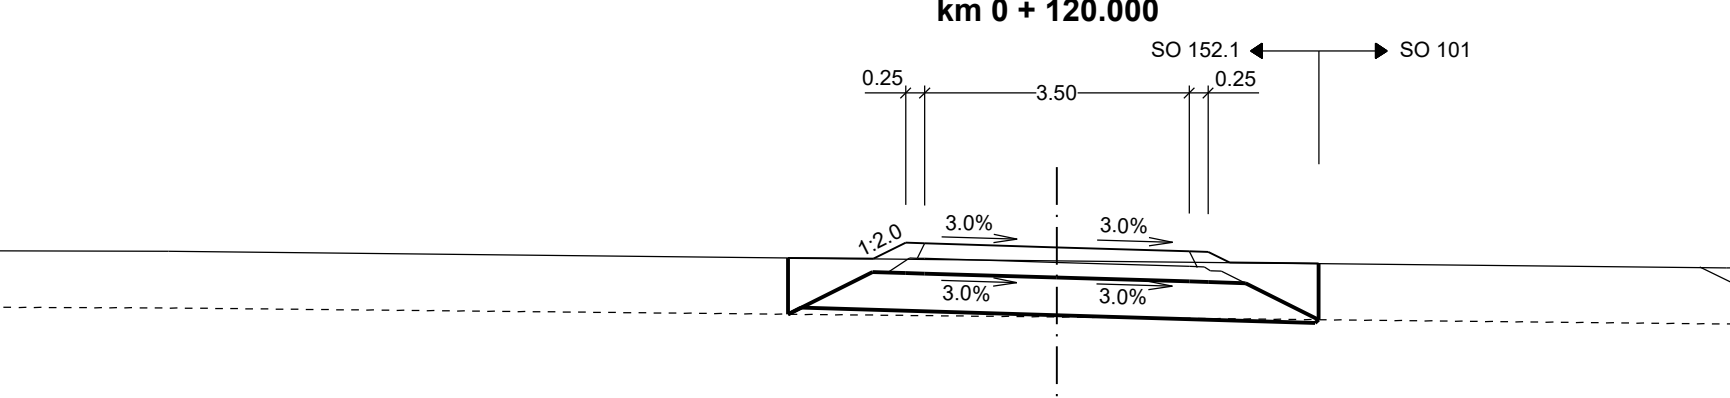


PROJEKTOVANÝ STAV	
ODSAZENÍ OD OSY	-3.56 219.30 -2.42 219.30 -2.00 219.74 -1.75 219.73 0.00 219.14 1.75 219.30 2.00 219.62 2.30 219.64 3.46 216.53
STÁVAJÍCÍ TERÉN	
ODSAZENÍ OD OSY	6.06 216.57

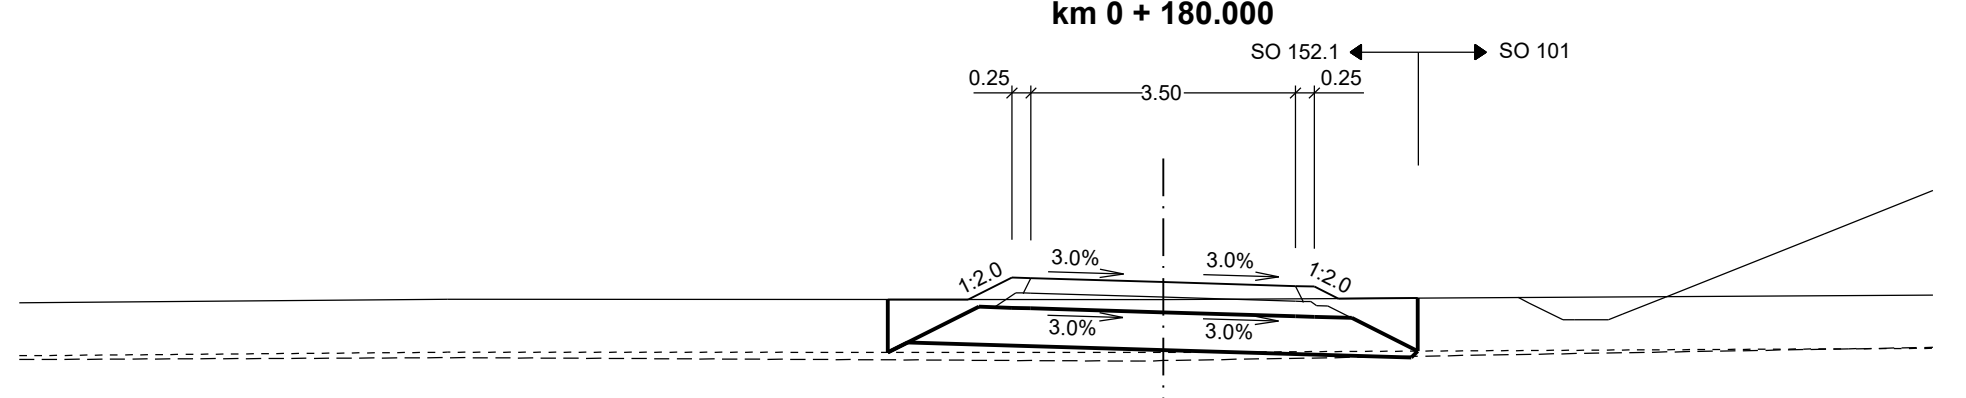


PROJEKTOVANÝ STAV	
ODSAZENÍ OD OSY	-3.65 219.45 -2.58 219.45 -2.00 219.74 -1.75 219.73 0.00 219.68 1.75 219.62 2.00 219.62 2.30 219.46 3.37 219.47
STÁVAJÍCÍ TERÉN	
ODSAZENÍ OD OSY	-0.31 219.45 0.00 219.45

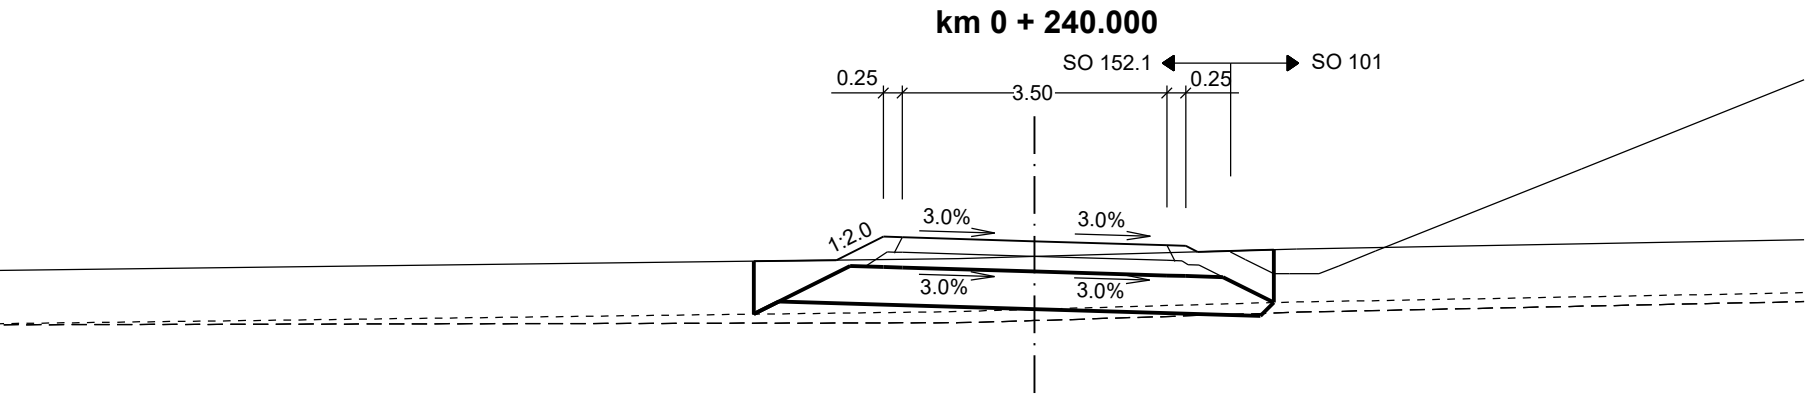

PROJEKTOVANÝ STAV	
ODSAZENÍ OD OSY	-3.71 219.96 -2.62 219.97 -2.00 220.27 -1.75 220.27 0.00 220.22 1.75 220.17 2.00 220.18 2.16 220.08 3.17 220.11
STÁVAJÍCÍ TERÉN	
ODSAZENÍ OD OSY	-0.00 220.02 3.47 220.12

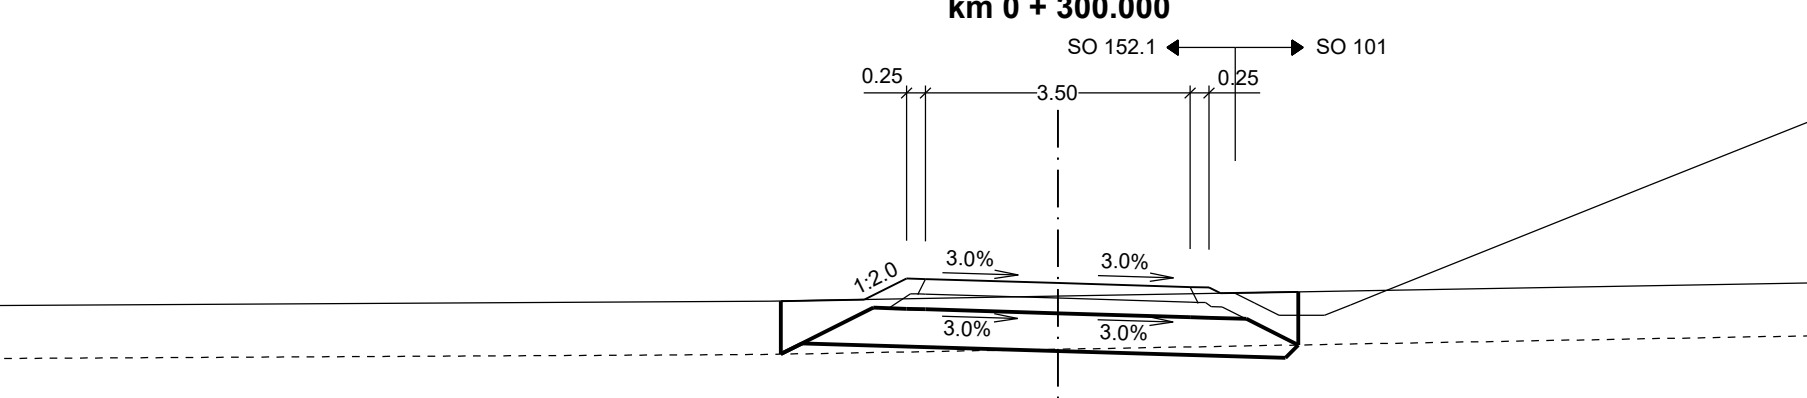

PROJEKTOVANÝ STAV	
ODSAZENÍ OD OSY	-3.68 220.43 -2.56 220.45 -2.00 220.73 -1.75 220.72 0.00 220.57 1.75 220.52 2.00 220.81 2.14 220.53 3.18 220.55
STÁVAJÍCÍ TERÉN	
ODSAZENÍ OD OSY	0.00 220.49

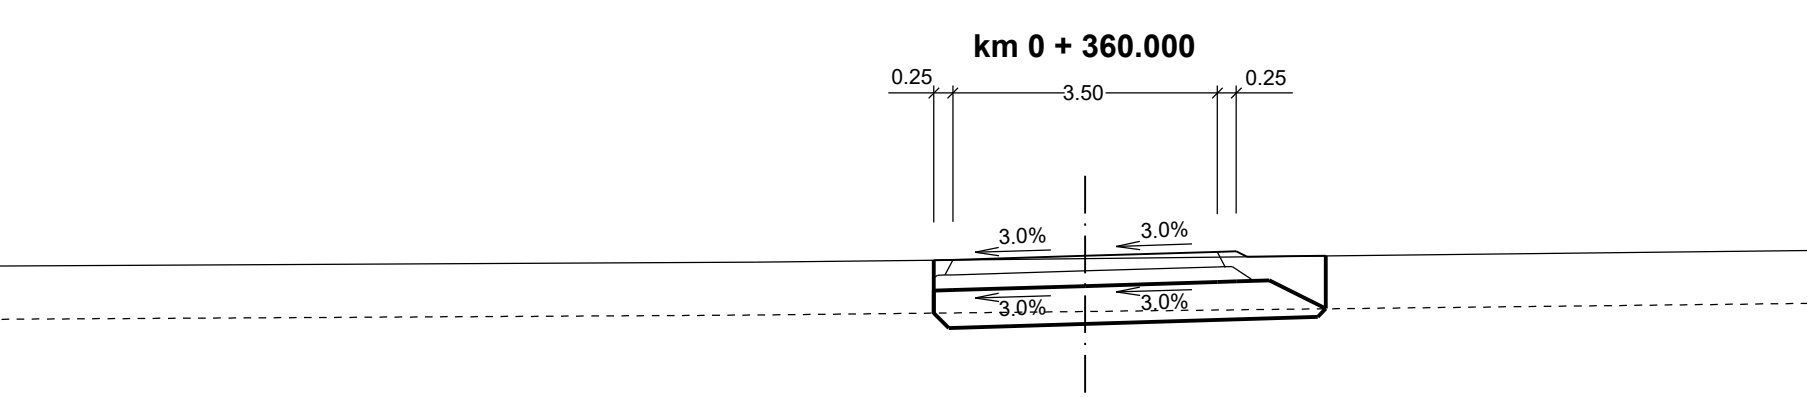

PROJEKTOVANÝ STAV	
ODSAZENÍ OD OSY	-2.00 220.97 -1.75 220.96 0.00 221.03 1.75 221.08 2.00 221.02 2.14 221.02 3.18 221.03
STÁVAJÍCÍ TERÉN	
ODSAZENÍ OD OSY	-4.35 220.95 0.00 220.99

Výkresový systém: Bpv

SO 152 Přístupy na pozemky k.ú. Židněves

Objednatel: ŘEDITELSTVÍ SILNIC A DÁLNIC
Ředitelství silnic a dálnic s. p.
Čerňanská 2023/12, Krč, 140 00 Praha 4

Zhotovitel: Valbek
Valbek, spol. s r.o.
Vaňurova 505/17
460 07 Liberec 3

Valbek	Vypracoval: P. BARTUSEK Zodp. projektant: ING. T. KLIMENT Tech. kontrola: ING. M. HANŽL Akce: I/16 MLADÁ BOLESLAV - MARTINOVICE	Zak. číslo: 21-L113-001 Datum: 02/2025 Stupeň: P01P Počet formátů: 20 x A4 Měřítko: 1:100 Č. přílohy: Paré	5.1
Zhotovitel: Valbek, spol. s r.o. Vaňurova 505/17 460 07 Liberec 3	Příloha: PŘÍČNÉ ŘEZY SO 152.1		