




SO 152 - PŘÍSTUPY NA POZEMKY k.ú. ŽIDNĚVES
PŘÍČNÉ REZY SO 152.2 - km 0,020 - 0,420, M 1 : 100

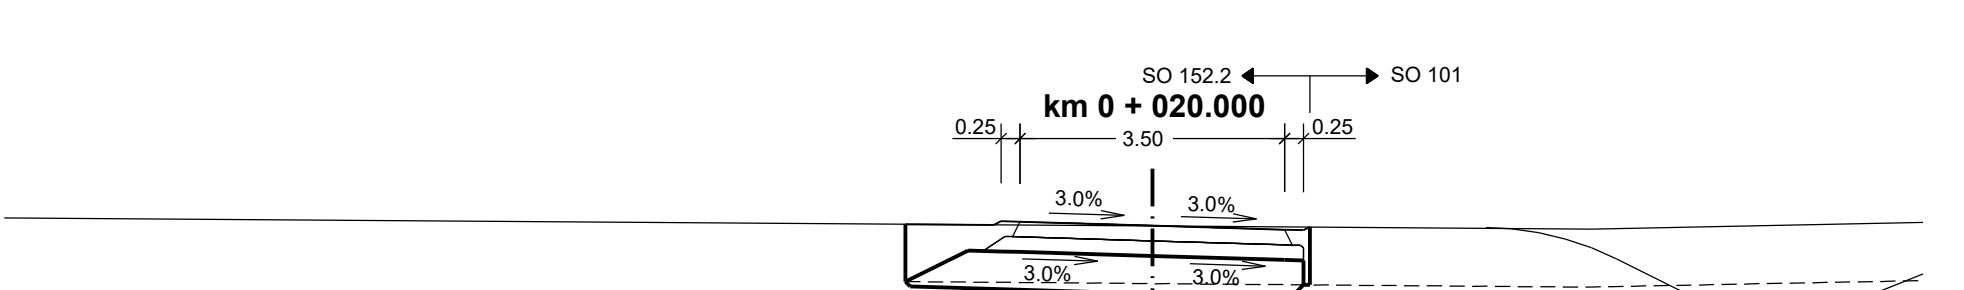


PROJEKTOVANÝ STAV	
ODSAZENÍ OD OSY	-3.27 219.25 -2.36 221.01 -2.00 219.25 -1.75 219.28 0.00 219.23 1.75 219.18 2.00 219.17 2.08 219.21 5.81 219.19
STÁVAJÍCÍ TERÉN	
ODSAZENÍ OD OSY	0.00 219.23 5.81 219.19

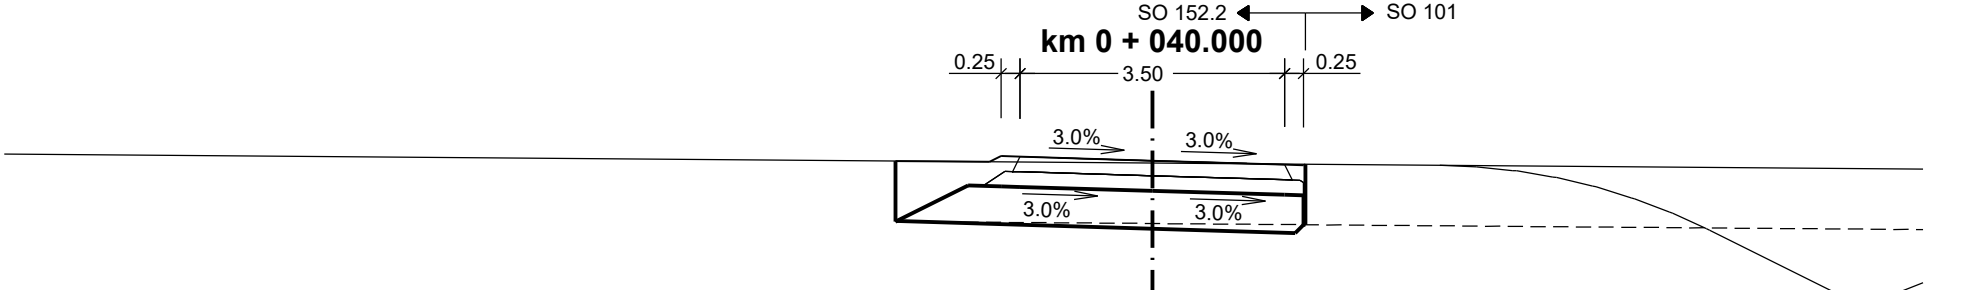


PROJEKTOVANÝ STAV	
ODSAZENÍ OD OSY	-3.40 219.80 -2.35 221.22 -2.00 219.87 -1.75 219.86 0.00 219.81 1.75 219.75 2.00 219.75 2.02 219.76 0.00 219.78
STÁVAJÍCÍ TERÉN	
ODSAZENÍ OD OSY	0.00 219.78

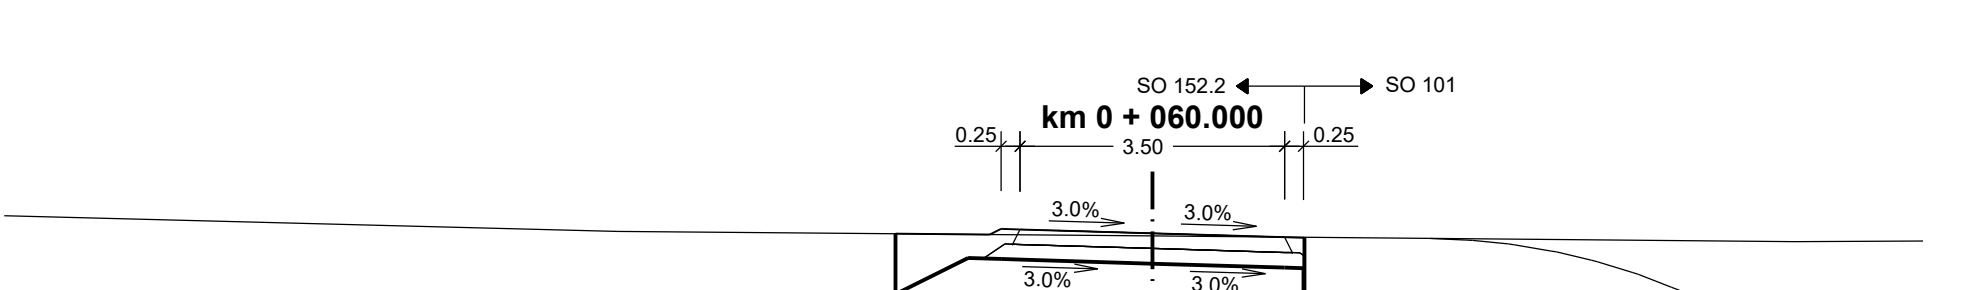


PROJEKTOVANÝ STAV	
ODSAZENÍ OD OSY	-3.40 220.36 -2.68 221.41 -2.00 220.33 -1.75 220.42 0.00 220.37 1.75 220.32 2.00 220.31 2.01 220.31 0.00 220.33 7.08 220.39 8.50 220.38
STÁVAJÍCÍ TERÉN	
ODSAZENÍ OD OSY	0.00 220.33 7.08 220.39 8.50 220.38

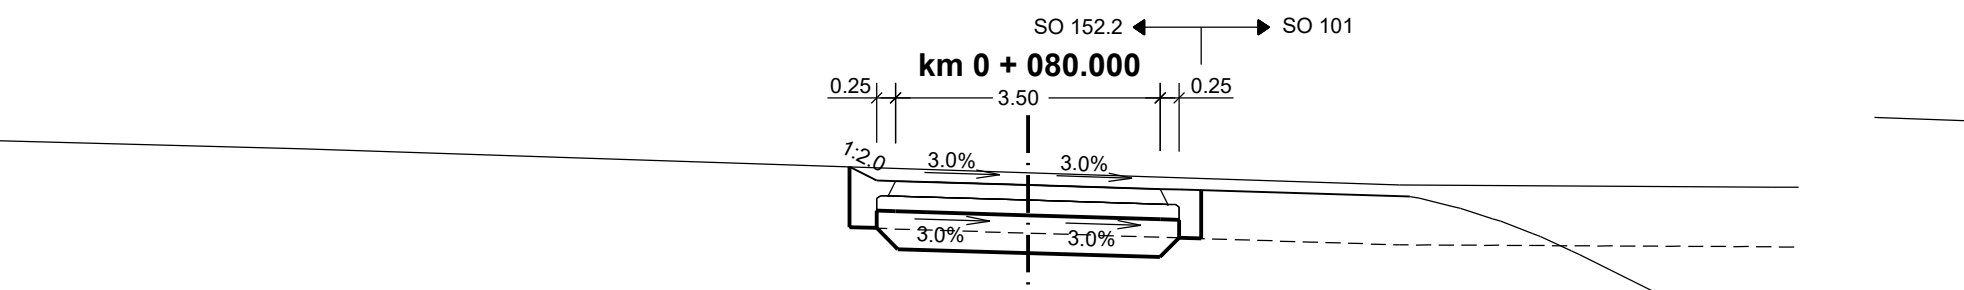


PROJEKTOVANÝ STAV	
ODSAZENÍ OD OSY	-2.54 221.21 -2.00 219.61 -1.75 220.82 0.00 220.77 1.75 220.72 2.00 220.71 2.29 220.85 4.92 220.77 9.54 220.74
STÁVAJÍCÍ TERÉN	
ODSAZENÍ OD OSY	-4.80 221.25 0.00 220.93 4.92 220.77 9.54 220.74

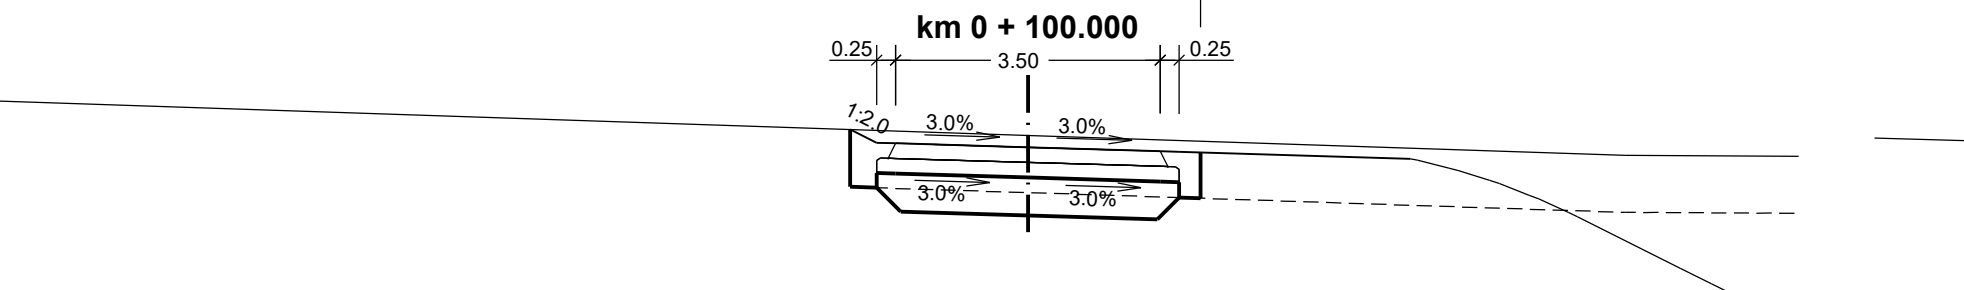


PROJEKTOVANÝ STAV	
ODSAZENÍ OD OSY	-2.35 221.22 -2.00 219.87 -1.75 221.04 0.00 220.96 1.75 220.93 2.00 220.93 2.28 221.07 0.00 221.14 7.90 220.88
STÁVAJÍCÍ TERÉN	
ODSAZENÍ OD OSY	0.00 221.14 7.90 220.88

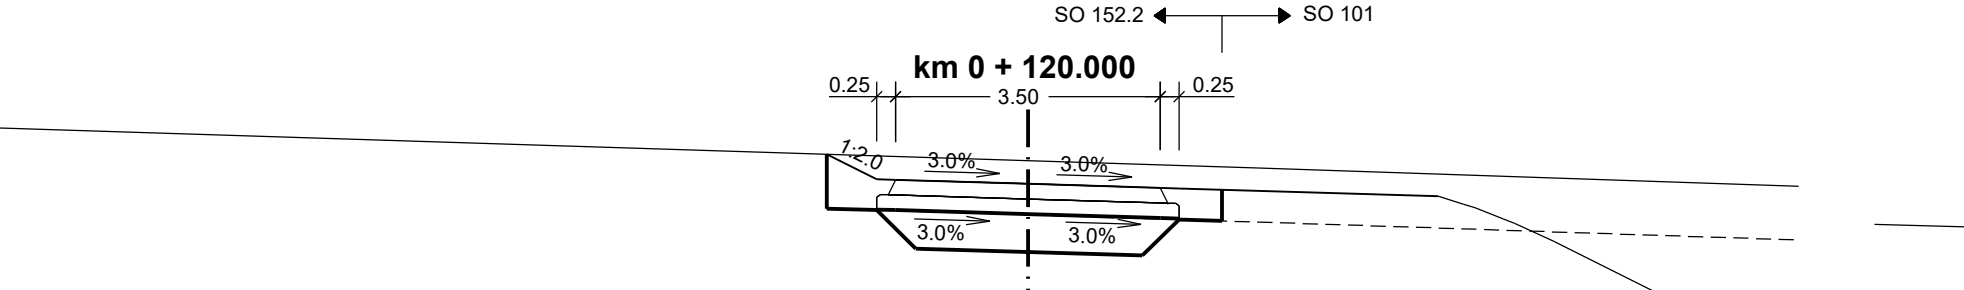


PROJEKTOVANÝ STAV	
ODSAZENÍ OD OSY	-2.68 221.41 -2.00 221.08 -1.75 221.08 0.00 221.02 1.75 220.97 2.00 220.96 2.01 220.96 0.00 221.02 3.07 221.23 4.32 219.95
STÁVAJÍCÍ TERÉN	
ODSAZENÍ OD OSY	0.00 221.02 3.07 221.23 4.32 219.95

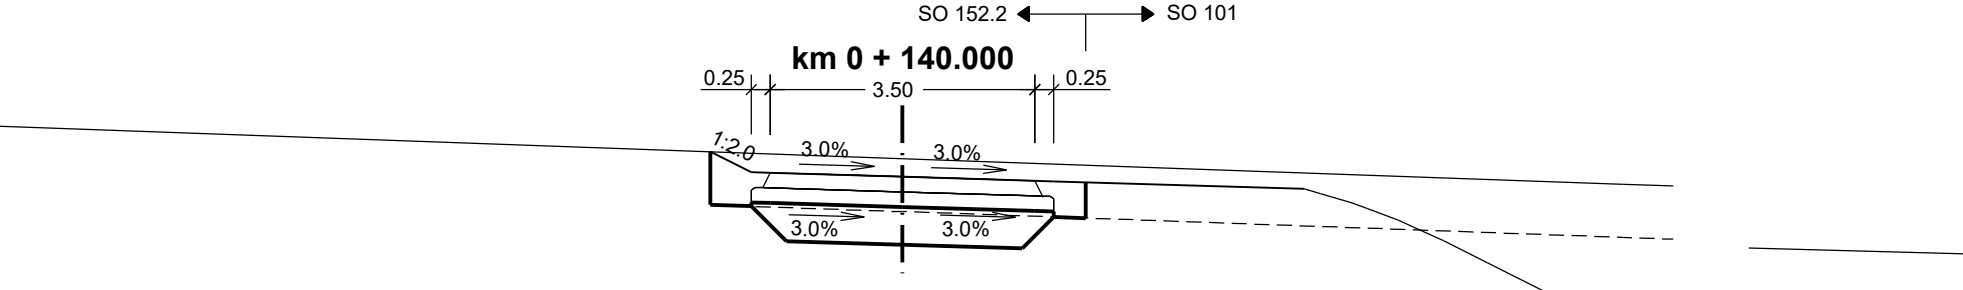


PROJEKTOVANÝ STAV	
ODSAZENÍ OD OSY	-2.54 221.21 -2.00 219.61 -1.75 220.83 0.00 220.86 1.75 220.82 2.00 220.82 2.42 221.03 0.00 221.12 9.53 220.78
STÁVAJÍCÍ TERÉN	
ODSAZENÍ OD OSY	0.00 221.12 9.53 220.78

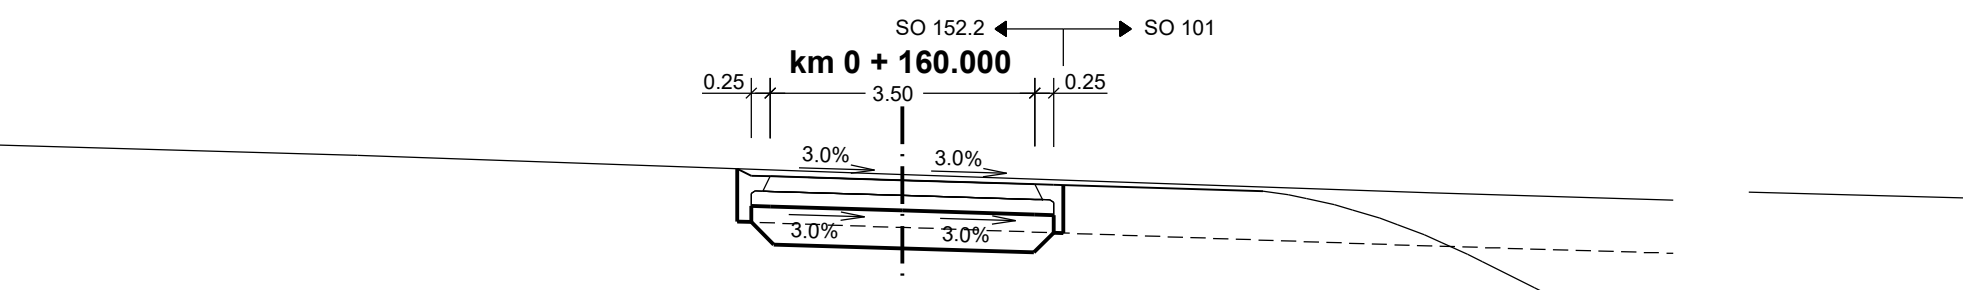


PROJEKTOVANÝ STAV	
ODSAZENÍ OD OSY	-2.19 220.70 -2.00 219.23 -1.75 220.60 0.00 220.55 1.75 220.50 2.00 220.49 2.13 220.55 0.00 220.63 6.88 220.38
STÁVAJÍCÍ TERÉN	
ODSAZENÍ OD OSY	-7.21 220.88 0.00 220.63 6.88 220.38

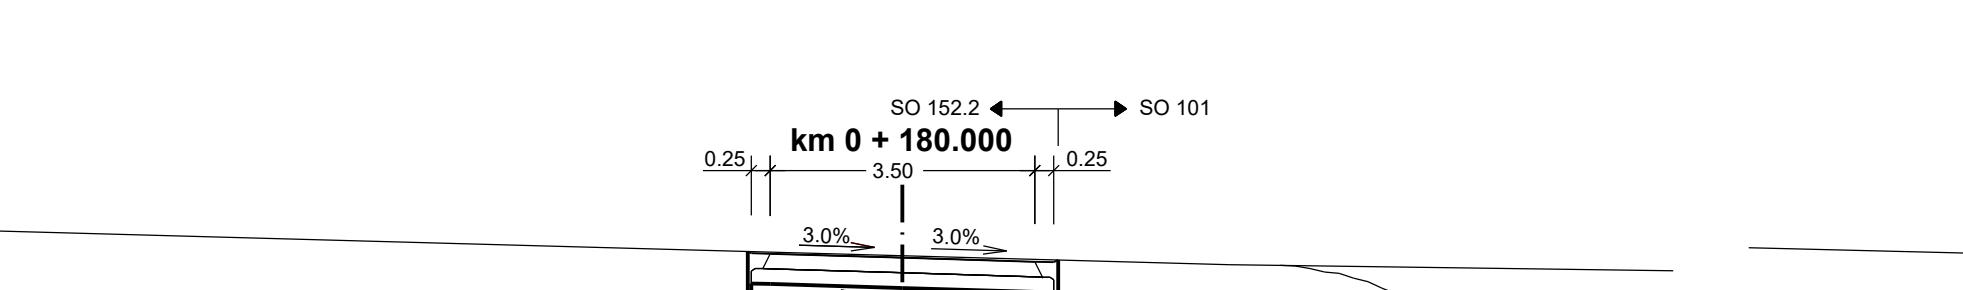


PROJEKTOVANÝ STAV	
ODSAZENÍ OD OSY	-2.05 220.13 -2.00 219.99 -1.75 220.10 0.00 220.05 1.75 219.99 2.00 220.00 2.06 220.02 0.00 220.07 4.32 219.95
STÁVAJÍCÍ TERÉN	
ODSAZENÍ OD OSY	0.00 220.07 4.32 219.95

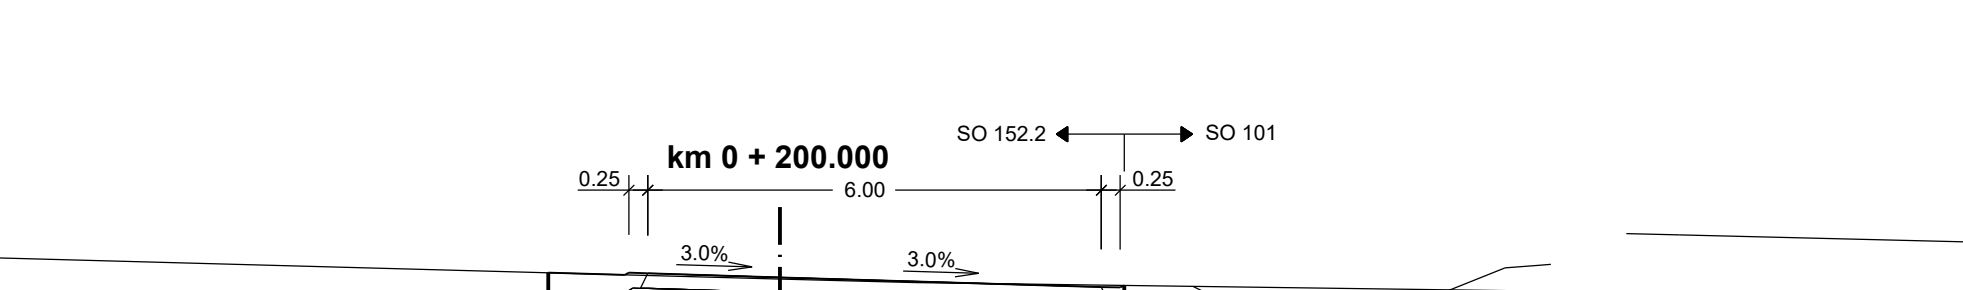


PROJEKTOVANÝ STAV	
ODSAZENÍ OD OSY	-3.06 219.61 -2.05 219.86 -2.00 219.61 -1.75 219.63 0.00 219.55 1.75 219.52 2.00 219.52 2.42 221.03 0.00 219.52 1.78 219.48 4.35 219.42 4.50 219.41 4.56 219.44
STÁVAJÍCÍ TERÉN	
ODSAZENÍ OD OSY	0.00 219.52 1.78 219.48 4.35 219.42 4.50 219.41 4.56 219.44

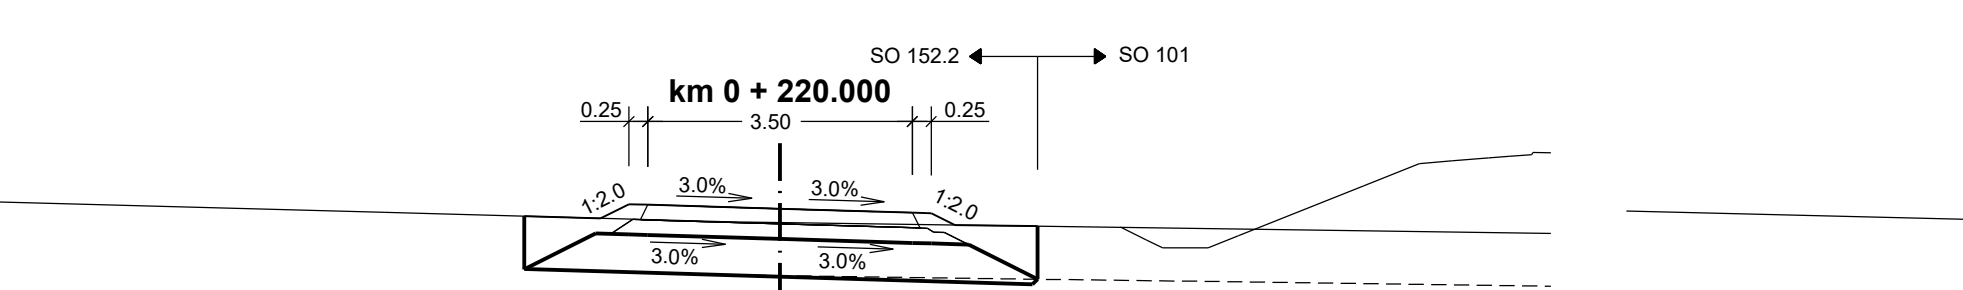


PROJEKTOVANÝ STAV	
ODSAZENÍ OD OSY	-3.39 219.07 -2.38 219.05 -2.00 219.23 -1.75 219.23 0.00 219.17 1.75 219.12 2.00 219.12 2.31 219.96 0.00 219.09 1.78 219.06 3.41 219.94
STÁVAJÍCÍ TERÉN	
ODSAZENÍ OD OSY	-5.24 219.12 0.00 219.09 1.78 219.06 3.41 219.94

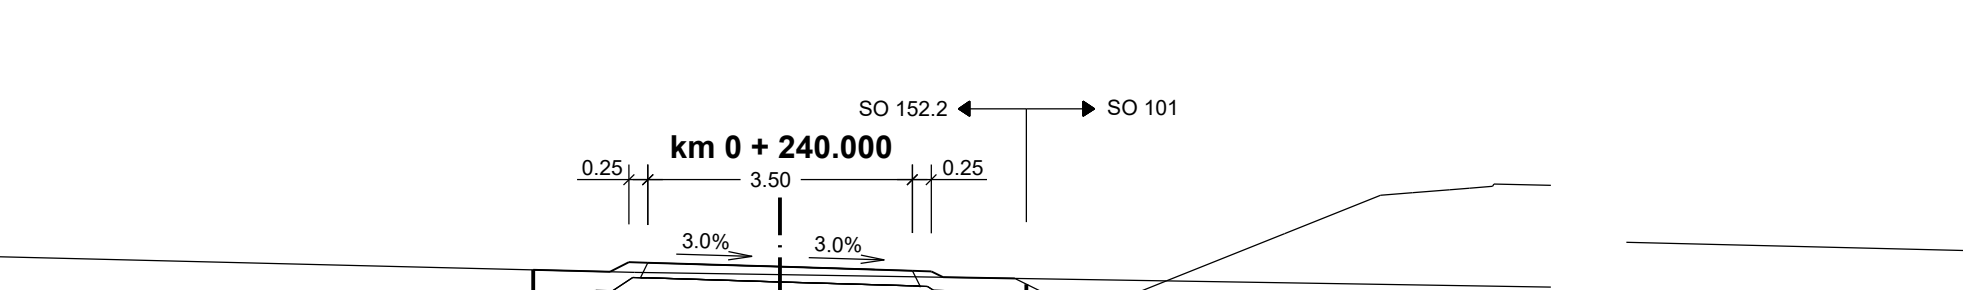


PROJEKTOVANÝ STAV	
ODSAZENÍ OD OSY	-3.13 218.96 -2.12 218.93 -2.00 220.12 -1.75 218.96 0.00 218.93 1.75 218.88 2.00 220.12 2.16 218.79 0.00 218.82 1.75 218.87 2.16 218.79 3.26 218.77
STÁVAJÍCÍ TERÉN	
ODSAZENÍ OD OSY	0.00 218.82 1.75 218.87 2.16 218.79 3.26 218.77

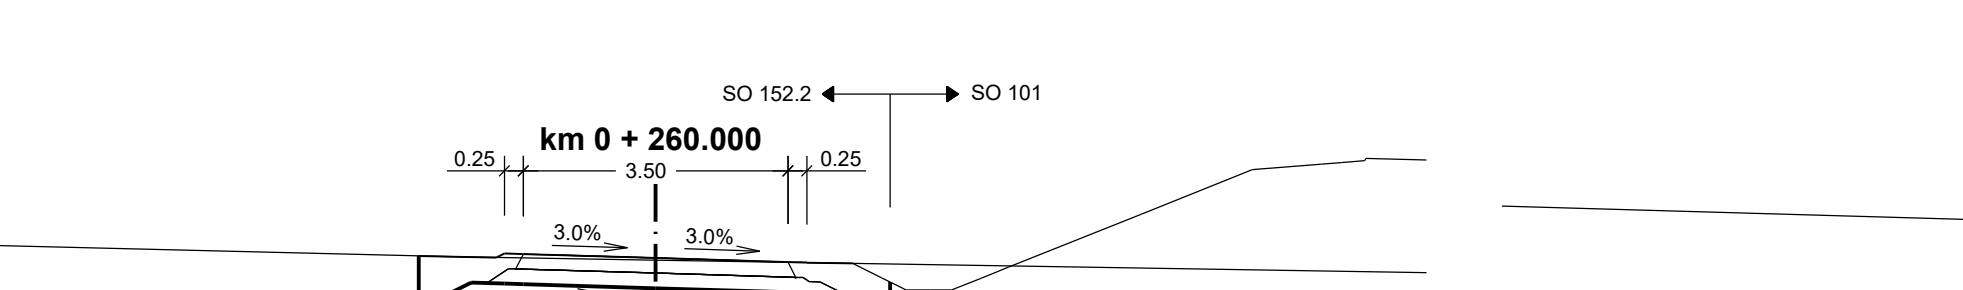


PROJEKTOVANÝ STAV	
ODSAZENÍ OD OSY	-3.13 218.83 -2.11 219.81 -2.00 218.86 -1.75 218.86 0.00 218.80 1.75 218.75 2.00 218.74 3.10 218.72 0.00 218.77 1.75 218.75 2.00 218.74 3.10 218.72
STÁVAJÍCÍ TERÉN	
ODSAZENÍ OD OSY	-2.89 218.82 0.00 218.77 1.75 218.75 2.00 218.74 3.10 218.72

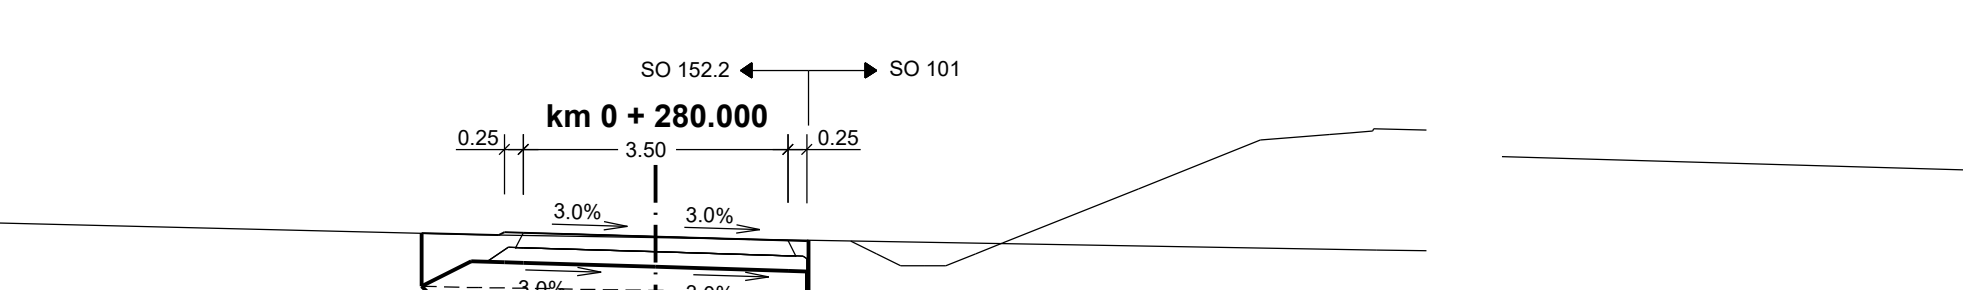


PROJEKTOVANÝ STAV	
ODSAZENÍ OD OSY	-3.09 218.85 -2.08 218.83 -2.00 218.86 -1.75 218.86 0.00 218.80 1.75 218.75 2.00 218.75 2.02 218.76 0.00 218.79 1.75 218.75 2.00 218.75 2.02 218.76
STÁVAJÍCÍ TERÉN	
ODSAZENÍ OD OSY	-2.34 218.83 0.00 218.79 1.75 218.75 2.00 218.75 2.02 218.76

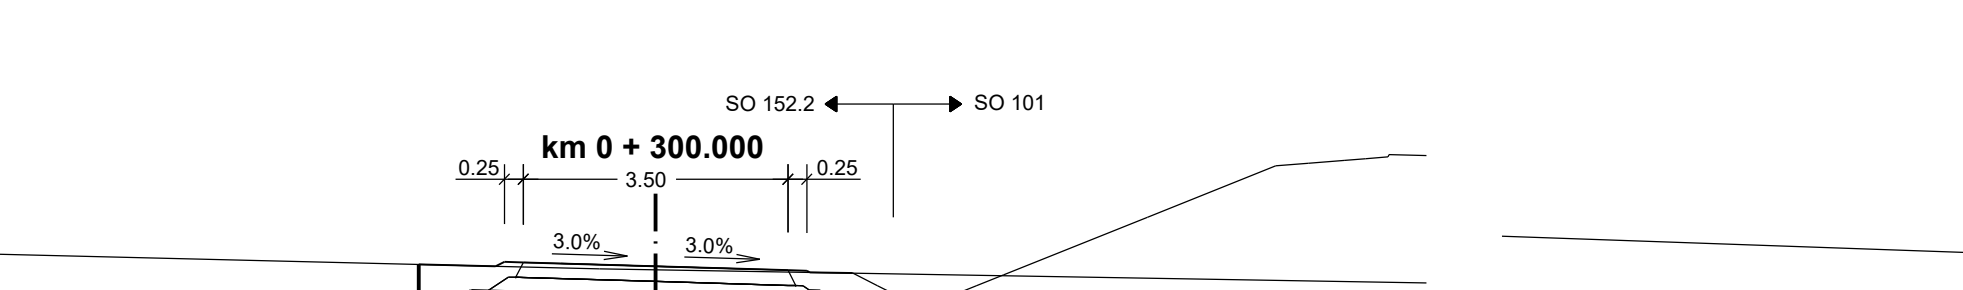


PROJEKTOVANÝ STAV	
ODSAZENÍ OD OSY	-3.13 218.96 -2.12 218.93 -2.00 220.12 -1.75 218.96 0.00 218.93 1.75 218.88 2.00 220.12 2.16 218.79 0.00 218.89 1.75 218.87 2.16 218.79 3.26 218.77
STÁVAJÍCÍ TERÉN	
ODSAZENÍ OD OSY	0.00 218.89 1.75 218.87 2.16 218.79 3.26 218.77

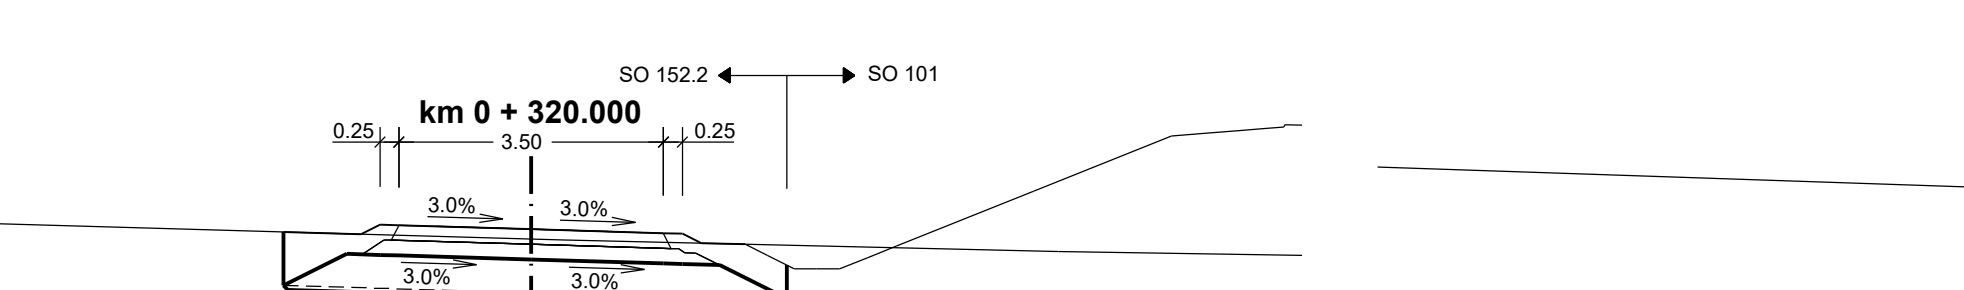


PROJEKTOVANÝ STAV	
ODSAZENÍ OD OSY	-3.28 219.15 -2.05 219.12 -2.00 219.24 -1.75 219.24 0.00 219.18 1.75 219.13 2.00 219.12 2.08 219.13 3.38 219.07 0.00 219.05 0.46 219.04 3.38 219.07
STÁVAJÍCÍ TERÉN	
ODSAZENÍ OD OSY	0.00 219.05 0.46 219.04 3.38 219.07

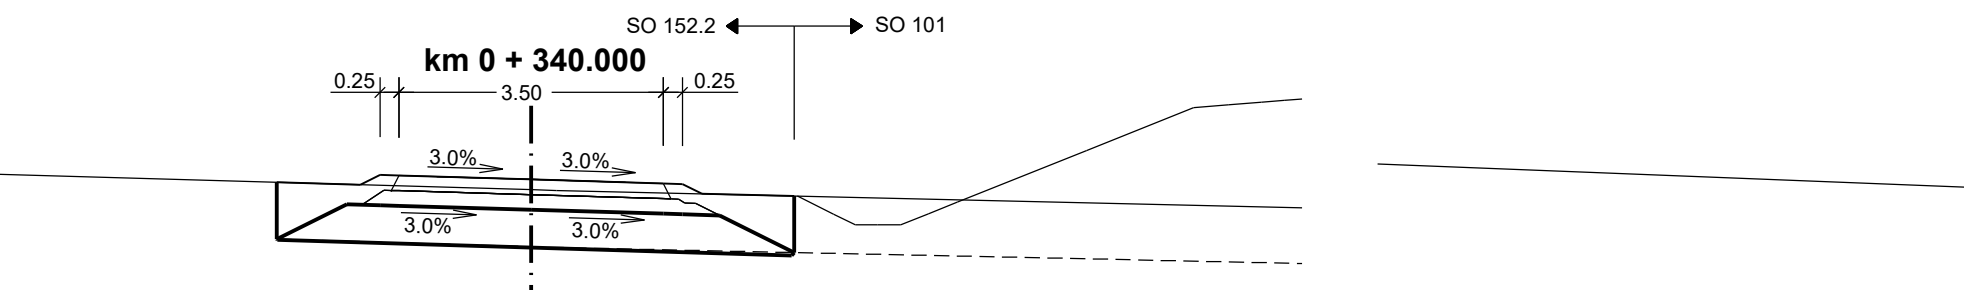


PROJEKTOVANÝ STAV	
ODSAZENÍ OD OSY	-3.37 219.52 -2.05 219.49 -2.00 219.62 -1.75 219.61 0.00 219.56 1.75 219.51 2.00 219.50 2.08 219.51 3.48 219.34 0.00 219.43 0.34 219.42 3.48 219.34
STÁVAJÍCÍ TERÉN	
ODSAZENÍ OD OSY	0.00 219.43 0.34 219.42 3.48 219.34

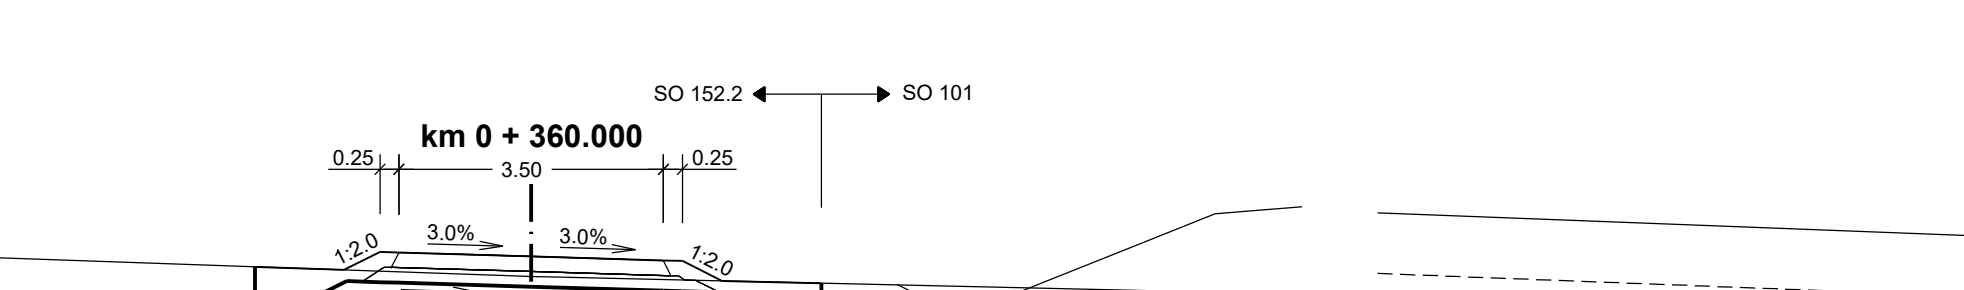

PROJEKTOVANÝ STAV	
ODSAZENÍ OD OSY	-3.65 219.92 -2.48 219.88 -2.00 220.12 -1.75 220.11 0.00 220.06 1.75 220.01 2.00 220.00 2.53 219.74 3.84 219.71 0.00 220.05 0.22 219.79 2.23 219.75 2.53 219.74 3.84 219.71
STÁVAJÍCÍ TERÉN	
ODSAZENÍ OD OSY	-0.33 219.81 0.00 219.80 0.22 219.79 2.23 219.75 2.53 219.74 3.84 219.71

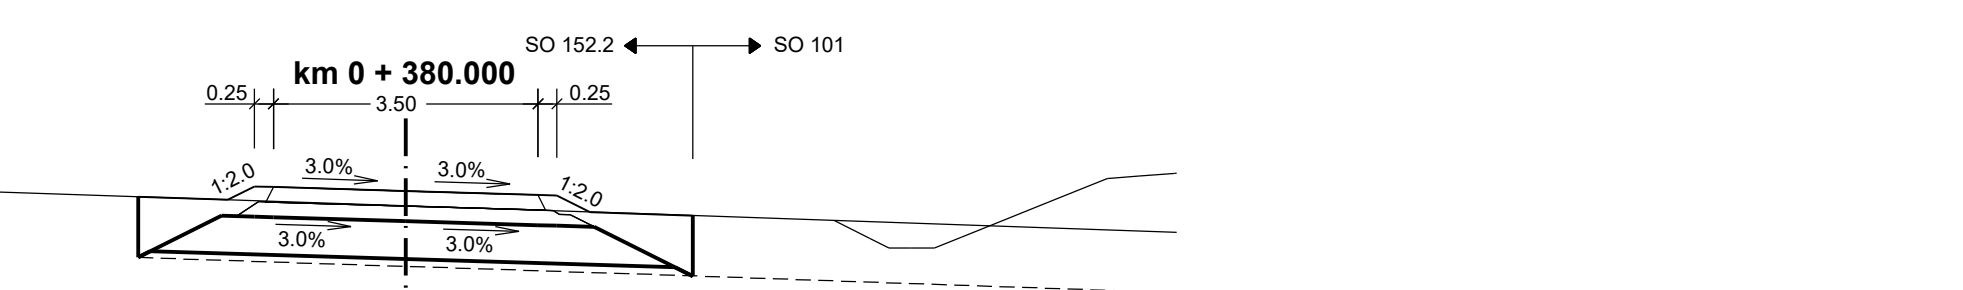

PROJEKTOVANÝ STAV	
ODSAZENÍ OD OSY	-3.54 220.91 -2.05 220.75 -2.00 220.75 -1.75 220.74 0.00 220.89 1.75 220.84 2.00 220.83 2.44 220.81 3.80 220.86 0.00 220.89 2.44 220.81 3.80 220.86
STÁVAJÍCÍ TERÉN	
ODSAZENÍ OD OSY	0.00 220.89 2.44 220.81 3.80 220.86

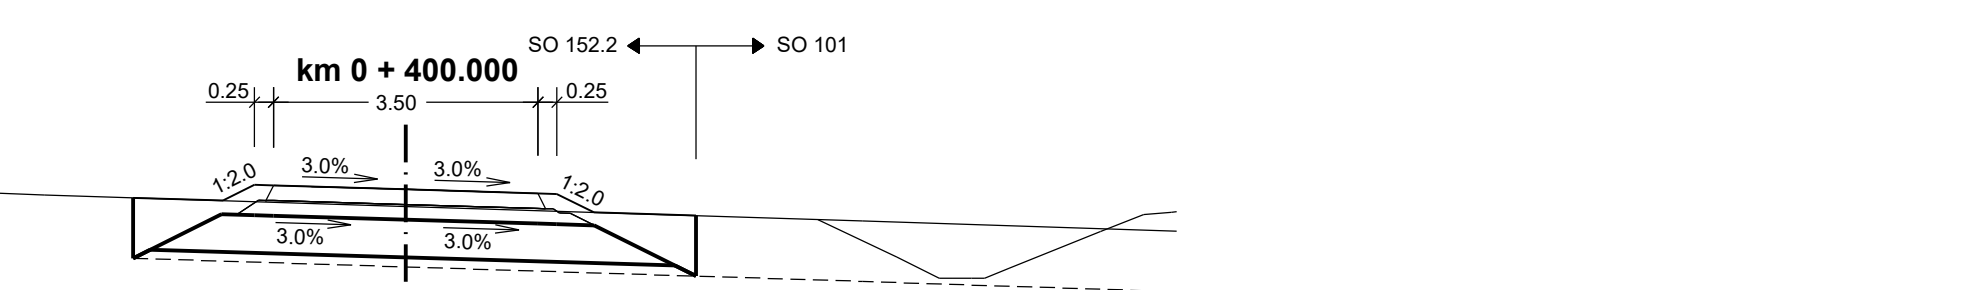

PROJEKTOVANÝ STAV	
ODSAZENÍ OD OSY	-3.61 221.32 -2.03 221.26 -2.00 221.48 -1.75 221.48 0.00 221.43 1.75 221.38 2.00 221.37 2.49 221.12 3.84 221.08 0.00 221.20 2.49 221.12 3.84 221.08
STÁVAJÍCÍ TERÉN	
ODSAZENÍ OD OSY	-4.77 221.36 0.00 221.20 1.75 221.38 2.00 221.37 2.49 221.12 3.84 221.08



PROJEKTOVANÝ STAV	
ODSAZENÍ OD OSY	-3.39 222.18 -2.03 222.15 -2.00 222.25 -1.75 222.24 0.00 222.19 1.75 222.14 2.00 222.13 2.53 221.96 3.70 221.91 0.00 222.05 1.75 222.14 2.00 222.13 2.53 221.96 3.70 221.91
STÁVAJÍCÍ TERÉN	
ODSAZENÍ OD OSY	0.00 222.05 1.75 222.14 2.00 222.13 2.53 221.96 3.70 221.91

Výškový systém: Bpv

SO 152

Přístupy na pozemky k.ú. Židněves

Objednatel:

ŘEDITELSTVÍ
SILNIC
A DÁLNIC
Ředitelství silnic a dálnic s. p.
Čerčanská 2023/12, Krč, 140 00 Praha 4

Zhotovitel:

Valbek, spol. s r.o.
Vaňurova 505/17
460 07 Liberec 3

Vypracoval:

P. BARTUSEK
ING. T. KLIMENT

Stupeň:

Ing. M. HANŽL

Č. přílohy

Paré

5.2.1

1:100

1:100

1:100

1:100

1:100