SO 152 - PŘÍSTUPY NA POZEMKY k.ú. ŽIDNĚVES
PŘÍČNÉ ŘEZY SO 152.2 - km 0,440 - 0,840, M 1 : 100

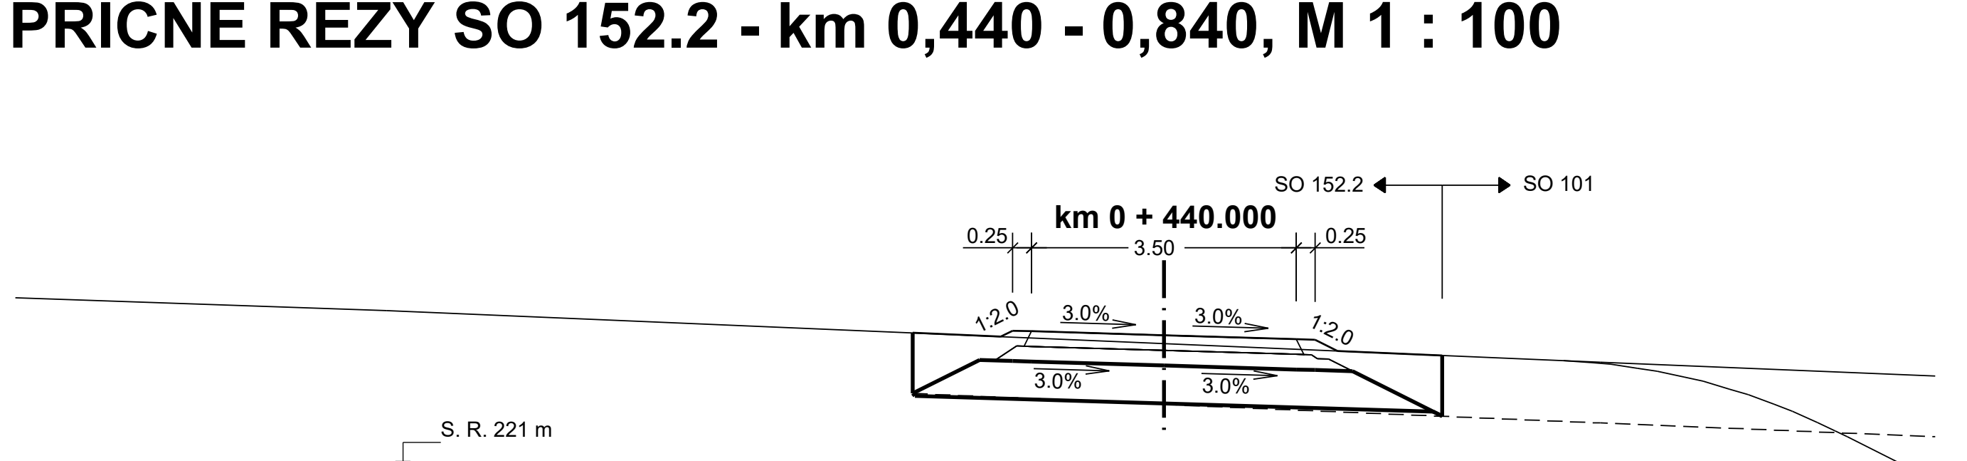
SO 152.2
SO 101
km 0 + 440.000
0.25
3.50
0.25
1:2.0
3.0%
3.0%
1:2.0
3.0%
3.0%
S. R. 221 m

PROJEKTOVANÝ STAV	222.95	222.90	222.98	222.97	222.92	222.86	222.86	222.71	222.65
ODSAZENÍ OD OSY	-3.32	-2.16	-2.00	-1.75	0.00	1.75	2.00	2.30	3.68

STÁVAJÍCÍ TERÉN	222.81	222.56
ODSAZENÍ OD OSY	0.00	5.77

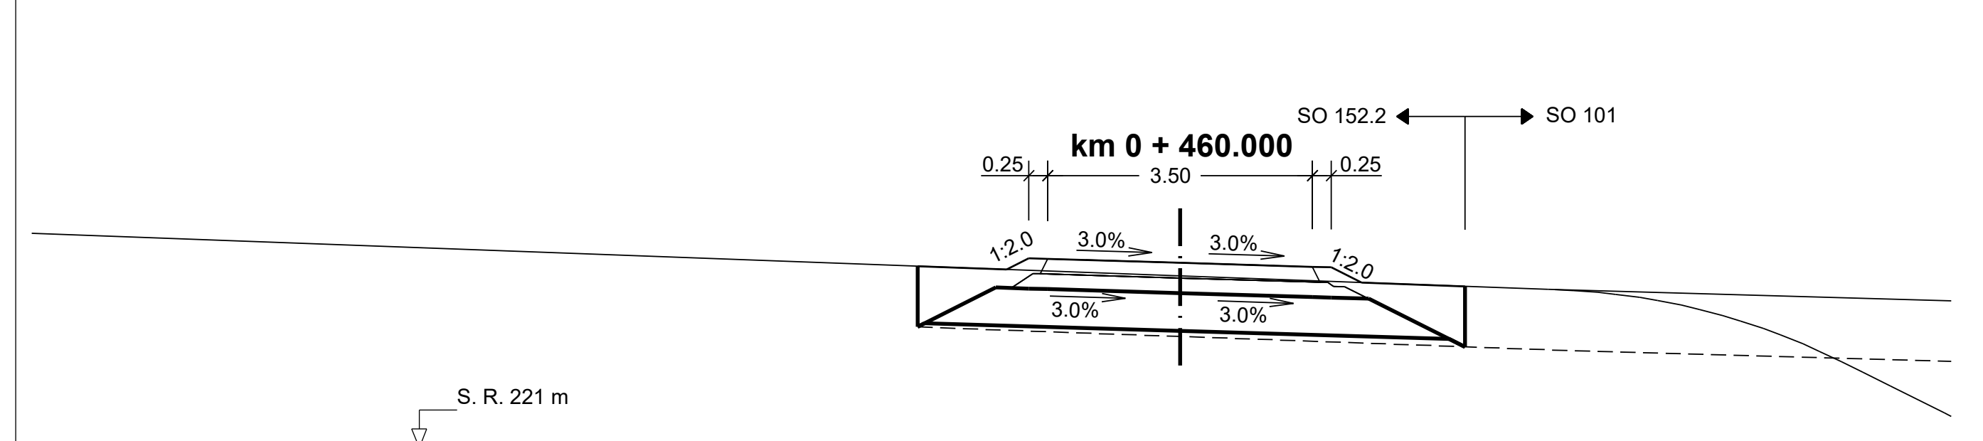
SO 152.2
SO 101
km 0 + 460.000
0.25
3.50
0.25
1:2.0
3.0%
3.0%
1:2.0
3.0%
3.0%
S. R. 221 m

PROJEKTOVANÝ STAV	223.40	223.36	223.50	223.50	223.44	223.39	223.38	223.18	223.13
ODSAZENÍ OD OSY	-3.47	-2.29	-2.00	-1.75	0.00	1.75	2.00	2.40	3.77

STÁVAJÍCÍ TERÉN	223.27	223.09
ODSAZENÍ OD OSY	0.00	4.86

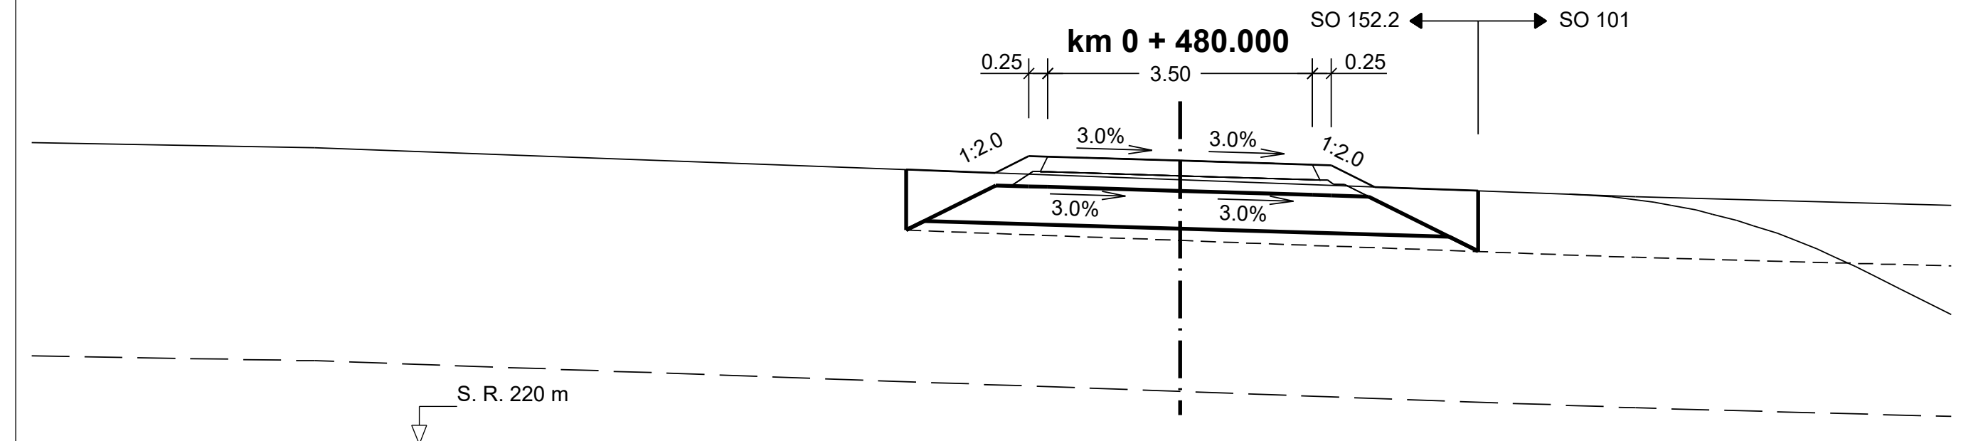
SO 152.2
SO 101
km 0 + 480.000
0.25
3.50
0.25
1:2.0
3.0%
3.0%
1:2.0
3.0%
3.0%
S. R. 220 m

PROJEKTOVANÝ STAV	223.63	223.59	223.81	223.80	223.75	223.70	223.69	223.40	223.35
ODSAZENÍ OD OSY	-3.62	-2.44	-2.00	-1.75	0.00	1.75	2.00	2.58	3.94

STÁVAJÍCÍ TERÉN	223.50	223.28
ODSAZENÍ OD OSY	0.00	6.03

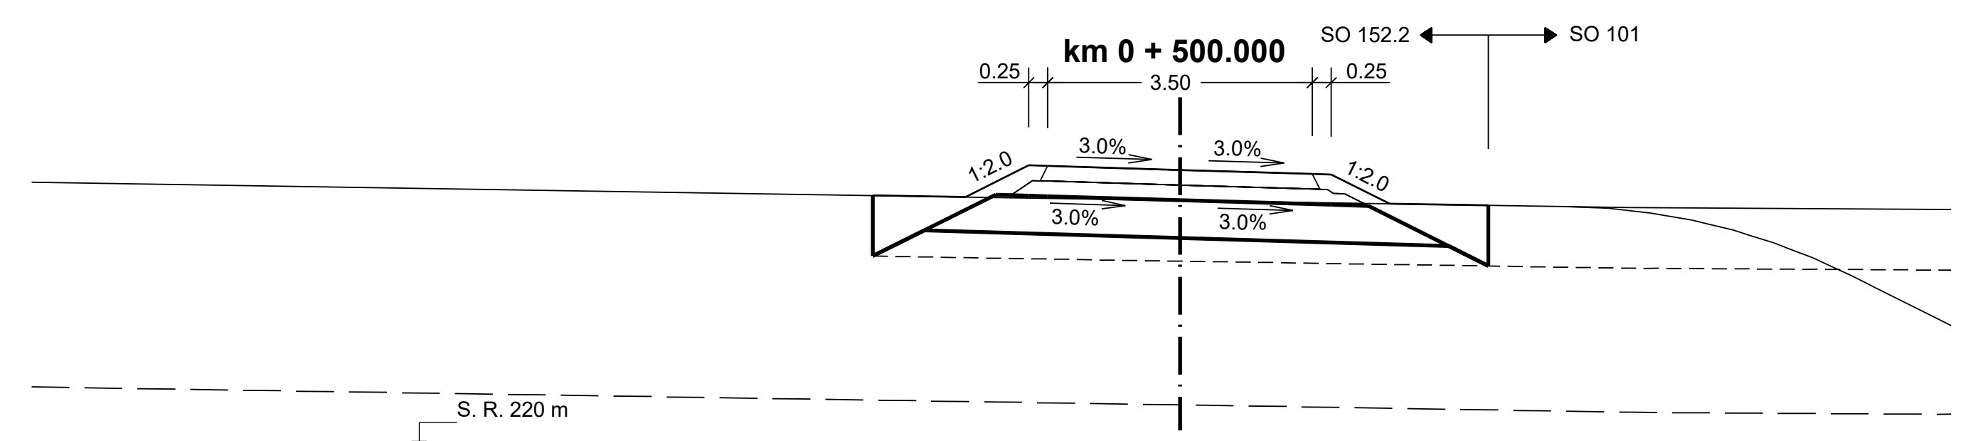
km 0 + 500.000
SO 152.2
SO 101
0.25
3.50
0.25
1:2.0
3.0%
3.0%
1:2.0
3.0%
3.0%
S. R. 220 m

PROJEKTOVANÝ STAV	223.50	223.48	223.89	223.89	223.83	223.78	223.77	223.39	223.37
ODSAZENÍ OD OSY	-4.06	-2.84	-2.00	-1.75	0.00	1.75	2.00	2.77	4.08

STÁVAJÍCÍ TERÉN	223.43	223.34
ODSAZENÍ OD OSY	0.00	5.95

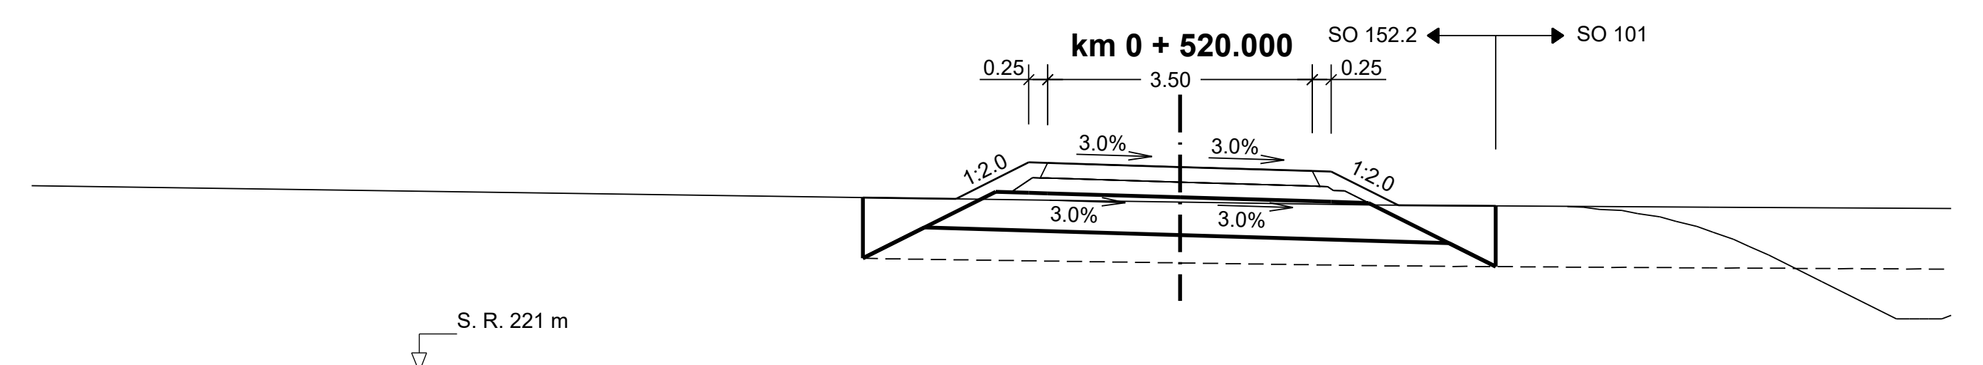
km 0 + 520.000
SO 152.2
SO 101
0.25
3.50
0.25
1:2.0
3.0%
3.0%
1:2.0
3.0%
3.0%
S. R. 221 m

PROJEKTOVANÝ STAV	223.30	223.28	223.76	223.75	223.70	223.65	223.64	223.20	223.19
ODSAZENÍ OD OSY	-4.19	-2.96	-2.00	-1.75	0.00	1.75	2.00	2.89	4.17

STÁVAJÍCÍ TERÉN	223.24	223.20	223.19	223.17
ODSAZENÍ OD OSY	0.00	2.51	3.58	7.01

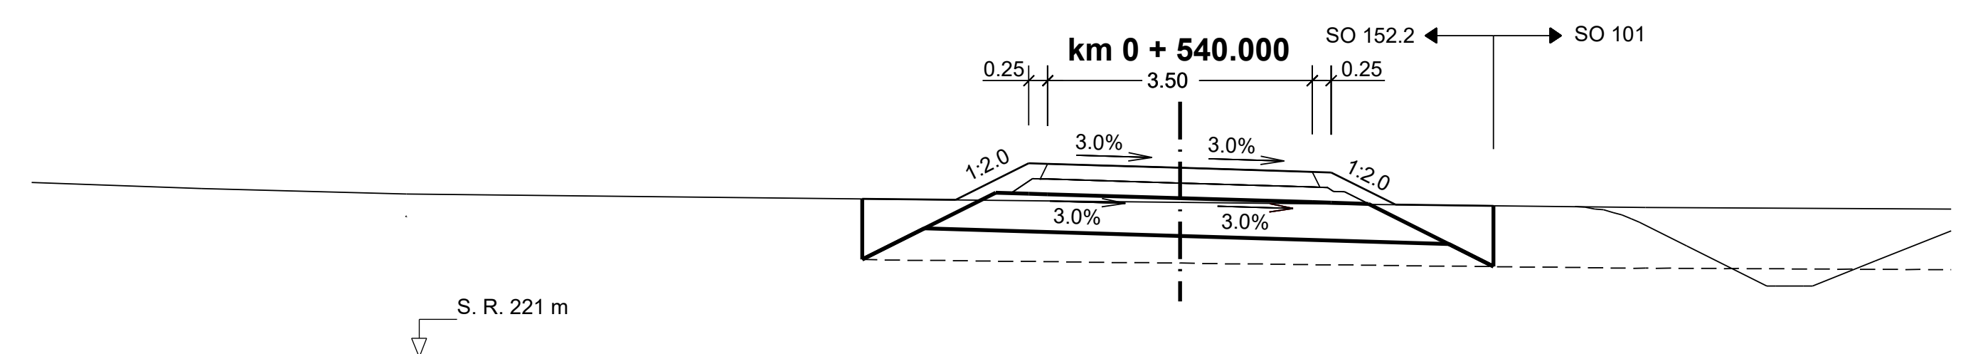
km 0 + 540.000
SO 152.2
SO 101
0.25
3.50
0.25
1:2.0
3.0%
3.0%
1:2.0
3.0%
3.0%
S. R. 221 m

PROJEKTOVANÝ STAV	223.09	223.08	223.56	223.55	223.50	223.45	223.44	223.02	223.00
ODSAZENÍ OD OSY	-4.20	-2.97	-2.00	-1.75	0.00	1.75	2.00	2.85	4.14

STÁVAJÍCÍ TERÉN	223.05	222.98
ODSAZENÍ OD OSY	0.00	6.16

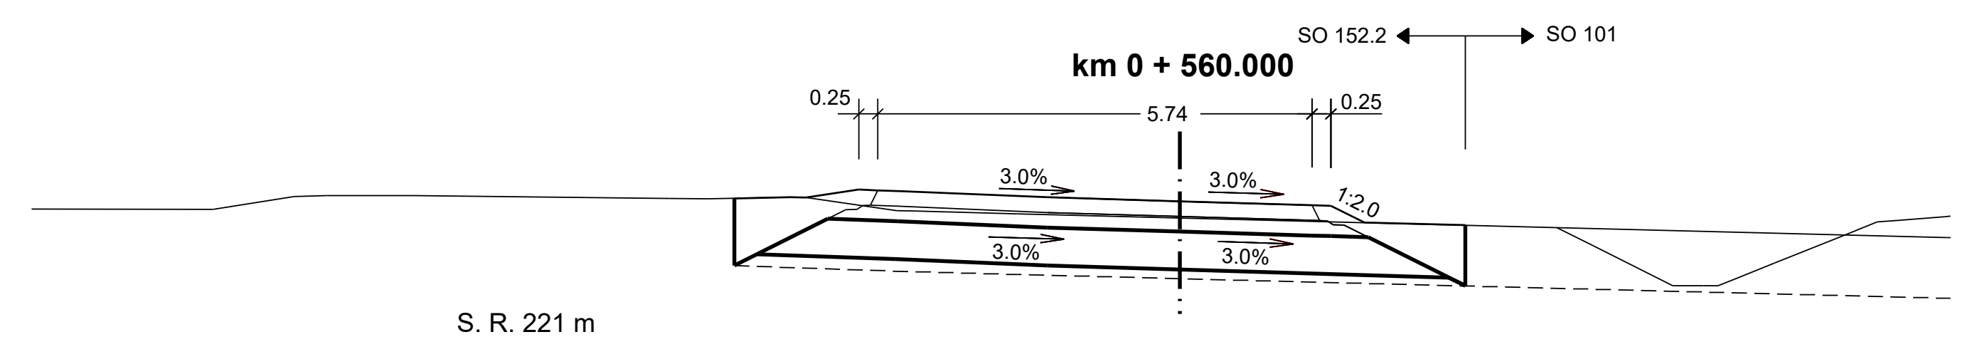
SO 152.2
SO 101
km 0 + 560.000
0.25
5.74
0.25
3.0%
3.0%
1:2.0
3.0%
3.0%
S. R. 221 m

PROJEKTOVANÝ STAV	223.34	223.35	223.47	223.45	223.44	223.35	223.30	223.25	223.24	223.02	222.99
ODSAZENÍ OD OSY	-5.89	-4.94	-4.05	-3.99	-3.71	-1.75	0.00	1.75	2.00	2.45	3.78

STÁVAJÍCÍ TERÉN	223.34	223.33	223.35	223.35	223.18	223.17	223.14	223.08
ODSAZENÍ OD OSY	-6.75	-6.24	-5.15	-4.94	-3.74	-3.52	-2.15	0.00

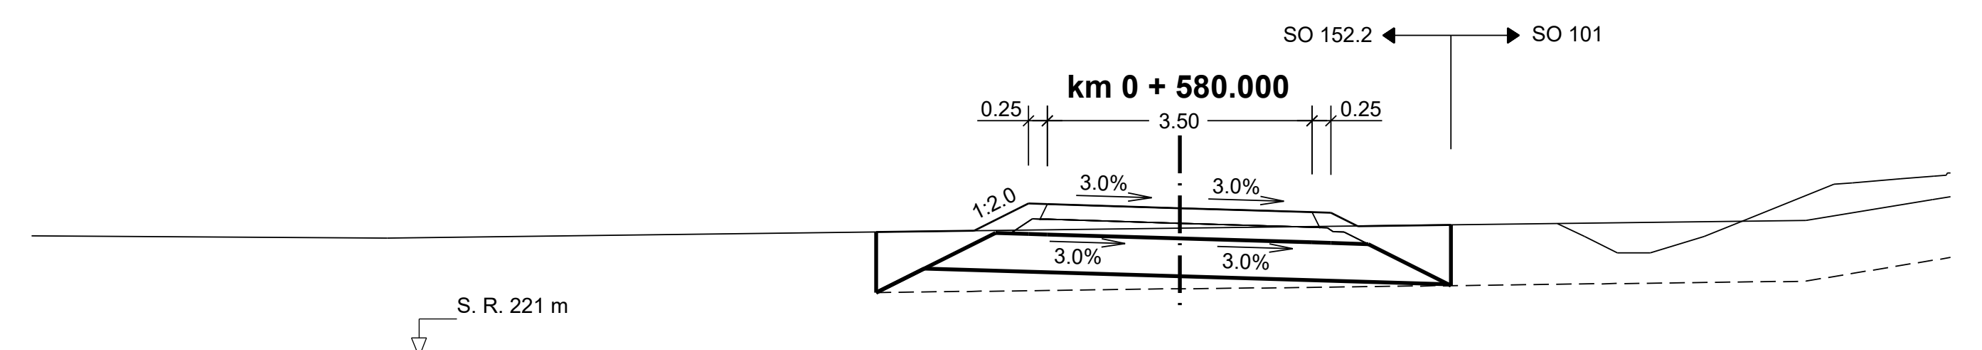
SO 152.2
SO 101
km 0 + 580.000
0.25
3.50
0.25
1:2.0
3.0%
3.0%
3.0%
3.0%
S. R. 221 m

PROJEKTOVANÝ STAV	222.65	222.66	223.02	223.01	222.96	222.91	222.90	222.72	222.74
ODSAZENÍ OD OSY	-4.02	-2.72	-2.00	-1.75	0.00	1.75	2.00	2.35	3.59

STÁVAJÍCÍ TERÉN	222.70	222.80	223.07
ODSAZENÍ OD OSY	0.00	8.28	9.96

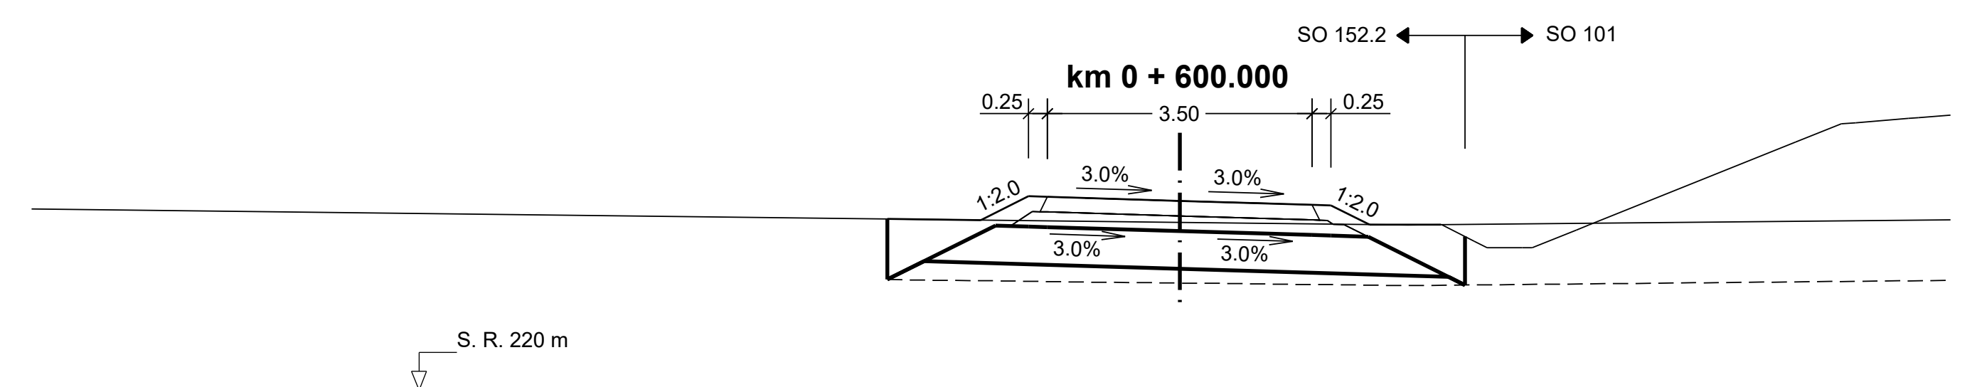
SO 152.2
SO 101
km 0 + 600.000
0.25
3.50
0.25
1:2.0
3.0%
3.0%
1:2.0
3.0%
3.0%
S. R. 220 m

PROJEKTOVANÝ STAV	222.26	222.25	222.57	222.56	222.51	222.45	222.45	222.19	222.19
ODSAZENÍ OD OSY	-3.87	-2.63	-2.00	-1.75	0.00	1.75	2.00	2.51	3.77

STÁVAJÍCÍ TERÉN	222.22	222.18
ODSAZENÍ OD OSY	0.00	3.02

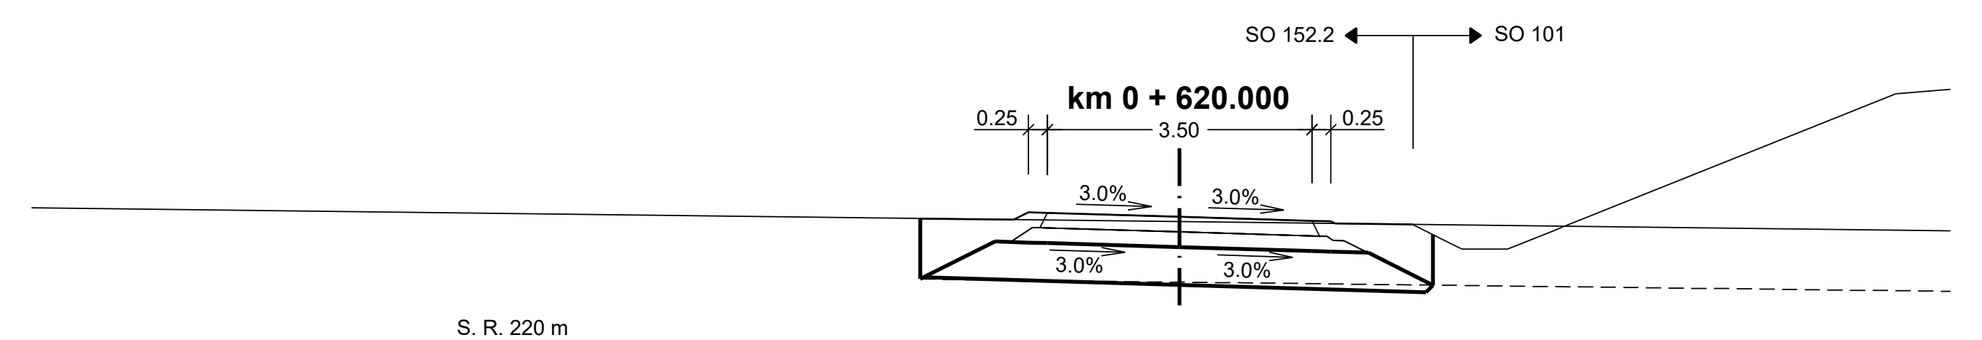
SO 152.2
SO 101
km 0 + 620.000
0.25
3.50
0.25
3.0%
3.0%
3.0%
3.0%
S. R. 220 m

PROJEKTOVANÝ STAV	222.12	222.10	222.20	222.19	222.14	222.09	222.08	222.05	222.03
ODSAZENÍ OD OSY	-3.43	-2.19	-2.00	-1.75	0.00	1.75	2.00	2.06	3.35

STÁVAJÍCÍ TERÉN	222.08
ODSAZENÍ OD OSY	0.00

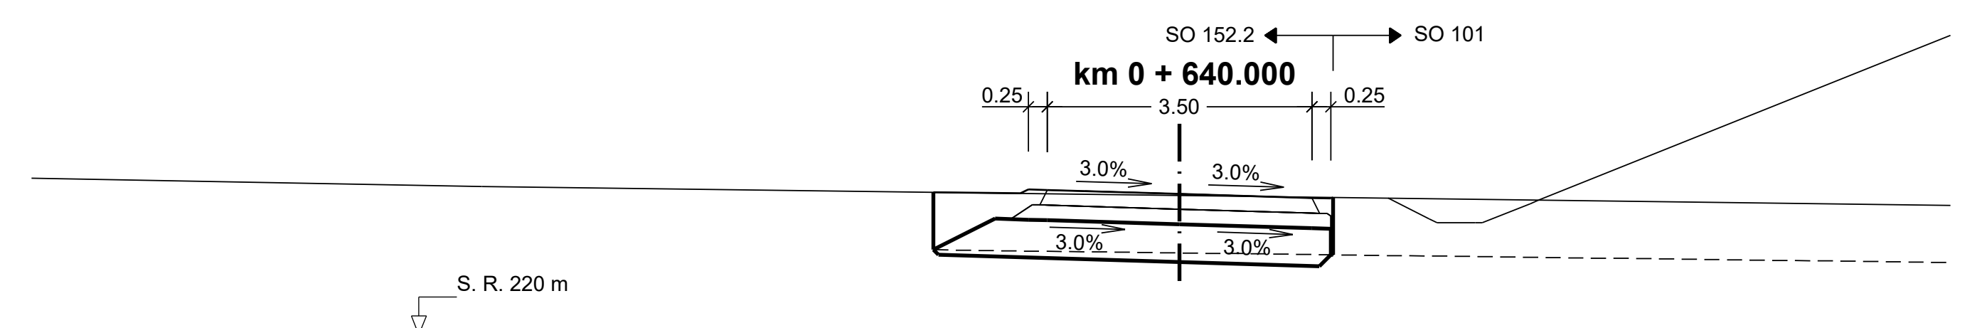
SO 152.2
SO 101
km 0 + 640.000
0.25
3.50
0.25
3.0%
3.0%
3.0%
3.0%
S. R. 220 m

PROJEKTOVANÝ STAV	221.88	221.87	221.92	221.91	221.86	221.81	221.80	221.81
ODSAZENÍ OD OSY	-3.26	-2.11	-2.00	-1.75	0.00	1.75	2.00	2.03

STÁVAJÍCÍ TERÉN	221.96	221.84
ODSAZENÍ OD OSY	-9.23	0.00

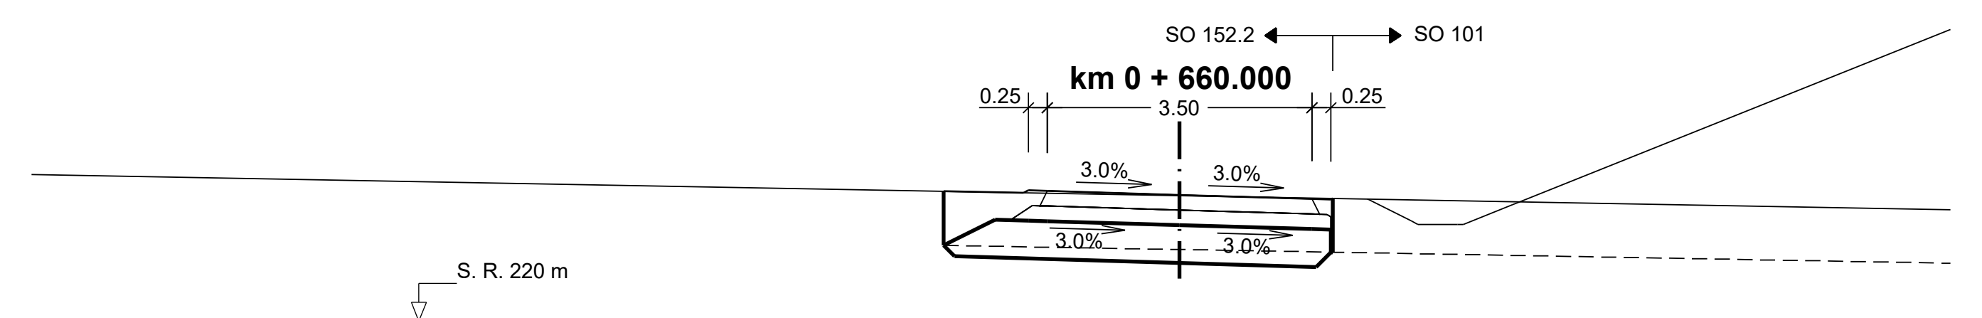
SO 152.2
SO 101
km 0 + 660.000
0.25
3.50
0.25
3.0%
3.0%
3.0%
3.0%
S. R. 220 m

PROJEKTOVANÝ STAV	221.72	221.70	221.73	221.72	221.67	221.62	221.61	221.63
ODSAZENÍ OD OSY	-3.12	-2.06	-2.00	-1.75	0.00	1.75	2.00	2.03

STÁVAJÍCÍ TERÉN	221.66
ODSAZENÍ OD OSY	0.00

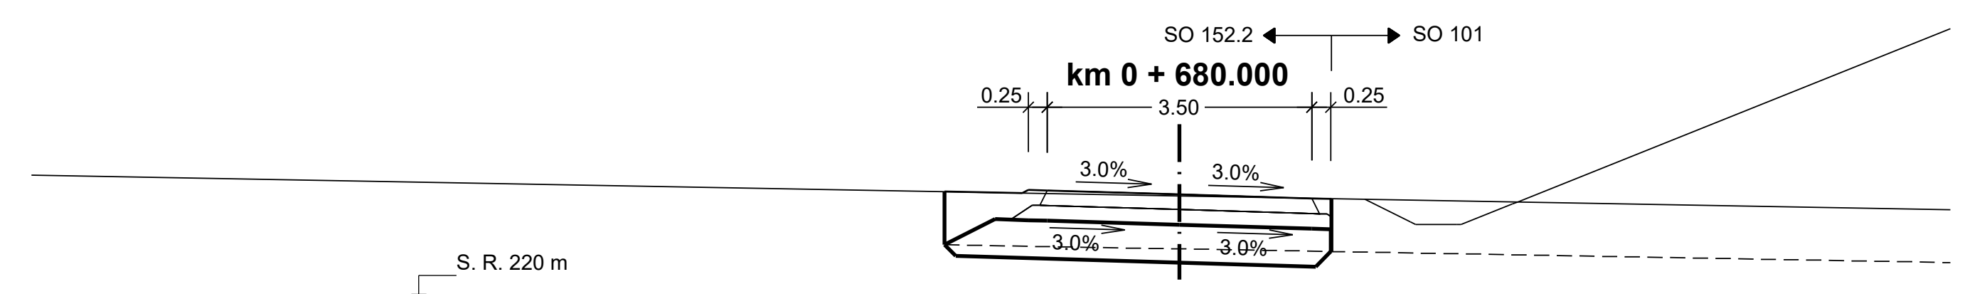
SO 152.2
SO 101
km 0 + 680.000
0.25
3.50
0.25
3.0%
3.0%
3.0%
3.0%
S. R. 220 m

PROJEKTOVANÝ STAV	221.61	221.59	221.63	221.62	221.57	221.52	221.51	221.52
ODSAZENÍ OD OSY	-3.11	-2.08	-2.00	-1.75	0.00	1.75	2.00	2.01

STÁVAJÍCÍ TERÉN	221.55
ODSAZENÍ OD OSY	0.00

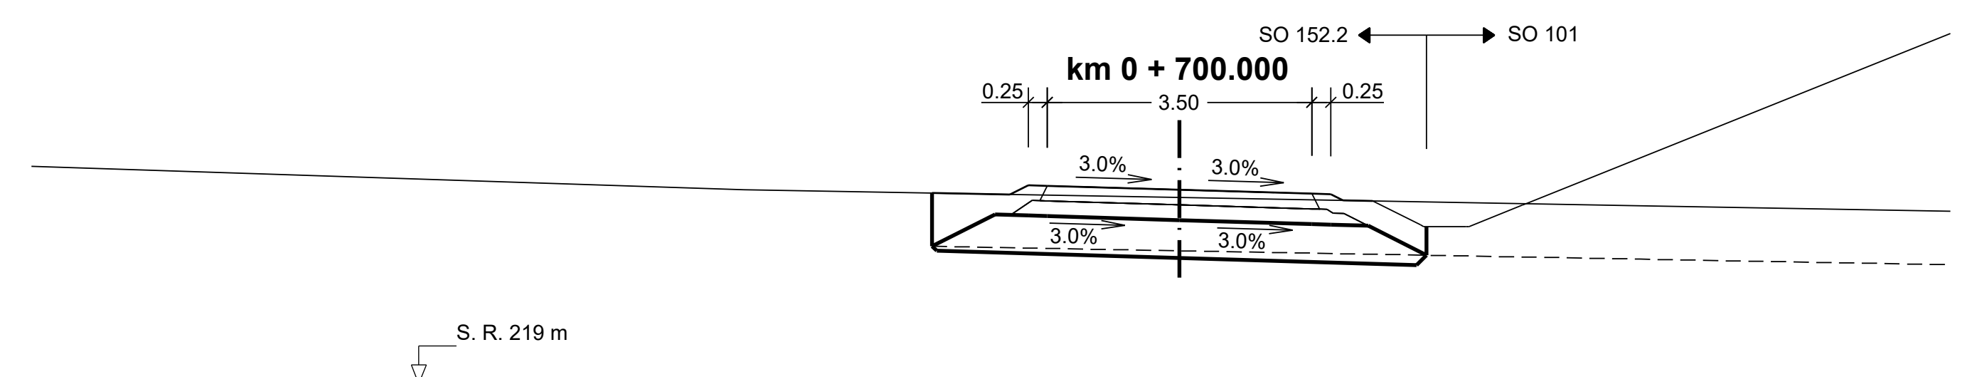
SO 152.2
SO 101
km 0 + 700.000
0.25
3.50
0.25
3.0%
3.0%
3.0%
3.0%
S. R. 219 m

PROJEKTOVANÝ STAV	221.52	221.50	221.62	221.61	221.56	221.51	221.50	221.42	221.40
ODSAZENÍ OD OSY	-3.27	-2.24	-2.00	-1.75	0.00	1.75	2.00	2.16	3.27

STÁVAJÍCÍ TERÉN	221.56	221.46	221.35
ODSAZENÍ OD OSY	-5.76	0.00	6.09

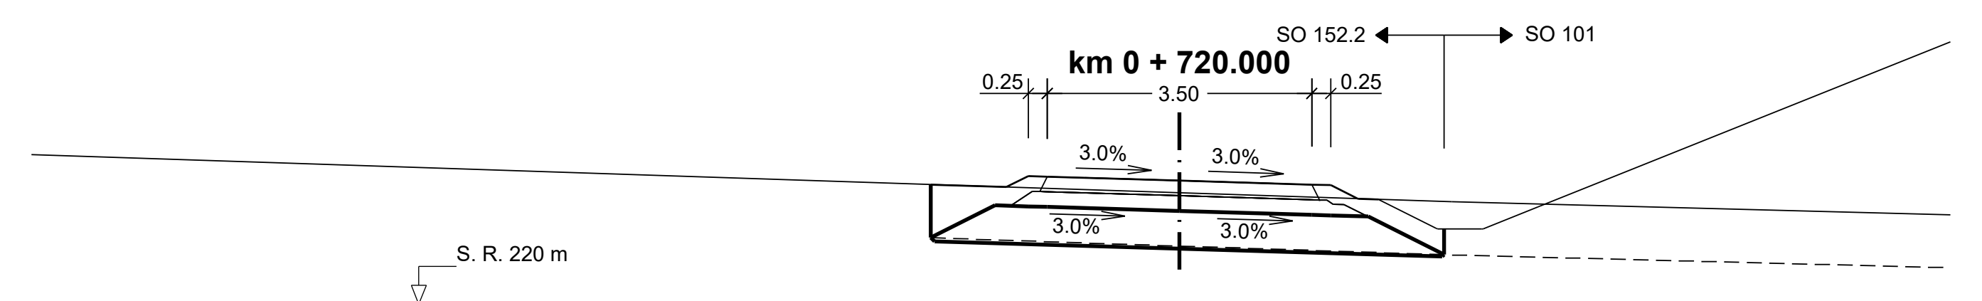
SO 152.2
SO 101
km 0 + 720.000
0.25
3.50
0.25
3.0%
3.0%
3.0%
3.0%
S. R. 220 m

PROJEKTOVANÝ STAV	221.58	221.55	221.69	221.69	221.63	221.58	221.57	221.40	221.36
ODSAZENÍ OD OSY	-3.29	-2.29	-2.00	-1.75	0.00	1.75	2.00	2.36	3.50

STÁVAJÍCÍ TERÉN	221.47	221.35
ODSAZENÍ OD OSY	0.00	3.60

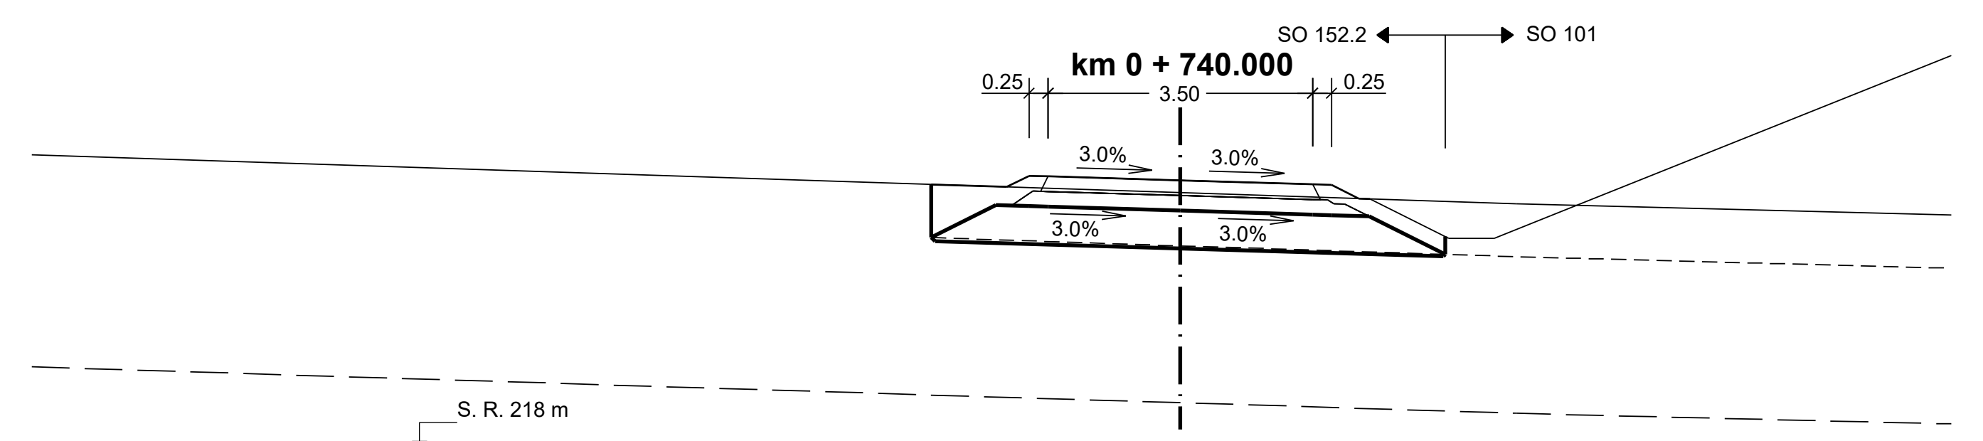
SO 152.2
SO 101
km 0 + 740.000
0.25
3.50
0.25
3.0%
3.0%
3.0%
3.0%
S. R. 218 m

PROJEKTOVANÝ STAV	221.65	221.61	221.76	221.75	221.70	221.65	221.64	221.46	221.42
ODSAZENÍ OD OSY	-3.29	-2.29	-2.00	-1.75	0.00	1.75	2.00	2.36	3.50

STÁVAJÍCÍ TERÉN	221.54	221.39
ODSAZENÍ OD OSY	0.00	4.44

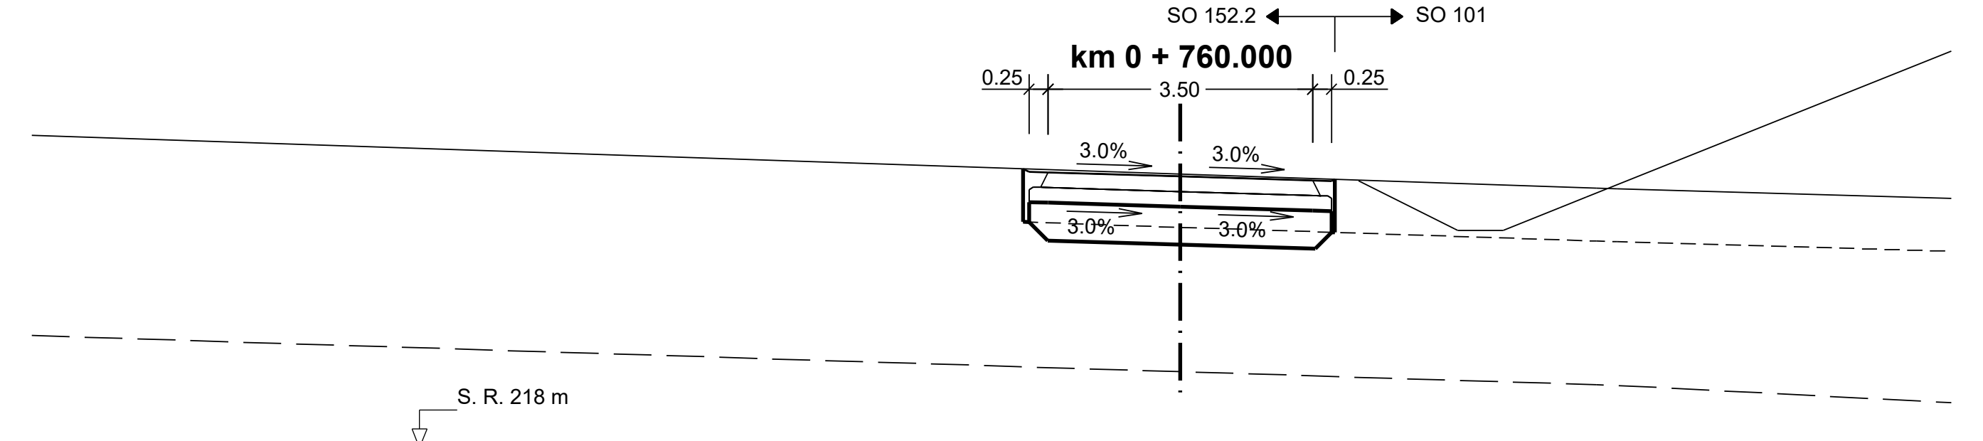
SO 152.2
SO 101
km 0 + 760.000
0.25
3.50
0.25
3.0%
3.0%
3.0%
3.0%
S. R. 218 m

PROJEKTOVANÝ STAV	221.69	221.65	221.64	221.59	221.53	221.53	221.55
ODSAZENÍ OD OSY	-2.08	-2.00	-1.75	0.00	1.75	2.00	2.04

STÁVAJÍCÍ TERÉN	221.62	221.43	221.42
ODSAZENÍ OD OSY	0.00	5.51	5.77

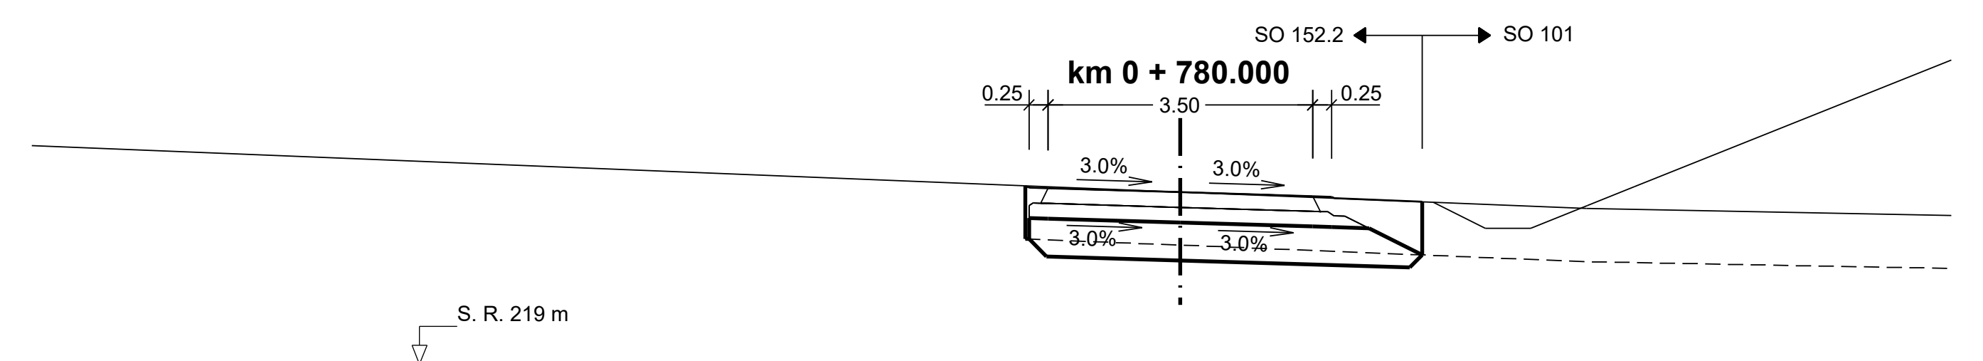
SO 152.2
SO 101
km 0 + 780.000
0.25
3.50
0.25
3.0%
3.0%
3.0%
3.0%
S. R. 219 m

PROJEKTOVANÝ STAV	221.36	221.33	221.33	221.27	221.22	221.21	221.19	221.15
ODSAZENÍ OD OSY	-2.05	-2.00	-1.75	0.00	1.75	2.00	2.04	3.20

STÁVAJÍCÍ TERÉN	221.27	221.06
ODSAZENÍ OD OSY	0.00	5.37

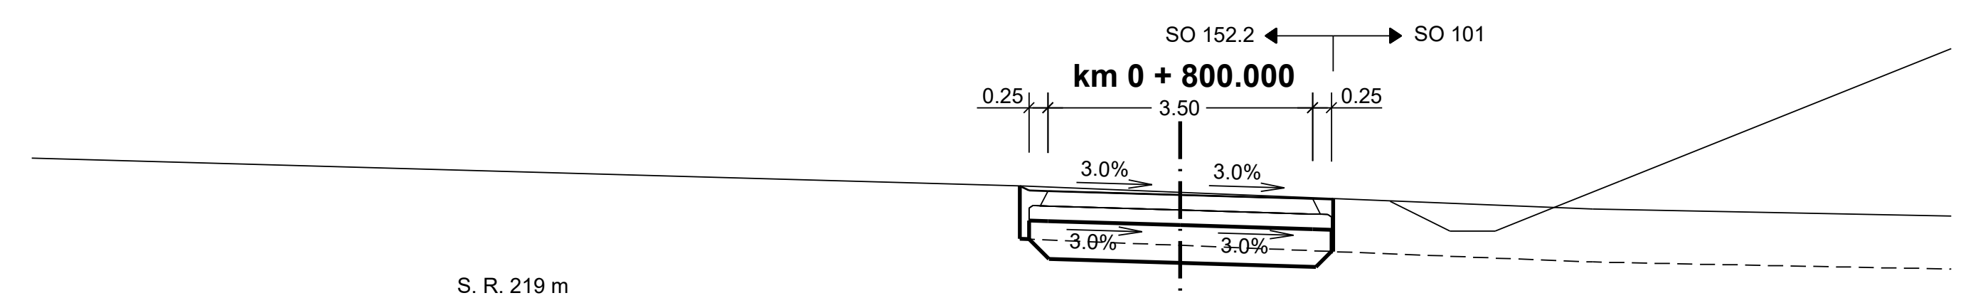
SO 152.2
SO 101
km 0 + 800.000
0.25
3.50
0.25
3.0%
3.0%
3.0%
3.0%
S. R. 219 m

PROJEKTOVANÝ STAV	220.99	220.93	220.93	220.87	220.82	220.81	220.83
ODSAZENÍ OD OSY	-2.12	-2.00	-1.75	0.00	1.75	2.00	2.02

STÁVAJÍCÍ TERÉN	220.99	220.91	220.69
ODSAZENÍ OD OSY	-2.08	0.00	5.46

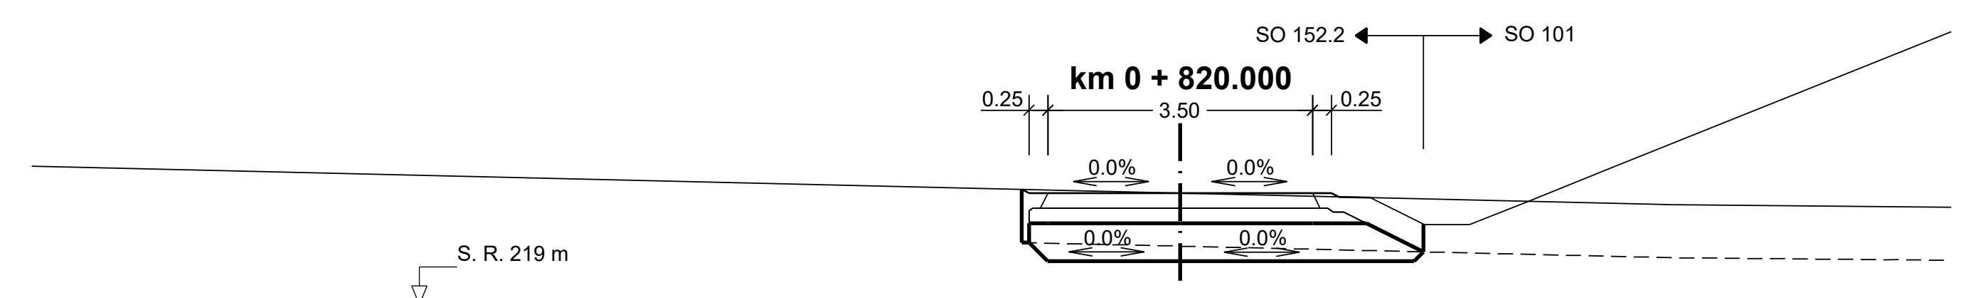
SO 152.2
SO 101
km 0 + 820.000
0.25
3.50
0.25
0.0%
0.0%
0.0%
0.0%
S. R. 219 m

PROJEKTOVANÝ STAV	220.52	220.47	220.47	220.47	220.47	220.47	220.42	220.40
ODSAZENÍ OD OSY	-2.10	-2.00	-1.75	0.00	1.75	2.00	2.10	3.22

STÁVAJÍCÍ TERÉN	220.47	220.32
ODSAZENÍ OD OSY	0.00	6.52

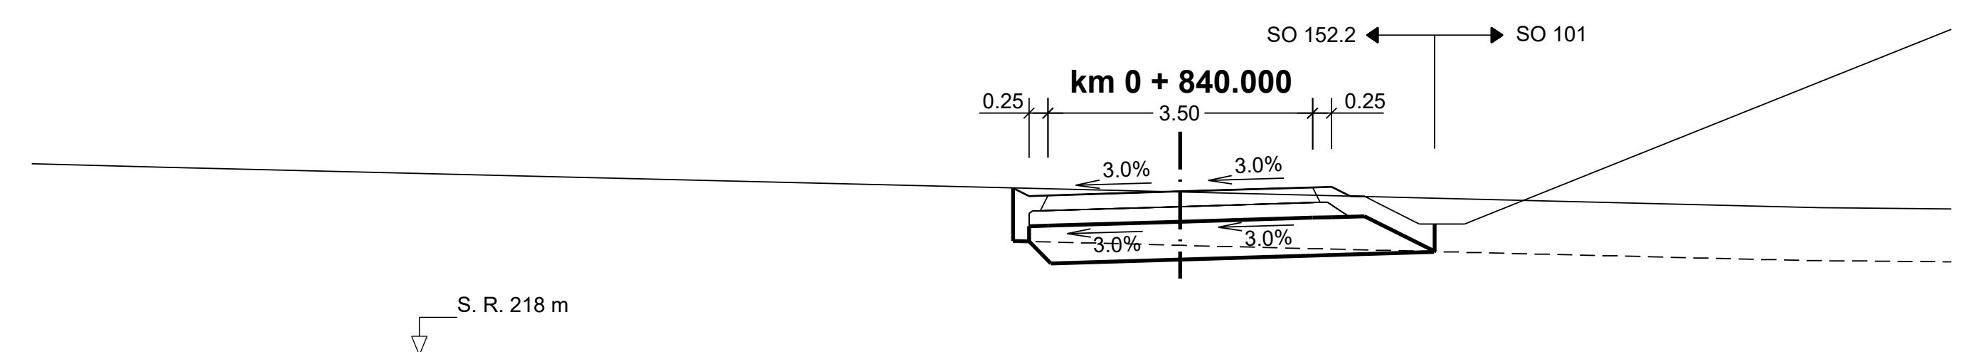
SO 152.2
SO 101
km 0 + 840.000
0.25
3.50
0.25
3.0%
3.0%
3.0%
3.0%
S. R. 218 m

PROJEKTOVANÝ STAV	220.21	220.10	220.11	220.16	220.22	220.22	220.10	220.07
ODSAZENÍ OD OSY	-2.21	-2.00	-1.75	0.00	1.75	2.00	2.25	3.37

STÁVAJÍCÍ TERÉN	220.15	219.95
ODSAZENÍ OD OSY	0.00	8.44

Výškový systém: Bpv

SO 152 Přístupy na pozemky k.ú. Židněves

Objednatel:
ŘEDITELSTVÍ SILNIC A DÁLNIC
Ředitelství silnic a dálnic s. p.
Čerčanská 2023/12, Krč, 140 00 Praha 4

Zhotovitel:
Valbek
Valbek, spol. s r.o.
Vaňurova 505/17
460 07 Liberec 3

Vypracoval	P. BARTUSEK	Zak. číslo	21-LI13-001
Zodp. projektant	ING. T. KLIMENT	Datum	02/2025
Tech. kontrola	ING. M. HANŽL	Stupeň	PDPS
Akce	I/16 MLADÁ BOLESLAV - MARTINOVICE	Počet formátů	20 x A4
		Měřítko	1 : 100
		Č. přílohy	Paré
Příloha	PŘÍČNÉ ŘEZY SO 152.2 - km 0,440 - 0,840	5.2.2	

Valbek

Zhotovitel:
Valbek, spol. s r.o.
Vaňurova 505/17
460 07 Liberec 3