




SO 152 - PŘÍSTUPY NA POZEMKY K.Ú. ŽIDNĚVES
PŘÍČNÉ ŘEZY SO 152.2 - km 0,860 - 1,260, M 1 : 100

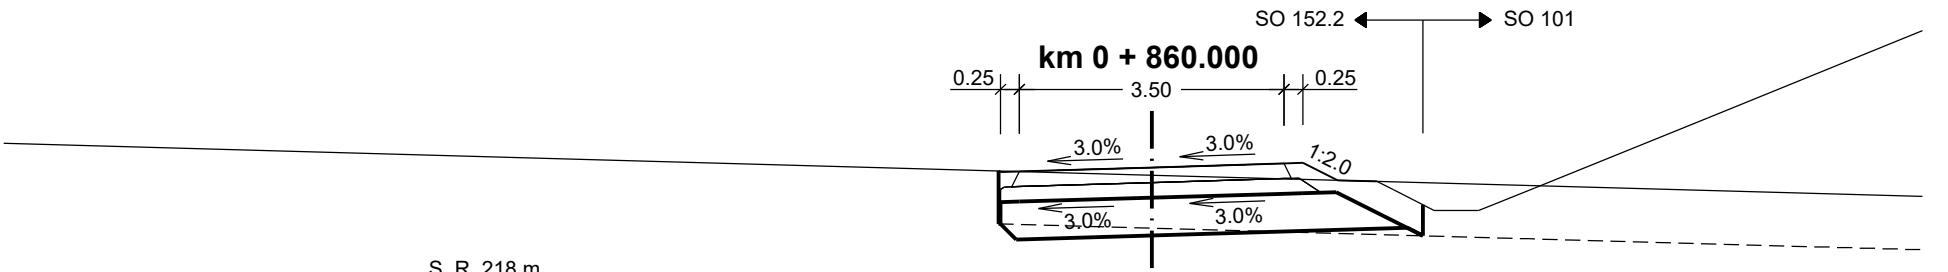


PROJEKTOVANÝ STAV ODSAZENÍ OD OSY	-2.03 219.88 -2.00 220.07 -1.75 219.86 0.00 220.01 1.75 220.06 2.00 220.07 2.00 219.84 3.38 219.81
STÁVAJÍCÍ TERÉN ODSAZENÍ OD OSY	0.00 219.81 4.99 219.77

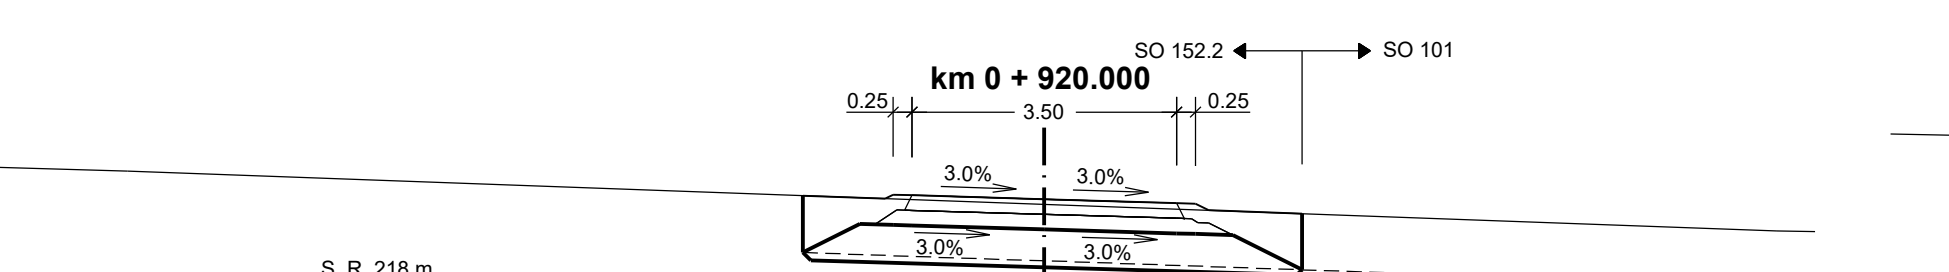


PROJEKTOVANÝ STAV ODSAZENÍ OD OSY	-3.19 219.64 -2.00 219.80 -2.00 219.81 -1.75 219.64 0.00 219.99 1.75 219.94 2.00 219.81 2.17 219.44 3.41 219.40
STÁVAJÍCÍ TERÉN ODSAZENÍ OD OSY	0.00 219.92 9.88 219.17

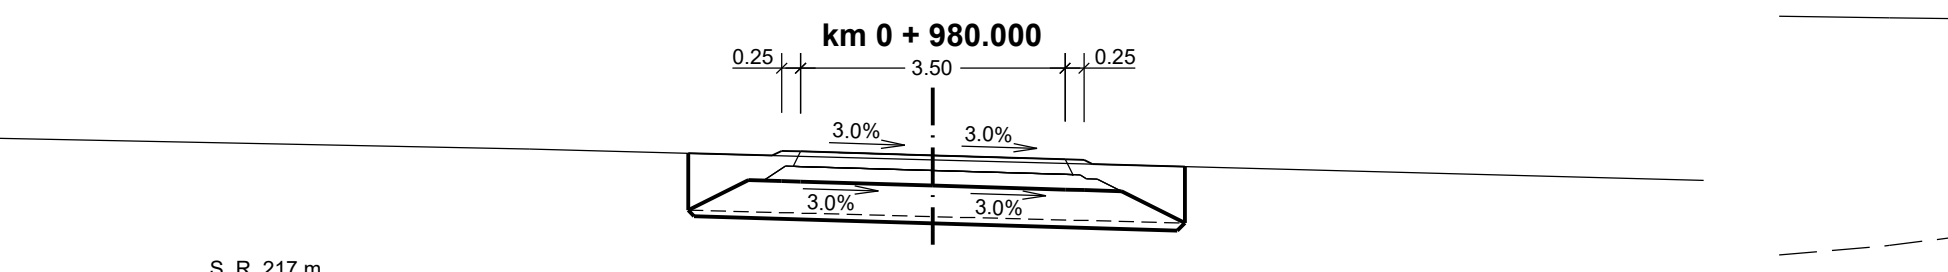


PROJEKTOVANÝ STAV ODSAZENÍ OD OSY	-3.24 219.20 -2.12 219.17 -2.00 219.25 -1.75 219.22 0.00 219.17 1.75 219.12 2.00 219.11 2.11 219.06 3.33 219.02
STÁVAJÍCÍ TERÉN ODSAZENÍ OD OSY	-5.34 219.25 0.00 219.11

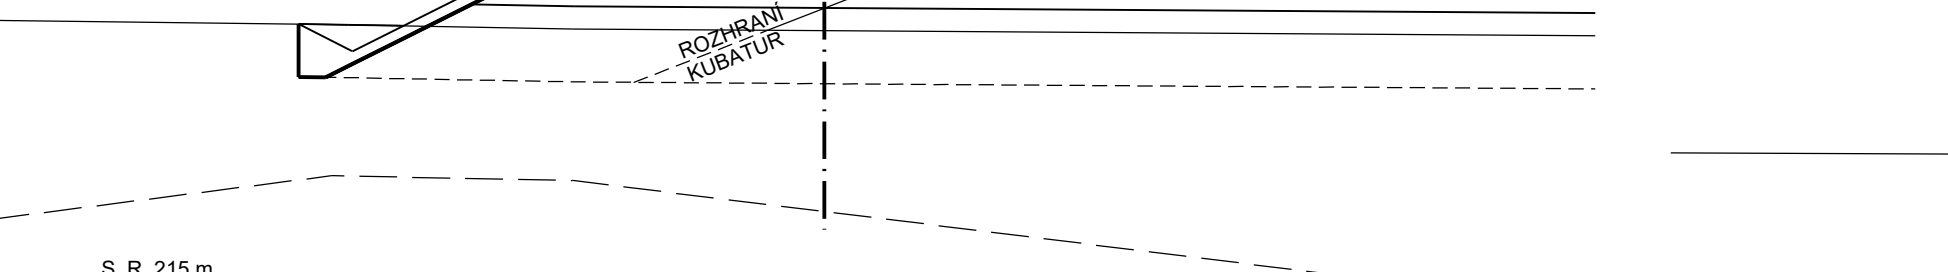


PROJEKTOVANÝ STAV ODSAZENÍ OD OSY	-7.26 219.90 -6.51 218.83 -5.91 218.93 -2.00 220.88 -1.75 220.89 0.00 220.84 1.75 220.76 2.00 220.79 2.80 221.02 4.59 220.83
STÁVAJÍCÍ TERÉN ODSAZENÍ OD OSY	-6.52 218.90 -3.33 218.84 0.00 218.82 1.75 220.76 2.00 220.79 2.80 221.02 4.59 220.83

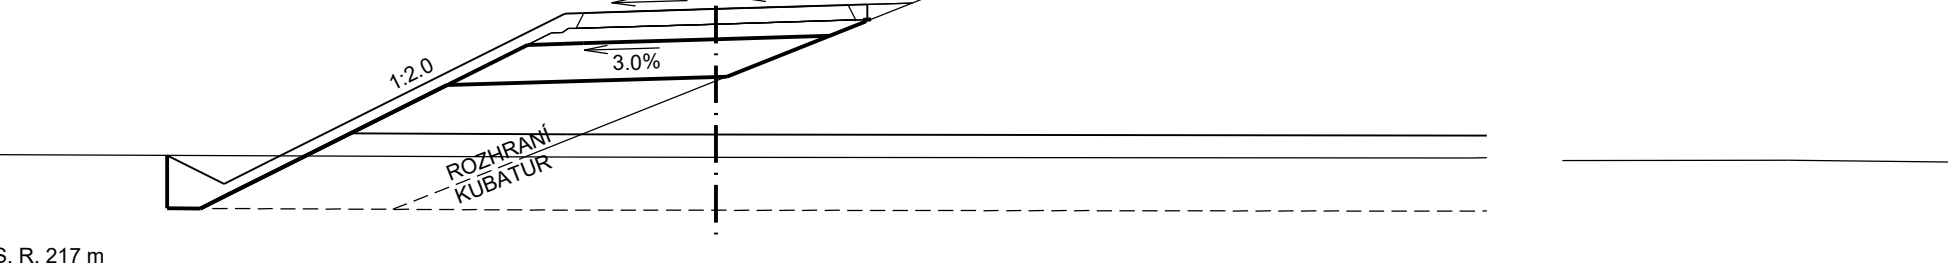


PROJEKTOVANÝ STAV ODSAZENÍ OD OSY	-7.26 219.90 -6.51 218.83 -5.91 218.93 -2.00 220.88 -1.75 220.89 0.00 220.84 1.75 220.76 2.00 220.79 2.80 221.02 4.59 220.83
STÁVAJÍCÍ TERÉN ODSAZENÍ OD OSY	10.00 218.97

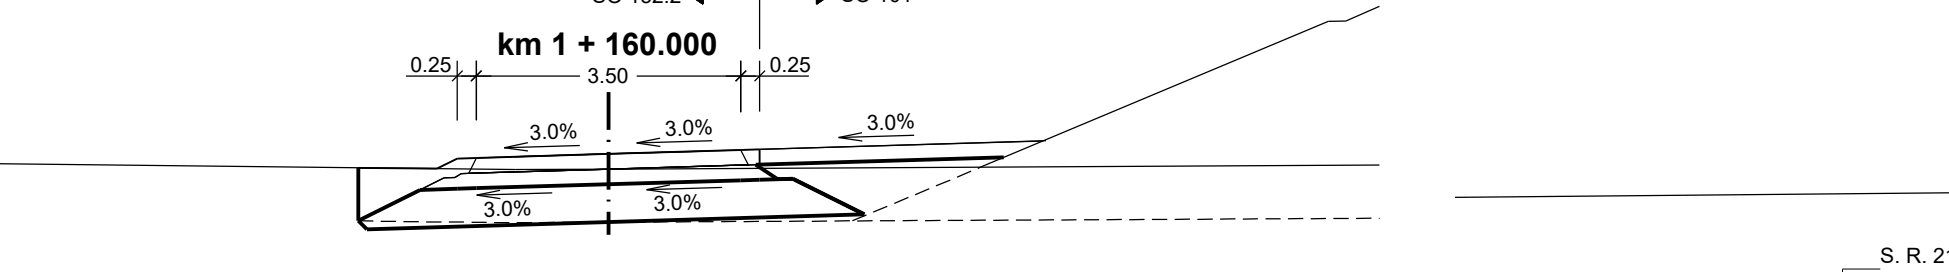


PROJEKTOVANÝ STAV ODSAZENÍ OD OSY	-3.31 219.94 -2.27 219.83 -2.00 220.71 -1.75 219.97 0.00 220.02 1.75 220.07 2.00 220.08 5.79 220.19
STÁVAJÍCÍ TERÉN ODSAZENÍ OD OSY	7.00 220.98

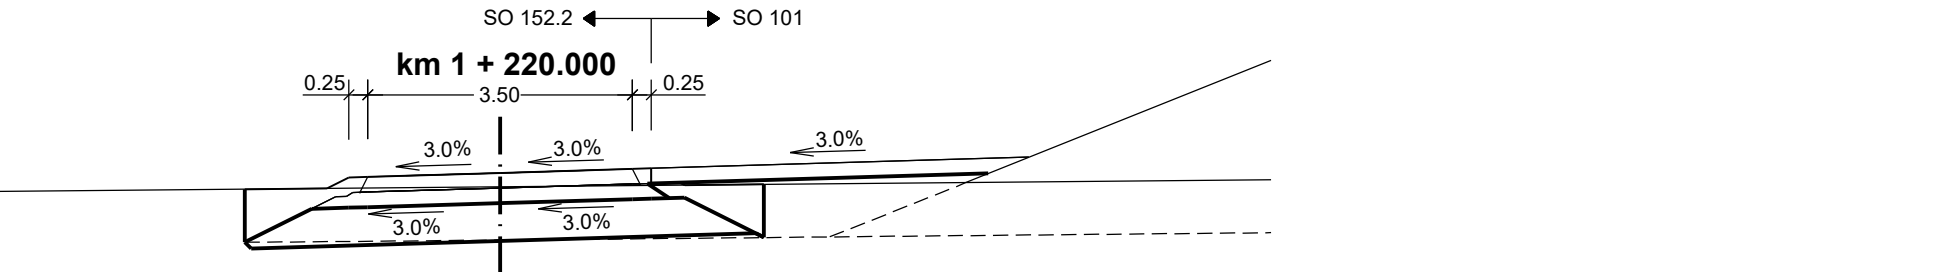


PROJEKTOVANÝ STAV ODSAZENÍ OD OSY	-3.38 220.95 -2.27 220.83 -2.00 220.71 -1.75 220.72 0.00 220.77 1.75 220.83 2.00 220.83 7.00 220.98
STÁVAJÍCÍ TERÉN ODSAZENÍ OD OSY	7.00 220.98

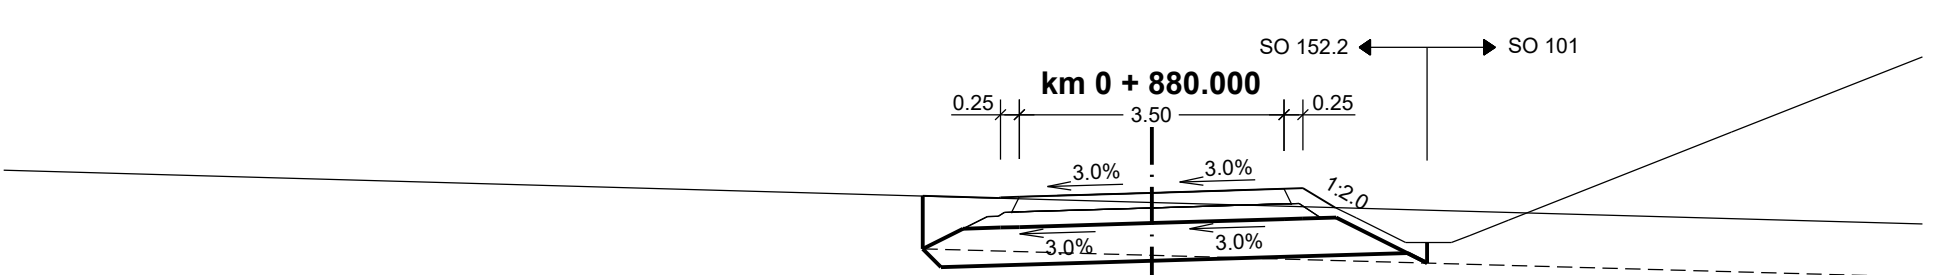


PROJEKTOVANÝ STAV ODSAZENÍ OD OSY	-3.03 219.83 -2.02 219.80 -2.00 219.81 -1.75 219.82 0.00 219.87 1.75 219.82 2.00 219.83 2.51 219.87 3.64 219.84
STÁVAJÍCÍ TERÉN ODSAZENÍ OD OSY	0.00 219.74

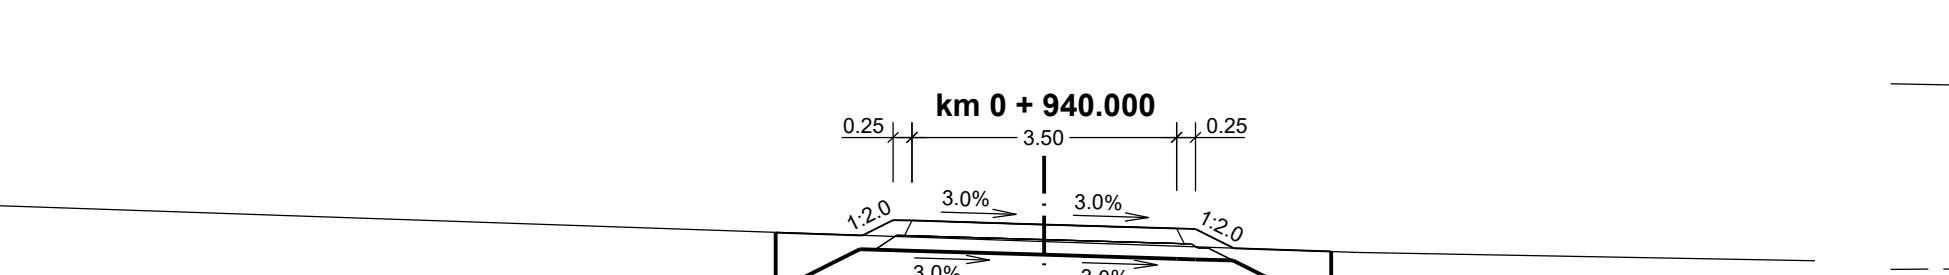


PROJEKTOVANÝ STAV ODSAZENÍ OD OSY	-3.55 219.35 -2.01 219.81 -2.00 219.81 -1.75 219.50 0.00 219.45 1.75 219.40 2.00 219.83 2.51 219.14 3.80 219.09
STÁVAJÍCÍ TERÉN ODSAZENÍ OD OSY	4.14 218.08

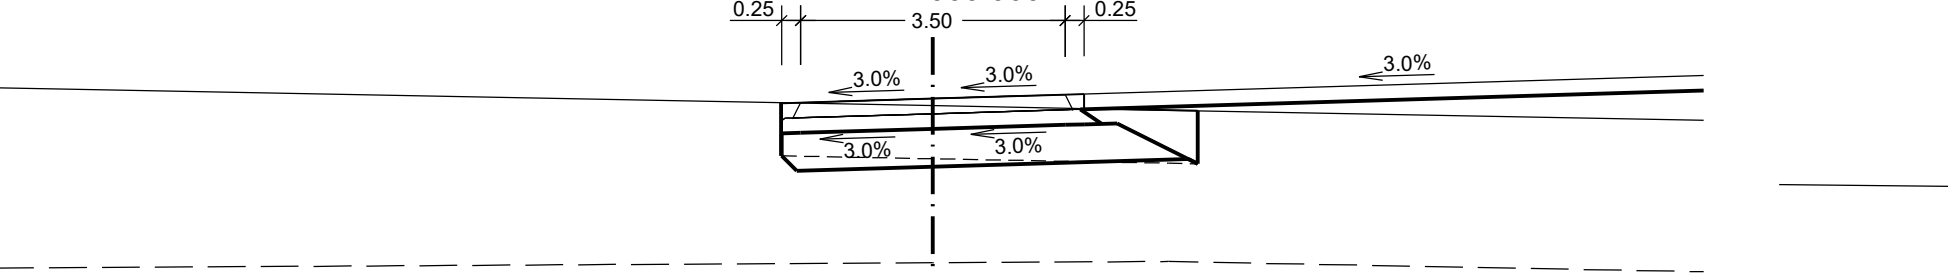


PROJEKTOVANÝ STAV ODSAZENÍ OD OSY	-2.01 219.06 -2.00 219.06 -1.75 219.06 0.00 219.12 1.75 219.17 2.00 219.18 2.40 218.96 3.51 218.96
STÁVAJÍCÍ TERÉN ODSAZENÍ OD OSY	3.12 218.96

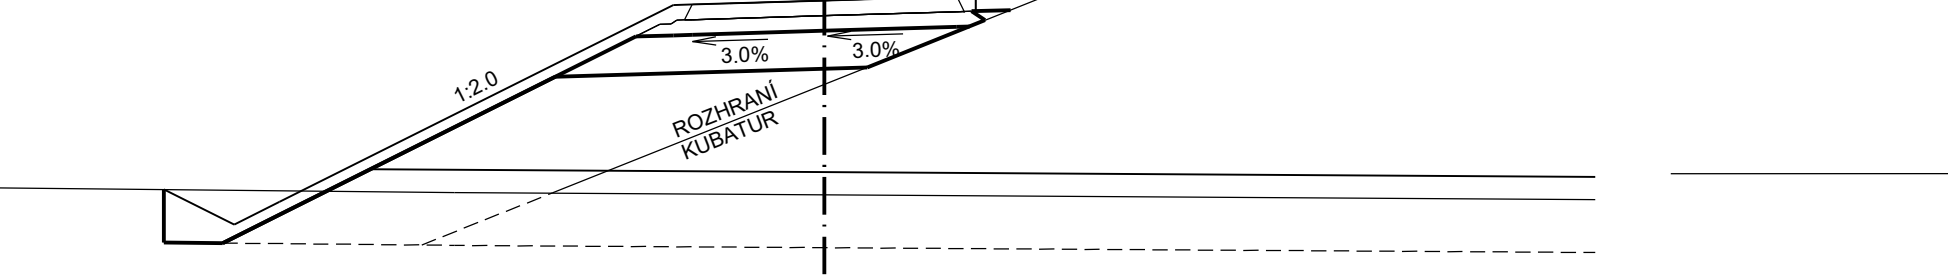


PROJEKTOVANÝ STAV ODSAZENÍ OD OSY	-8.74 218.91 -7.81 218.45 -7.21 218.75 -2.00 221.35 -1.75 221.36 0.00 221.41 1.75 221.47 2.00 221.47 3.00 221.50
STÁVAJÍCÍ TERÉN ODSAZENÍ OD OSY	0.00 218.84

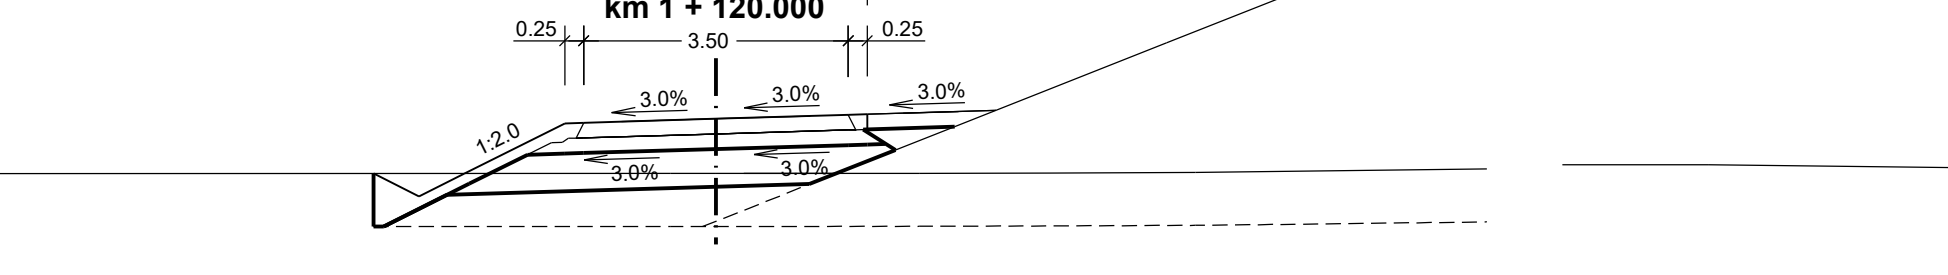


PROJEKTOVANÝ STAV ODSAZENÍ OD OSY	-4.53 219.13 -3.89 218.83 -3.33 218.13 -2.00 219.79 -1.75 219.50 0.00 219.85 1.75 219.85 2.00 219.81 2.69 219.13 4.43 219.13 6.35 219.14
STÁVAJÍCÍ TERÉN ODSAZENÍ OD OSY	0.00 218.14

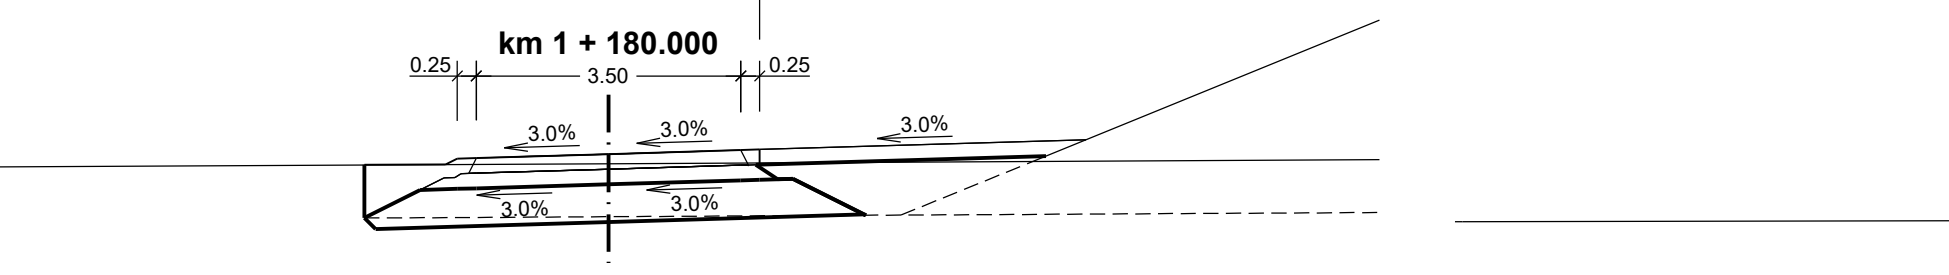


PROJEKTOVANÝ STAV ODSAZENÍ OD OSY	-3.23 220.24 -2.16 220.25 -2.00 220.34 -1.75 220.33 0.00 220.38 1.75 220.44 2.00 220.44 6.32 220.57
STÁVAJÍCÍ TERÉN ODSAZENÍ OD OSY	0.00 220.38

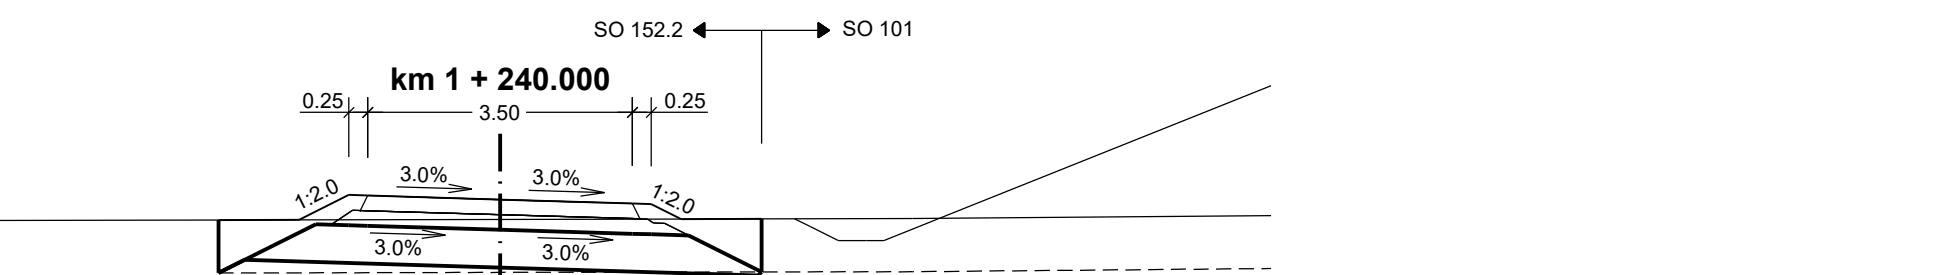


PROJEKTOVANÝ STAV ODSAZENÍ OD OSY	-3.73 220.51 -2.66 220.51 -2.00 220.84 -1.75 220.83 0.00 220.78 1.75 220.72 2.00 220.72 2.40 220.52 3.46 220.53
STÁVAJÍCÍ TERÉN ODSAZENÍ OD OSY	5.45 220.53

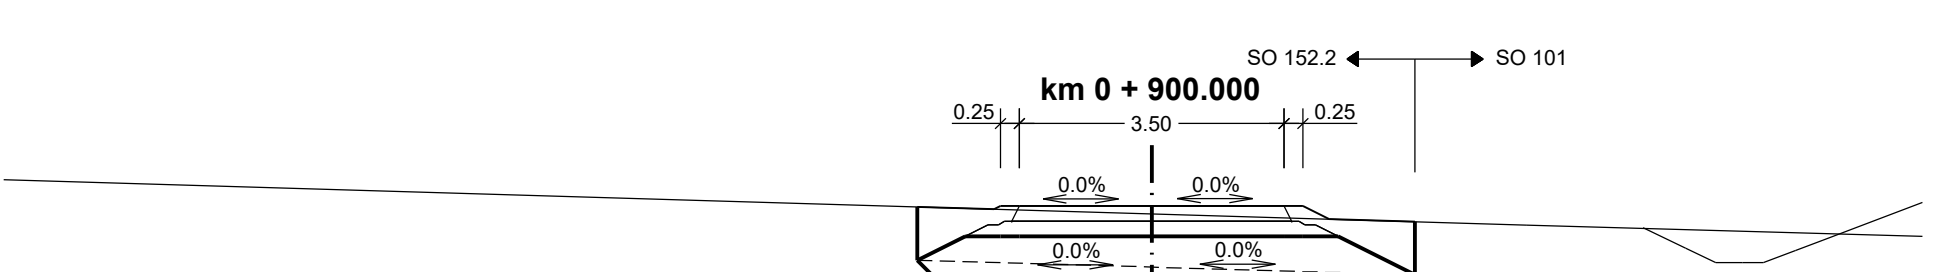


PROJEKTOVANÝ STAV ODSAZENÍ OD OSY	-3.10 219.72 -2.08 219.69 -2.00 219.73 -1.75 219.73 0.00 219.73 1.75 219.73 2.00 219.73 2.50 219.58 3.48 219.62
STÁVAJÍCÍ TERÉN ODSAZENÍ OD OSY	0.00 219.63 4.88 219.48

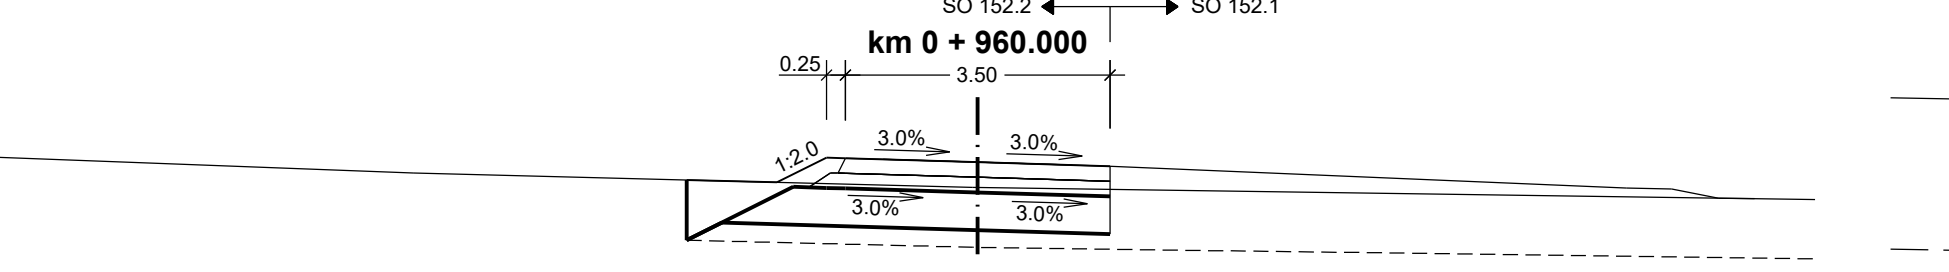


PROJEKTOVANÝ STAV ODSAZENÍ OD OSY	-3.85 219.08 -2.85 219.04 -2.00 219.39 -1.75 219.39 0.00 219.31 1.75 219.28 2.00 219.28 2.50 219.28 3.48 219.28
STÁVAJÍCÍ TERÉN ODSAZENÍ OD OSY	-7.47 218.17 1.75 219.28

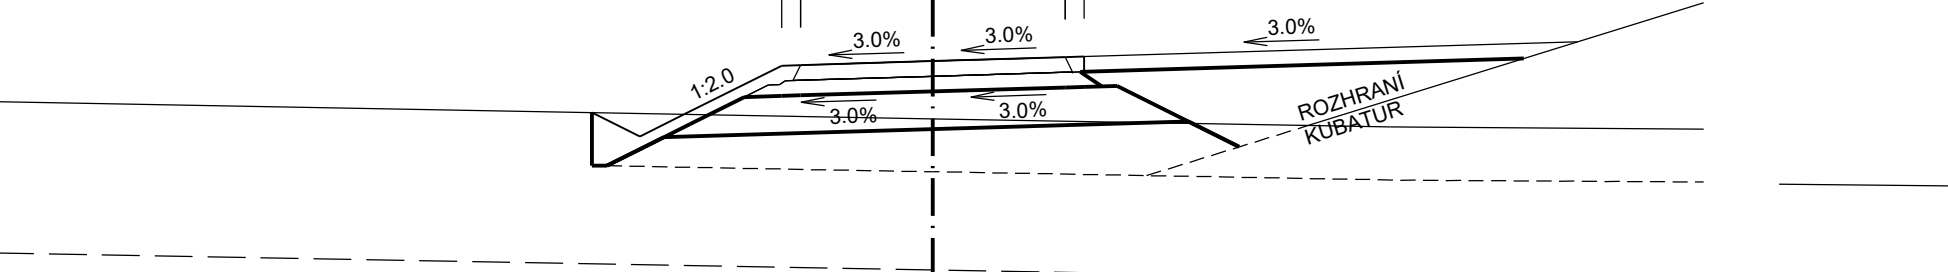


PROJEKTOVANÝ STAV ODSAZENÍ OD OSY	-4.51 218.97 -3.88 218.85 -3.32 218.85 -2.00 219.09 -1.75 219.09 0.00 219.05 1.75 219.05 2.00 219.05 2.50 219.05 3.06 218.97 6.53 218.96
STÁVAJÍCÍ TERÉN ODSAZENÍ OD OSY	6.53 218.96

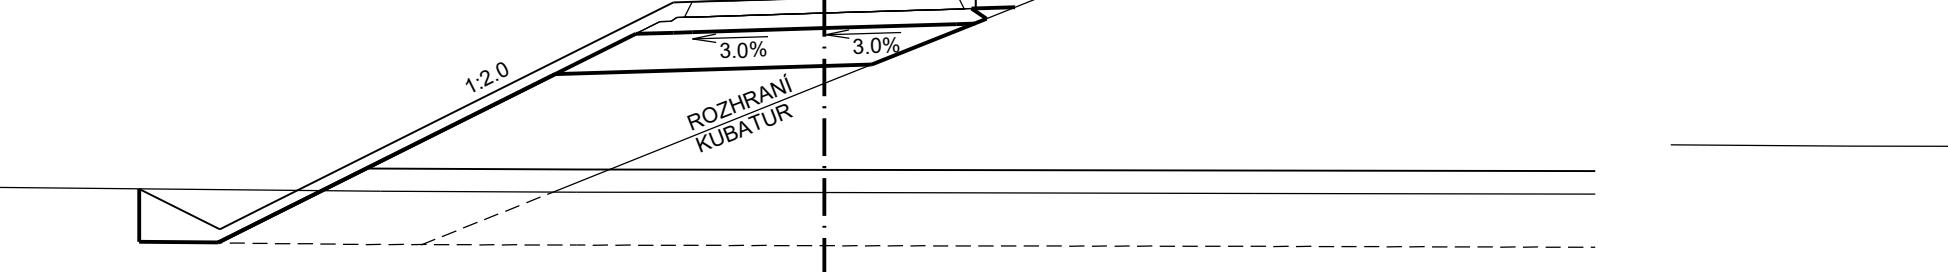


PROJEKTOVANÝ STAV ODSAZENÍ OD OSY	-9.08 218.86 -8.00 218.43 -7.40 218.73 -2.00 221.42 -1.75 221.43 0.00 221.48 1.75 221.54 2.00 221.54 3.06 221.58
STÁVAJÍCÍ TERÉN ODSAZENÍ OD OSY	5.68 218.80

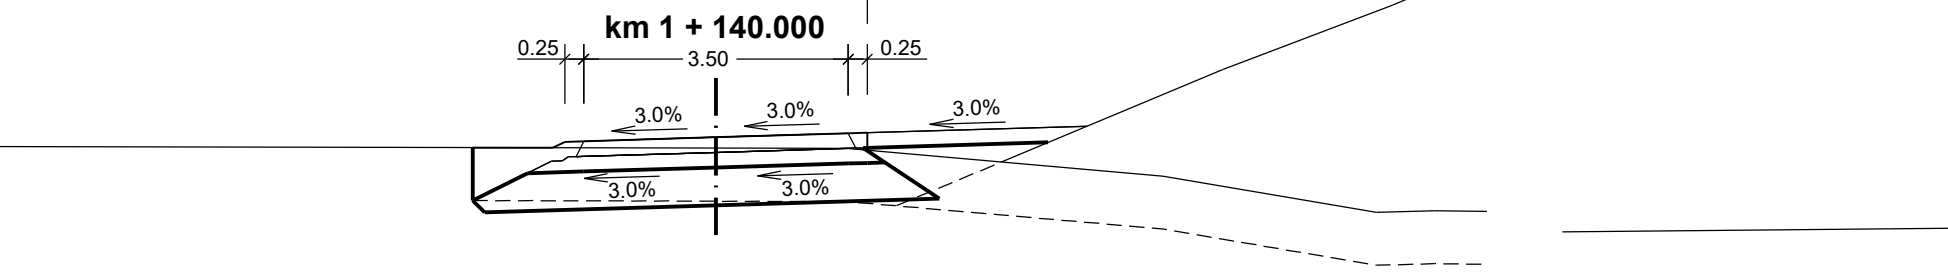

PROJEKTOVANÝ STAV ODSAZENÍ OD OSY	-3.22 219.50 -2.15 219.50 -2.00 219.50 -1.75 219.50 0.00 219.64 1.75 219.64 2.00 219.64 2.50 219.64 3.06 219.64 4.91 219.79
STÁVAJÍCÍ TERÉN ODSAZENÍ OD OSY	4.91 219.79

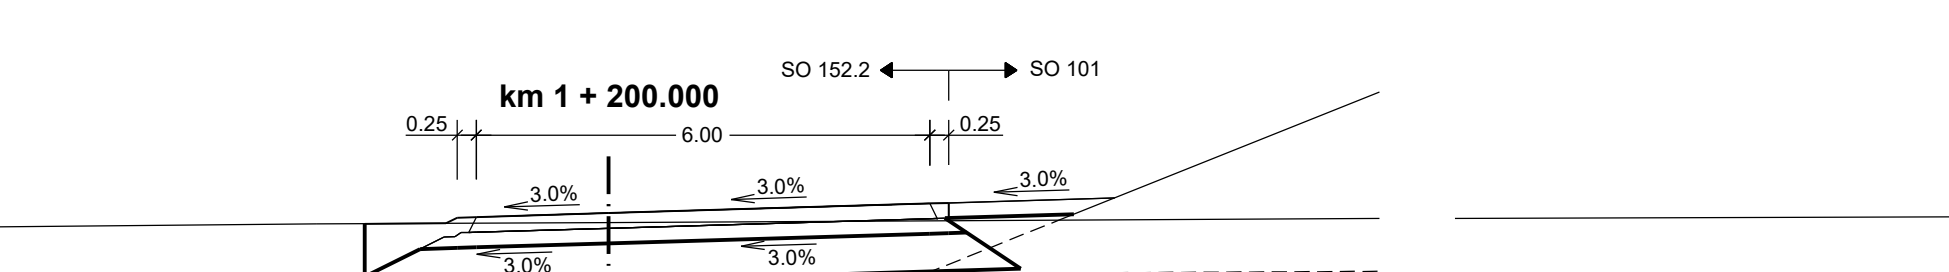

PROJEKTOVANÝ STAV ODSAZENÍ OD OSY	-3.23 220.50 -2.16 220.50 -2.00 220.50 -1.75 220.50 0.00 220.64 1.75 220.64 2.00 220.64 2.50 220.64 3.06 220.64 6.68 220.64
STÁVAJÍCÍ TERÉN ODSAZENÍ OD OSY	6.68 220.64

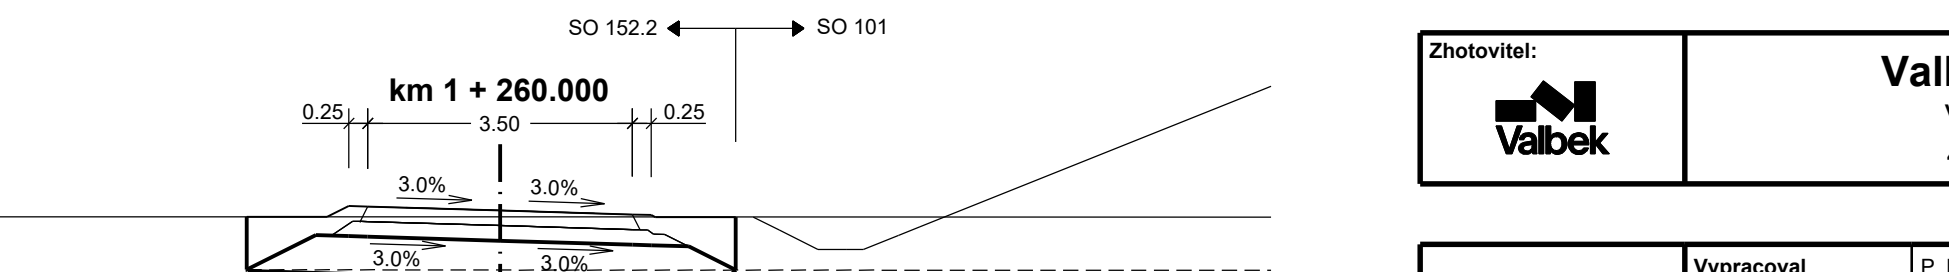

PROJEKTOVANÝ STAV ODSAZENÍ OD OSY	-3.32 220.59 -2.25 220.59 -2.00 220.73 -1.75 220.73 0.00 220.87 1.75 220.87 2.00 220.87 2.50 220.87 3.12 220.87 5.23 220.87
STÁVAJÍCÍ TERÉN ODSAZENÍ OD OSY	5.23 220.87

Výškový systém: Bpv

SO 152 Přístupy na pozemky k.ú. Židněves

**ŘEDITELSTVÍ
SILNIC
A DÁLNIC**

Ředitelství silnic a dálnic s. p.
Čertánská 2023/12, Křč, 140 00 Praha 4

Valbek

Valbek, spol. s r.o.
Vaňurova 505/17
460 07 Liberec 3

Valbek	Vypracoval Zodp. projektant Třech. kontrola Akce	P. BARTUSEK ING. T. KLIMENT ING. M. HANZL	Zak. číslo Datum Stupeň Počet formátů Měřítko Č. přílohy	21-LH3-001 02/2025 PPPS 20 x A4 1 : 100 Paré
Zhotovitel: Valbek, spol. s r.o. Vaňurova 505/17 460 07 Liberec 3	Příloha	PŘÍČNÉ ŘEZY SO 152.2 - km 0,860 - 1,260		