
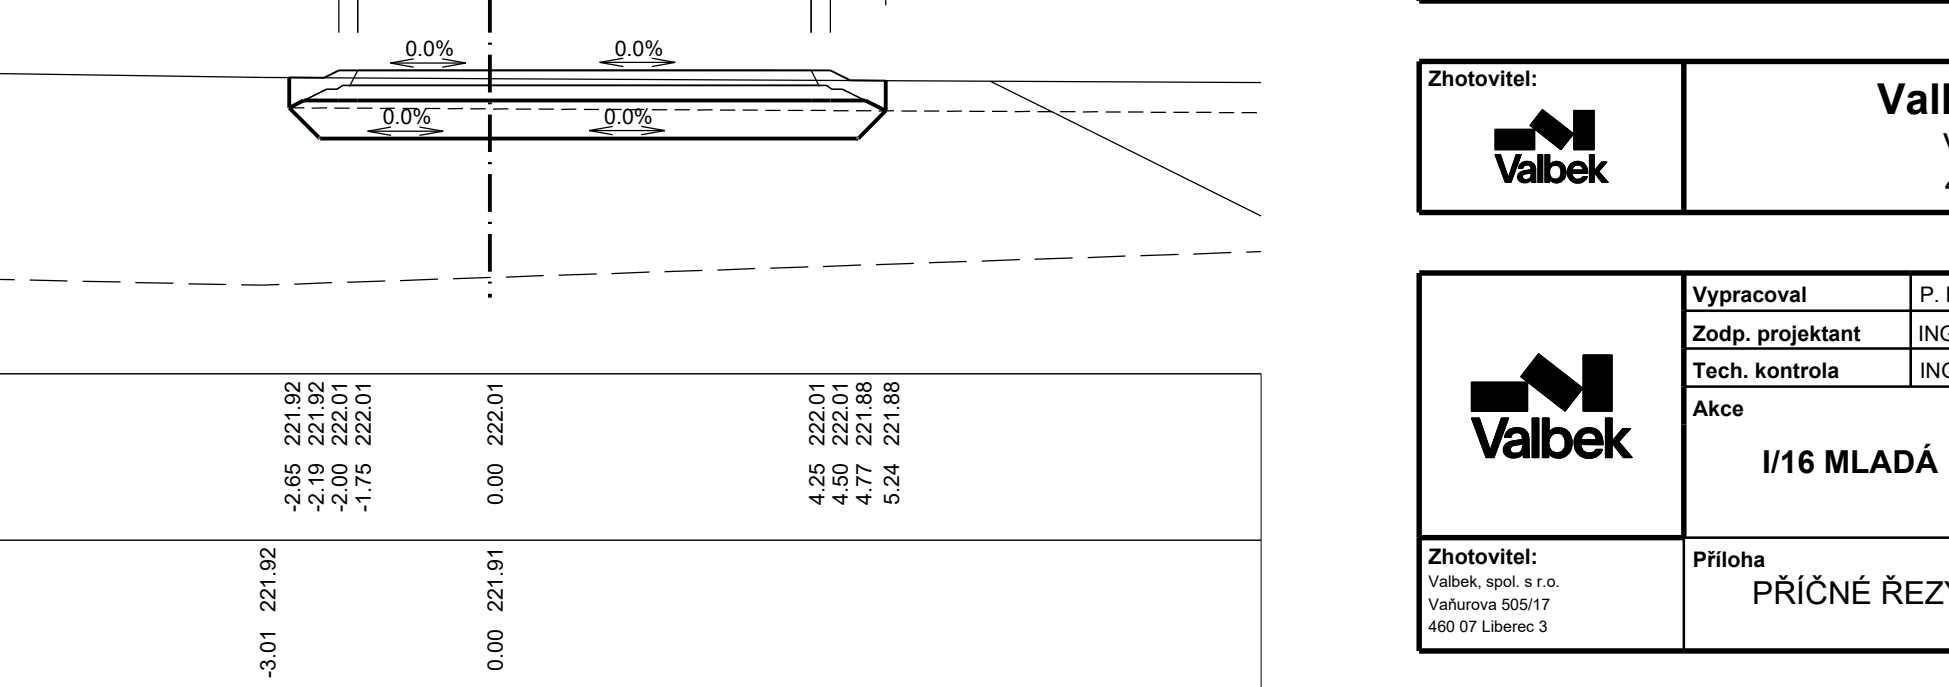
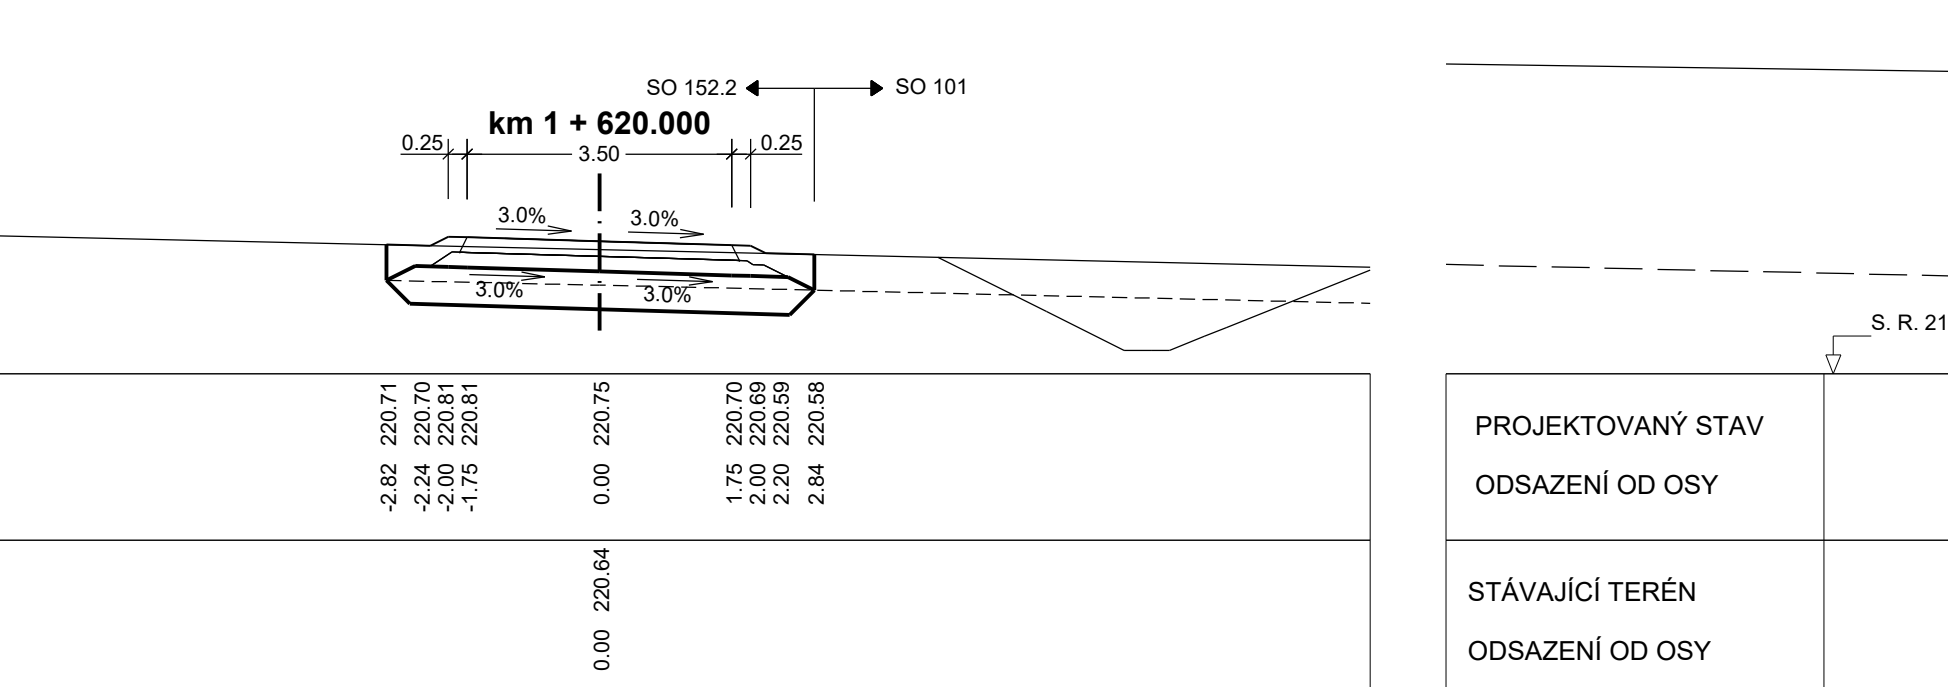
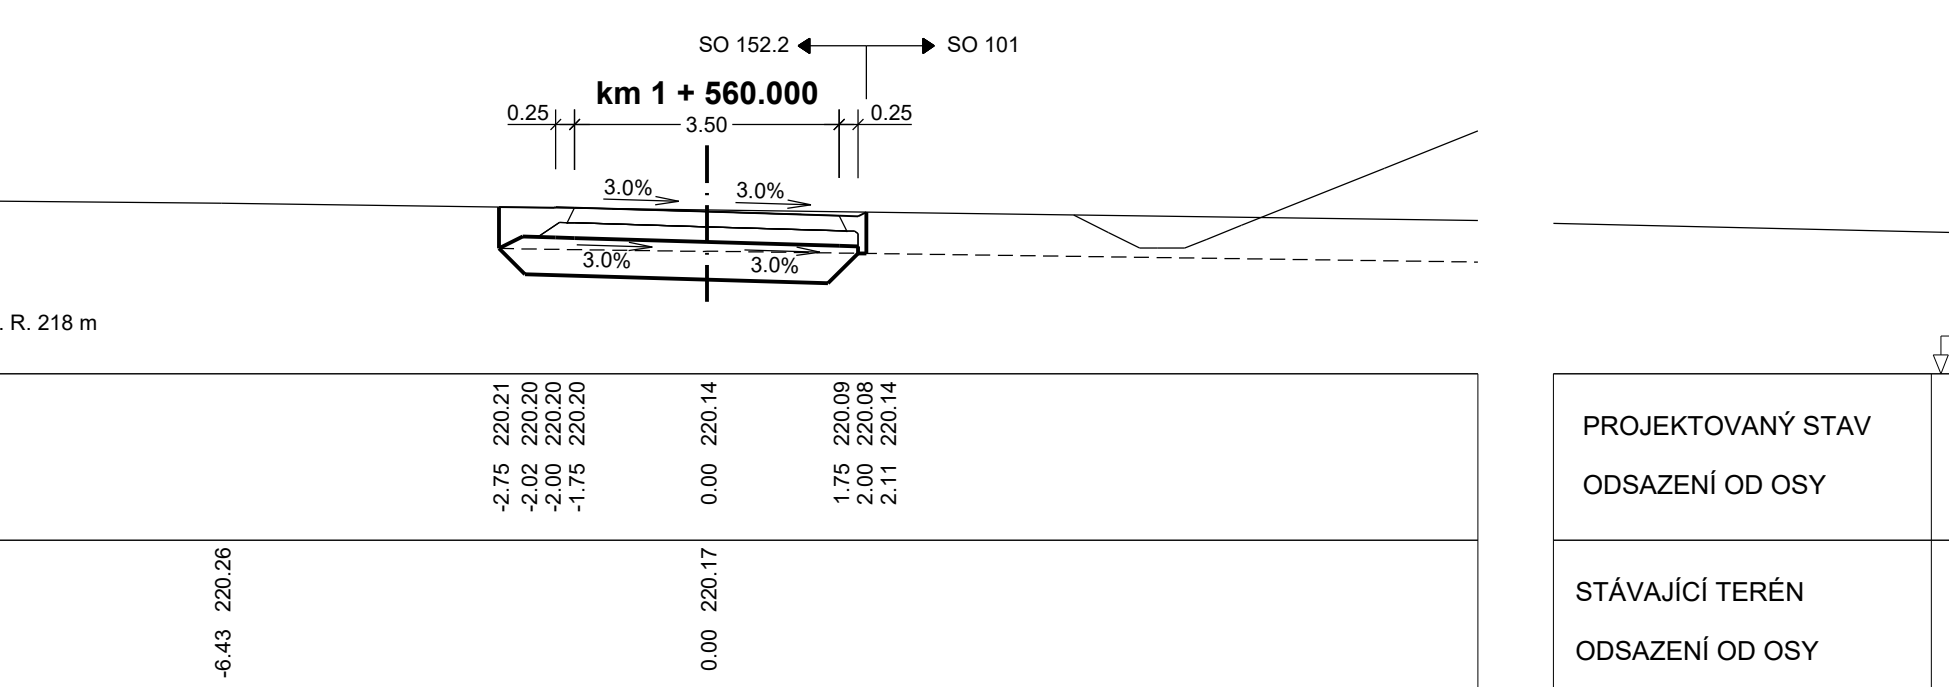
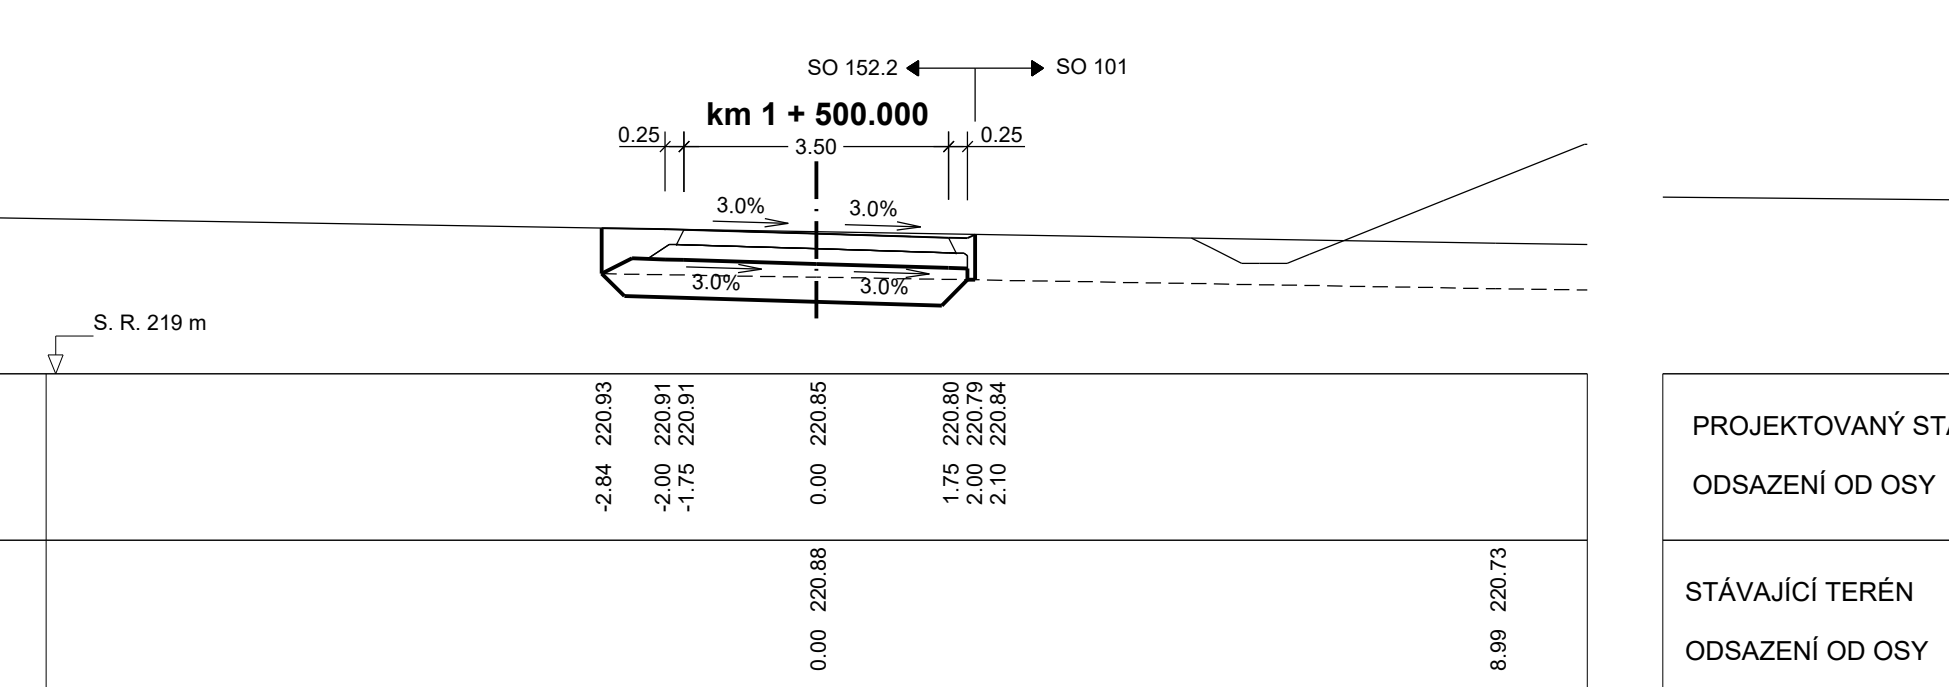
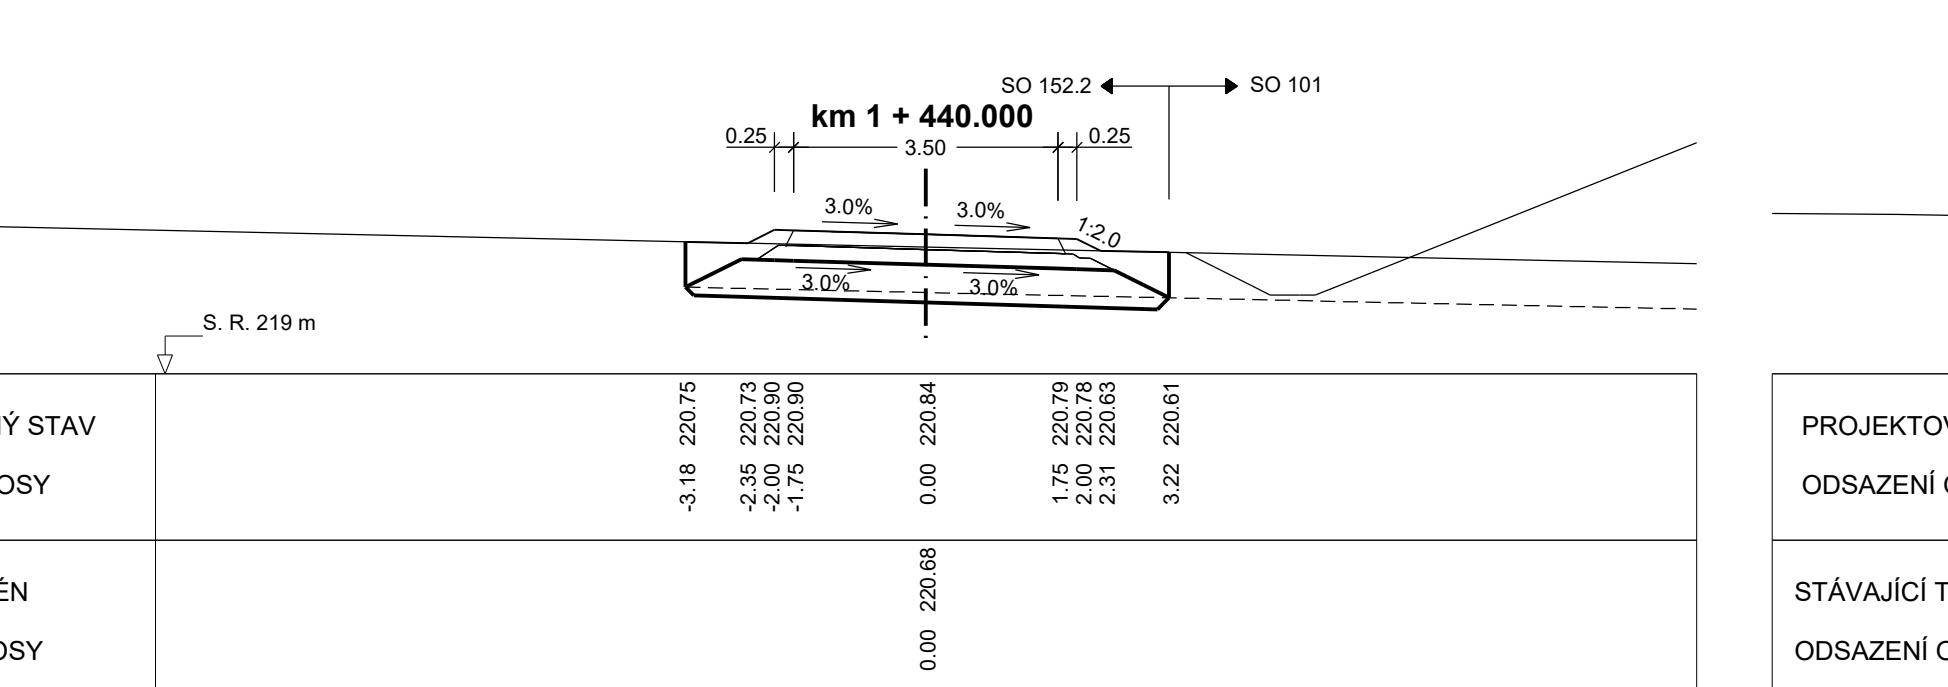
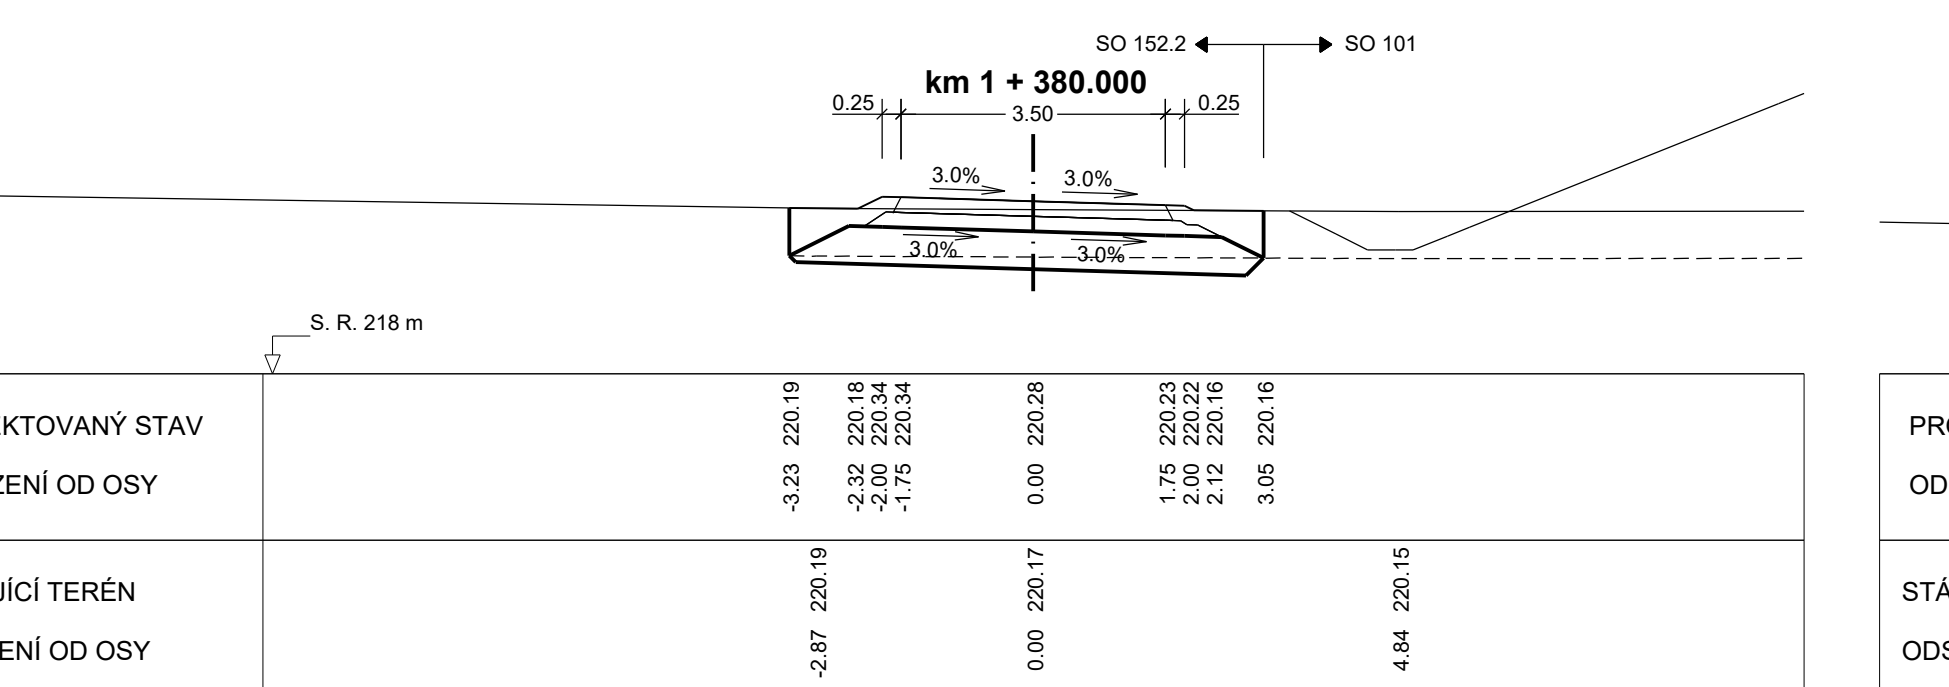
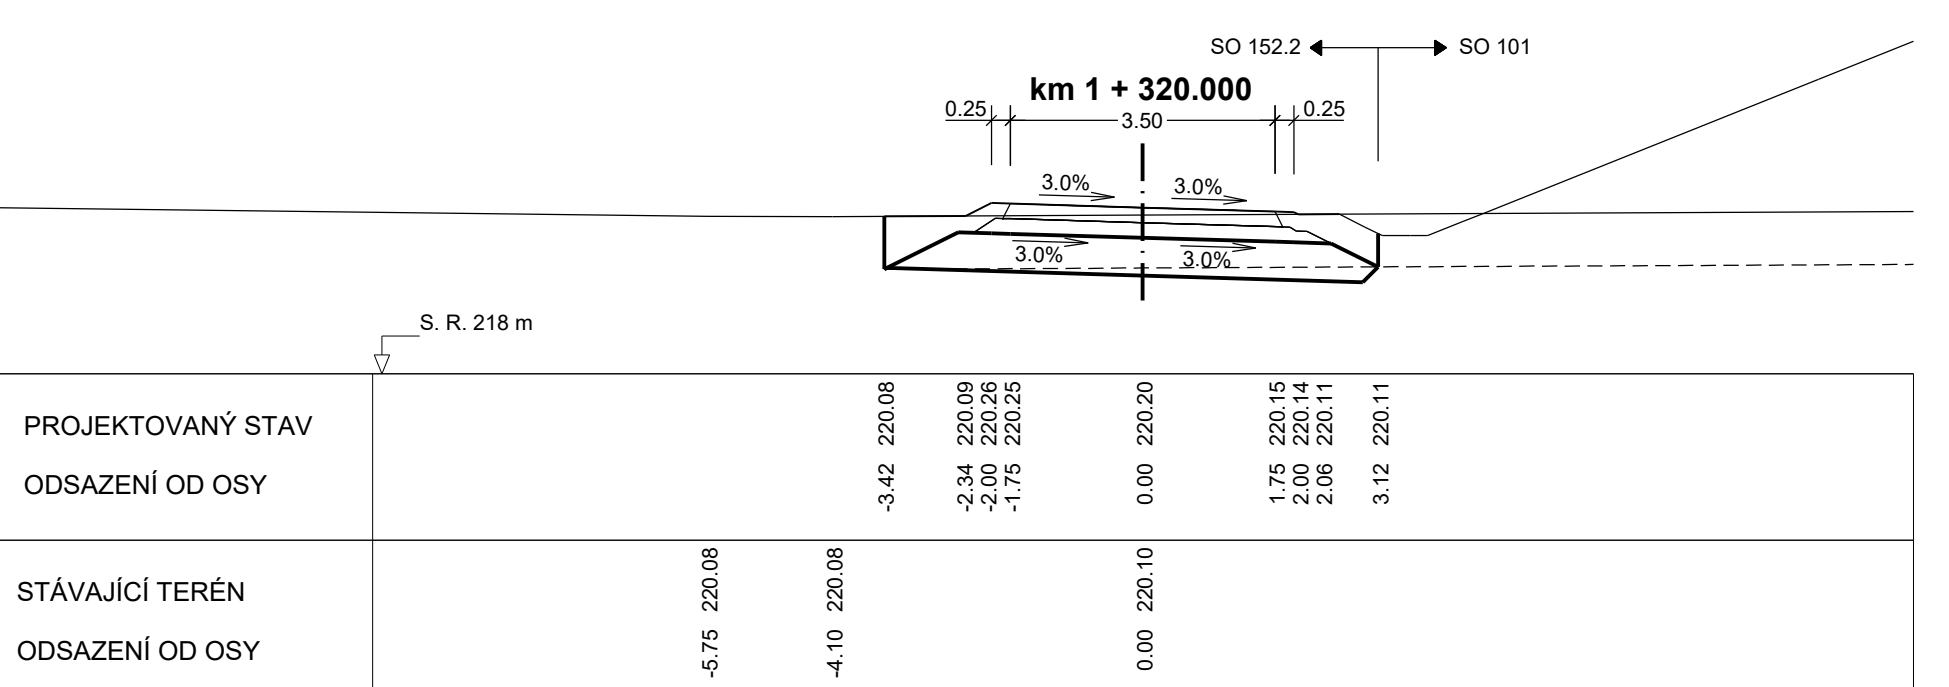
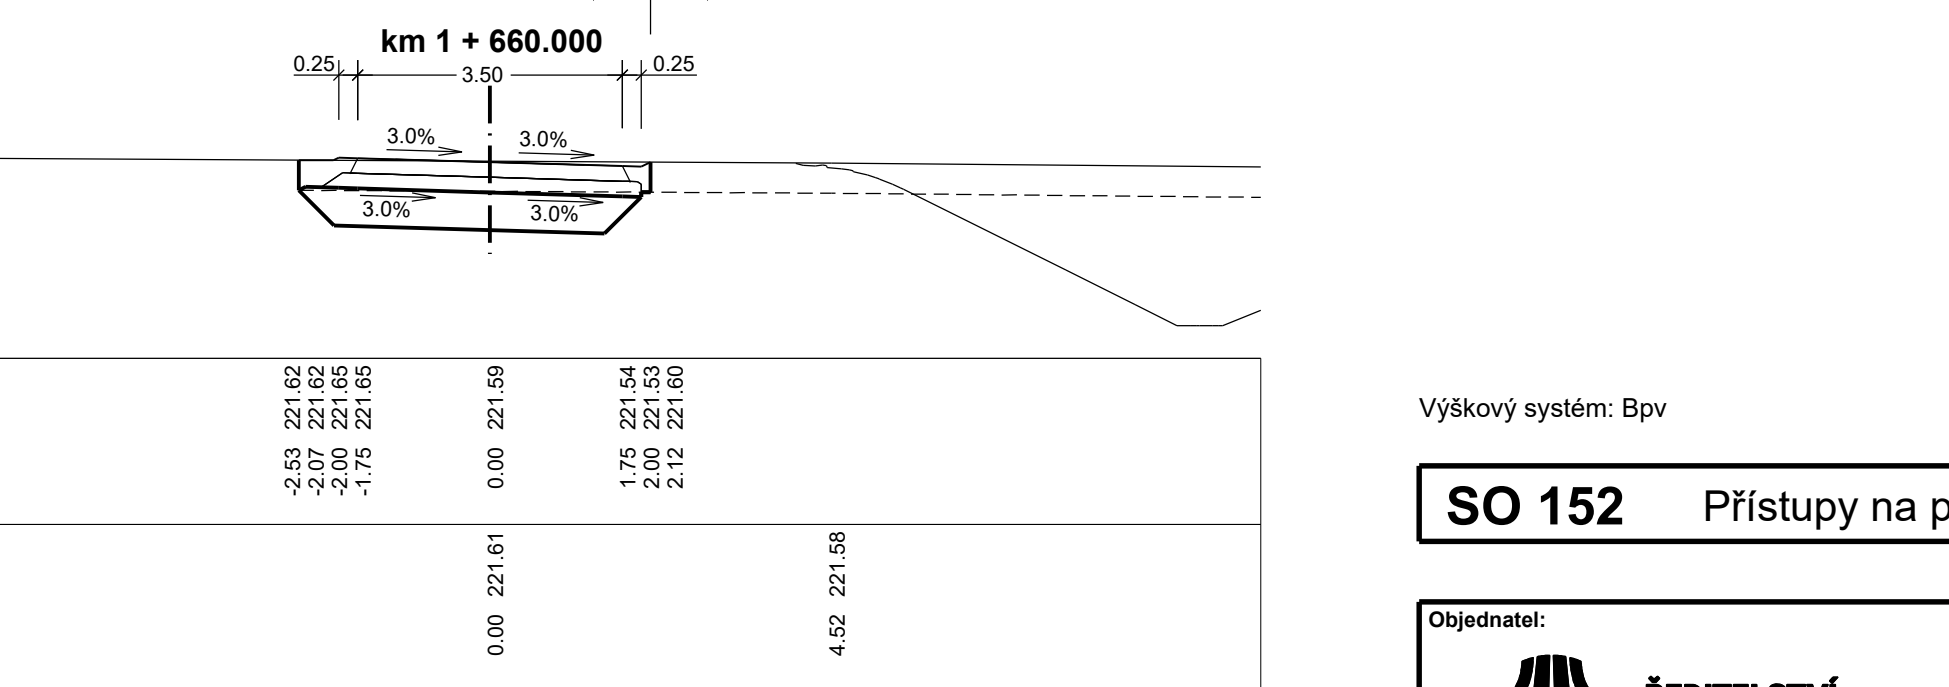
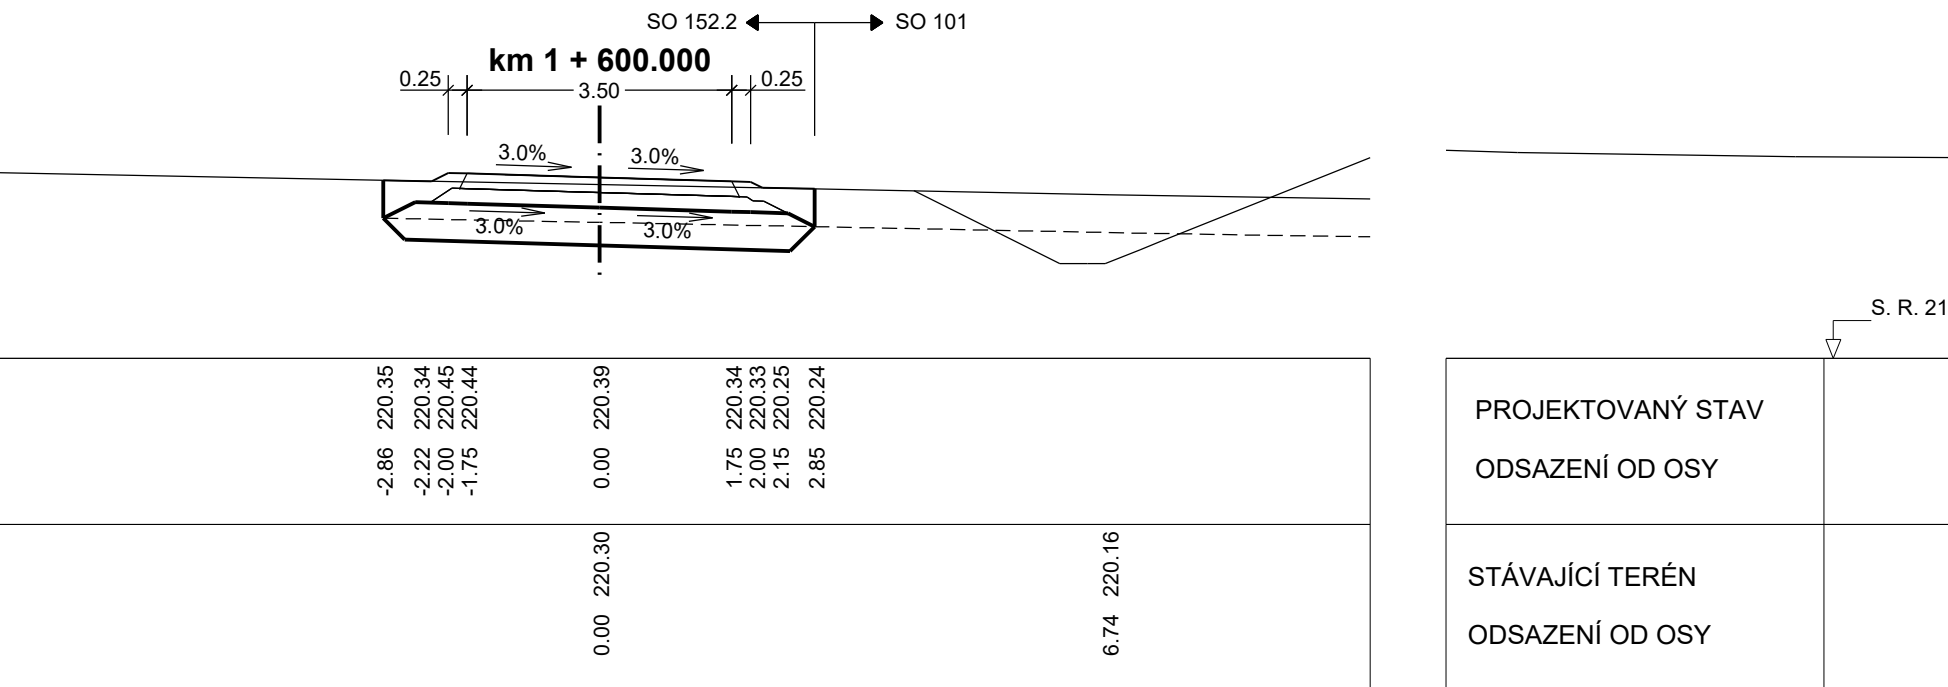
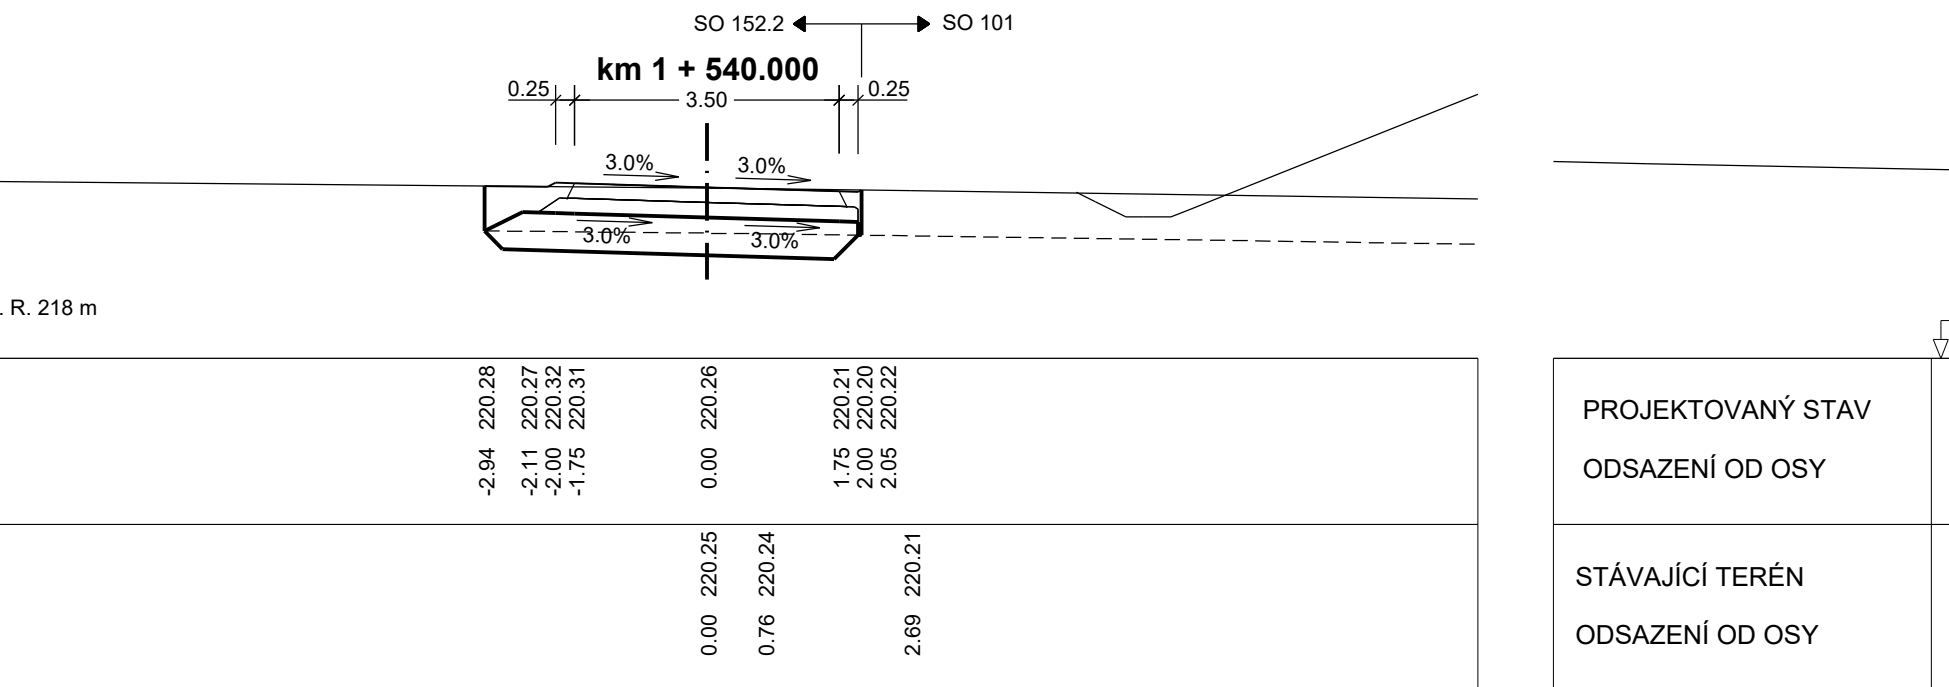
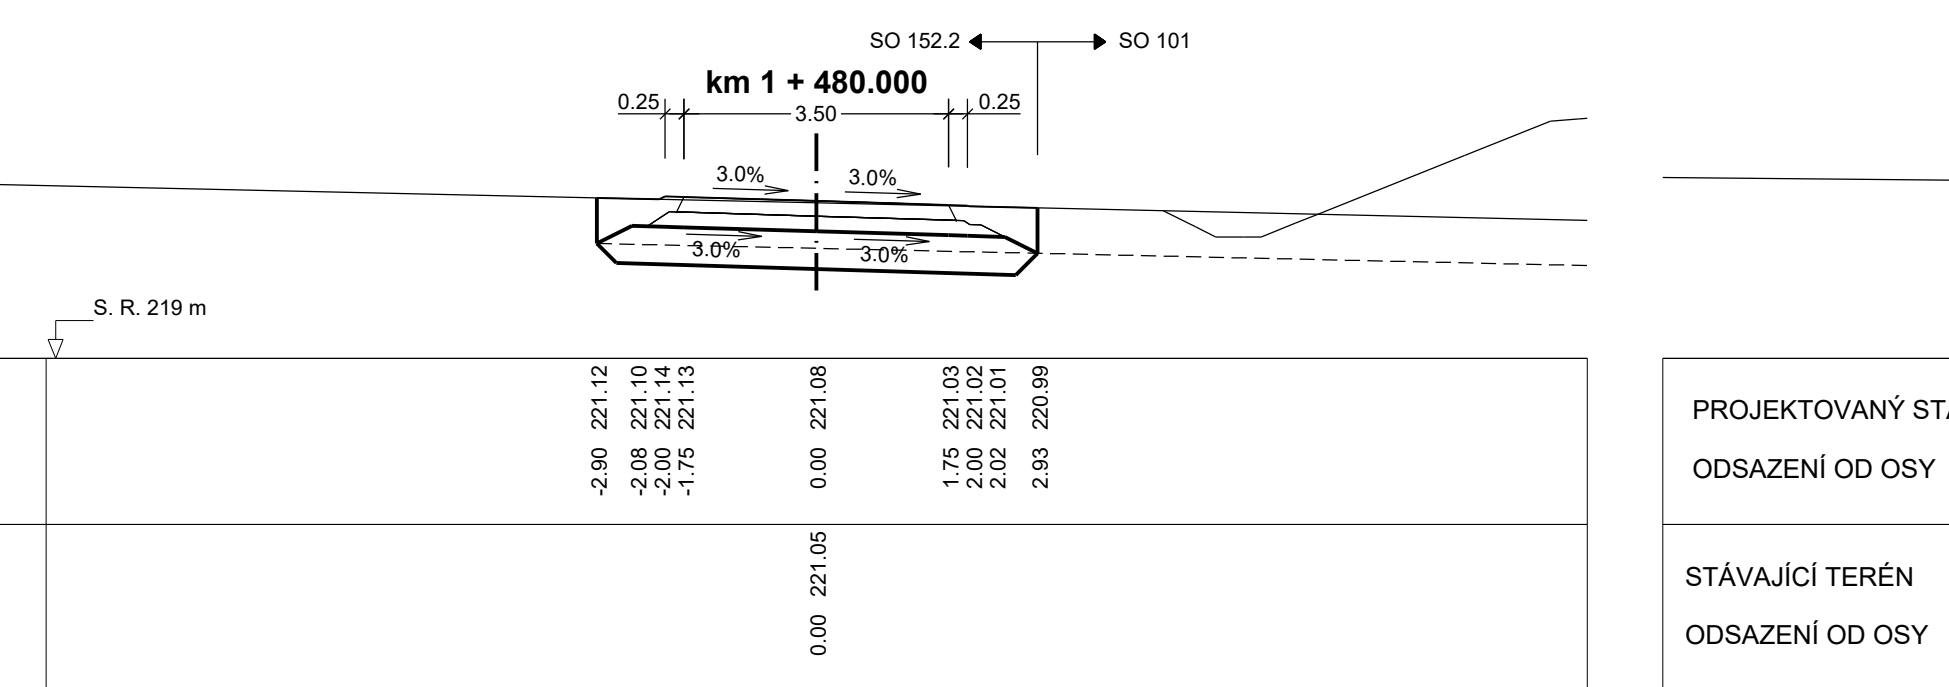
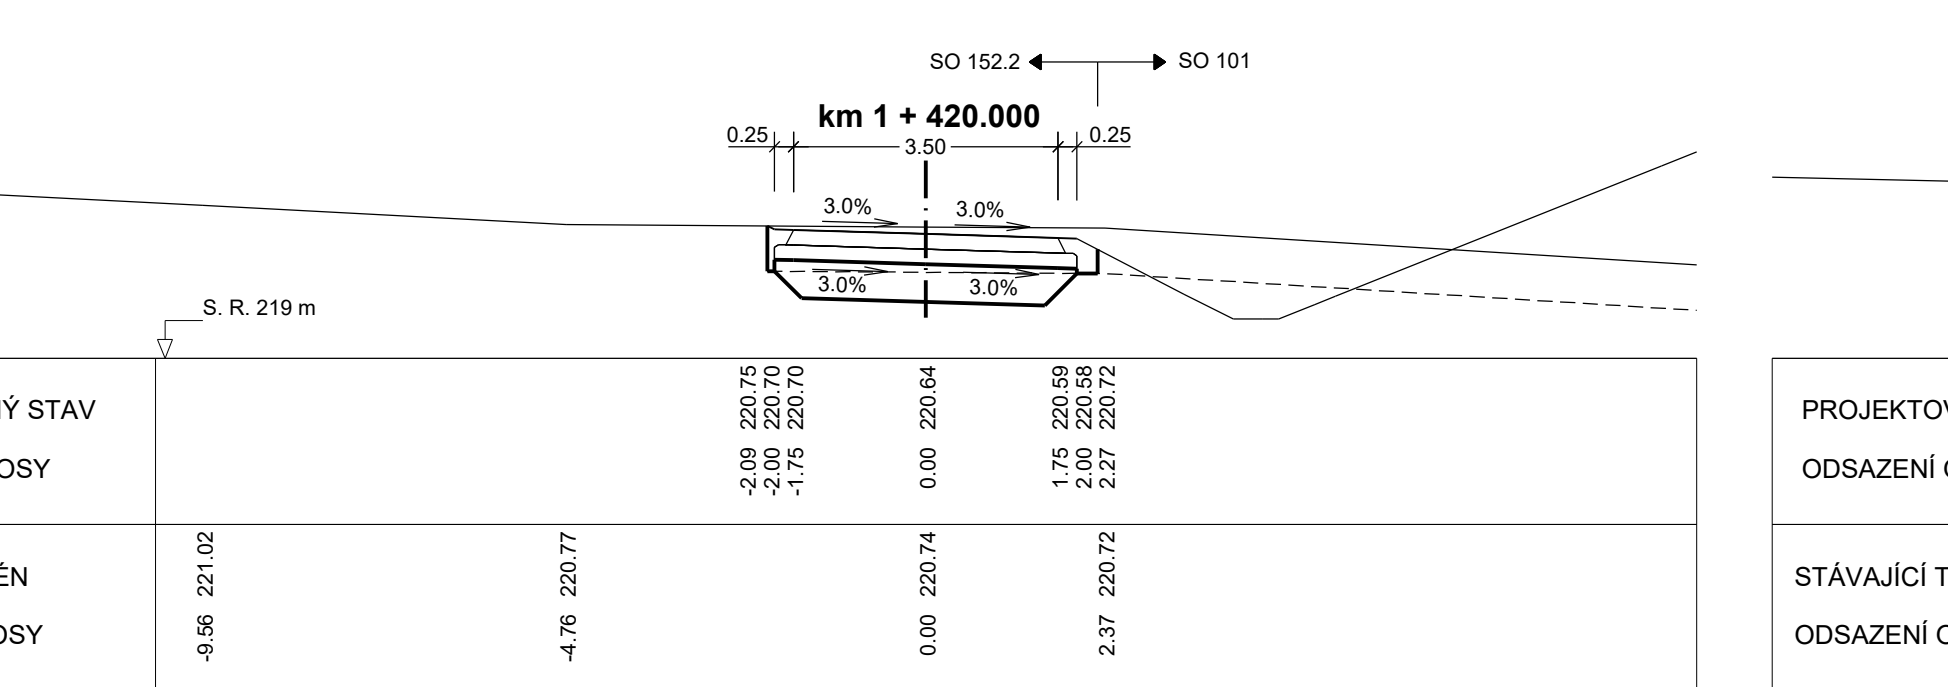
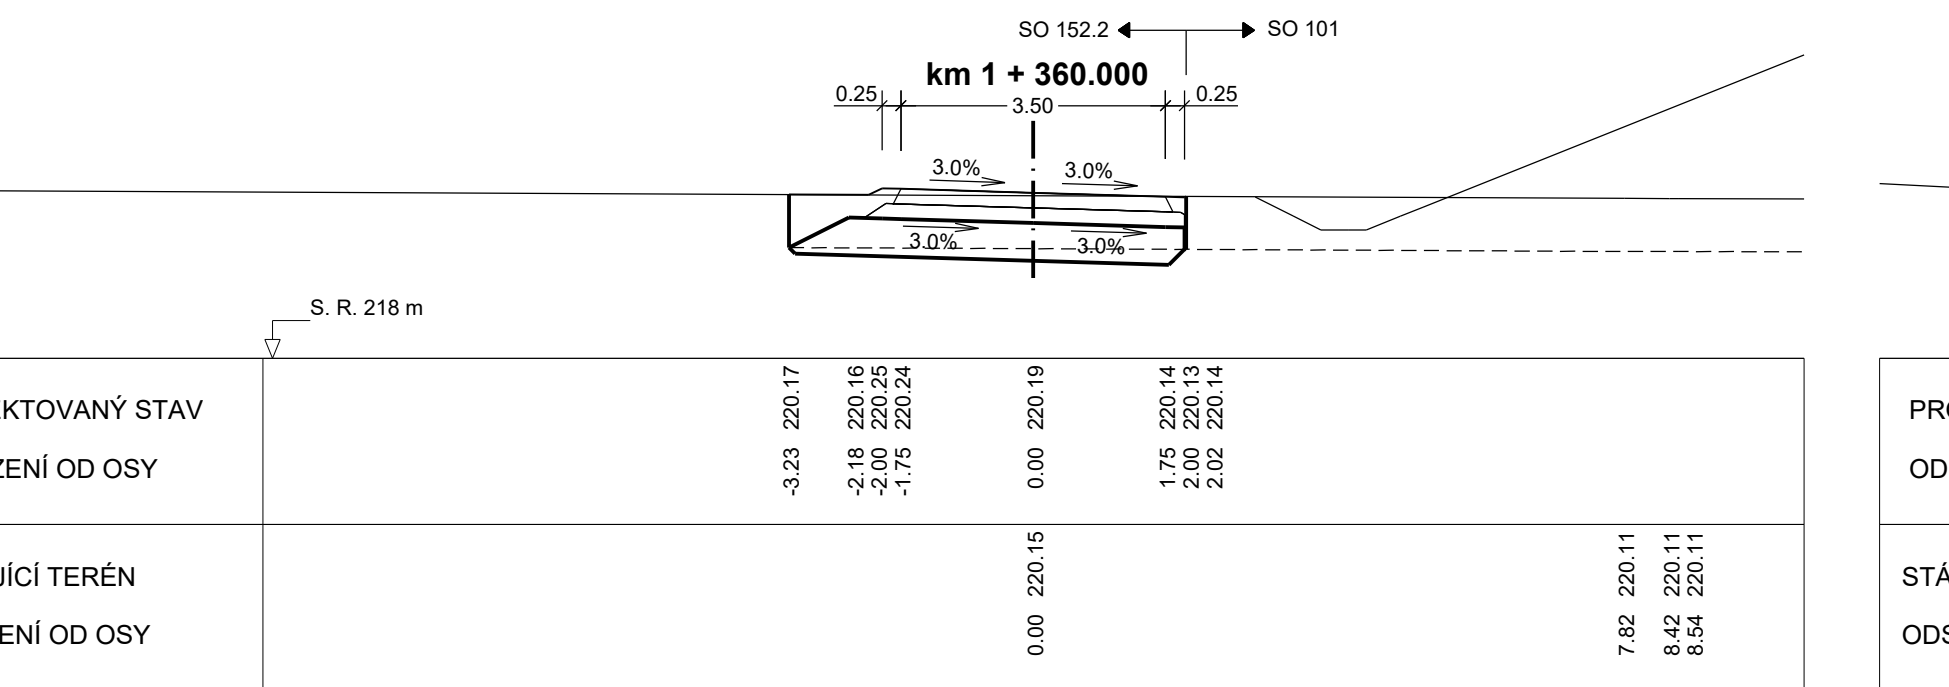
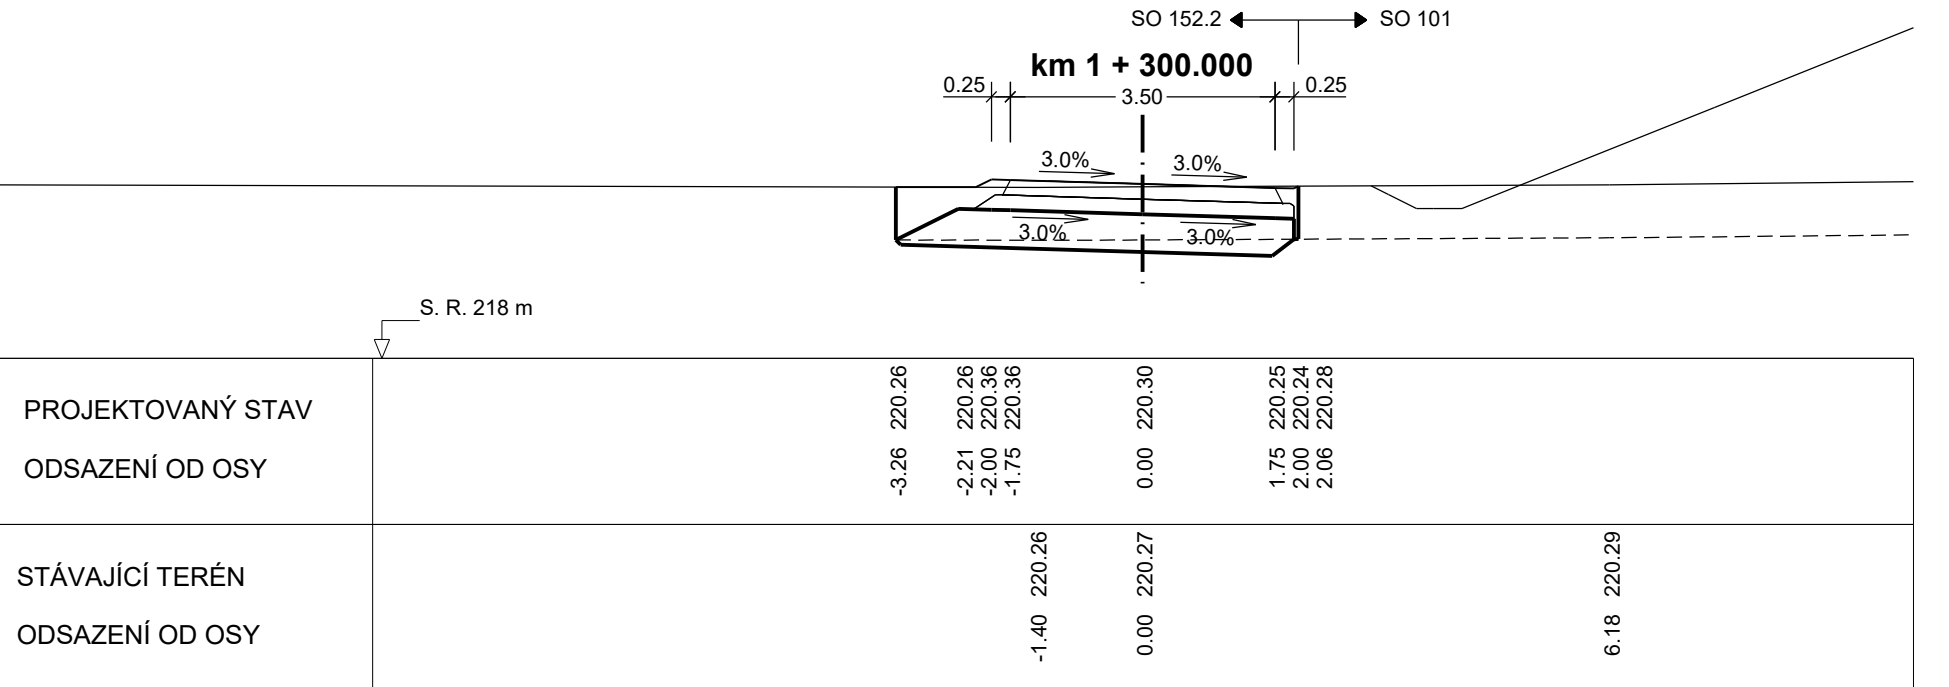
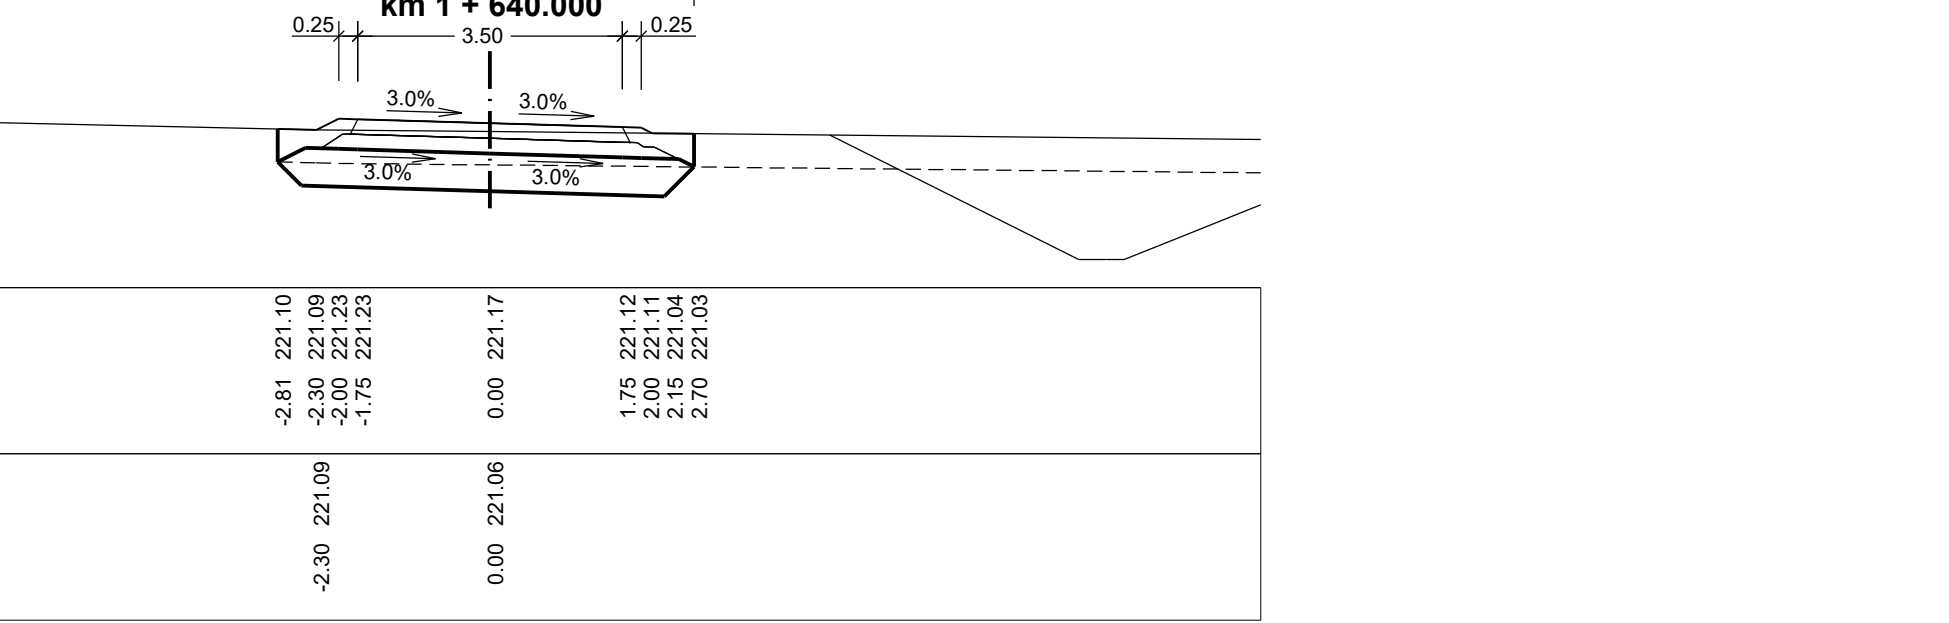
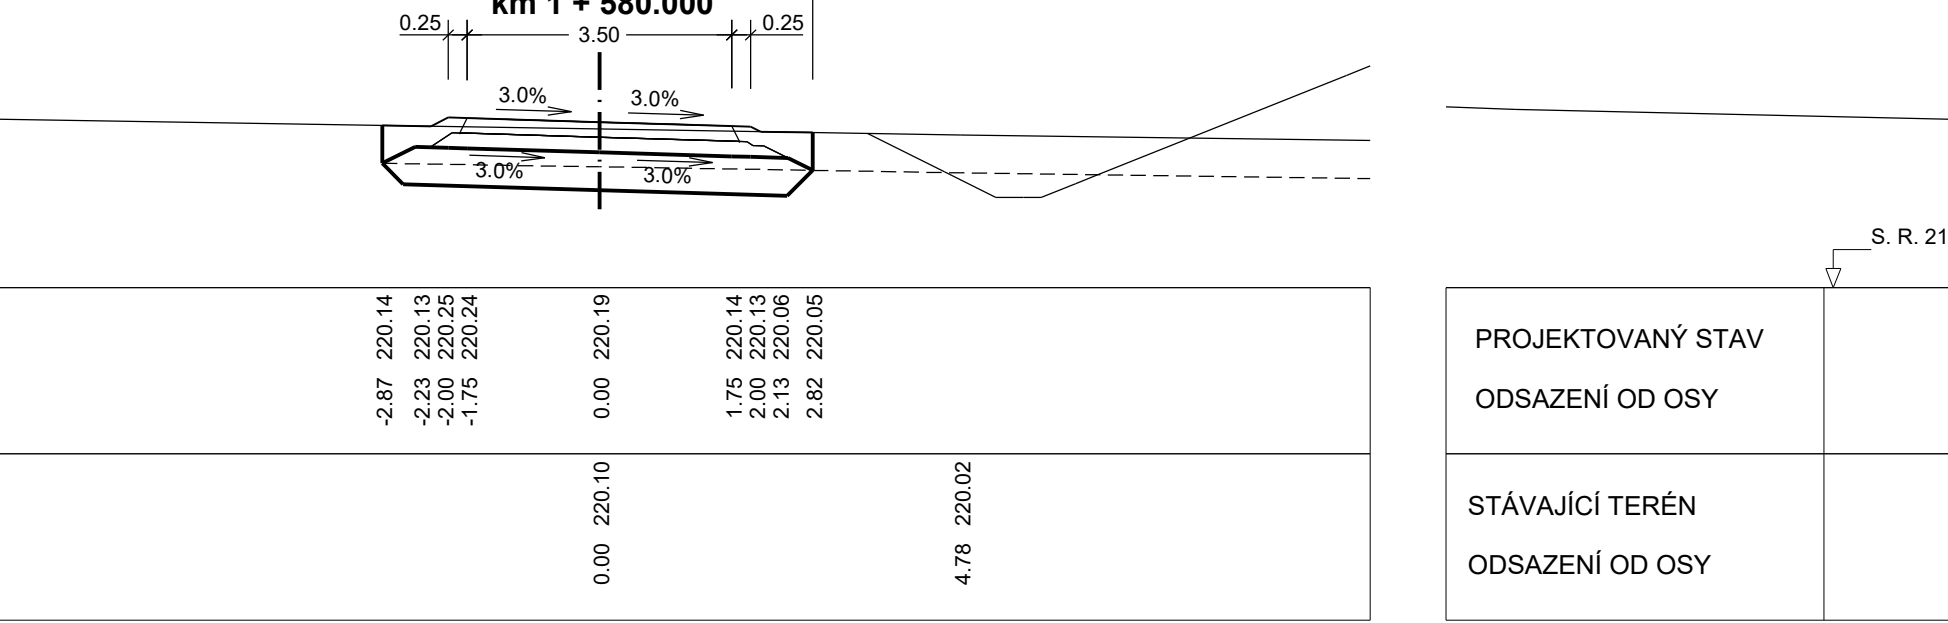
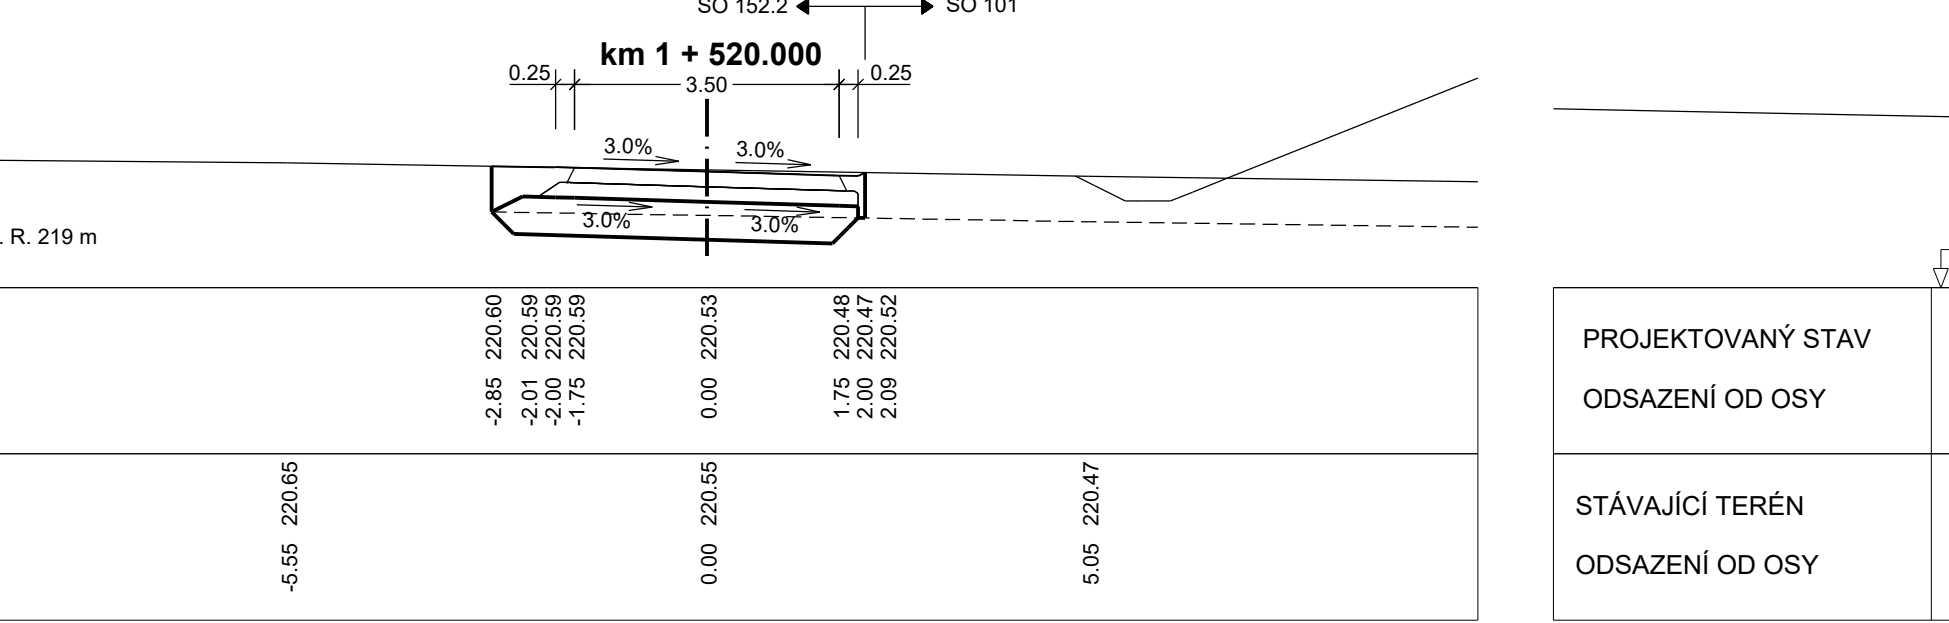
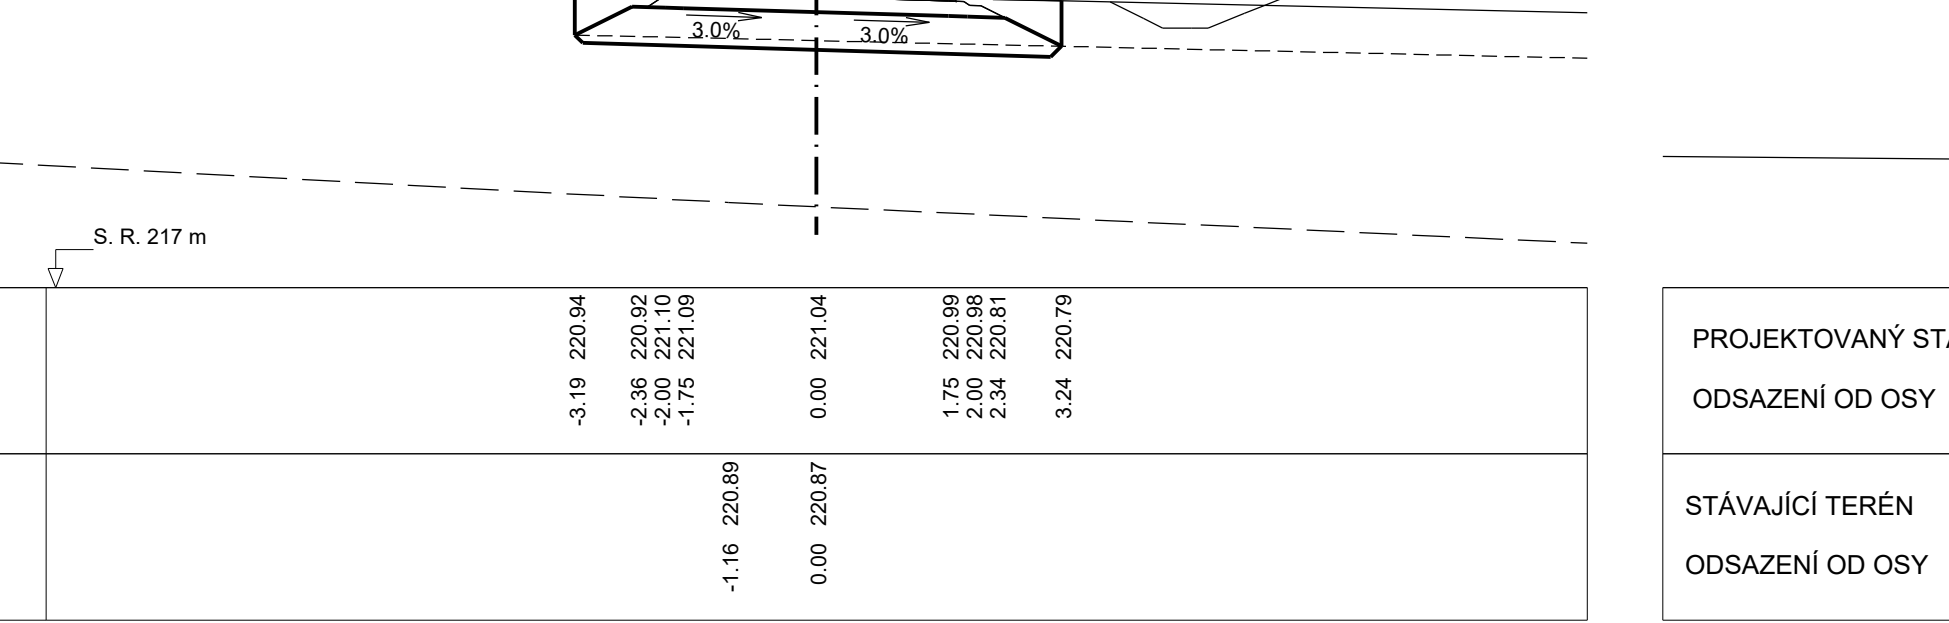
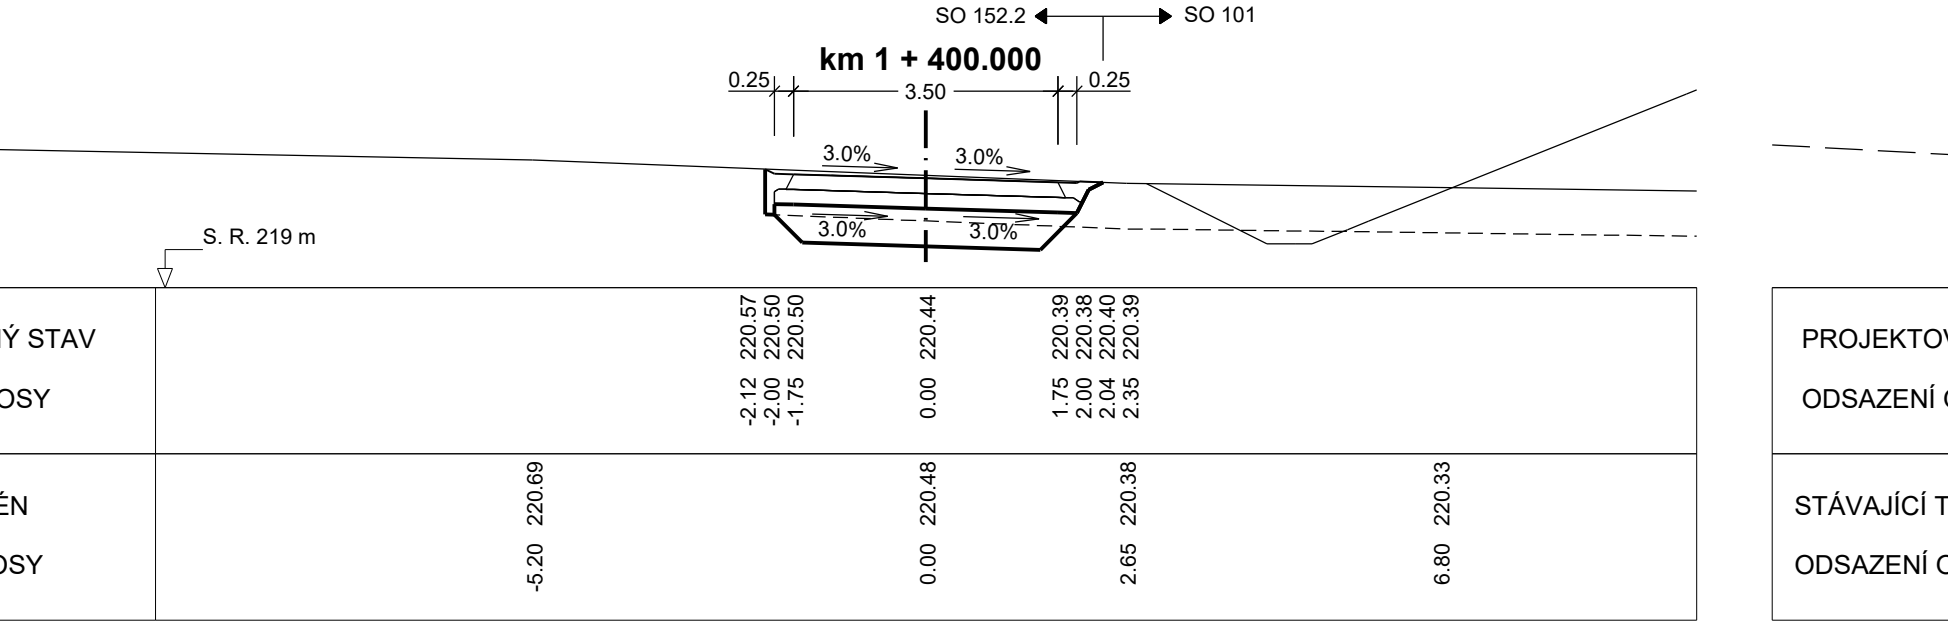
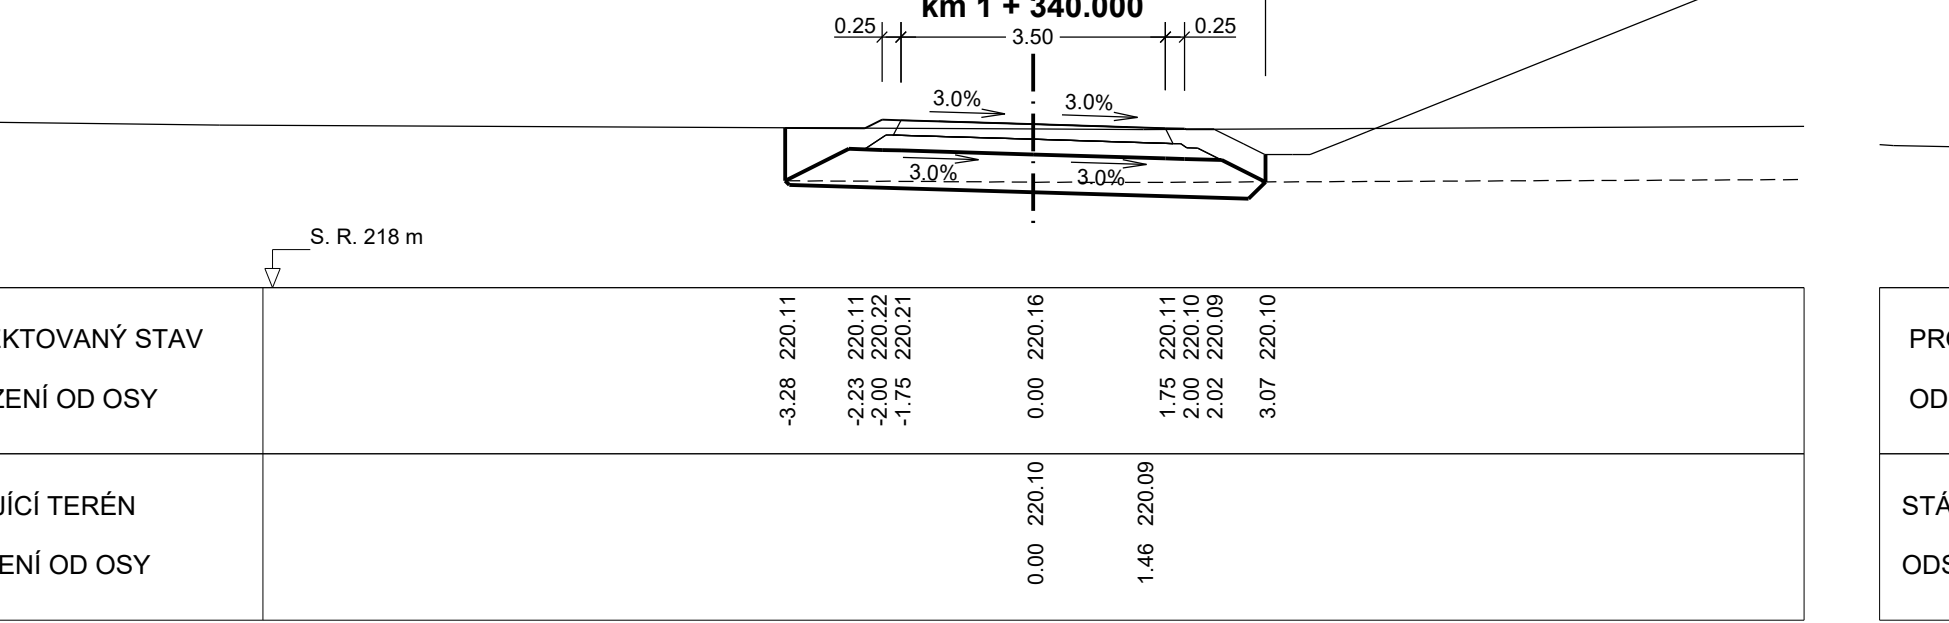


SO 152 - PŘÍSTUPY NA POZEMKY k.ú. ŽIDNĚVES
PŘÍČNÉ ŘEZY SO 152.2 - km 1,280 - 1,680, M 1 : 100

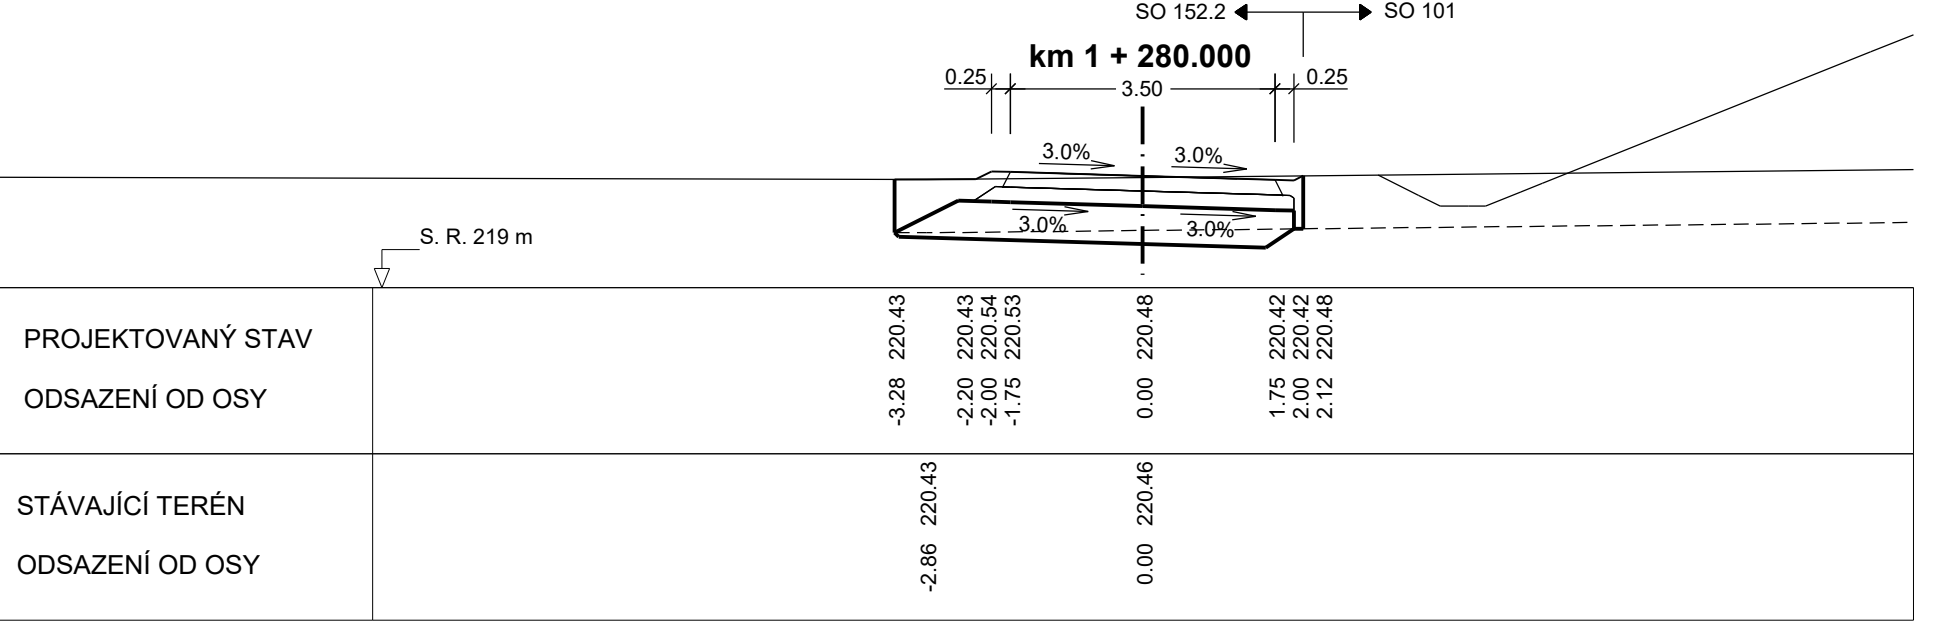

Výškový systém: Bpv

SO 152 Přístupy na pozemky k.ú. Židněves

Objednatel:



Ředitelství silnic a dálnic s. p.
Čerčanská 2023/12, Krč, 140 00 Praha 4

Zhotovitel:



Valbek, spol. s r.o.
Vaňurova 505/17
460 07 Liberec 3



Vypracoval: P. BARTUSEK
Zoop. projektant: ING. T. KLIMENT
Tech. kontrola: ING. M. HANŽL
Akce: I/16 MLADÁ BOLESLAV - MARTINOVICE

Zak. číslo: 21-L113-001
Datum: 02/2025
Stupeň: PDPS
Počet formátů: 20 x A4
Měřítko: 1:100
Č. přílohy: Paré

Zhotovitel:

Příloha
Valbek, spol. s r.o.
Vaňurova 505/17
460 07 Liberec 3

5.2.4