




SO 152 - PŘÍSTUPY NA POZEMKY k.ú. ŽIDNĚVES
PŘÍČNÉ ŘEZY SO 152.2 - km 1,700 - 2,100, M 1 : 100

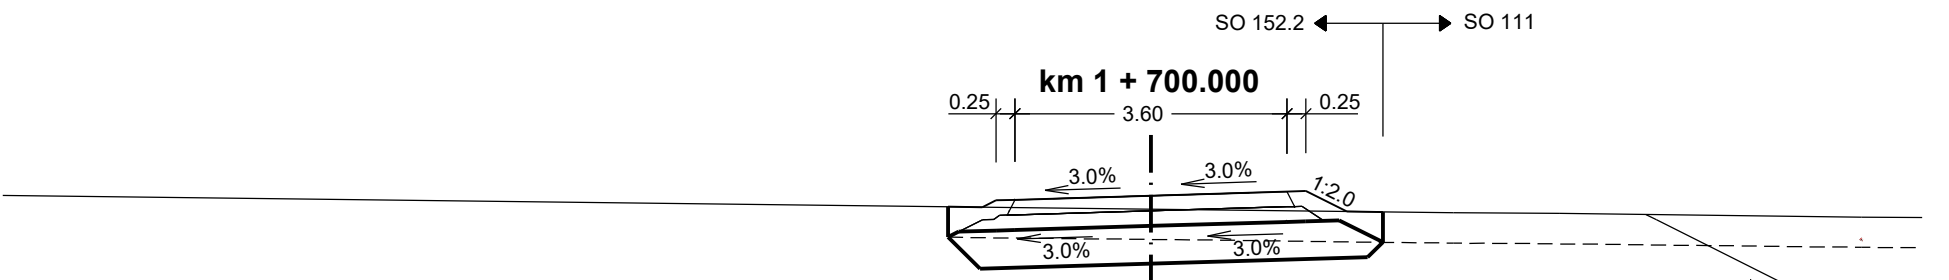


PROJEKTOVANÝ STAV	
ODSAZENÍ OD OSY	
STÁVAJÍCÍ TERÉN	
ODSAZENÍ OD OSY	

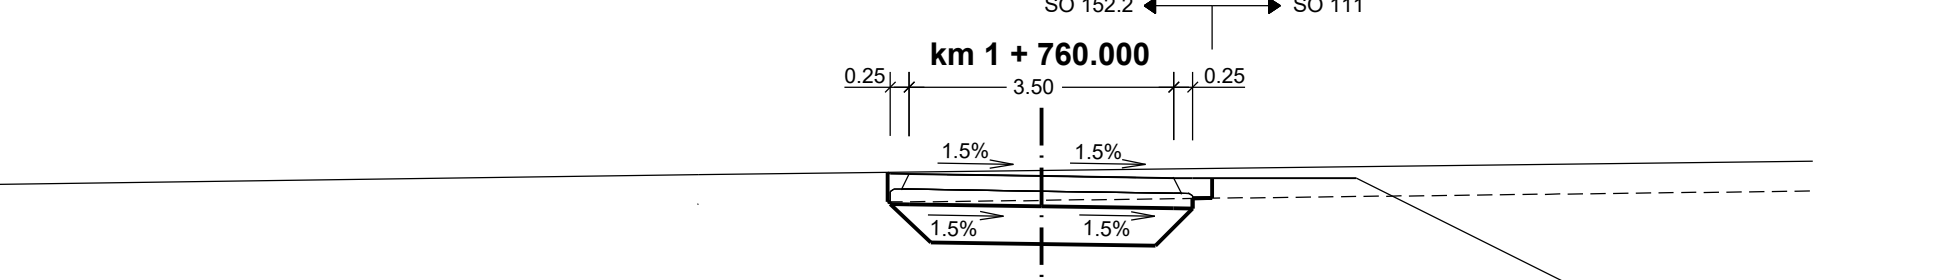


PROJEKTOVANÝ STAV	
ODSAZENÍ OD OSY	
STÁVAJÍCÍ TERÉN	
ODSAZENÍ OD OSY	

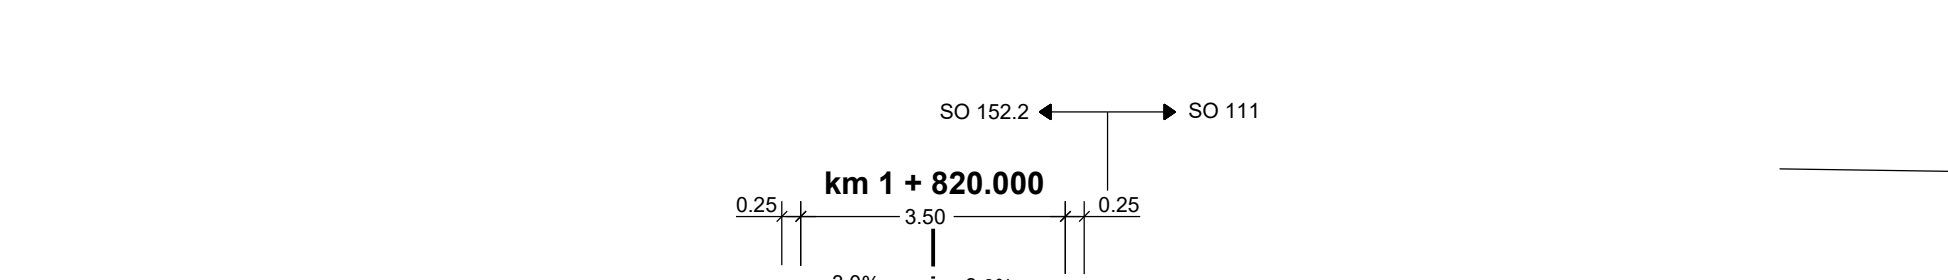

PROJEKTOVANÝ STAV	
ODSAZENÍ OD OSY	
STÁVAJÍCÍ TERÉN	
ODSAZENÍ OD OSY	

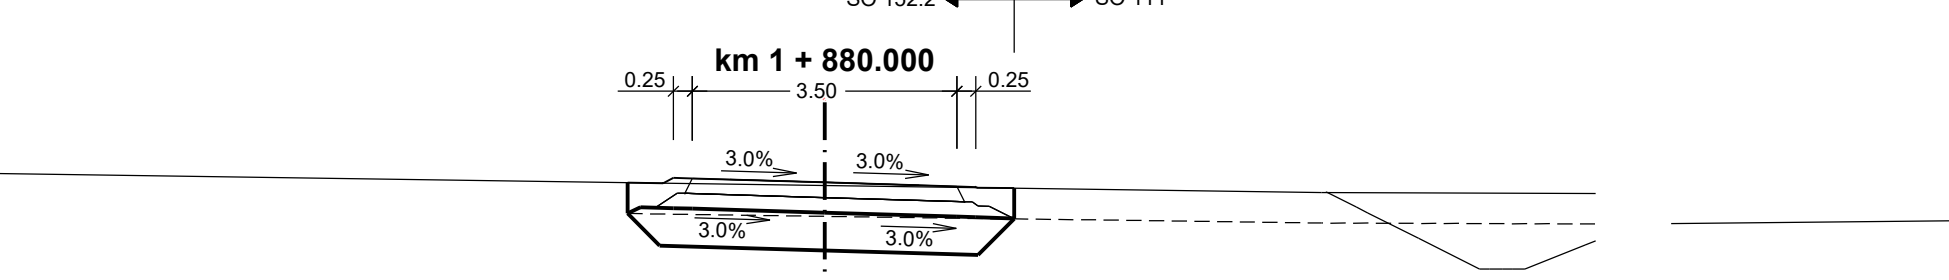

PROJEKTOVANÝ STAV	
ODSAZENÍ OD OSY	
STÁVAJÍCÍ TERÉN	
ODSAZENÍ OD OSY	

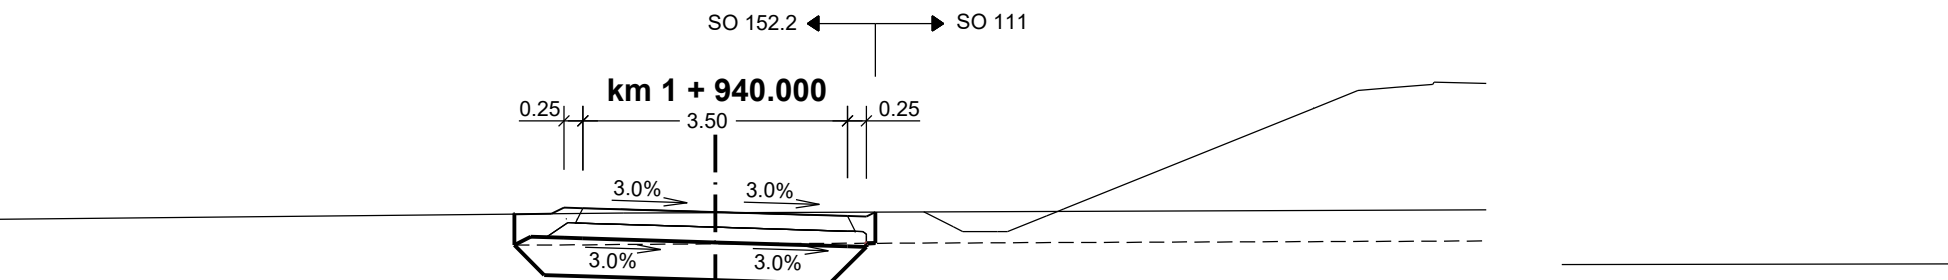


PROJEKTOVANÝ STAV	
ODSAZENÍ OD OSY	
STÁVAJÍCÍ TERÉN	
ODSAZENÍ OD OSY	




PROJEKTOVANÝ STAV	
ODSAZENÍ OD OSY	
STÁVAJÍCÍ TERÉN	
ODSAZENÍ OD OSY	




PROJEKTOVANÝ STAV	
ODSAZENÍ OD OSY	
STÁVAJÍCÍ TERÉN	
ODSAZENÍ OD OSY	

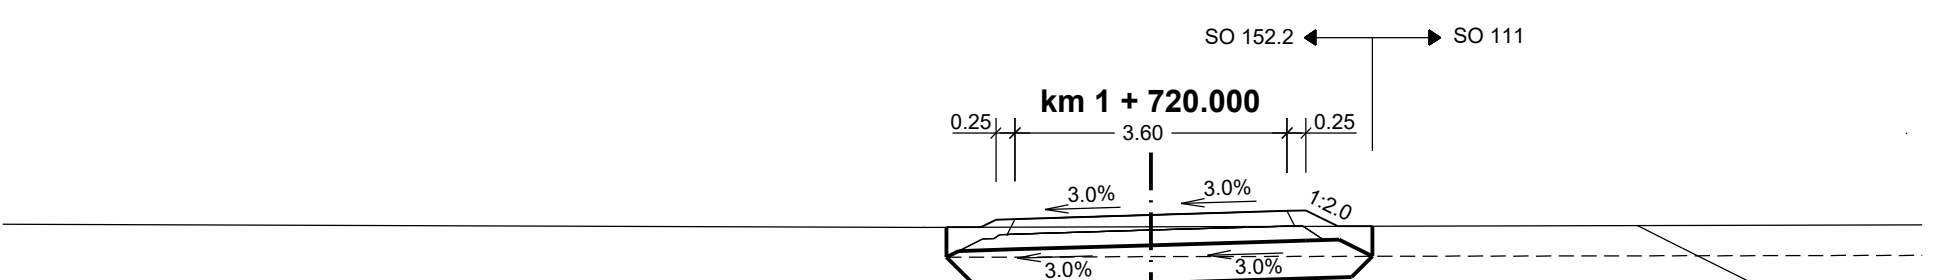


PROJEKTOVANÝ STAV	
ODSAZENÍ OD OSY	
STÁVAJÍCÍ TERÉN	
ODSAZENÍ OD OSY	

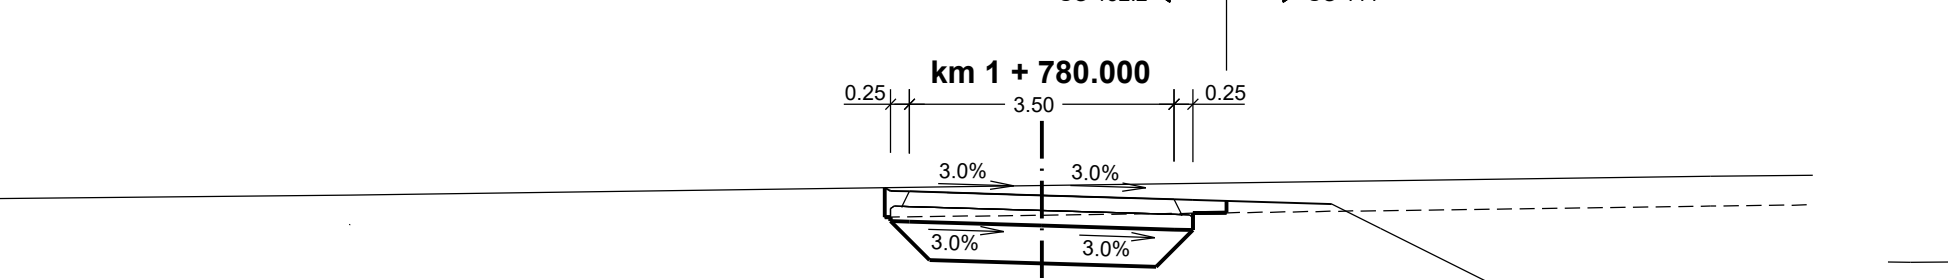


PROJEKTOVANÝ STAV	
ODSAZENÍ OD OSY	
STÁVAJÍCÍ TERÉN	
ODSAZENÍ OD OSY	

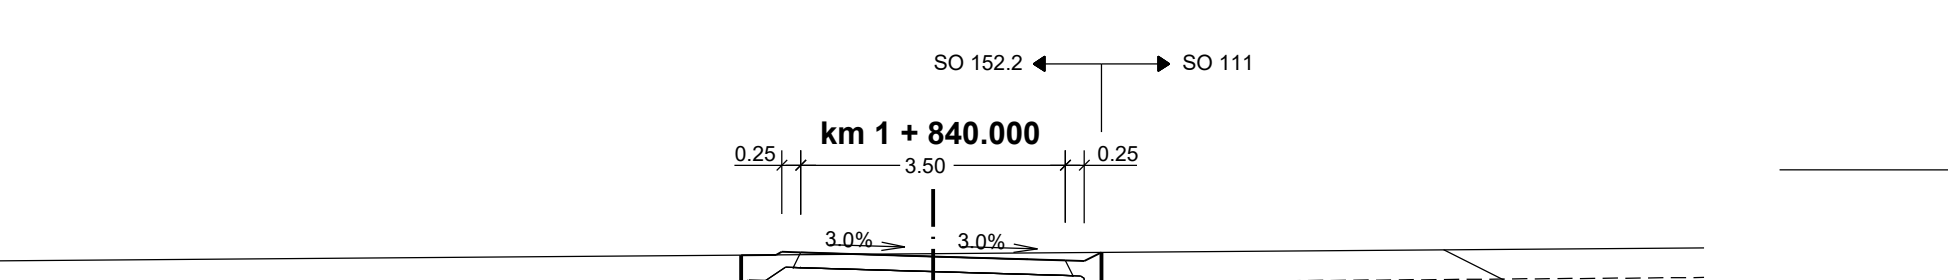


PROJEKTOVANÝ STAV	
ODSAZENÍ OD OSY	
STÁVAJÍCÍ TERÉN	
ODSAZENÍ OD OSY	

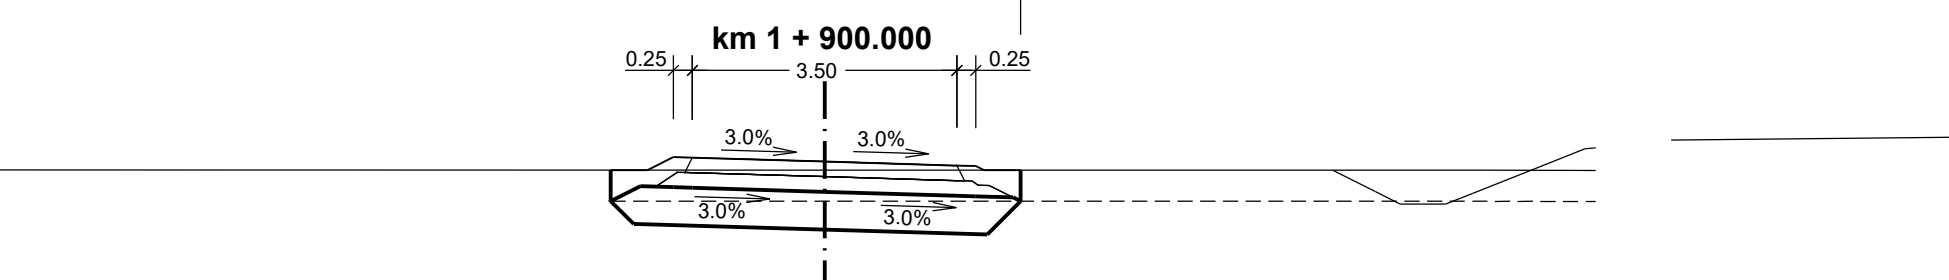

PROJEKTOVANÝ STAV	
ODSAZENÍ OD OSY	
STÁVAJÍCÍ TERÉN	
ODSAZENÍ OD OSY	

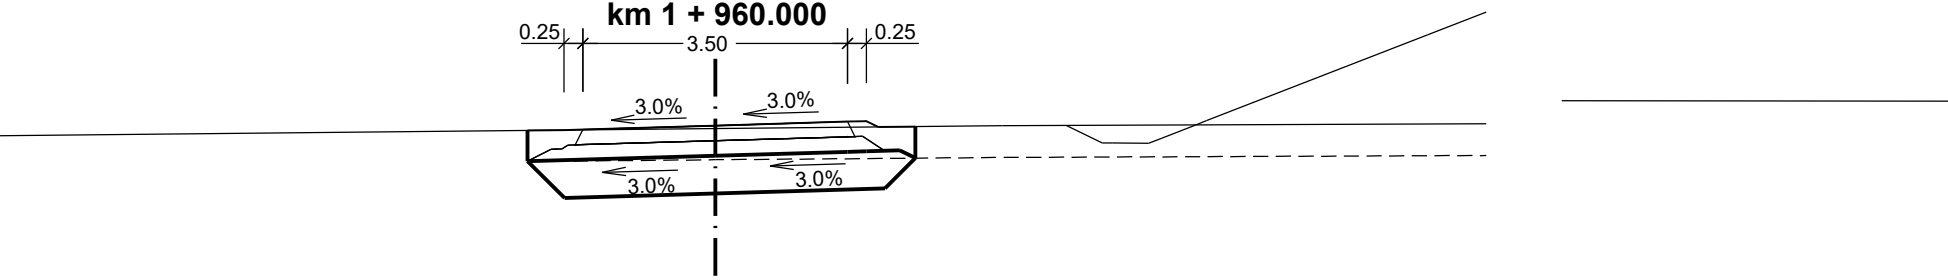


PROJEKTOVANÝ STAV	
ODSAZENÍ OD OSY	
STÁVAJÍCÍ TERÉN	
ODSAZENÍ OD OSY	

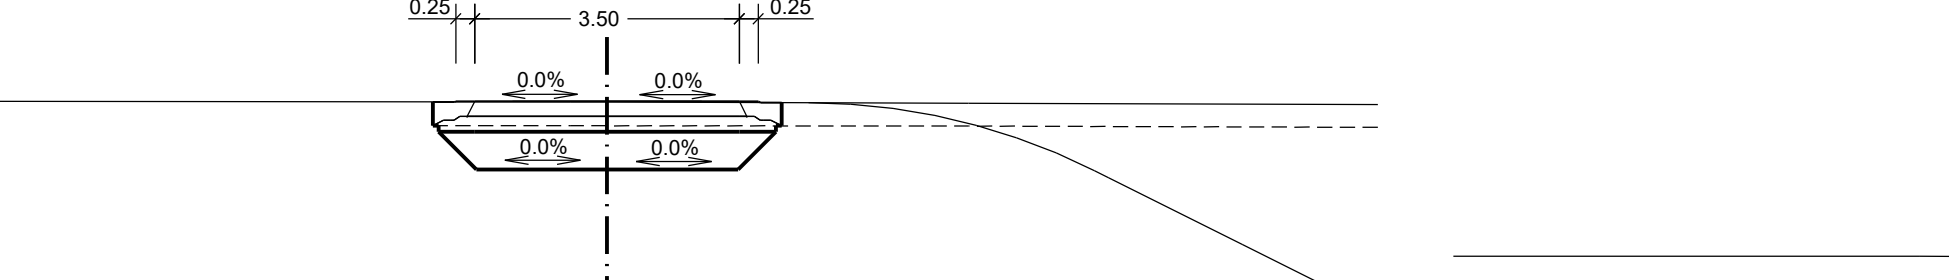


PROJEKTOVANÝ STAV	
ODSAZENÍ OD OSY	
STÁVAJÍCÍ TERÉN	
ODSAZENÍ OD OSY	




PROJEKTOVANÝ STAV	
ODSAZENÍ OD OSY	
STÁVAJÍCÍ TERÉN	
ODSAZENÍ OD OSY	

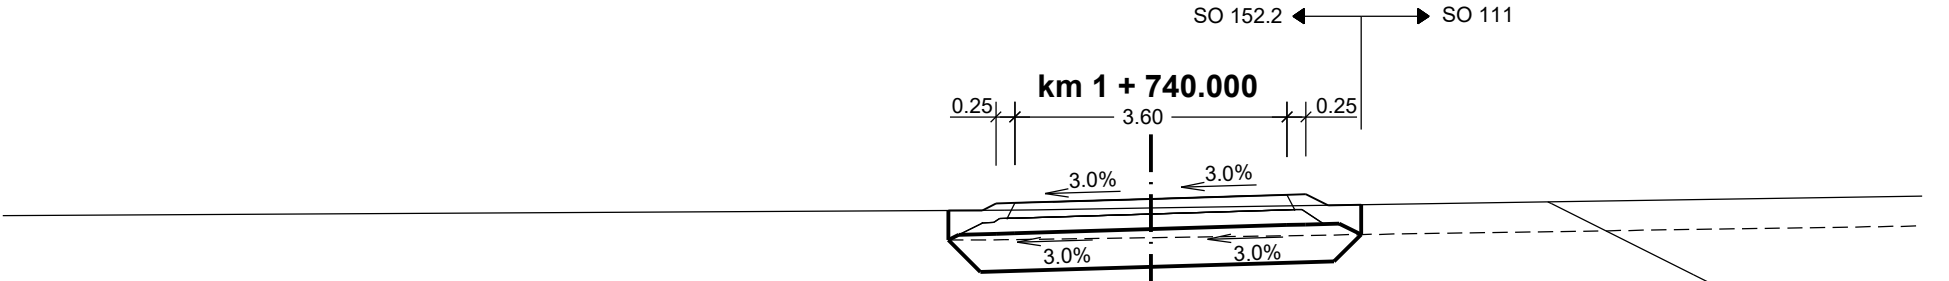


PROJEKTOVANÝ STAV	
ODSAZENÍ OD OSY	
STÁVAJÍCÍ TERÉN	
ODSAZENÍ OD OSY	

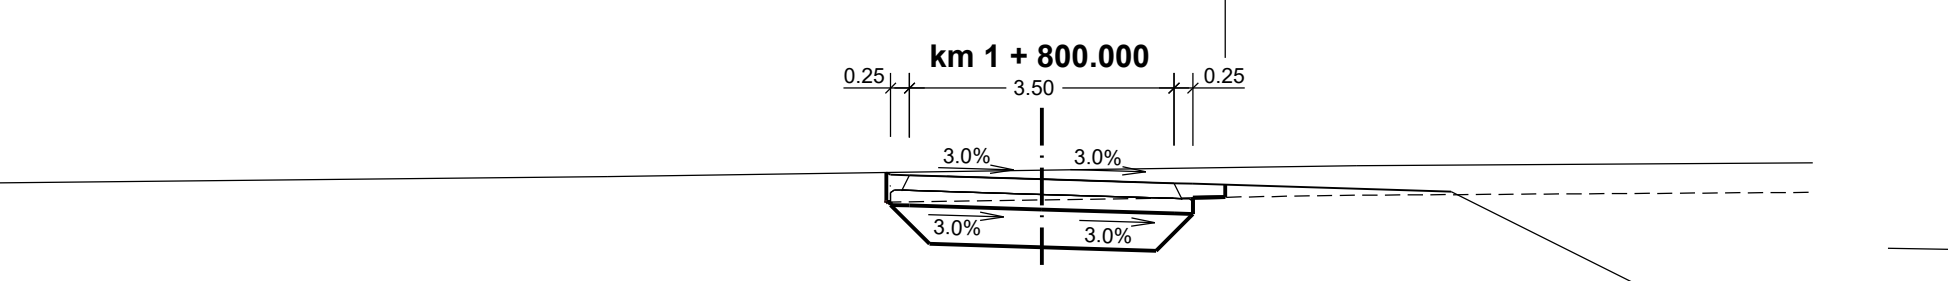


PROJEKTOVANÝ STAV	
ODSAZENÍ OD OSY	
STÁVAJÍCÍ TERÉN	
ODSAZENÍ OD OSY	

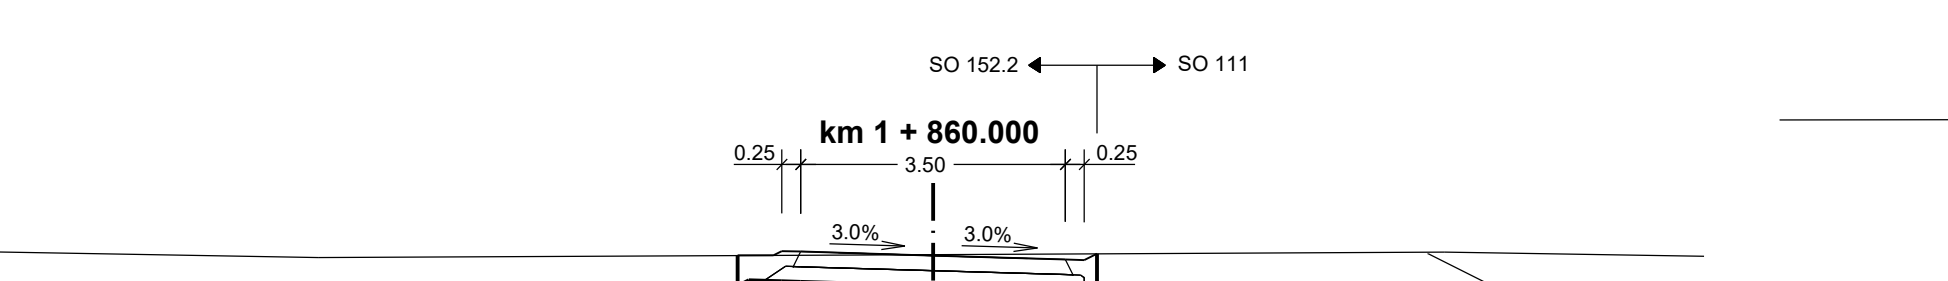


PROJEKTOVANÝ STAV	
ODSAZENÍ OD OSY	
STÁVAJÍCÍ TERÉN	
ODSAZENÍ OD OSY	

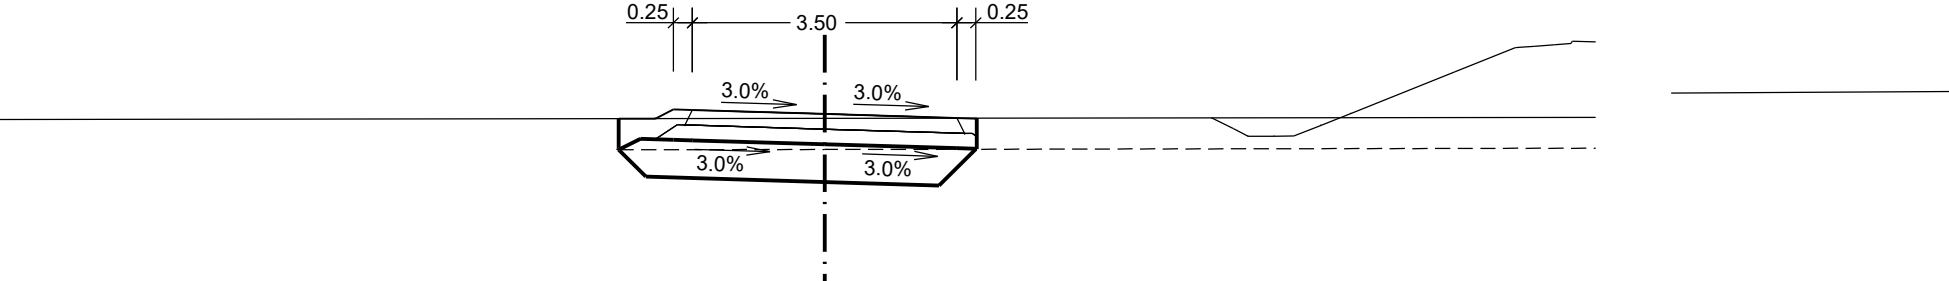


PROJEKTOVANÝ STAV	
ODSAZENÍ OD OSY	
STÁVAJÍCÍ TERÉN	
ODSAZENÍ OD OSY	

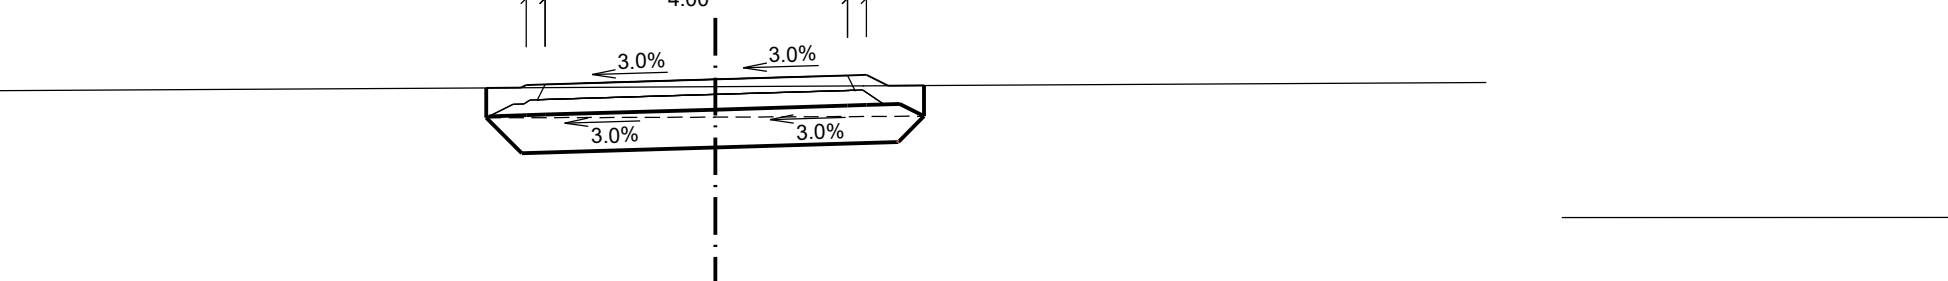

PROJEKTOVANÝ STAV	
ODSAZENÍ OD OSY	
STÁVAJÍCÍ TERÉN	
ODSAZENÍ OD OSY	

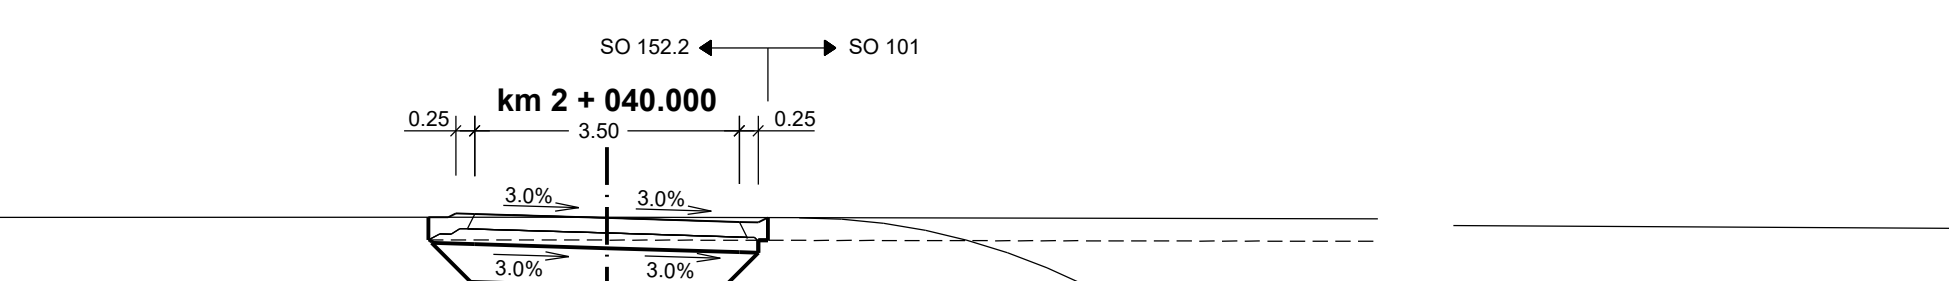

PROJEKTOVANÝ STAV	
ODSAZENÍ OD OSY	
STÁVAJÍCÍ TERÉN	
ODSAZENÍ OD OSY	

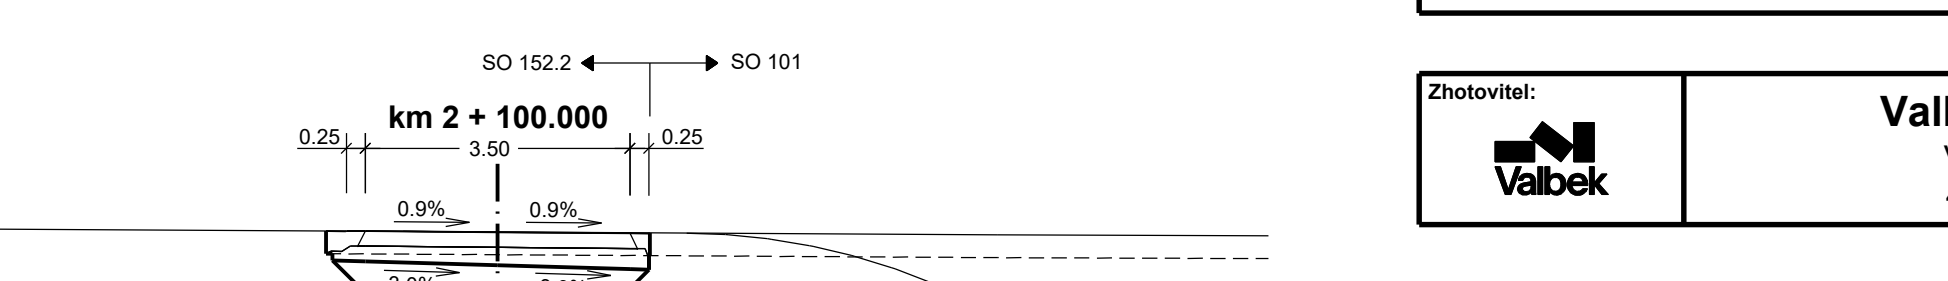

PROJEKTOVANÝ STAV	
ODSAZENÍ OD OSY	
STÁVAJÍCÍ TERÉN	
ODSAZENÍ OD OSY	

Výškový systém: Bpv

SO 152 Přístupy na pozemky k.ú. Židněves

Ověřeno:



Ředitelství silnic a dálnic s. p.
Čerčanská 2023/12, Křč, 140 00 Praha 4

Zhotovitel:



Valbek, spol. s r.o.
Vaňurova 505/17
460 07 Liberec 3



Vypracoval: P. BARTUSEK
Zodp. projektant: ING. T. KLIMENT
Tech. kontrola: ING. M. HANŽL
Akce: I/16 MLADÁ BOLESLAV - MARTINOVICE

Zak. číslo: 21-L113-001
Datum: 02/2025
Stupeň: PDP
Počet formátů: 20 x A4
Mřížko: 1 : 100
Č. přílohy: Paré

Zhotovitel:

Valbek, spol. s r.o.
Vaňurova 505/17
460 07 Liberec 3

Příloha: PŘÍČNÉ ŘEZY SO 152.2 - km 1,700 - 2,100

5.2.5