


SO 153 - PŘÍSTUPY NA POZEMKY k.ú. SUKORADY U MLADÉ BOLESLAVI
SITUACE - SO 153.1, M 1 : 1 000

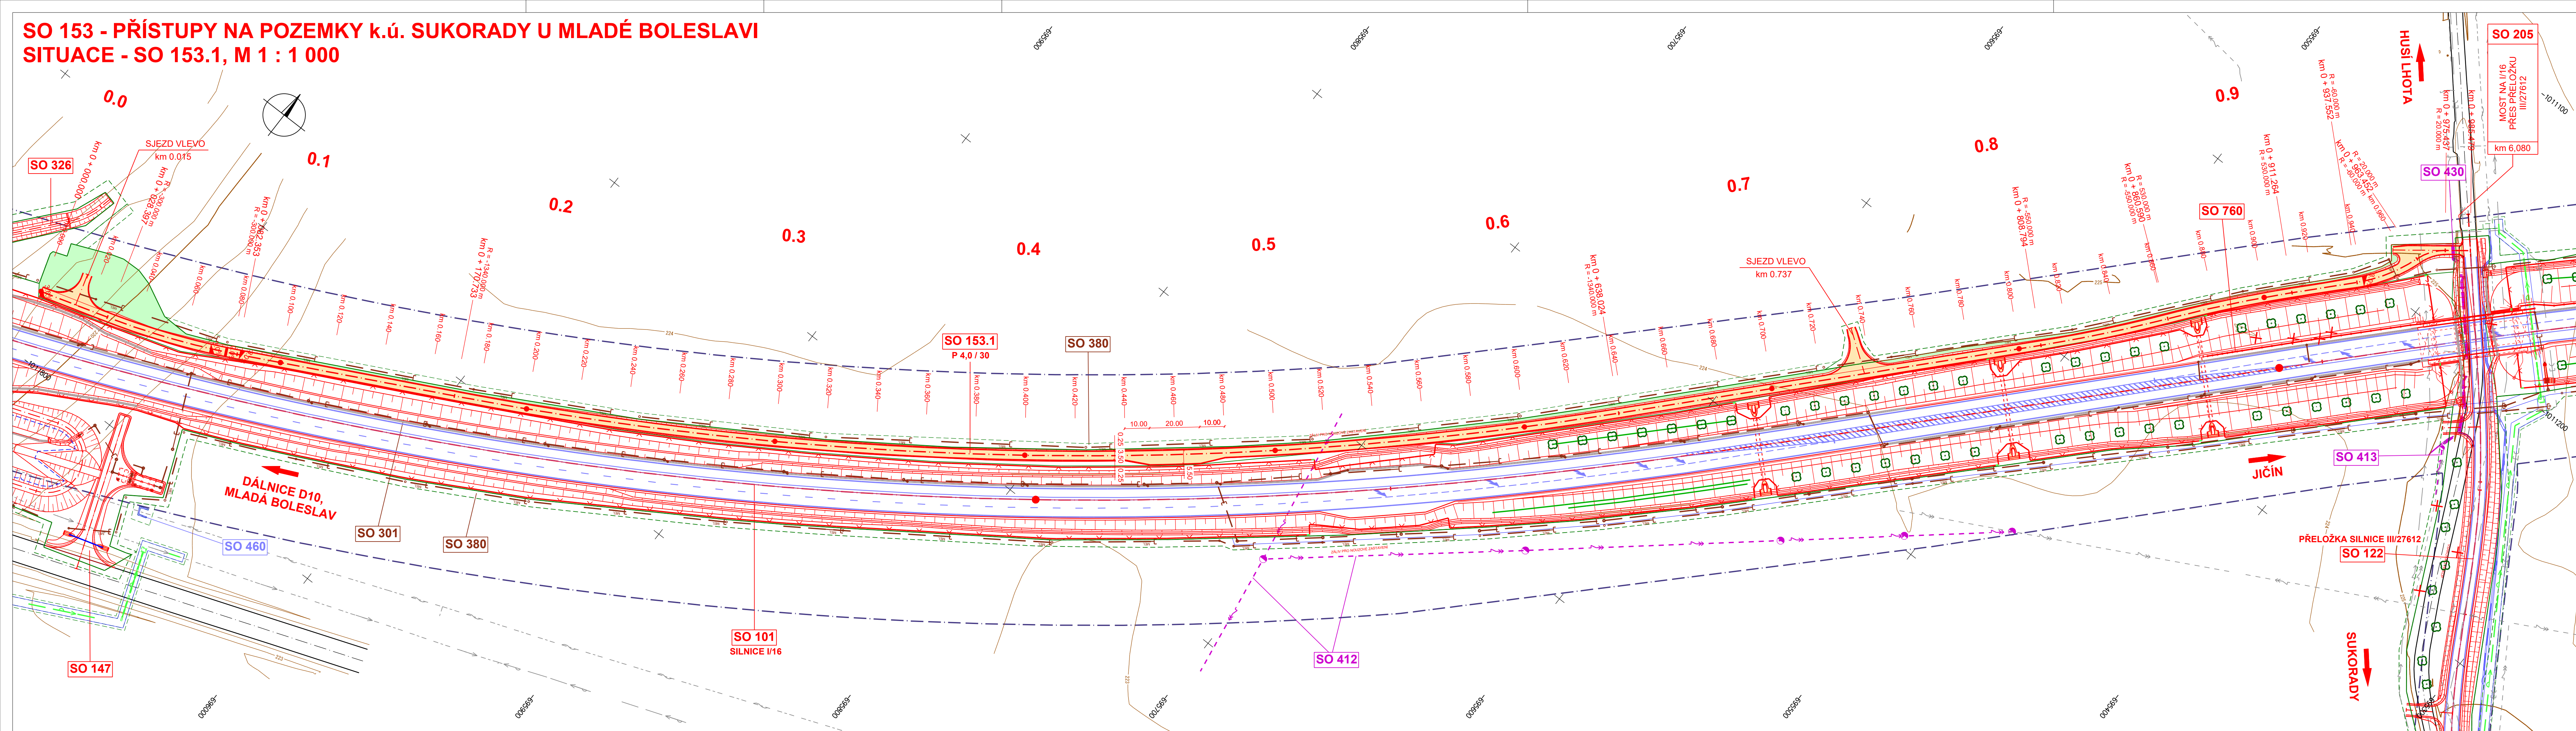

LEGENDA:

PLOCHY

- VOZOVKA - ASFALTOVÝ KRYT
- VOZOVKA - FRÉZOVANÁ
- VOZOVKA - POLNÍ CESTY
- CHODNÍK
- DLAŽBA VOZOVKY
- SVAHY VÝKOPU
- SVAHY NÁSPY
- VEGETAČNÍ ÚPRAVY

OBVOD STAVBY

- TRVALÝ ZÁBOR
- DOČASNÝ ZÁBOR

NOVÉ IS

- DEŠŤOVÁ KANALIZACE
- MELIORACE
- VÝTLAK
- VODOVOD
- NADZEMNÍ VEDENÍ NN
- NADZEMNÍ VEDENÍ VN
- PODZEMNÍ VEDENÍ NN
- PODZEMNÍ SDĚLOVACÍ VEDENÍ
- PLYNOVOD - STL

STÁVAJÍCÍ IS - INFORMATIVNÍ ZÁKRES

- PODZEMNÍ VEDENÍ NN
- PODZEMNÍ VEDENÍ VN
- NADZEMNÍ VEDENÍ NN
- NADZEMNÍ VEDENÍ VN
- NADZEMNÍ VEDENÍ VVN
- DEŠŤOVÁ KANALIZACE
- PLYNOVOD - STL
- PODZEMNÍ SDĚLOVACÍ VEDENÍ
- VODOVOD

Souřadnicový systém: S-JSTK

Výškový systém Bpv

SO 153 Přístupy na pozemky k.ú. Sukorady u Mladé Boleslavi

Objednatel:



Ředitelství silnic a dálnic s. p.
Čerčanská 2023/12, Krč, 140 00 Praha 4

Zhotovitel:



Valbek, spol. s r.o.
Vaňurova 505/17
460 07 Liberec 3

HIP:

ING. T. KLIMENT



Vypracoval	ING. A. DUMANSKA	Zak. číslo	21-L113-001	
Zodp. projektant	ING. T. KLIMENT	Datum	02/2025	
Tech. kontrola	ING. M. HANŽL	Stupeň	PDPS	
Akce	I/16 MLADÁ BOLESLAV - MARTINOVICE		Počet formátů	6 x A4
Měřítko			1 : 1000	
Č. přílohy			Paré	
Příloha	SITUACE - SO 153.1		2.1	