
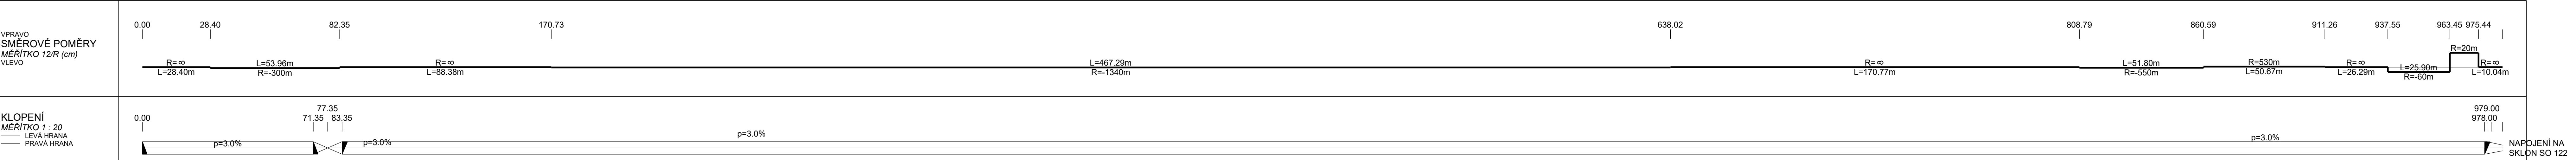


SO 153 - PŘÍSTUP NA POZEMKY k.ú. SUKORADY U MLADÉ BOLESLAVI
PODÉLNÝ PROFIL - SO 153.1, M 1 : 1 000 / 100

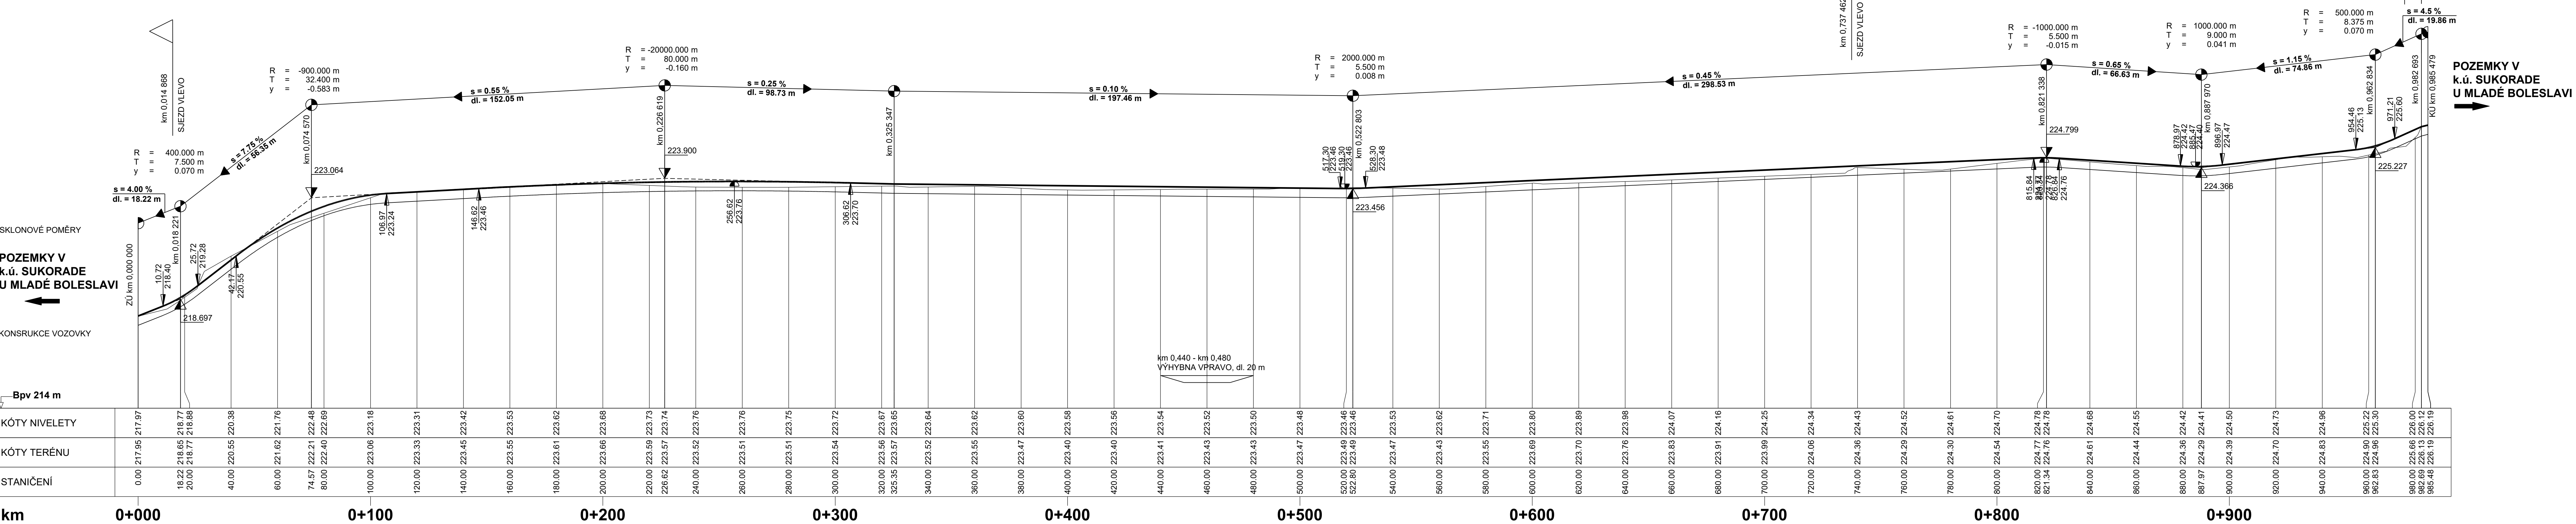

úřkový systém Bpv

SO 153 Přístupy na pozemky k.ú. Sukorady u Mladé Boleslavi

Objednatel:  **Ředitelství
silnic
a dálnic**

fotovitel: 	Valbek, spol. s r.o. Vaňurova 505/17 460 07 Liberec 3	HIP: ING. T. KLIMENT
---	--	-----------------------------

	Vypracoval	ING. A. DUMANSKA	Zak. číslo	21-L113-001
	Zodp. projektant	ING. T. KLIMENT	Datum	02/2025
	Tech. kontrola	ING. M. HANŽL	Stupeň	PDPS
	Akce		Počet formátů	14 x A4
I/16 MLADÁ BOLESLAV - MARTINOVICE			Měřítko	1 : 1000
			Č. přílohy	Paré
			3.1	
Protovitel: Valbek, spol. s r.o. Valbarkova 500/17 50 07 Líbavce 3	Příloha PODÉLNÝ PROFIL - SO 153.1			